


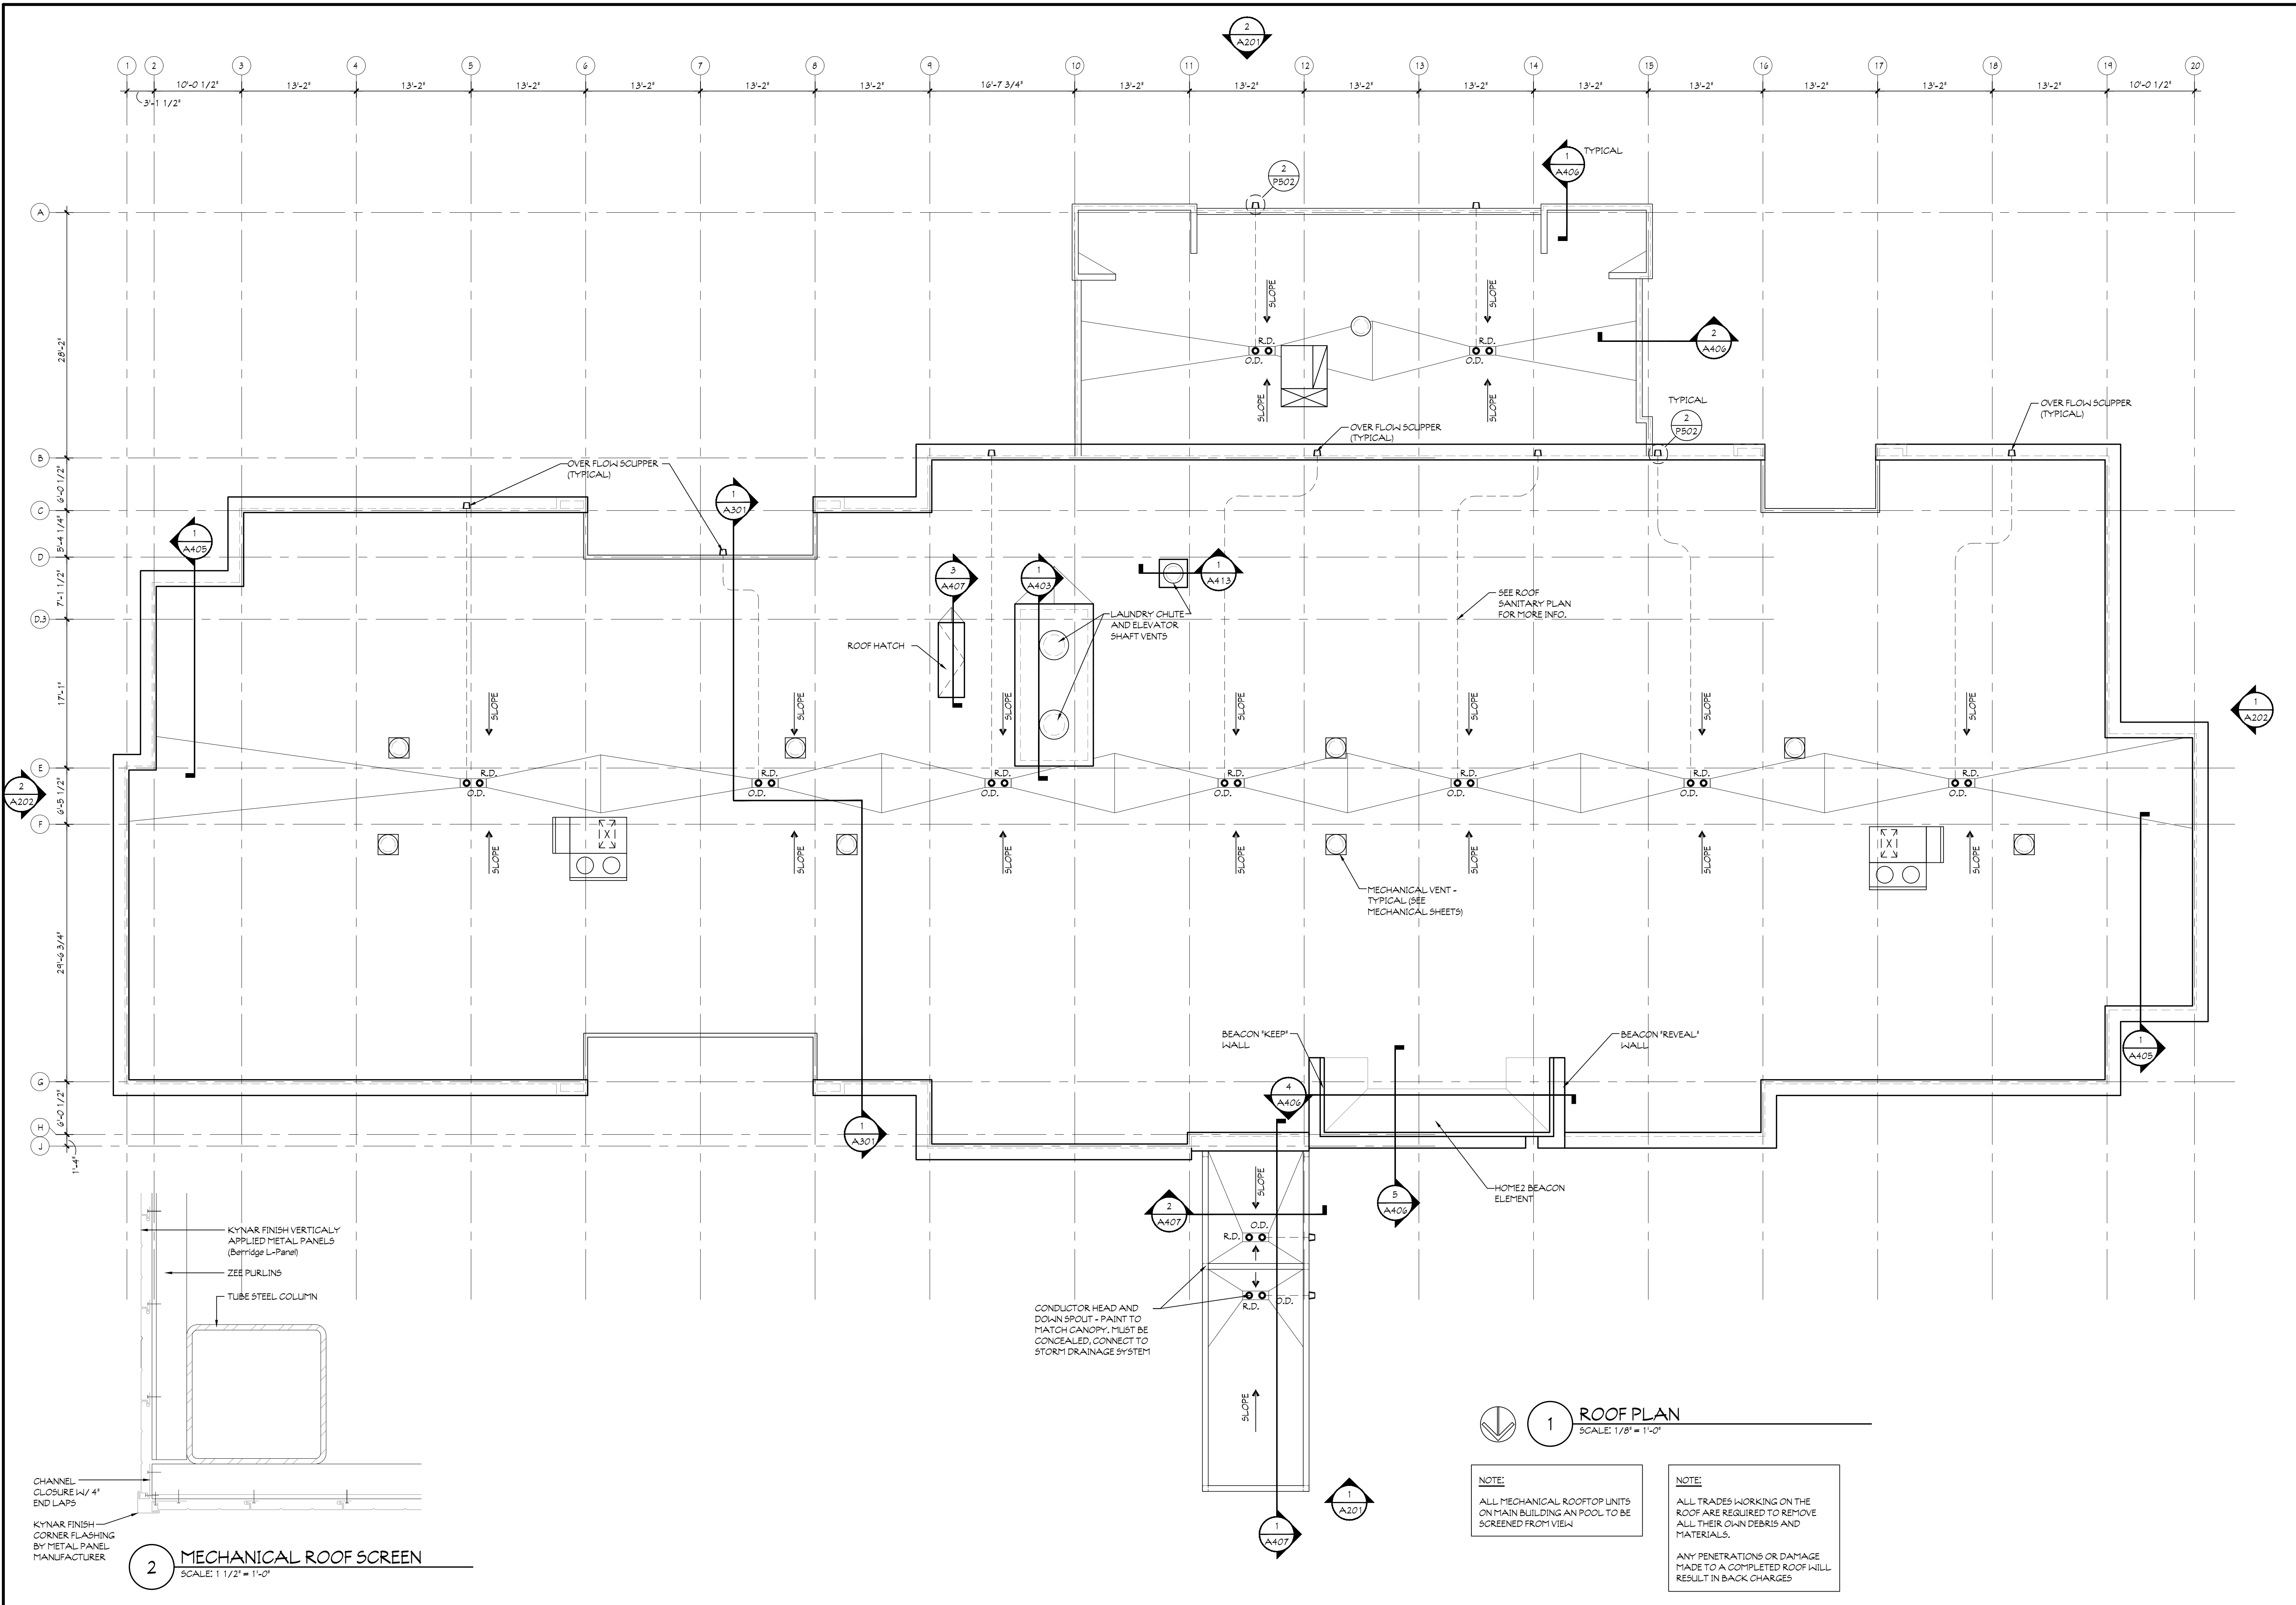

GENERAL NOTES

ALTHOUGH DRAWINGS ARE PREPARED TO SCALE, THE ACCURACY OF THE DRAWINGS CANNOT BE GUARANTEED. THE CONTRACTOR SHALL BE RESPONSIBLE FOR OBTAINING ALL NECESSARY PERMITS AND FOR VERIFYING ALL DIMENSIONS AND CONDITIONS PRIOR TO CONSTRUCTION.

ALL DIMENSIONS UNLESS OTHERWISE NOTED SHALL BE IN FEET AND INCHES. DIMENSIONS SHALL BE ROUNDED UP TO THE NEXT WHOLE INCH.

ALL DIMENSIONS UNLESS OTHERWISE NOTED SHALL BE IN FEET AND INCHES. DIMENSIONS SHALL BE ROUNDED UP TO THE NEXT WHOLE INCH.

Architects

MAUSET ARCHITECTURAL SERVICES
DIVISION OF L.E.M., INC.
112 NORTH MAIN STREET
GOSHEN, INDIANA 46526
PHONE: (574) 537-8500
FAX: (574) 537-0808

HOME2

SUITES BY HILTON

FT. WAYNE, INDIANA

REVISIONS:

1	PRELIMINARY - NOT FOR CONSTRUCTION
---	------------------------------------

DATE: 05/01/26

JOB NO.: MAS-26-105

NAME: ROOF PLAN

SHEET: A105