


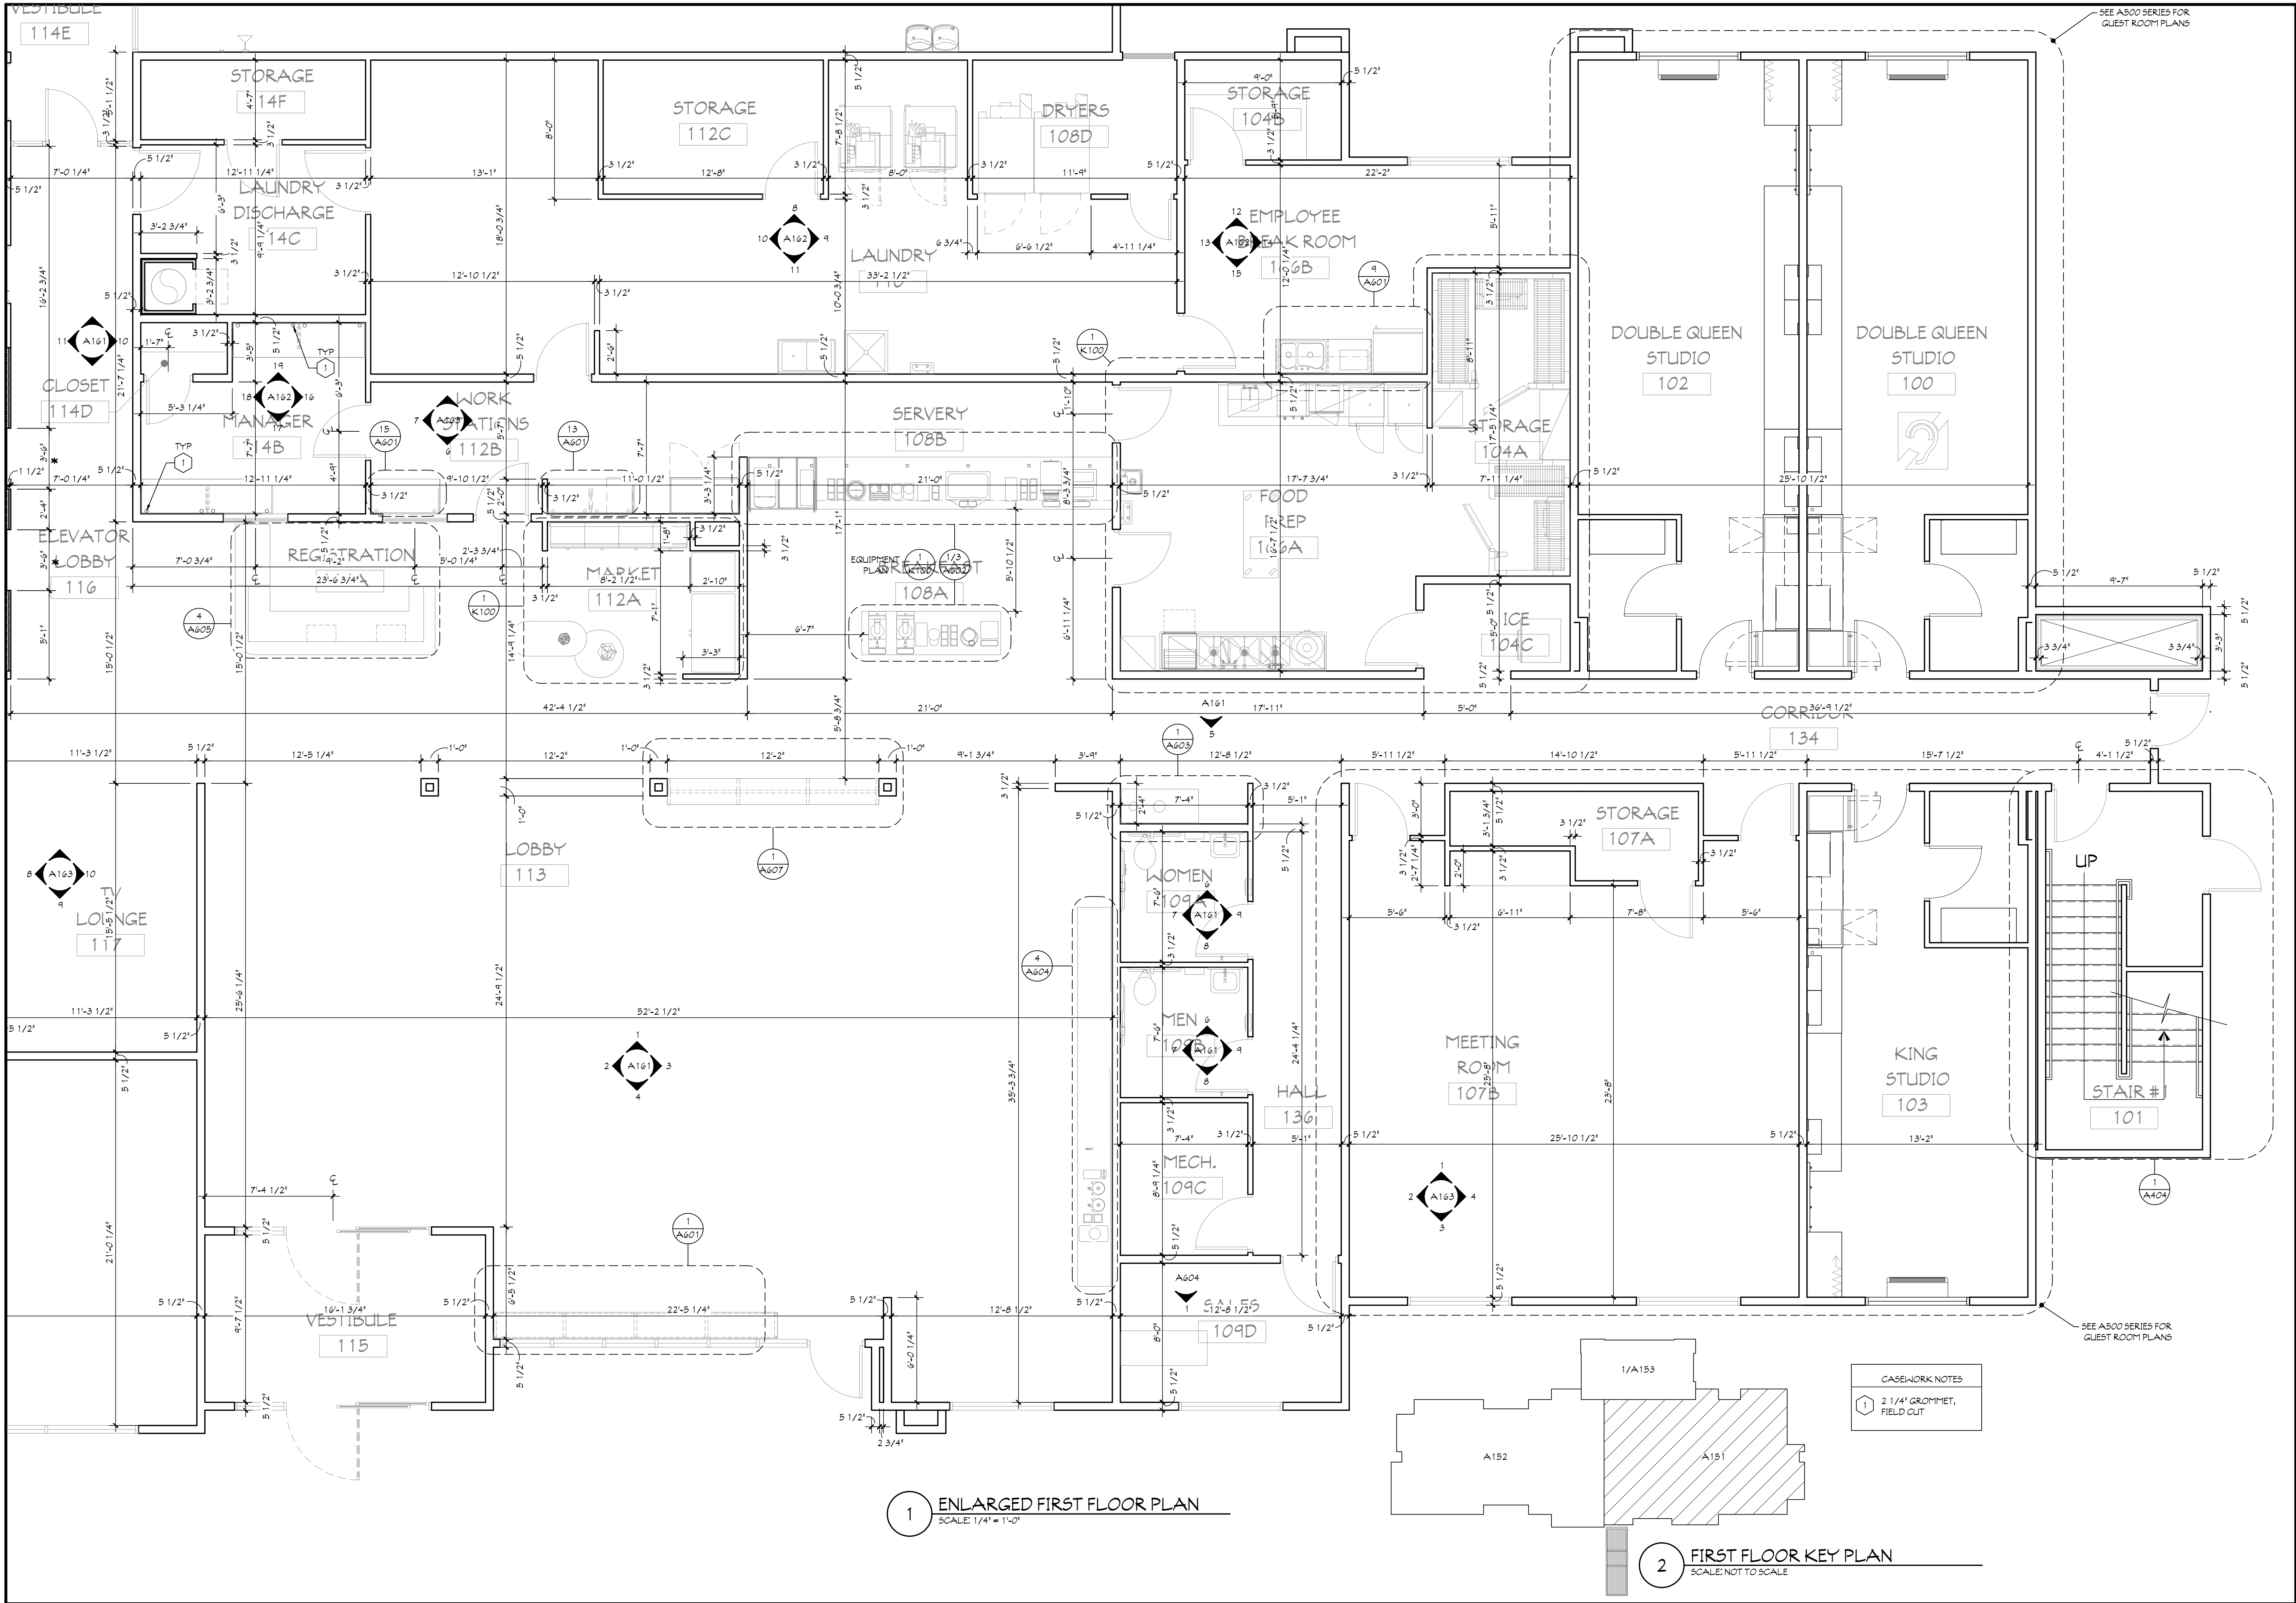

GENERAL NOTES

ALTHOUGH DRAWINGS ARE PREPARED TO SCALE, THE ACCURACY OF THE DRAWINGS CANNOT BE GUARANTEED. DIMENSIONS SHOWN ON THE DRAWINGS SHALL BE USED FOR CONSTRUCTION. DIMENSIONS SHALL BE USED FOR CONSTRUCTION. DIMENSIONS SHALL BE USED FOR CONSTRUCTION.

Architects
Planners
Engineers
Construction Mgmt.
* Rule 5 and MS4 Filing
L.E.M., INC.
PHONE (574) 537-8500
FAX (574) 537-0808
112 NORTH MAIN STREET
GOSHEN, INDIANA 46526

MAUST ARCHITECTURAL SERVICES
DIVISION OF
L.E.M., INC.

These drawings are the property of Maust Architectural Services and may not be reprinted, copied or used in any manner without the express written consent of Maust Architectural Services.

HOME 2
SUITES BY HILTON

SHEET SIZE 24x36

FT. WAYNE, INDIANA

REVISIONS:

DATE: 05/01/26
JOB NO.: MAS-26-105
NAME: ENLARGED FIRST FLOOR PLAN
SHEET:

A151

PRELIMINARY - NOT FOR CONSTRUCTION