



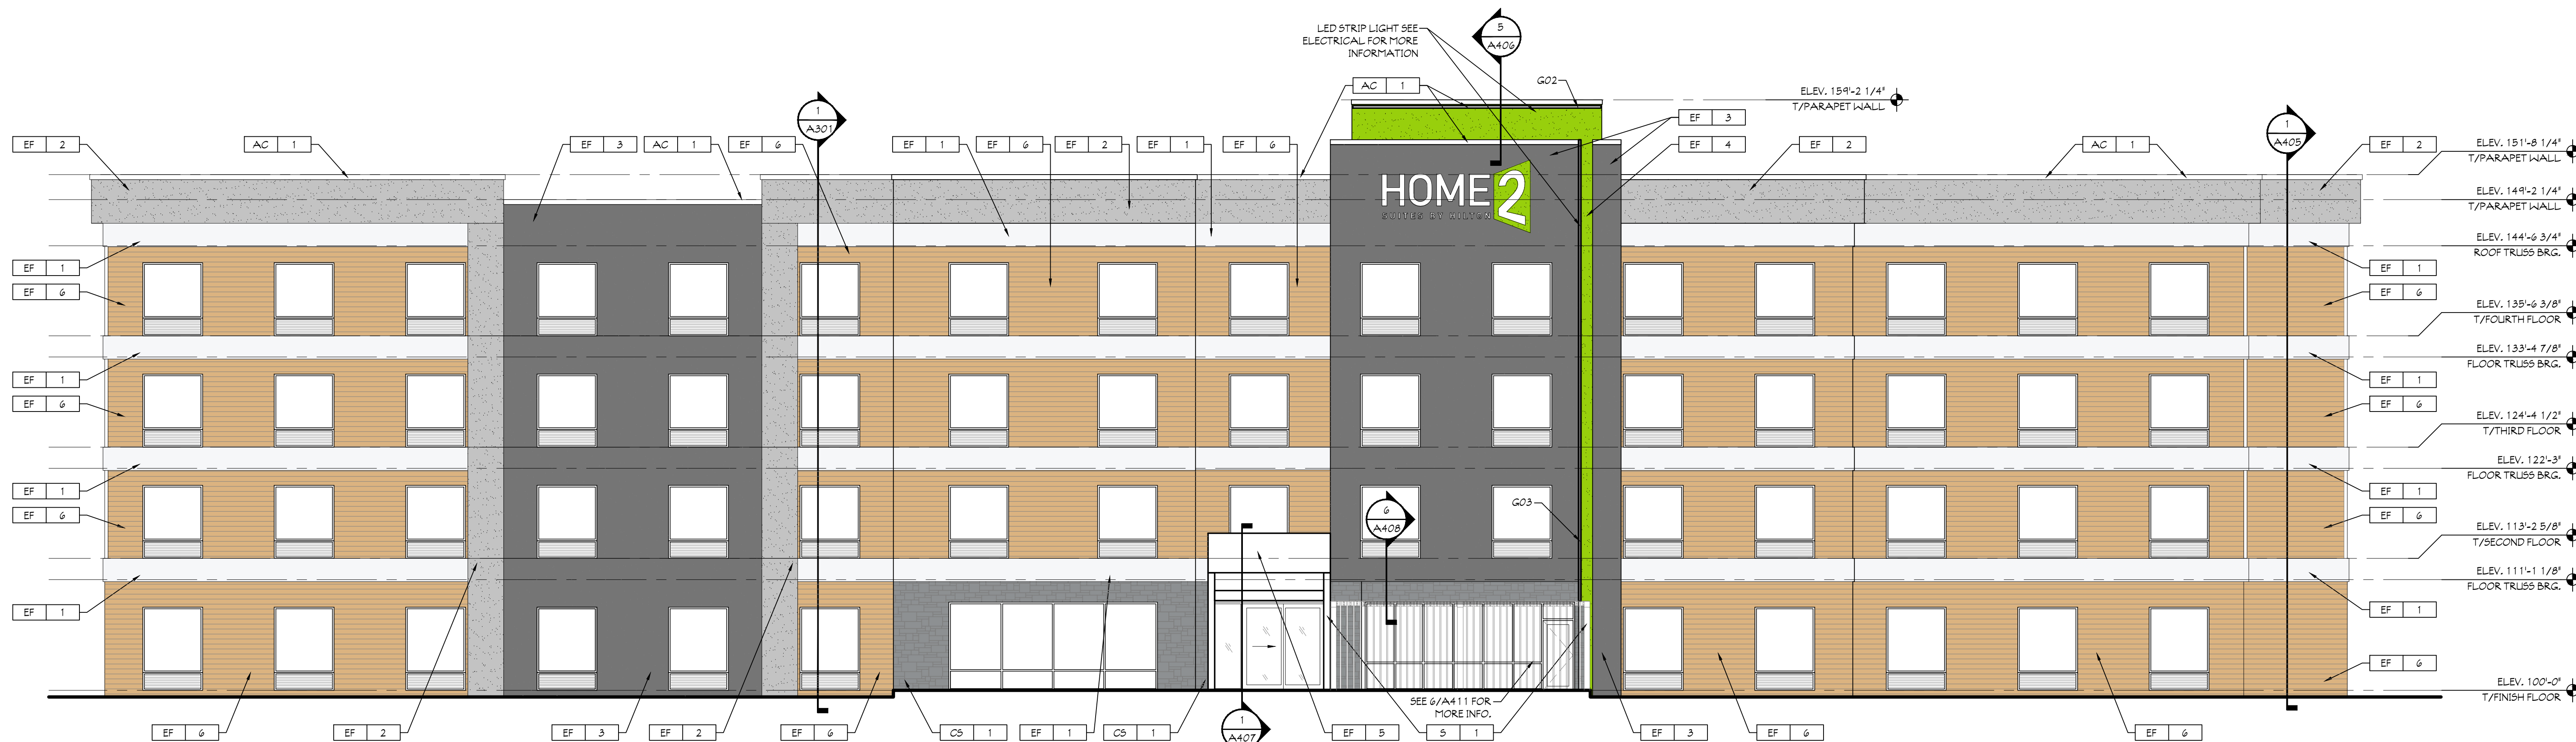

MATERIAL LEGEND	
AC-1:	ALUMINUM COPING TO MATCH SURROUNDING FINISH
CS-1	CULTURE STONE COLOR TO MATCH PAINT; AF-560 FLINT
EF-1:	4" MINIMUM EIFS SYSTEM, PAINT: 2121-70 CHANTILLY
EF-2:	1 1/2" MINIMUM EIFS SYSTEM, PAINT: CW-700 SLATE
EF-3:	1 1/2" MINIMUM EIFS SYSTEM, PAINT: 2120-10 JET BLACK
EF-4:	1 1/2" MINIMUM EIFS SYSTEM, PAINT: 398 FLOWER POWER
EF-5:	1 1/2" MINIMUM EIFS SYSTEM, PAINT: OC-17 WHITE DOVE
EF-6:	1 1/2" MINIMUM EIFS SYSTEM, PAINT: 2165-40 DARK
S-1:	PAINTED HSS STEEL, PAINT: OC-17 WHITE DOVE
ALL PAINT COLORS ARE BY BENJAMIN MOORE AND TO BE VERIFIED WITH OWNER BEFORE SELECTING	
ALL MECHANICAL GRILLES AND LOUVERS TO BE PAINTED TO MATCH THE SURROUNDING MATERIAL COLOR	

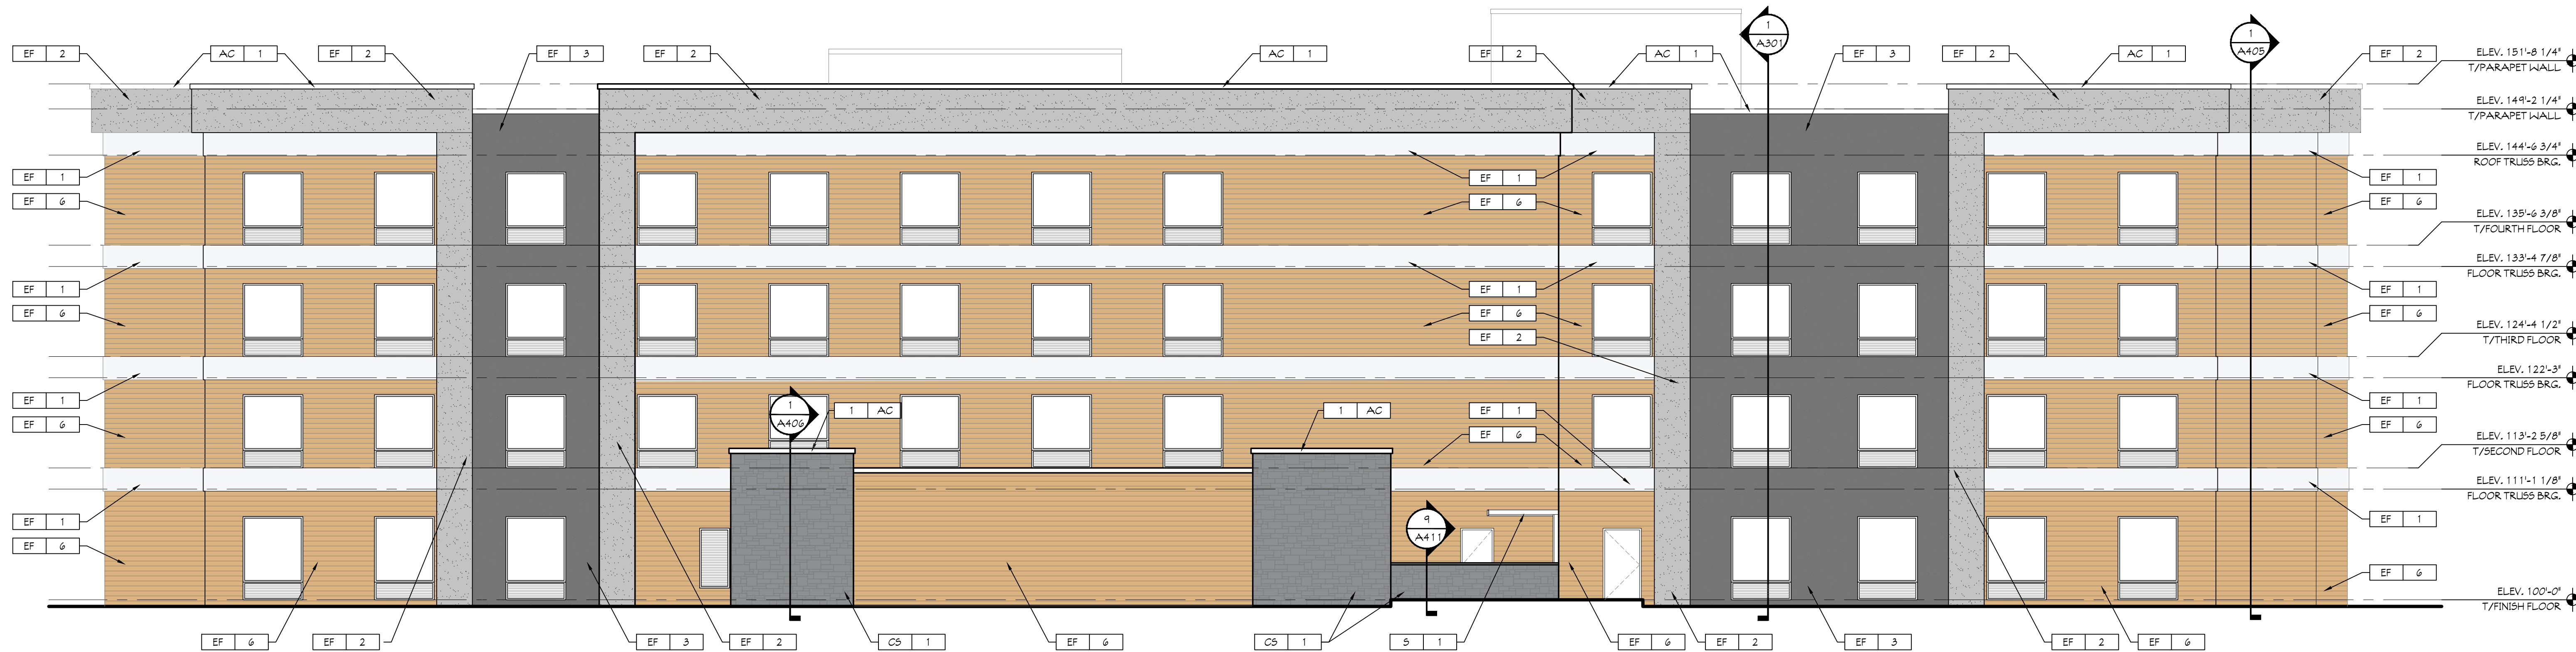


GENERAL NOTES

ALL DIMENSIONS UNLESS OTHERWISE NOTED ARE TO FACE UNLESS NOTED OTHERWISE.
* Architects
* Planners
* Construction Mgmt.
* Rule 5 and MS4 Filing
L.E.M., INC.
PHONE: (574) 537-8500
FAX: (574) 537-0808
112 NORTH MAIN STREET
GOSHEN, INDIANA 46526

These drawings are the property of L.E.M. Architectural Services and may not be reprinted, copied or used in any manner without the express written consent of L.E.M. Architectural Services.

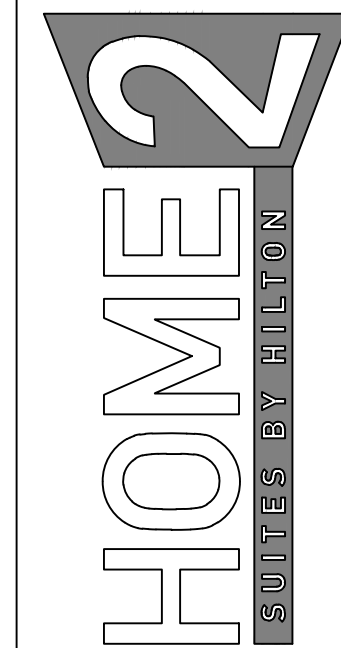

SHEET SIZE 24x36

FT. WAYNE, INDIANA

REVISIONS:

DATE: 05/01/26

JOB NO.: MAS-26-105

NAME:

EXTERIOR ELEVATIONS

SHEET:

A201