



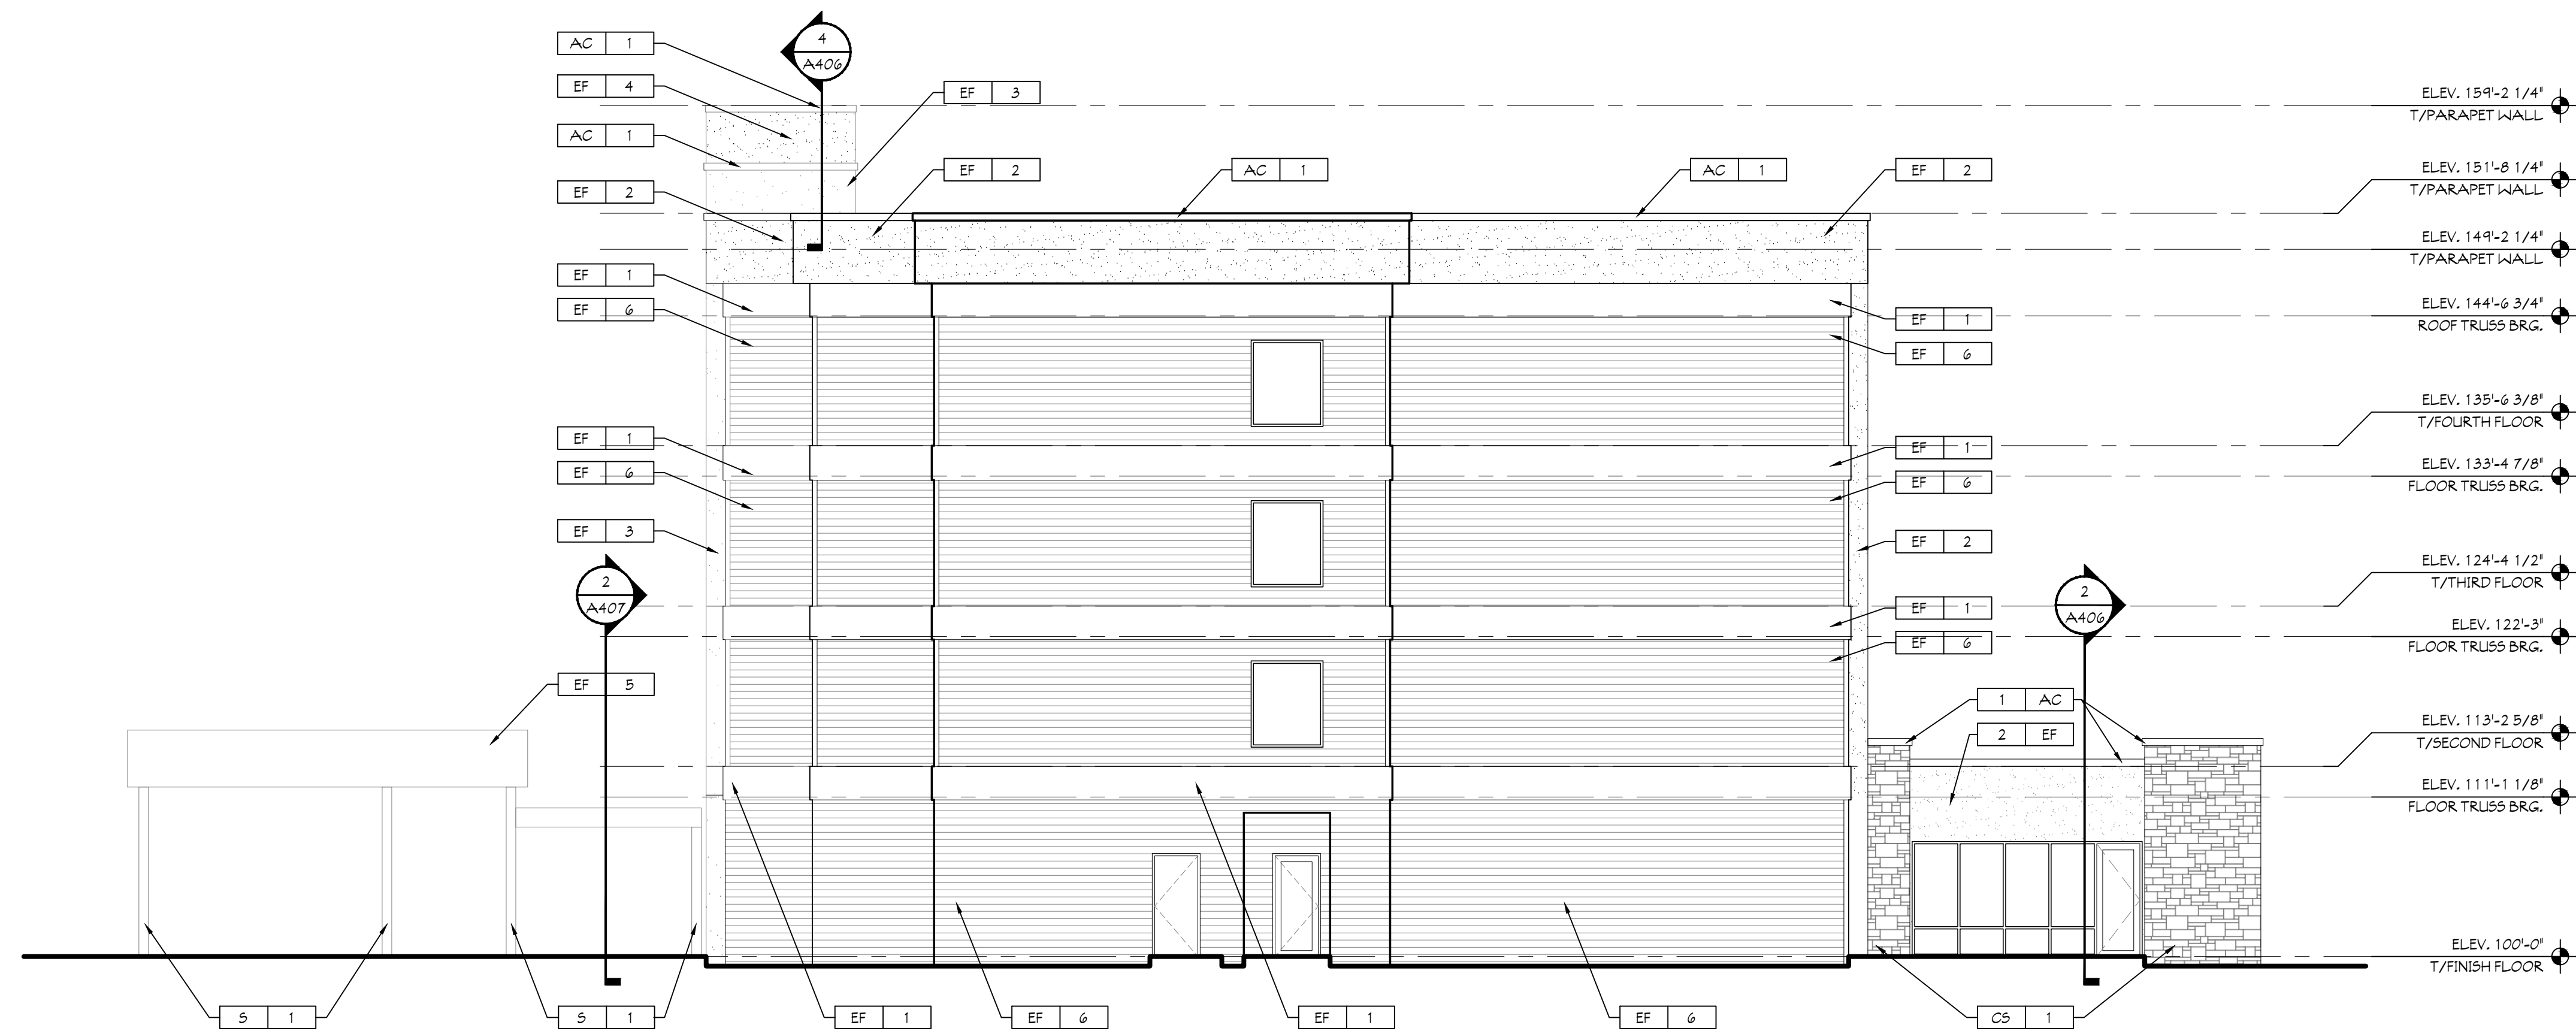

1 SIDE ELEVATION
SCALE: 1/8" = 1'-0"

MATERIAL LEGEND	
AC-1:	ALUMINUM COPING TO MATCH SURROUNDING FINISH
CS-1	CULTURE STONE COLOR TO MATCH PAINT: AS-560 FLINT
EF-1:	4" MINIMUM EIFS SYSTEM, PAINT: 2121-70 CHANTILLY
EF-2:	1 1/2" MINIMUM EIFS SYSTEM, PAINT: CW-700 SLATE
EF-3:	1 1/2" MINIMUM EIFS SYSTEM, PAINT: 2120-10 JET BLACK
EF-4:	1 1/2" MINIMUM EIFS SYSTEM, PAINT: 3A8 FLOWER POWER
EF-5:	1 1/2" MINIMUM EIFS SYSTEM, PAINT: OC-17 WHITE DOVE
EF-6:	1 1/2" MINIMUM EIFS SYSTEM, PAINT: 2165-40 DARK
S-1:	PAINTED HSS STEEL, PAINT: OC-17 WHITE DOVE
ALL PAINT COLORS ARE BY BENJAMIN MOORE AND TO BE VERIFIED WITH OWNER BEFORE SELECTING	
ALL MECHANICAL GRILLES AND LOUVERS TO BE PAINTED TO MATCH THE SURROUNDING MATERIAL COLOR	

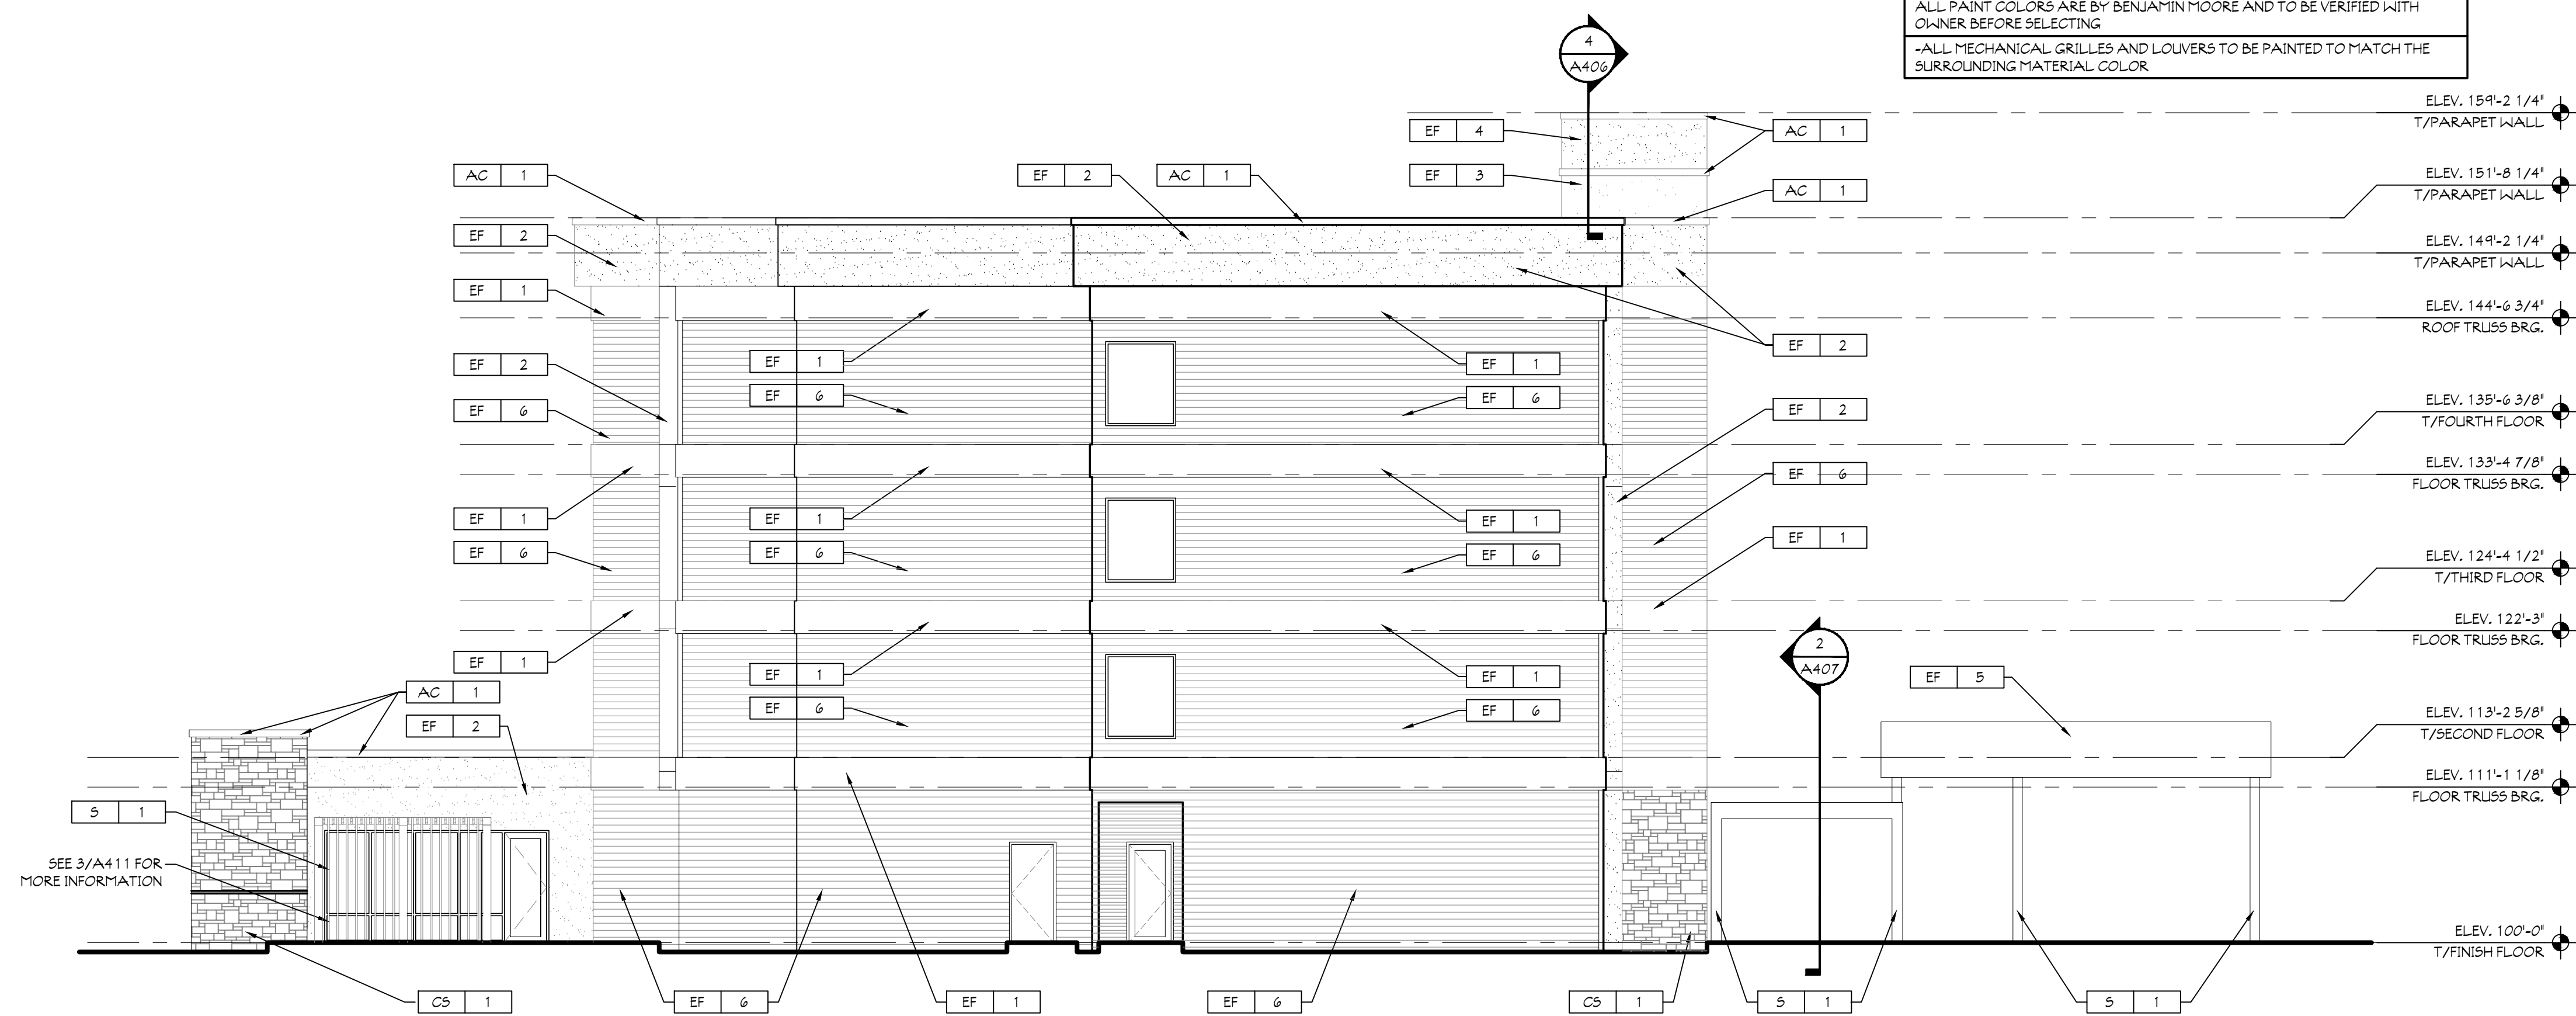

2 SIDE ELEVATION
SCALE: 1/8" = 1'-0"

GENERAL NOTES

ALTHOUGH DRAWINGS ARE DRAWN TO SCALE, THE ACCURACY OF THE DRAWINGS CANNOT BE GUARANTEED. THE CONTRACTOR SHALL BE RESPONSIBLE FOR VERIFYING ALL DIMENSIONS AND CONDITIONS OF REPRODUCTION. DIMENSIONS SHOULD BE DERIVED FROM DIMENSIONED PLANS.

ALL DIMENSIONS GROSS OPENING SIZES AND FINISHES SHALL NOT BE HELD RESPONSIBLE FOR ANY GENERAL CONTRACTOR. MUST ASSESS THE GENERAL CONTRACTOR'S ATTENTION PRIOR TO CONSTRUCTION.

* Architects
* Planners
* Construction Mgmt.
* Rule 5 and MS4 Filing
* PHONE: (574) 537-5600
* FAX: (574) 537-0808

MAUST ARCHITECTURAL SERVICES
DIVISION OF
L.E.M., INC.
112 NORTH MAIN STREET
GOSHEN, INDIANA 46526

HOME 2
SUITES BY HILTON

SHEET SIZE 24x36

FT. WAYNE, INDIANA

REVISIONS:

DATE: 05/01/26

JOB NO.: MAS-26-105

NAME:

EXTERIOR ELEVATIONS

SHEET:

A202