


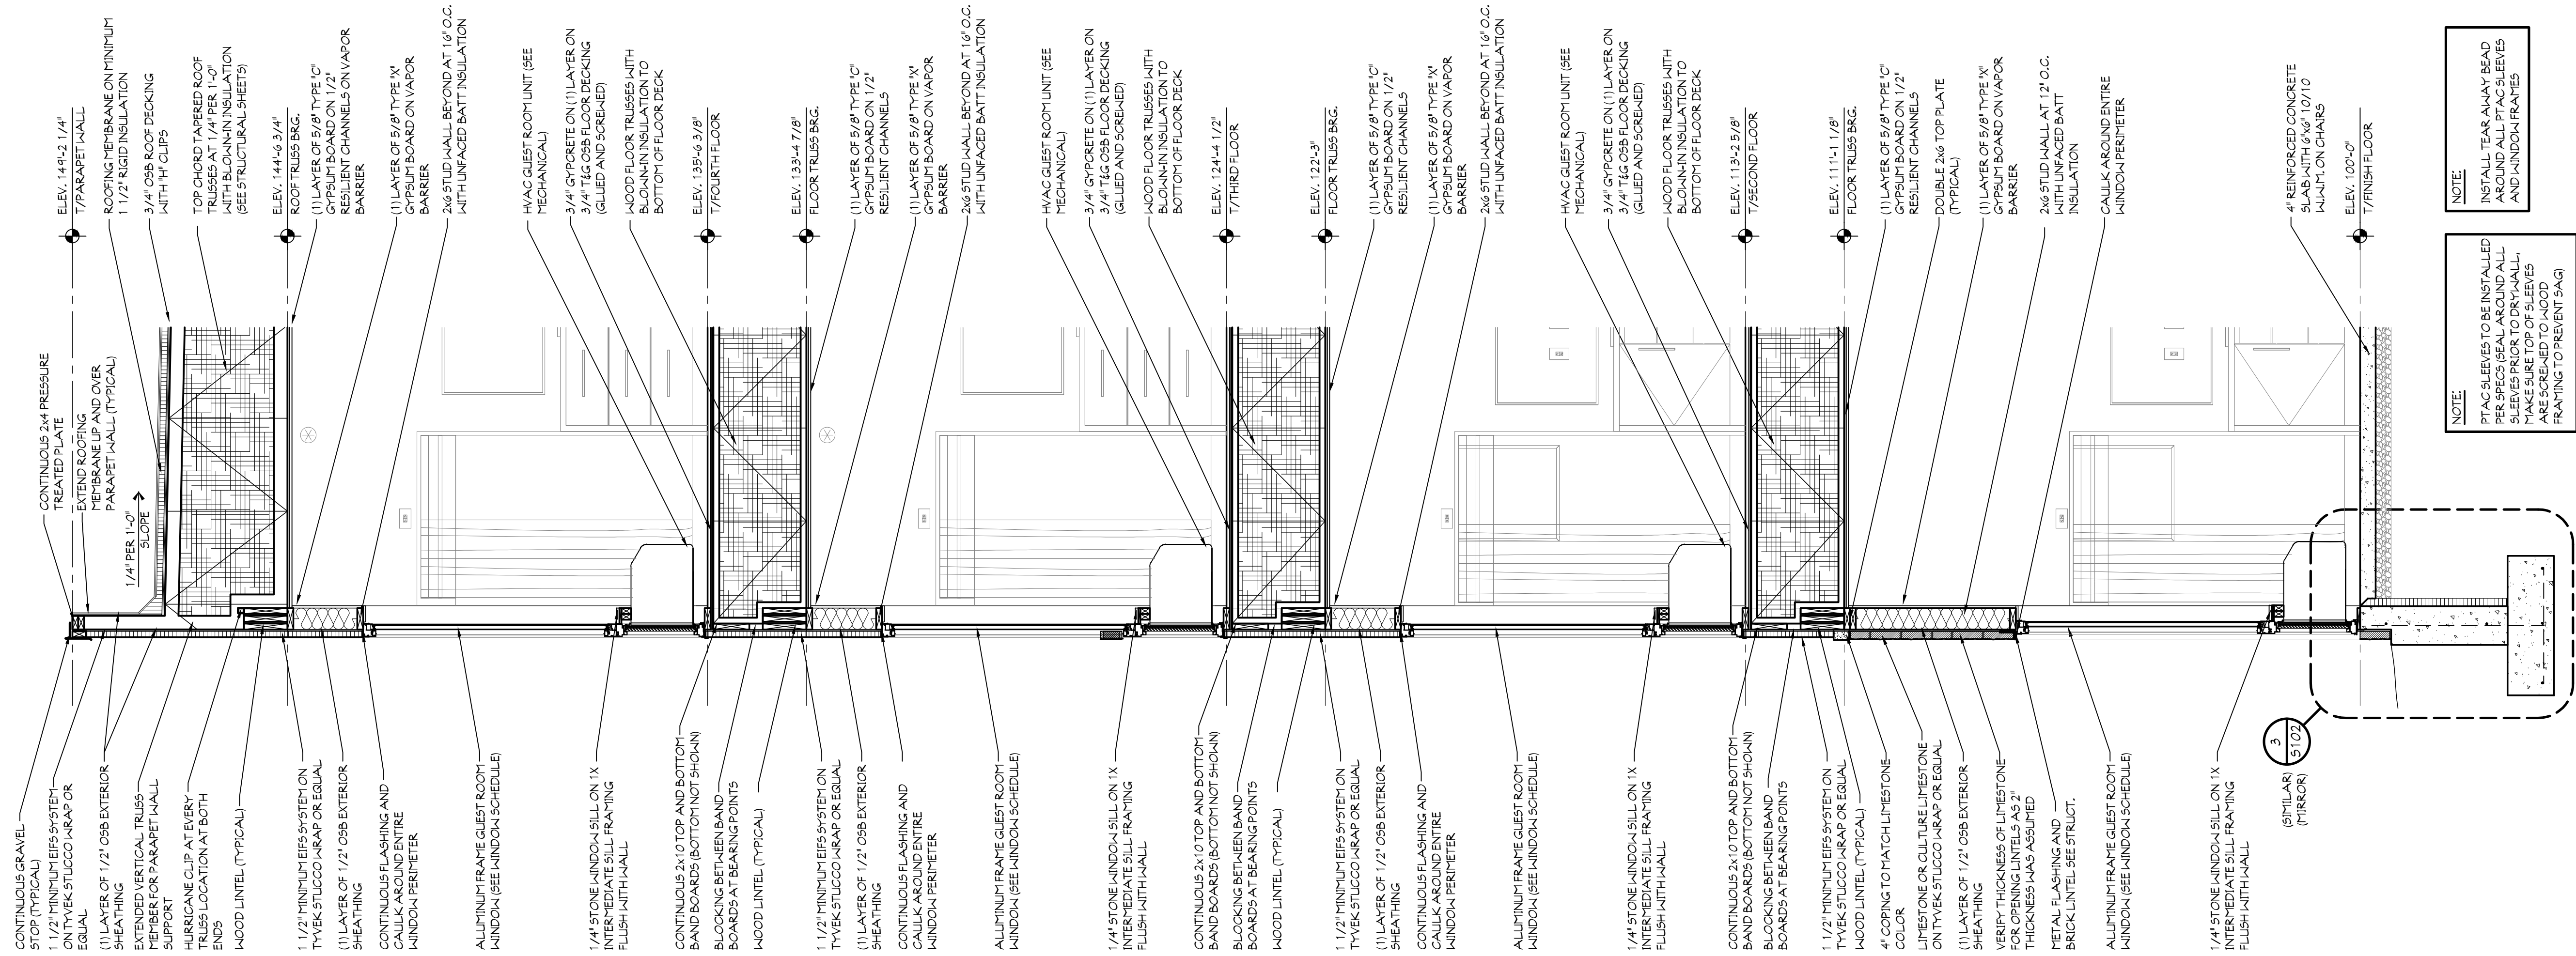


1 EXTERIOR WALL SECTION
SCALE: 1/2" = 1'-0"

NOTE:
PTAC SLEEVES TO BE INSTALLED PER SPECS (SEAL AROUND ALL SLEEVES PRIOR TO DRY WALL, MAKE SURE TOP OF SLEEVES ARE SECURED TO WOOD FRAMING TO PREVENT SAG)

NOTE:
INSTALL TEAR AWAY BEAD AROUND ALL PTAC SLEEVES AND WINDOW FRAMES

2 CORRIDOR STEEL SECTION
SCALE: 1" = 1'-0"

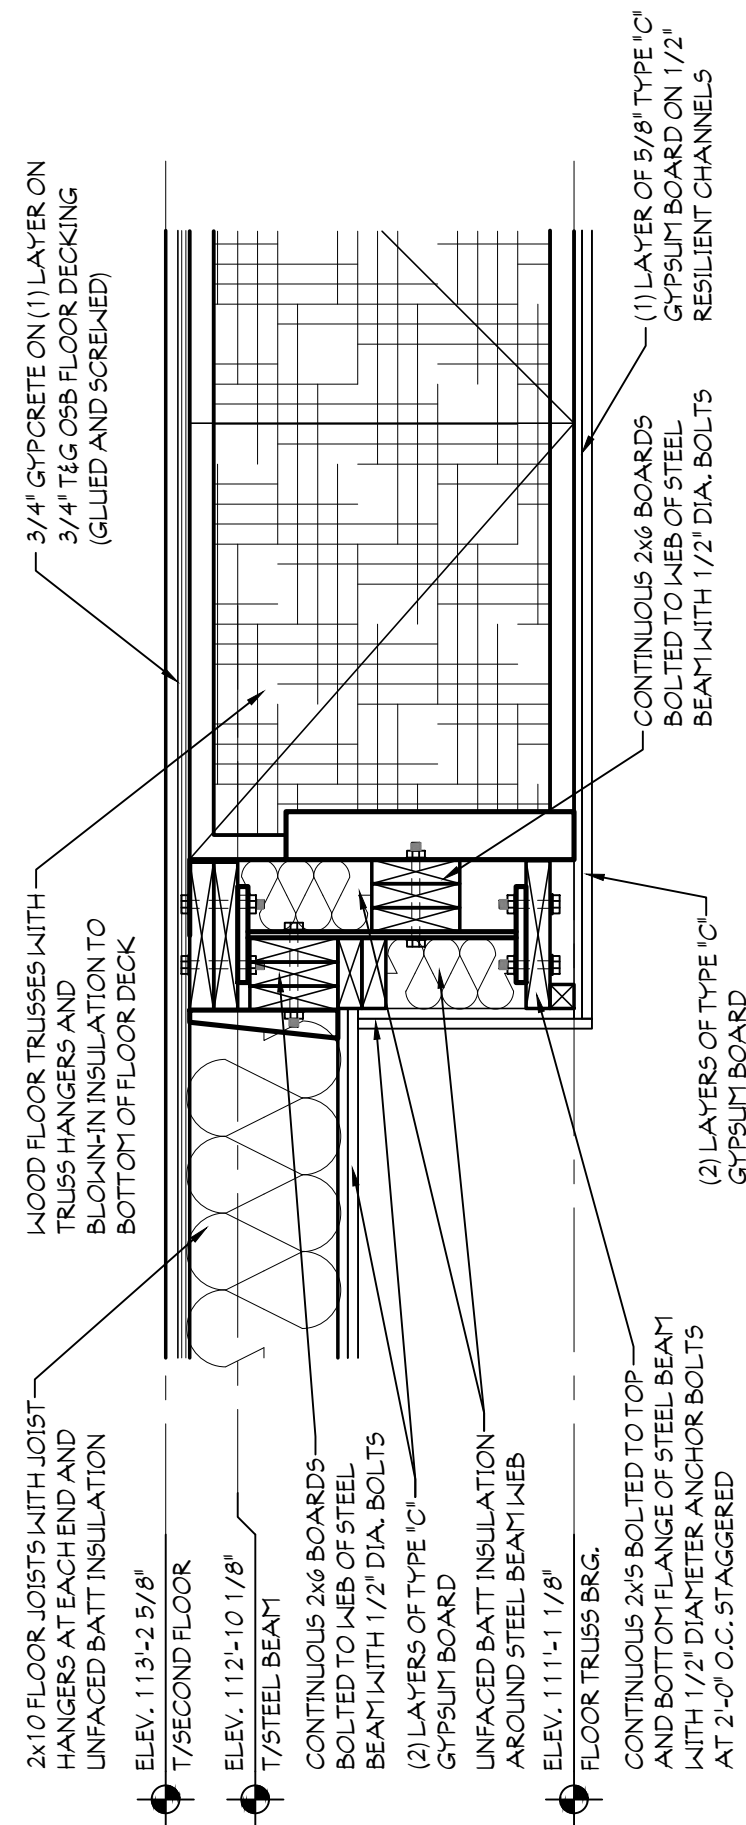

A402

SHEET:

ENLARGED BUILDING SECTIONS

NAME:

JOB NO.: MAS-26-105

DATE: 05/01/26

PRELIMINARY - NOT FOR CONSTRUCTION

REVISIONS:

FT. WAYNE, INDIANA

SHEET SIZE 24x36

HOME 2
SUITES BY HILTON

MAUIST ARCHITECTURAL SERVICES
DIVISION OF L.E.M., INC.
112 NORTH MAIN STREET
GOSHEN, INDIANA 46526
ARCHITECTS
PLUMBERS
ELECTRICIANS
MECHANICAL
* Rule 5 and MS4 Filing
PHONE: (574) 537-6500
FAX: (574) 537-0808

GENERAL NOTES
ALTHOUGH DRAWINGS ARE DRAWN TO SCALE, THE ACCURACY OF THE DRAWINGS CANNOT BE GUARANTEED. THE USER SHALL BE RESPONSIBLE FOR THE VERIFICATION OF DIMENSIONS AND MATERIALS. DIMENSIONS SHOULD BE DERIVED FROM DIMENSIONED PLANS.
ALL DIMENSIONS UNLESS OTHERWISE NOTED SHALL BE IN FEET AND INCHES. DIMENSIONS SHOULD BE DERIVED FROM DIMENSIONED PLANS.
SERVICES SHALL NOT BE HELD RESPONSIBLE FOR ANY CONSTRUCTION DEFECTS OR OMISSIONS THAT HAVE BEEN BROUGHT TO THEIR ATTENTION PRIOR TO CONSTRUCTION.