


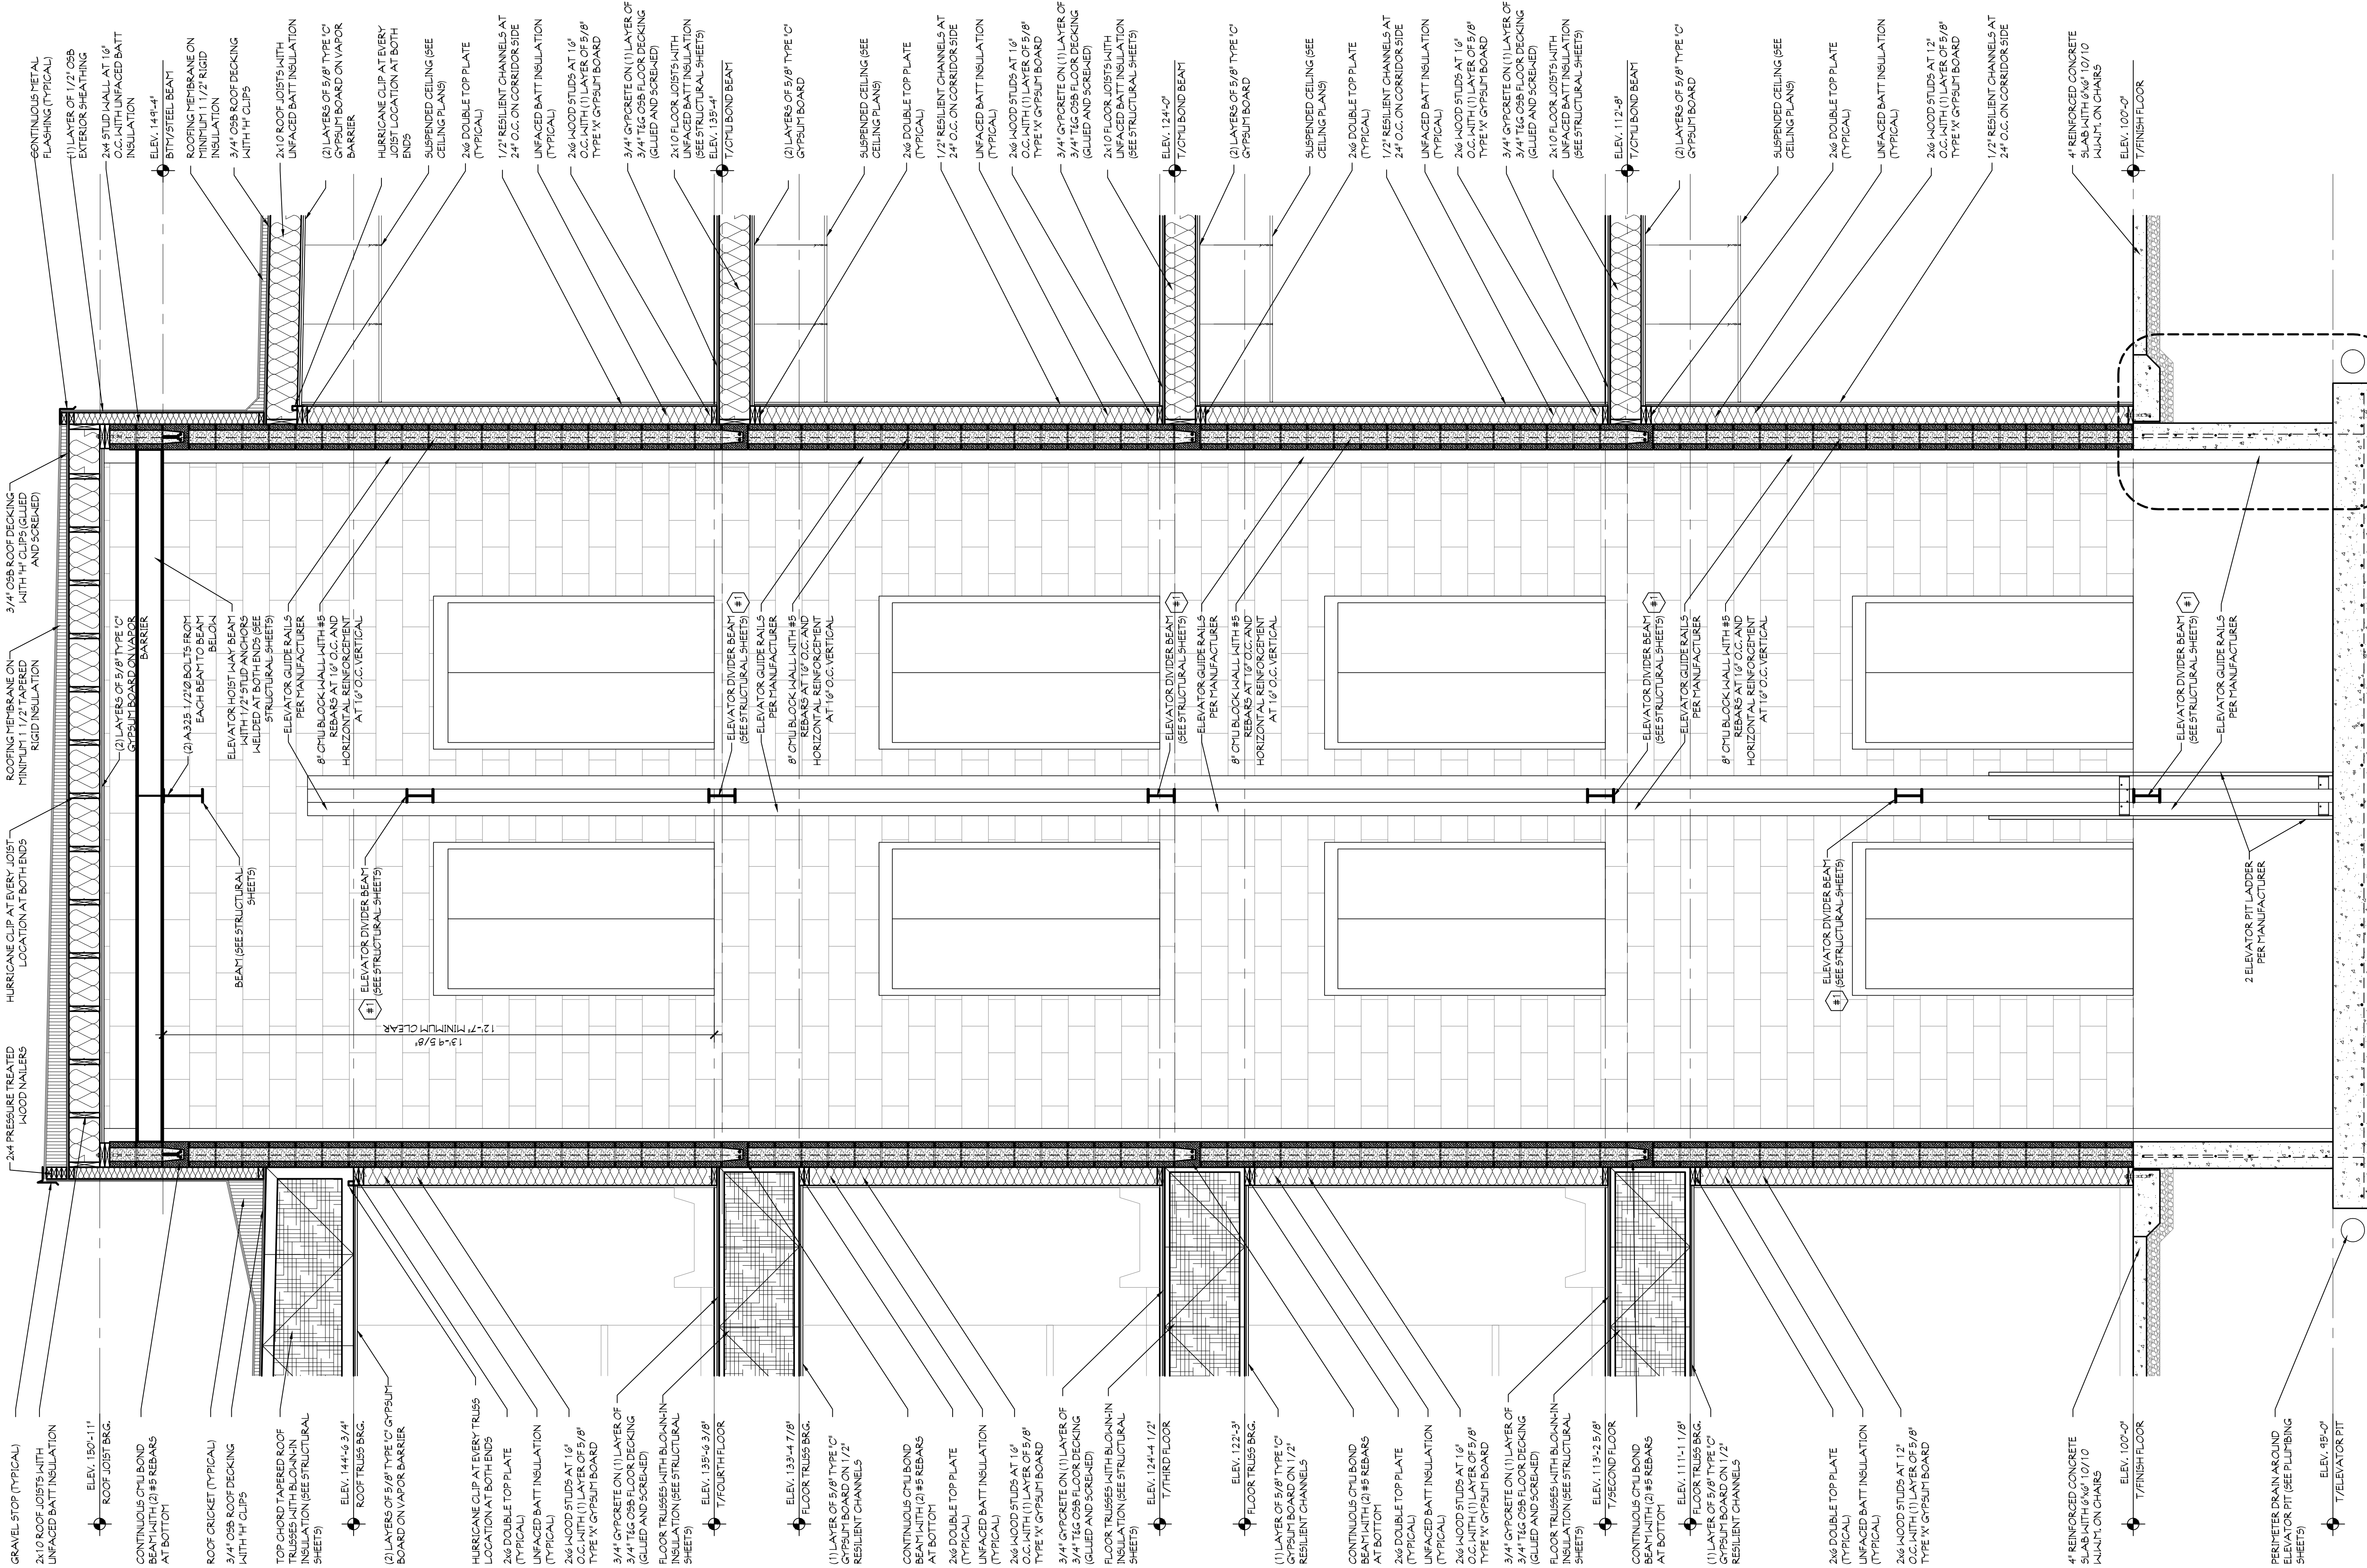

NOTE: ELEVATOR CAB TO BE STRETCHER COMPLAINT

NOTE: ELEVATOR TO HAVE FIRE RATED BELTS

NOTE: ELEVATOR ENGINEERING DRAWINGS SHOULD BE APPROVED AS SOON AS THE SHAFT IS BUILT AND ORDERED.

1 ELEVATOR SECTION
SCALE: 1/2" = 1'-0"

NOTE: ELEVATOR SHAFT TO BE COORDINATED WITH SELECTED ELEVATOR MANUFACTURER

NOTE: SEE ELEVATOR SHOP DRAWINGS FOR EXACT LOCATION OF DIVIDER BEAMS, HOIST AND SAFETY BEAMS

NOTE: PERIMETER DRAIN AROUND PERIMETER PIT (SEE PLUMBING SHEETS)

GENERAL NOTES

ALTHOUGH DRAWINGS ARE DRAWN TO SCALE, THE ACCURACY OF THE DRAWINGS CANNOT BE GUARANTEED. THE CONTRACTOR SHALL BE RESPONSIBLE FOR THE VERIFICATION OF ALL DIMENSIONS AND CONDITIONS PRIOR TO CONSTRUCTION.

ALL DIMENSIONS UNLESS OTHERWISE NOTED SHALL BE IN FEET AND INCHES. DIMENSIONS SHALL BE BROUGHT TO THE ATTENTION OF THE CONTRACTOR PRIOR TO CONSTRUCTION.

* Architects
Plumbers
Electricians
Mechanical
Construction Mgmt
* Rule 5 and MS4 Filing
L.E.M., INC.
112 NORTH MAIN STREET
GOSHEN, INDIANA 46526
PHONE: (574) 537-8500
FAX: (574) 537-0808

These drawings are the property of Maust Architectural Services and may not be reprinted, copied or used in any way without the written consent of Maust Architectural Services.

HOME 2
SUITES BY HILTON

SHEET SIZE 24x36

FT. WAYNE, INDIANA

REVISIONS:

DATE: 05/01/26
JOB NO.: MAS-26-105
NAME: ELEVATOR SECTION
SHEET: A403

PRELIMINARY - NOT FOR CONSTRUCTION