


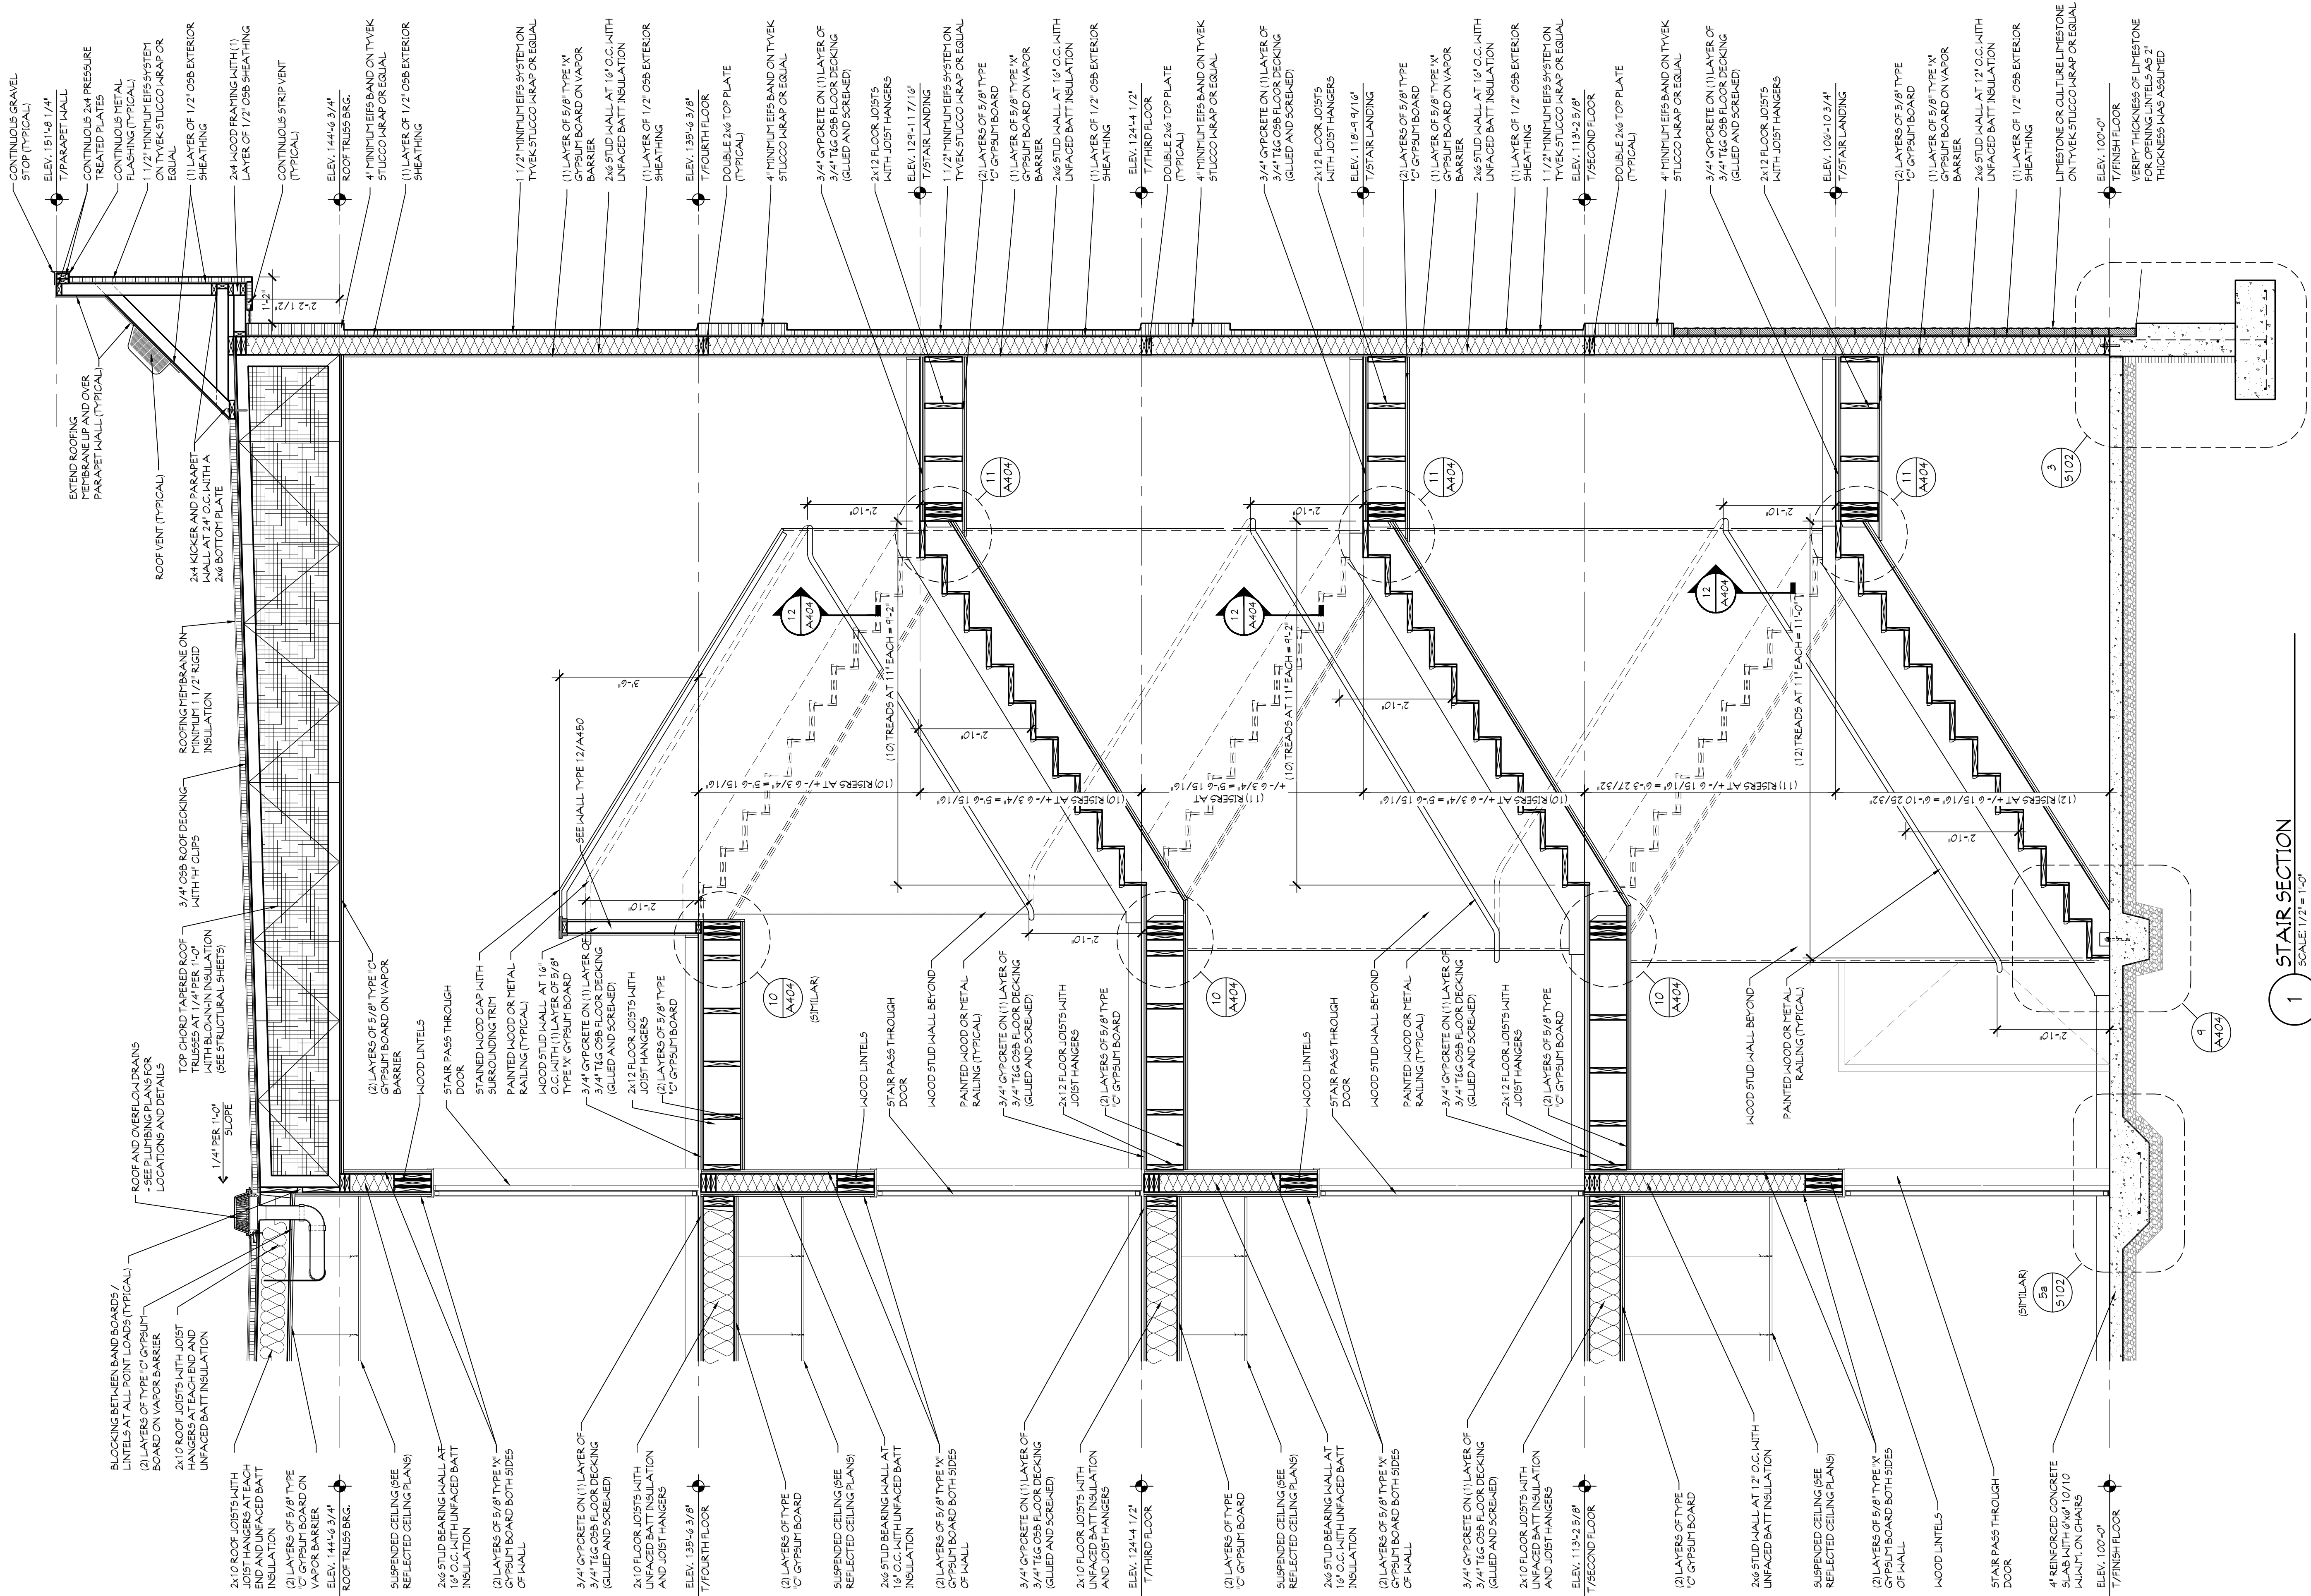

GENERAL NOTES

ALTHOUGH DRAWINGS ARE DRAWN TO SCALE, THE
ACCURACY OF THE DRAWINGS CANNOT BE
GUARANTEED. THE USER SHALL BE RESPONSIBLE
FOR REPRODUCTION, DIMENSIONS SHOULD BE DERIVED
FROM DIMENSIONED PLANS.
ALL DIMENSIONS UNLESS OTHERWISE NOTED
SHALL BE IN FEET AND INCHES. FRACTIONS
SHALL BE IN 16THS OF AN INCH. THE
GENERAL CONTRACTOR SHALL BE RESPONSIBLE FOR ANY
SERVICES NOT SHOWN OR NOTED AS NOT SHOWN.
BROUGHT TO THEIR ATTENTION PRIOR TO
CONSTRUCTION.

* Architects
* Plumbers
* Construction Mgmt.
* Rule 5 and MS4 Filing
MAUST ARCHITECTURAL
SERVICES
DIVISION OF
L.E.M., INC.
112 NORTH MAIN STREET
GOSHEN, INDIANA 46526
PHONE: (574) 537-4500
FAX: (574) 537-0808

HOME2
SUITES BY HILTON

SHEET SIZE 24x36

FT. WAYNE, INDIANA

REVISIONS:

PRELIMINARY - NOT
FOR CONSTRUCTION

DATE: 05/01/26

JOB NO.: MAS-26-105

NAME:

STAIR SECTION

SHEET:

A405