




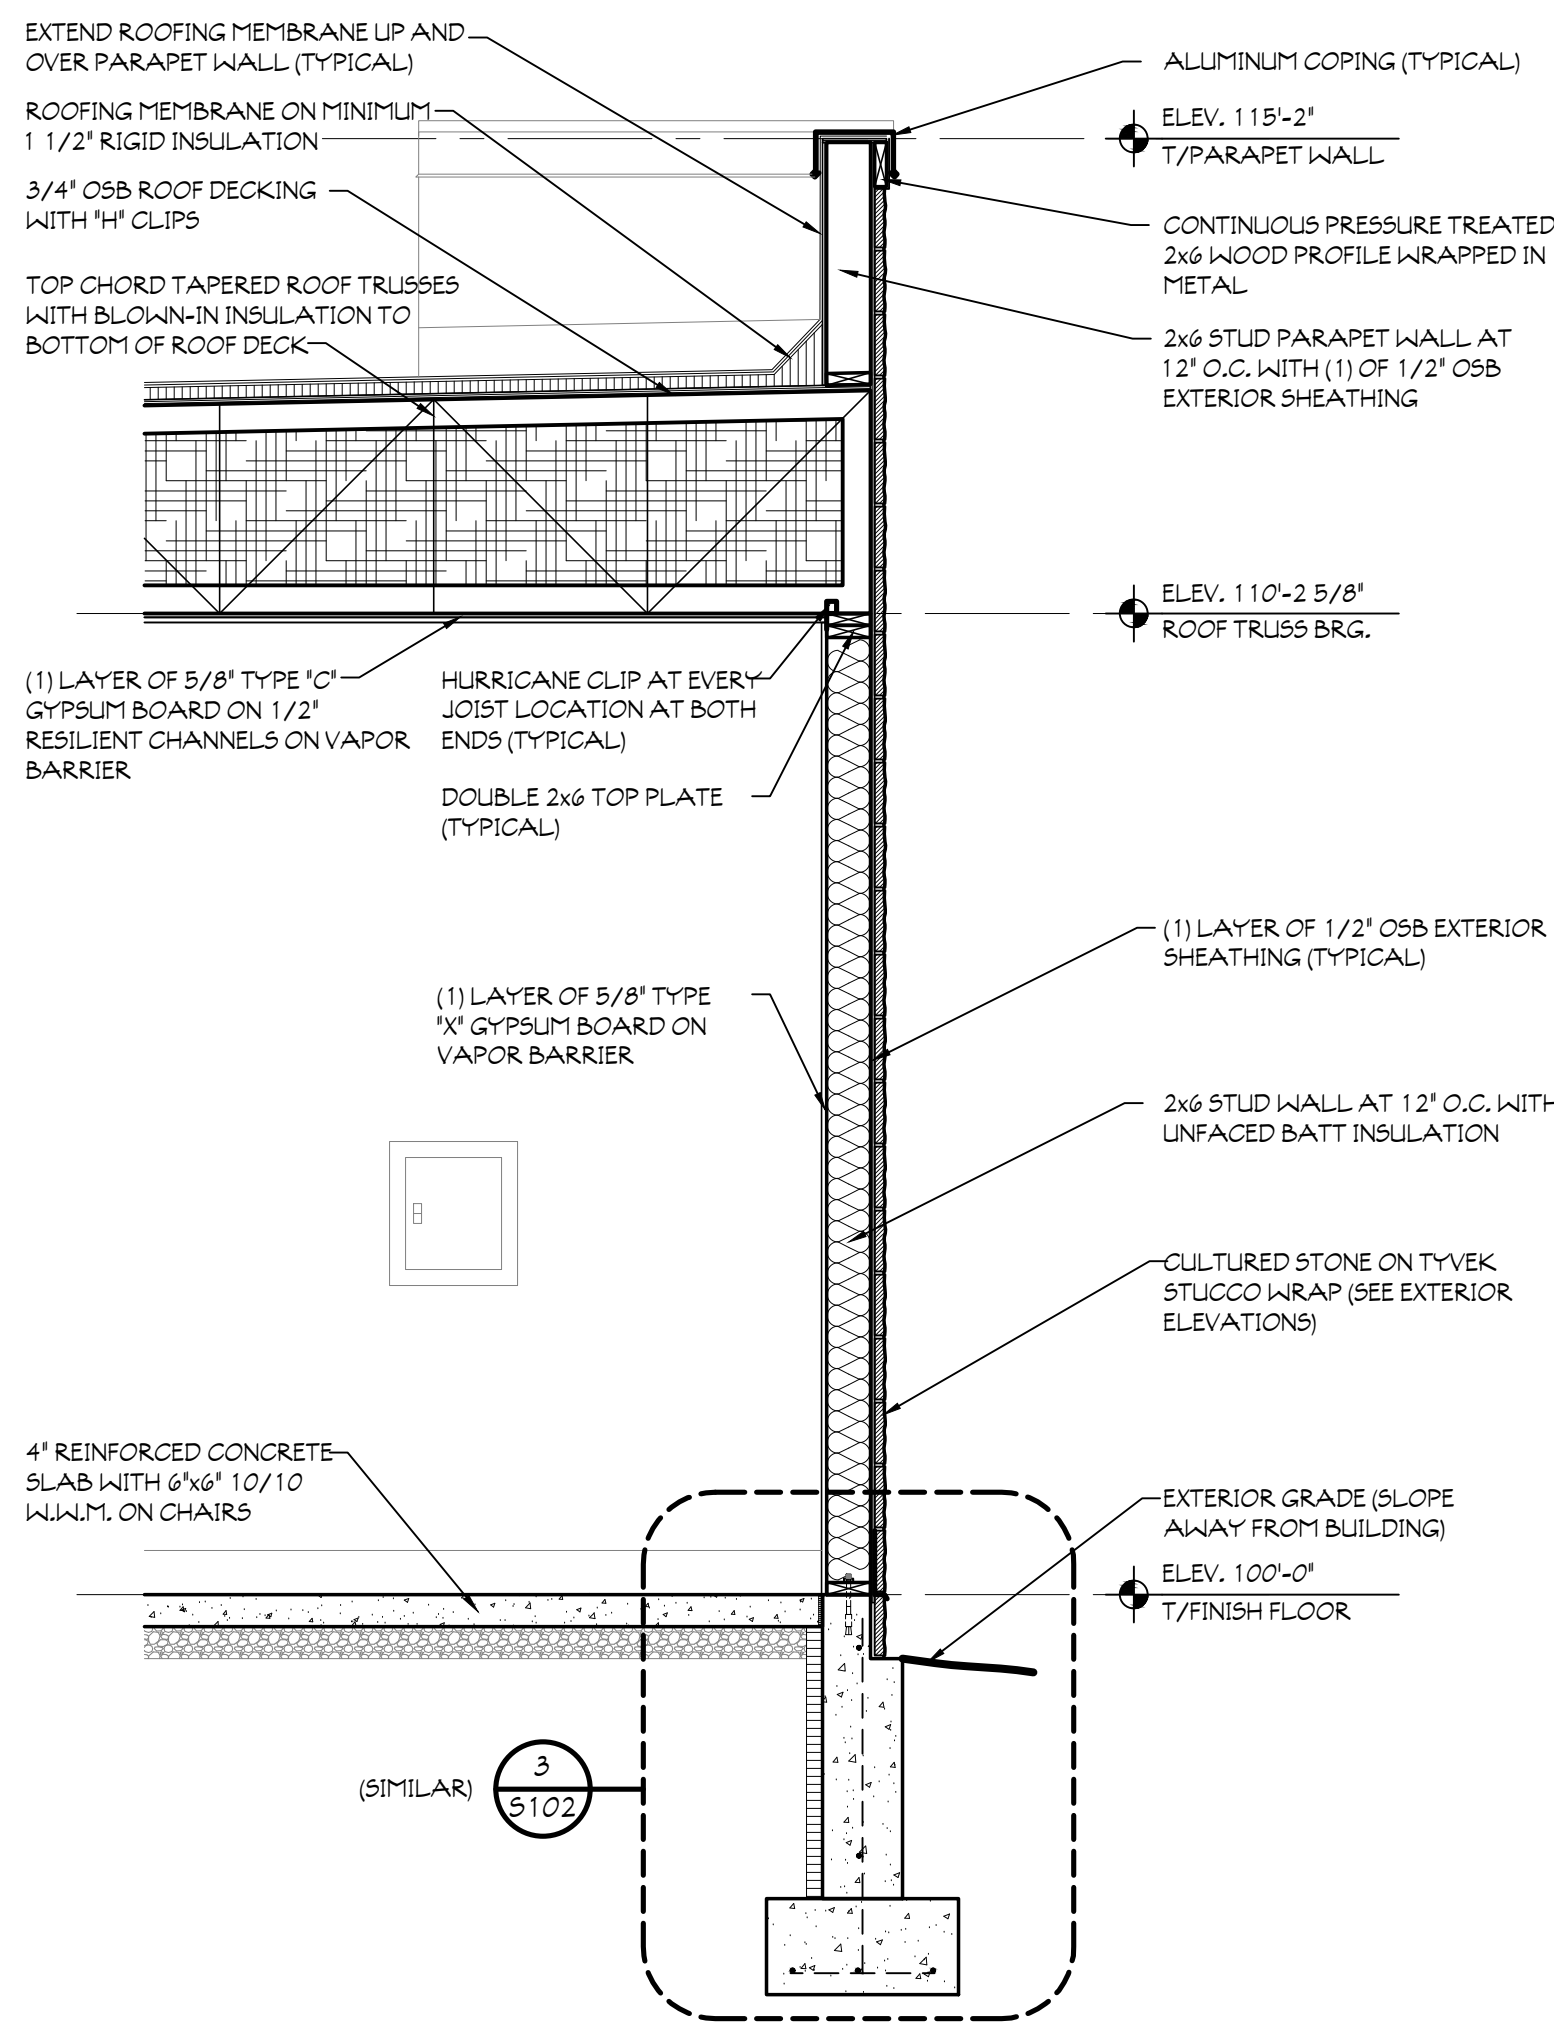


1 SINGLE STORY SECTION
SCALE: 1/2" = 1'-0"
AT POOL EXTERIOR WALL

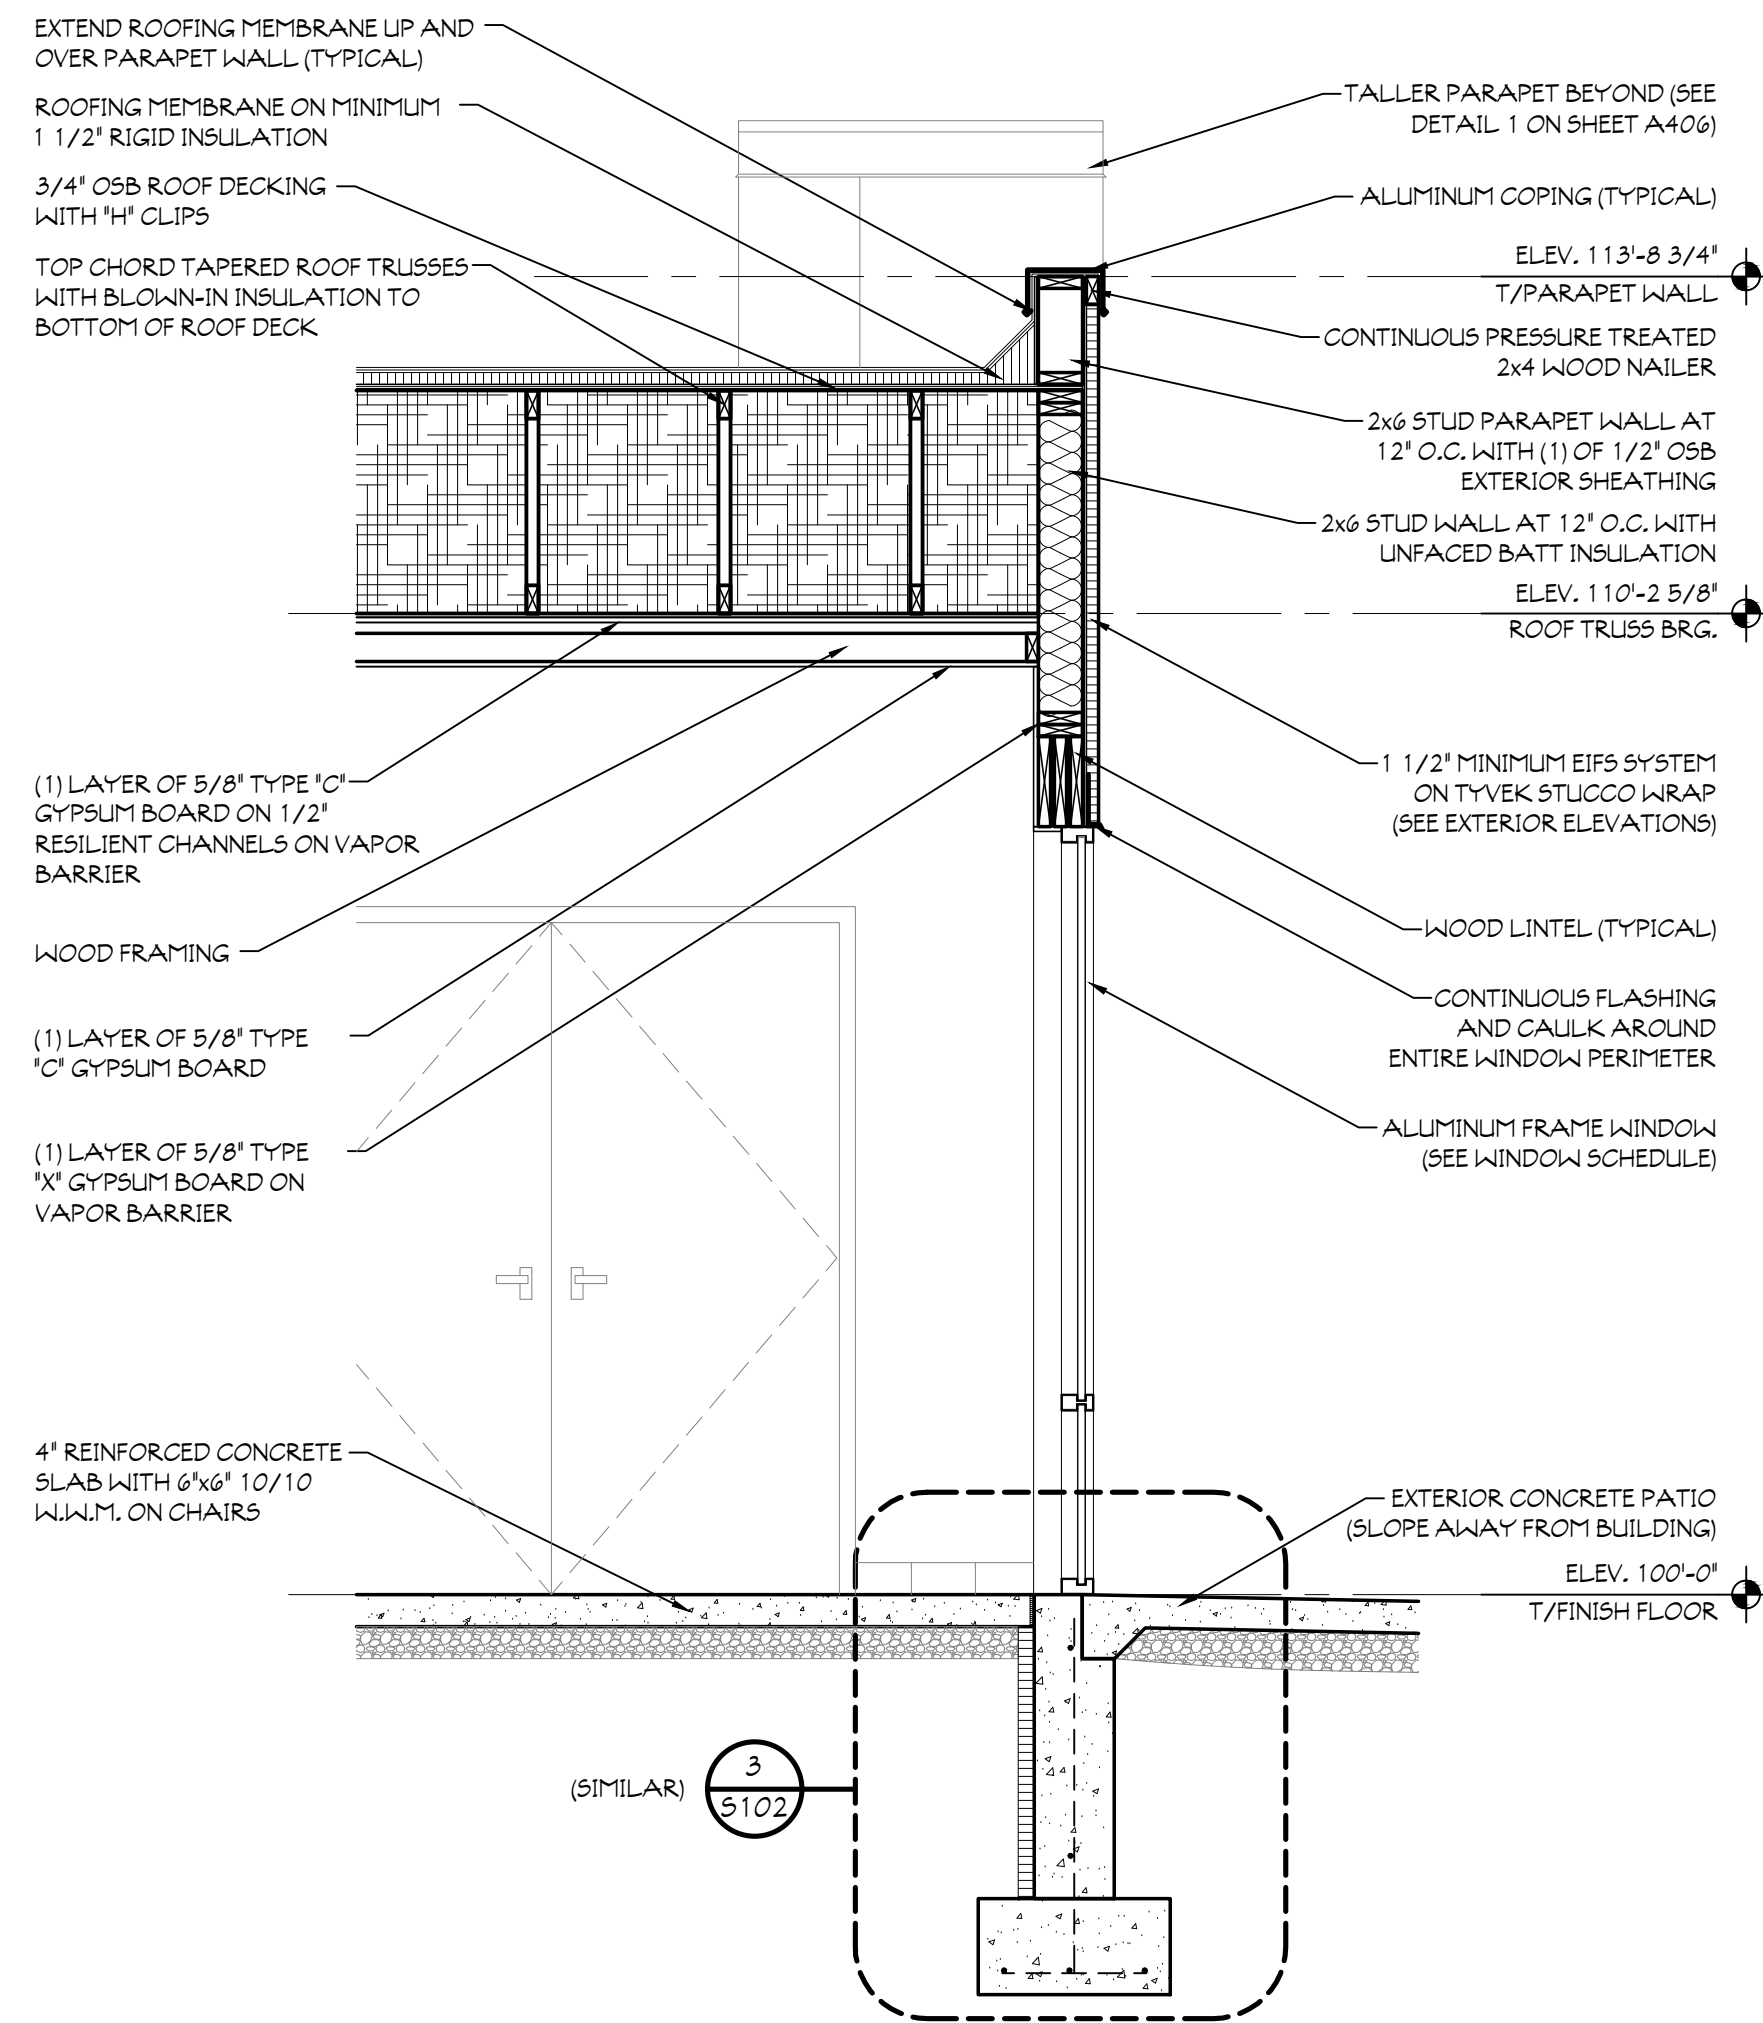


2 SINGLE STORY SECTION
SCALE: 1/2" = 1'-0"
AT POOL EXTERIOR WALL

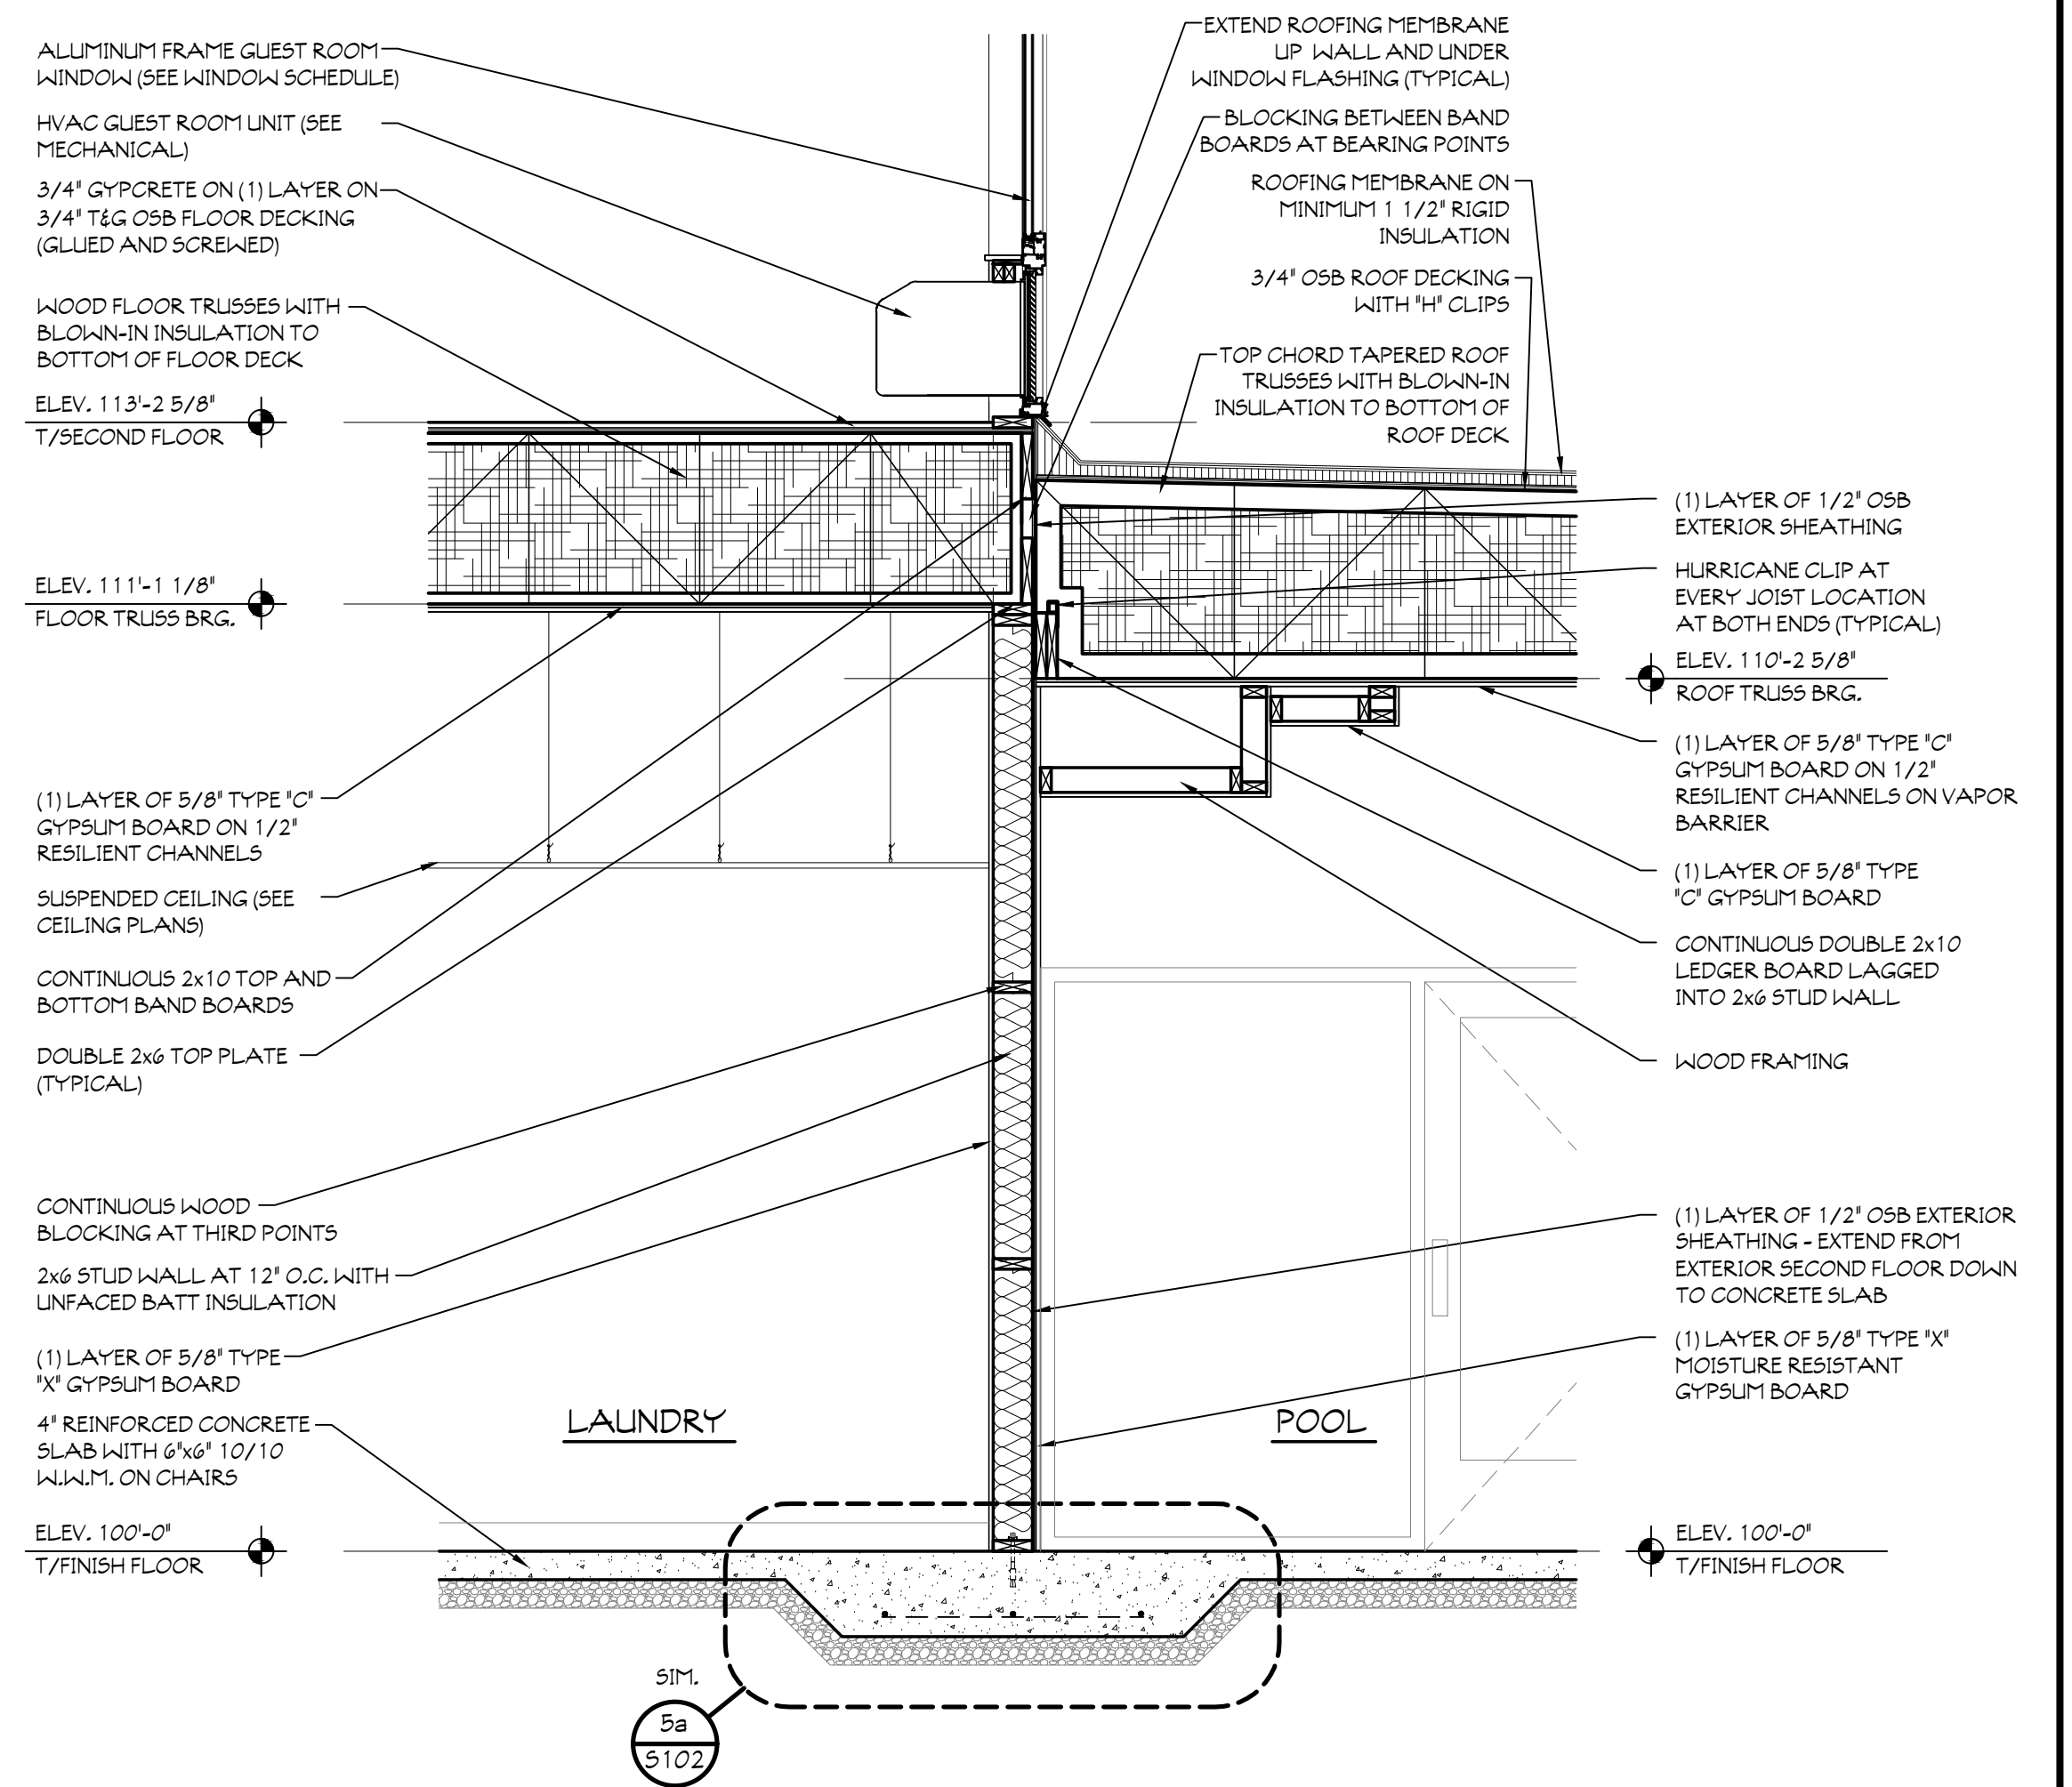

3 INTERIOR BEARING WALL SECTION
SCALE: 1/2" = 1'-0"
AT POOL INTERIOR WALL

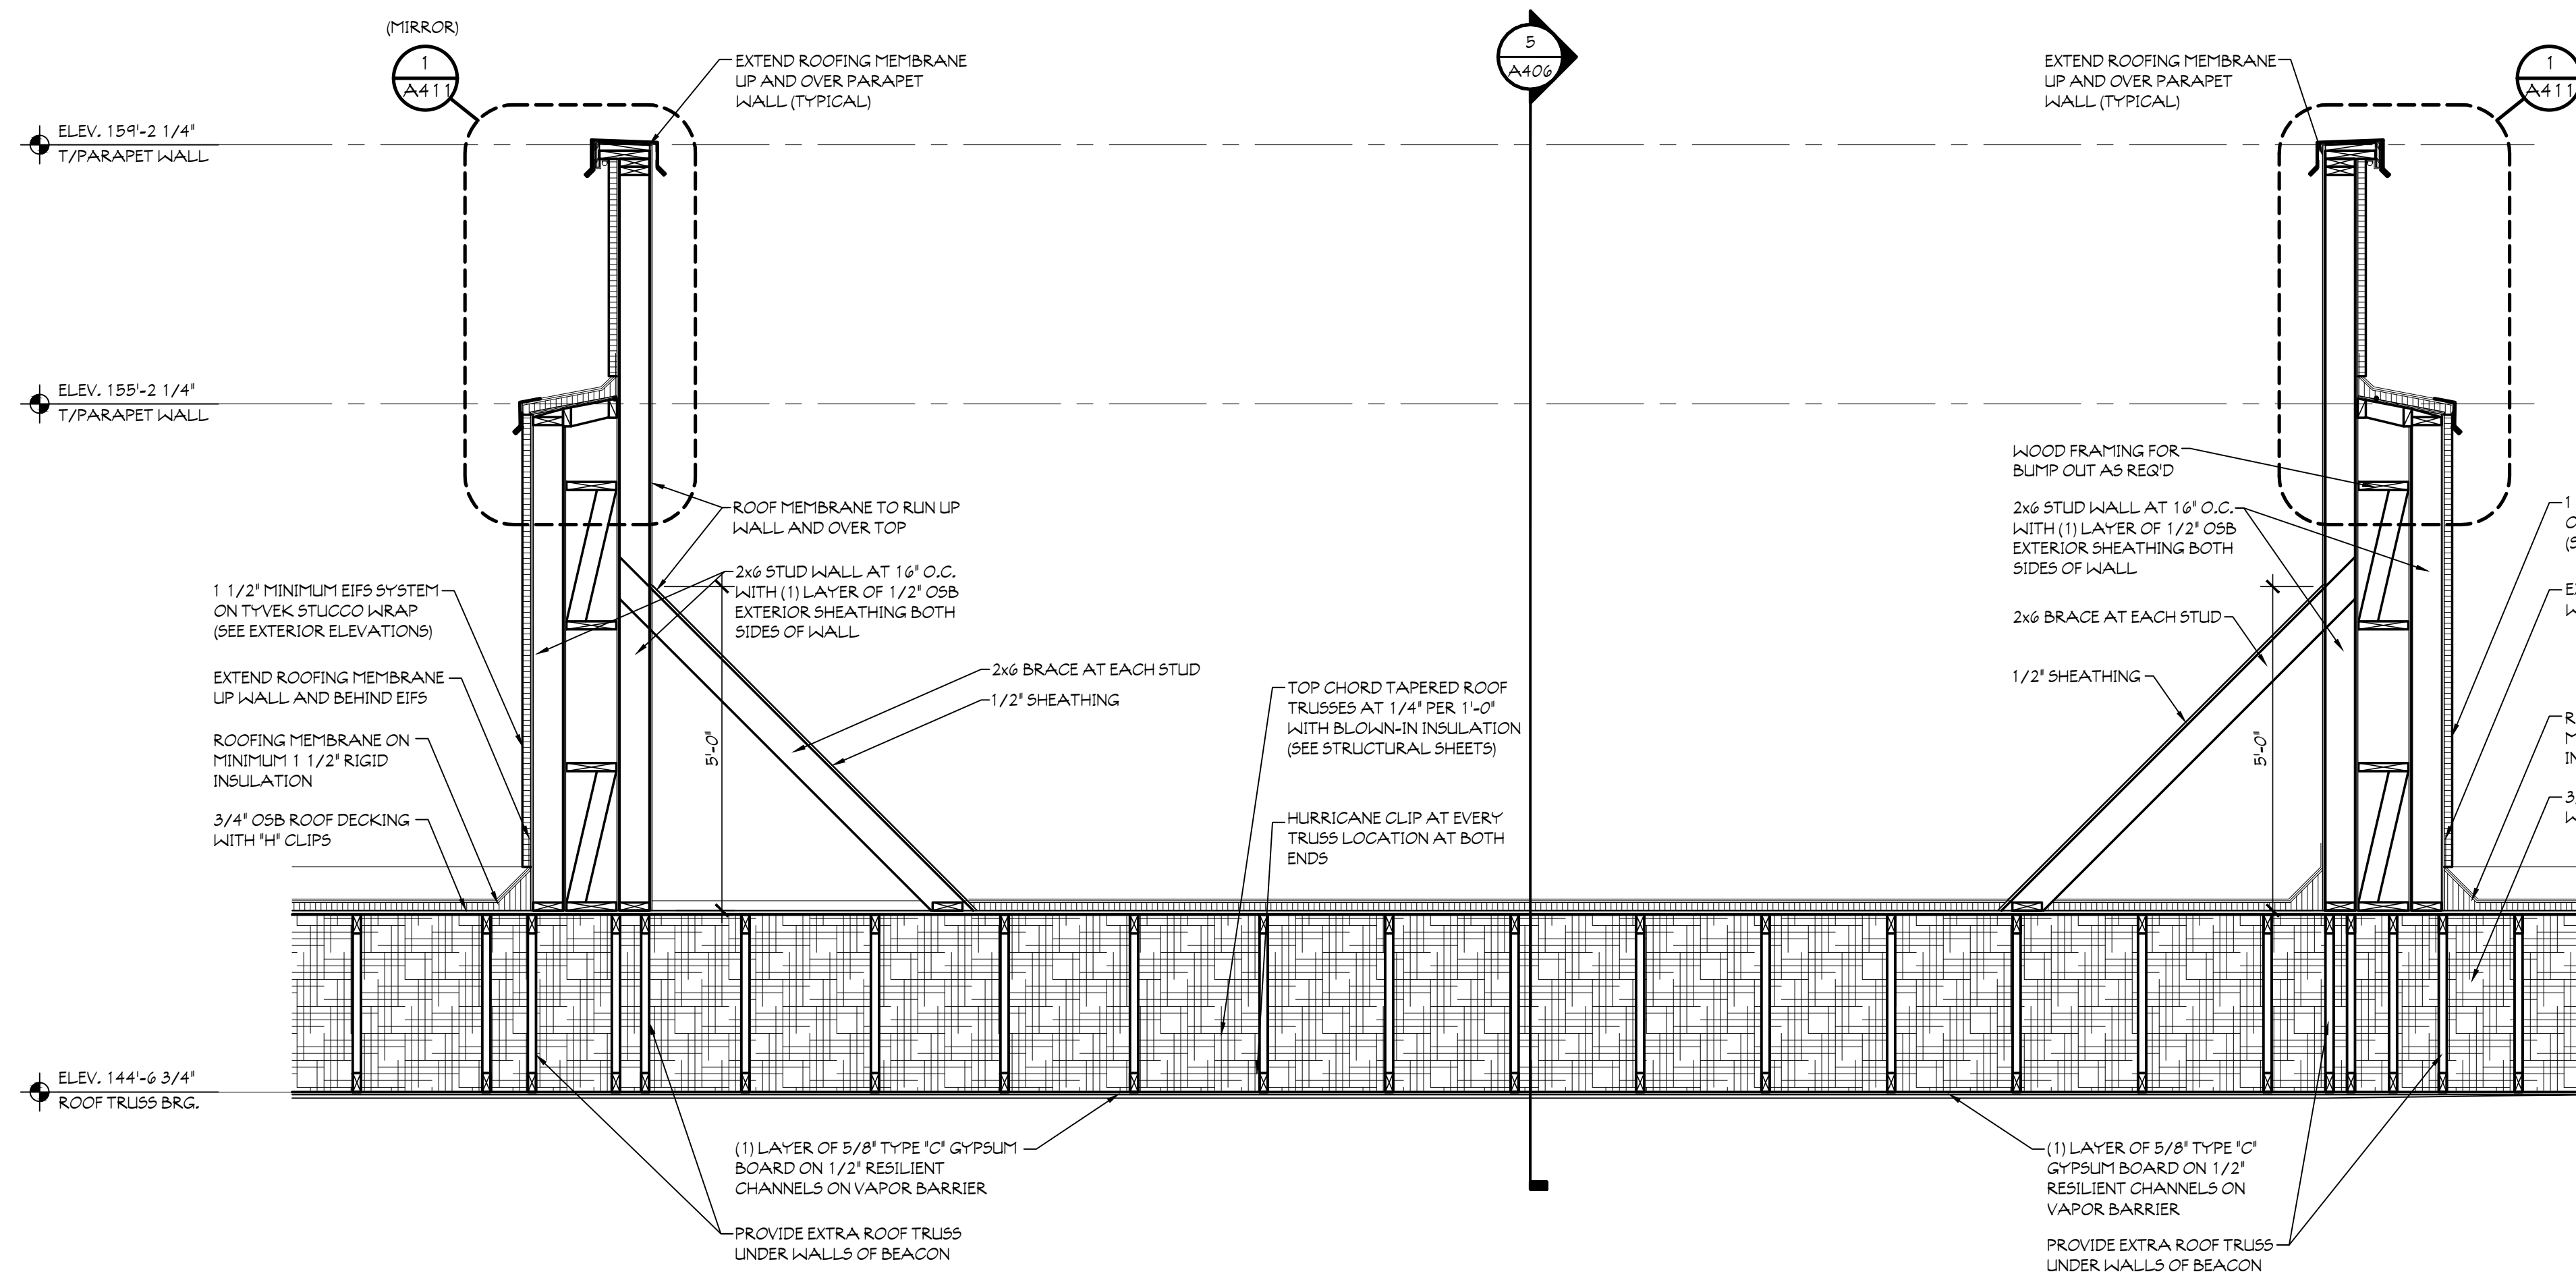

4 BEACON SECTION
SCALE: 1/2" = 1'-0"

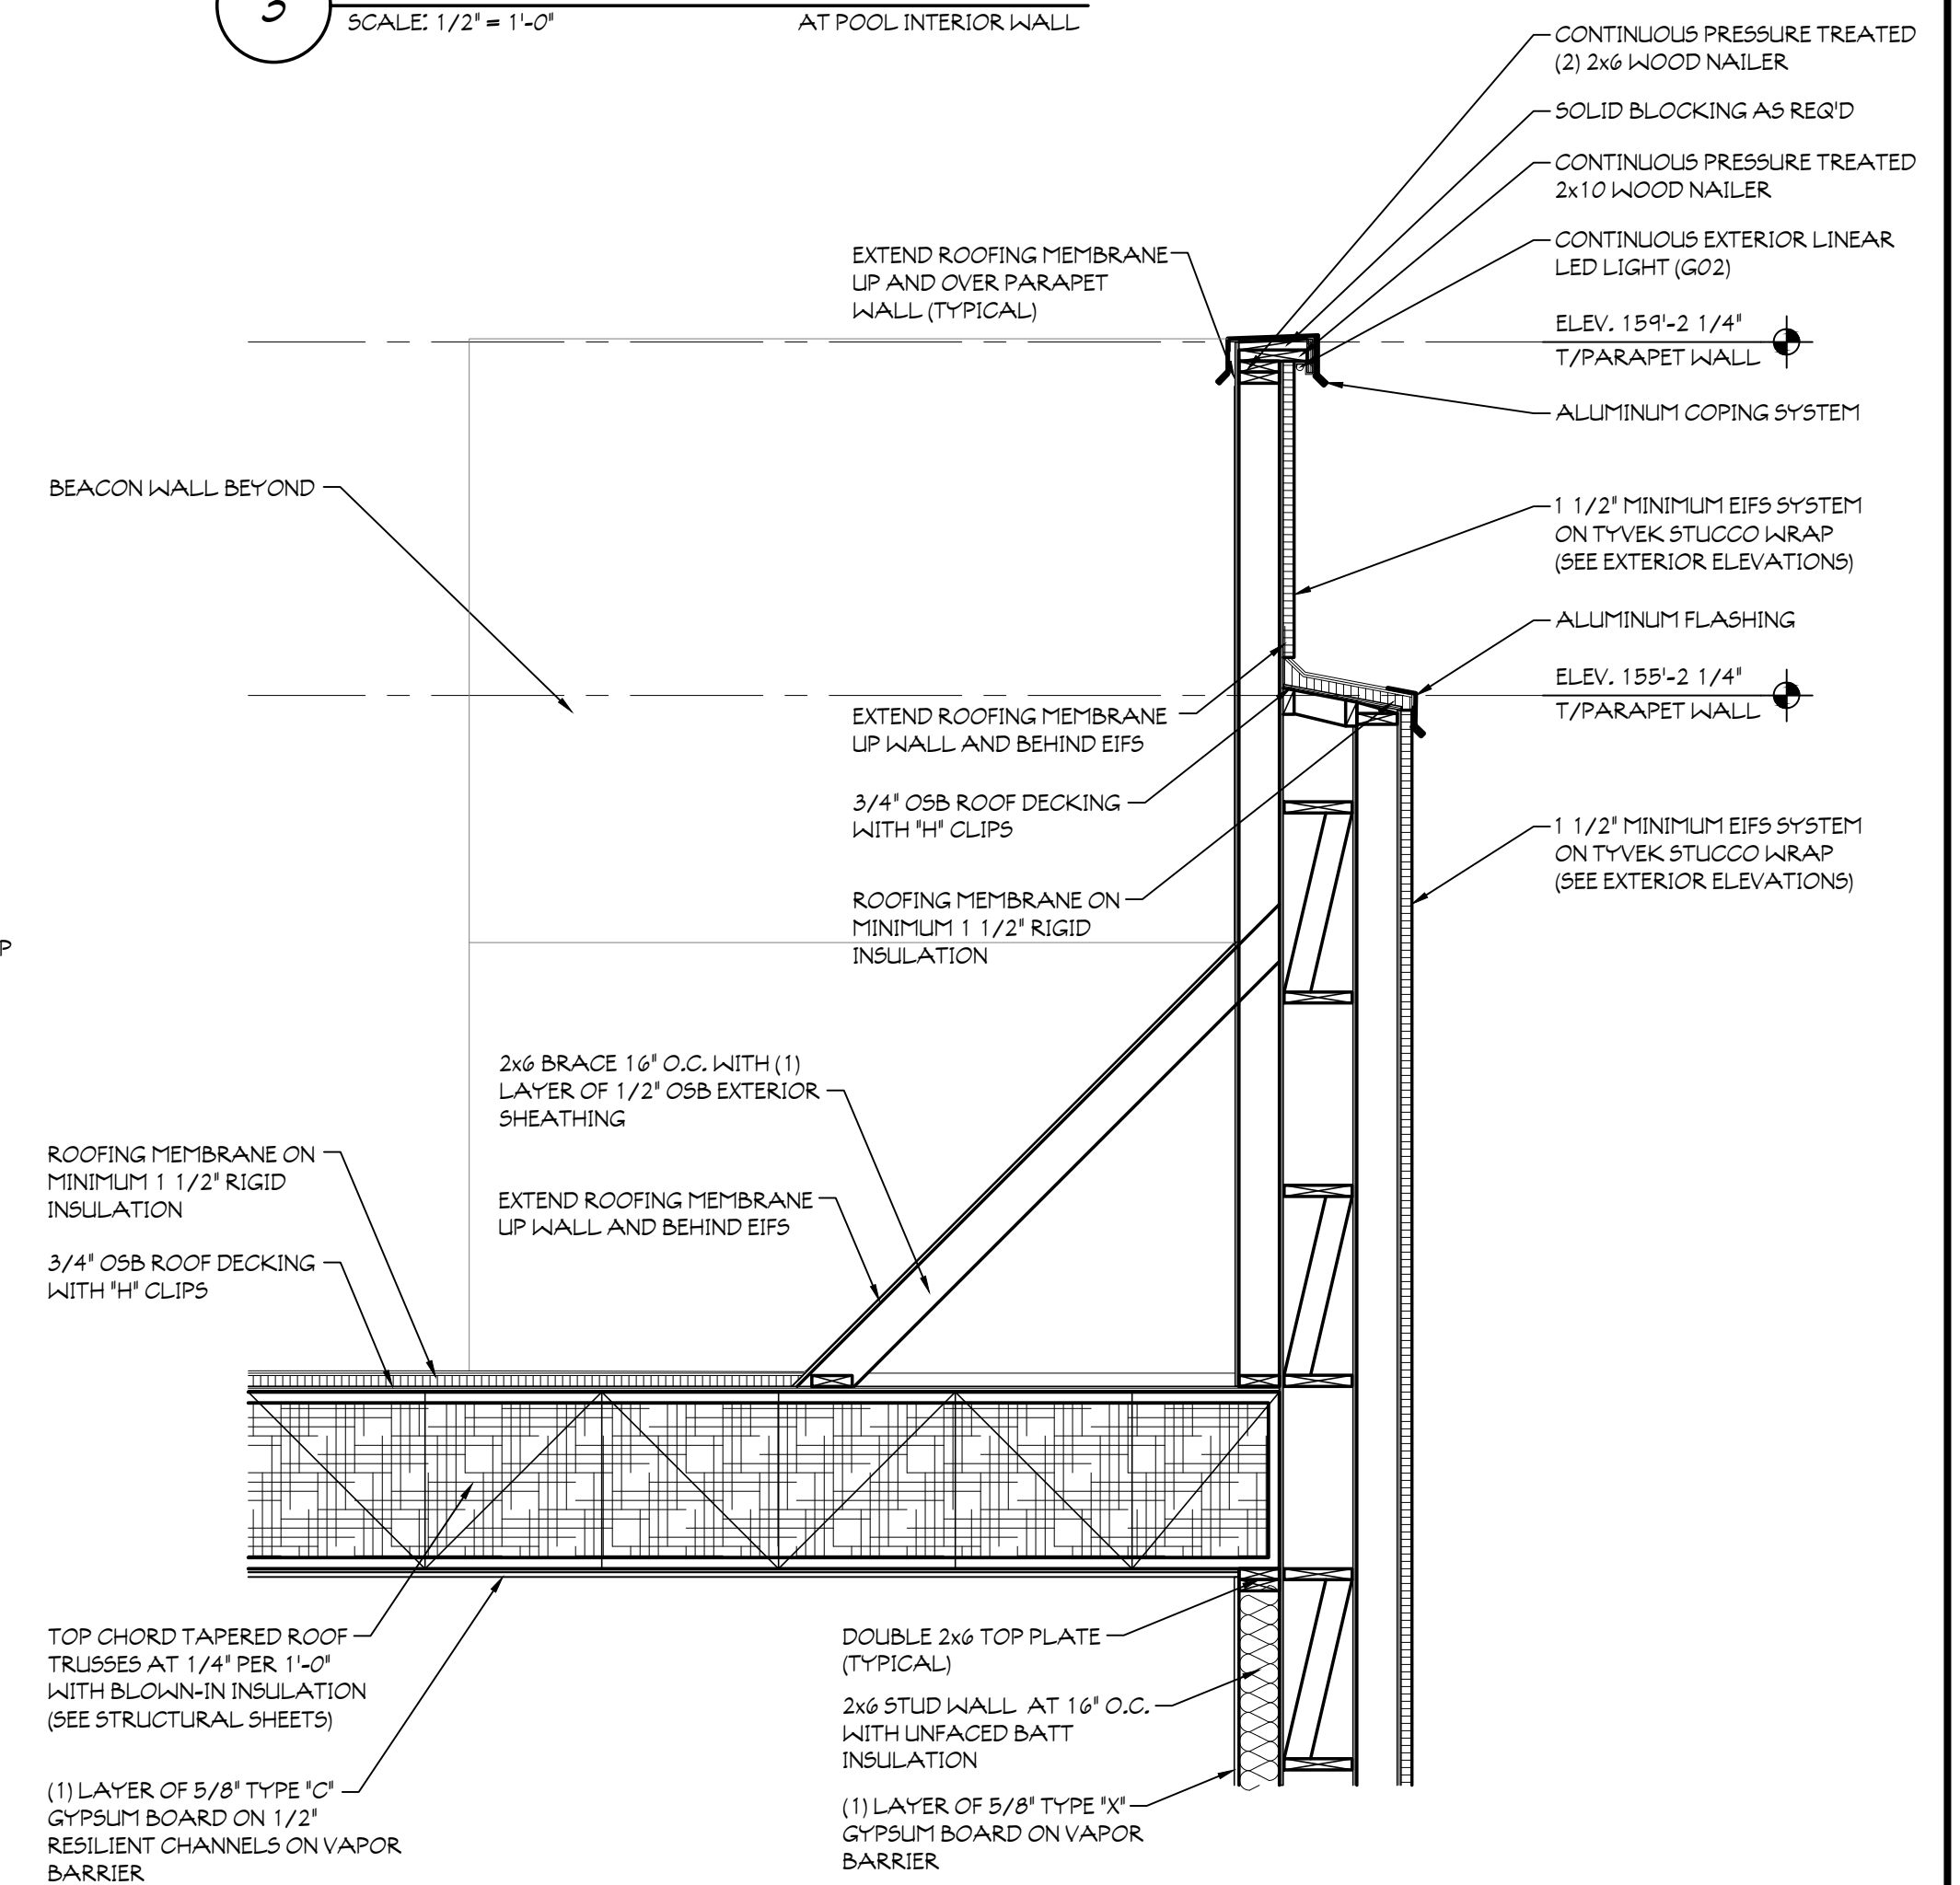

5 BEACON SECTION
SCALE: 1/2" = 1'-0"

GENERAL NOTES

ALTHOUGH DRAWINGS ARE PREPARED TO SCALE, THE ACCURACY OF THE DRAWINGS CANNOT BE GUARANTEED. THE CONTRACTOR SHALL BE RESPONSIBLE FOR VERIFYING ALL DIMENSIONS AND CONDITIONS PRIOR TO CONSTRUCTION. DIMENSIONS SHALL BE DELETED FROM DIMENSIONED PLANS.

ALL DIMENSIONS UNLESS OTHERWISE NOTED SHALL BE IN FEET AND INCHES. FRACTIONS SHALL NOT BE USED. DIMENSIONS SHALL BE ROUNDED UP OR DOWN TO THE NEAREST 1/8" OR 1/4" AS APPROPRIATE. THE CONTRACTOR SHALL BE RESPONSIBLE FOR VERIFYING ALL DIMENSIONS AND CONDITIONS PRIOR TO CONSTRUCTION.

Architects
Planners
Construction Mgmt.
Rule 5 and MS4 Filing
L.E.M., INC.
112 NORTH MAIN STREET
GOSHEN, INDIANA 46526
PHONE: (574) 537-8500
FAX: (574) 537-0808

These drawings are the property of L.E.M. Architectural Services and may not be reprinted, copied, altered or used in any manner without the written consent of L.E.M. Architectural Services.

HOME 2
SUITES BY HILTON

SHEET SIZE 24x36

FT. WAYNE, INDIANA

REVISIONS:

PRELIMINARY - NOT FOR CONSTRUCTION

DATE: 05/01/26

JOB NO.: MAS-26-105

NAME: MISCELLANEOUS SECTIONS AND DETAILS

SHEET:

A406