


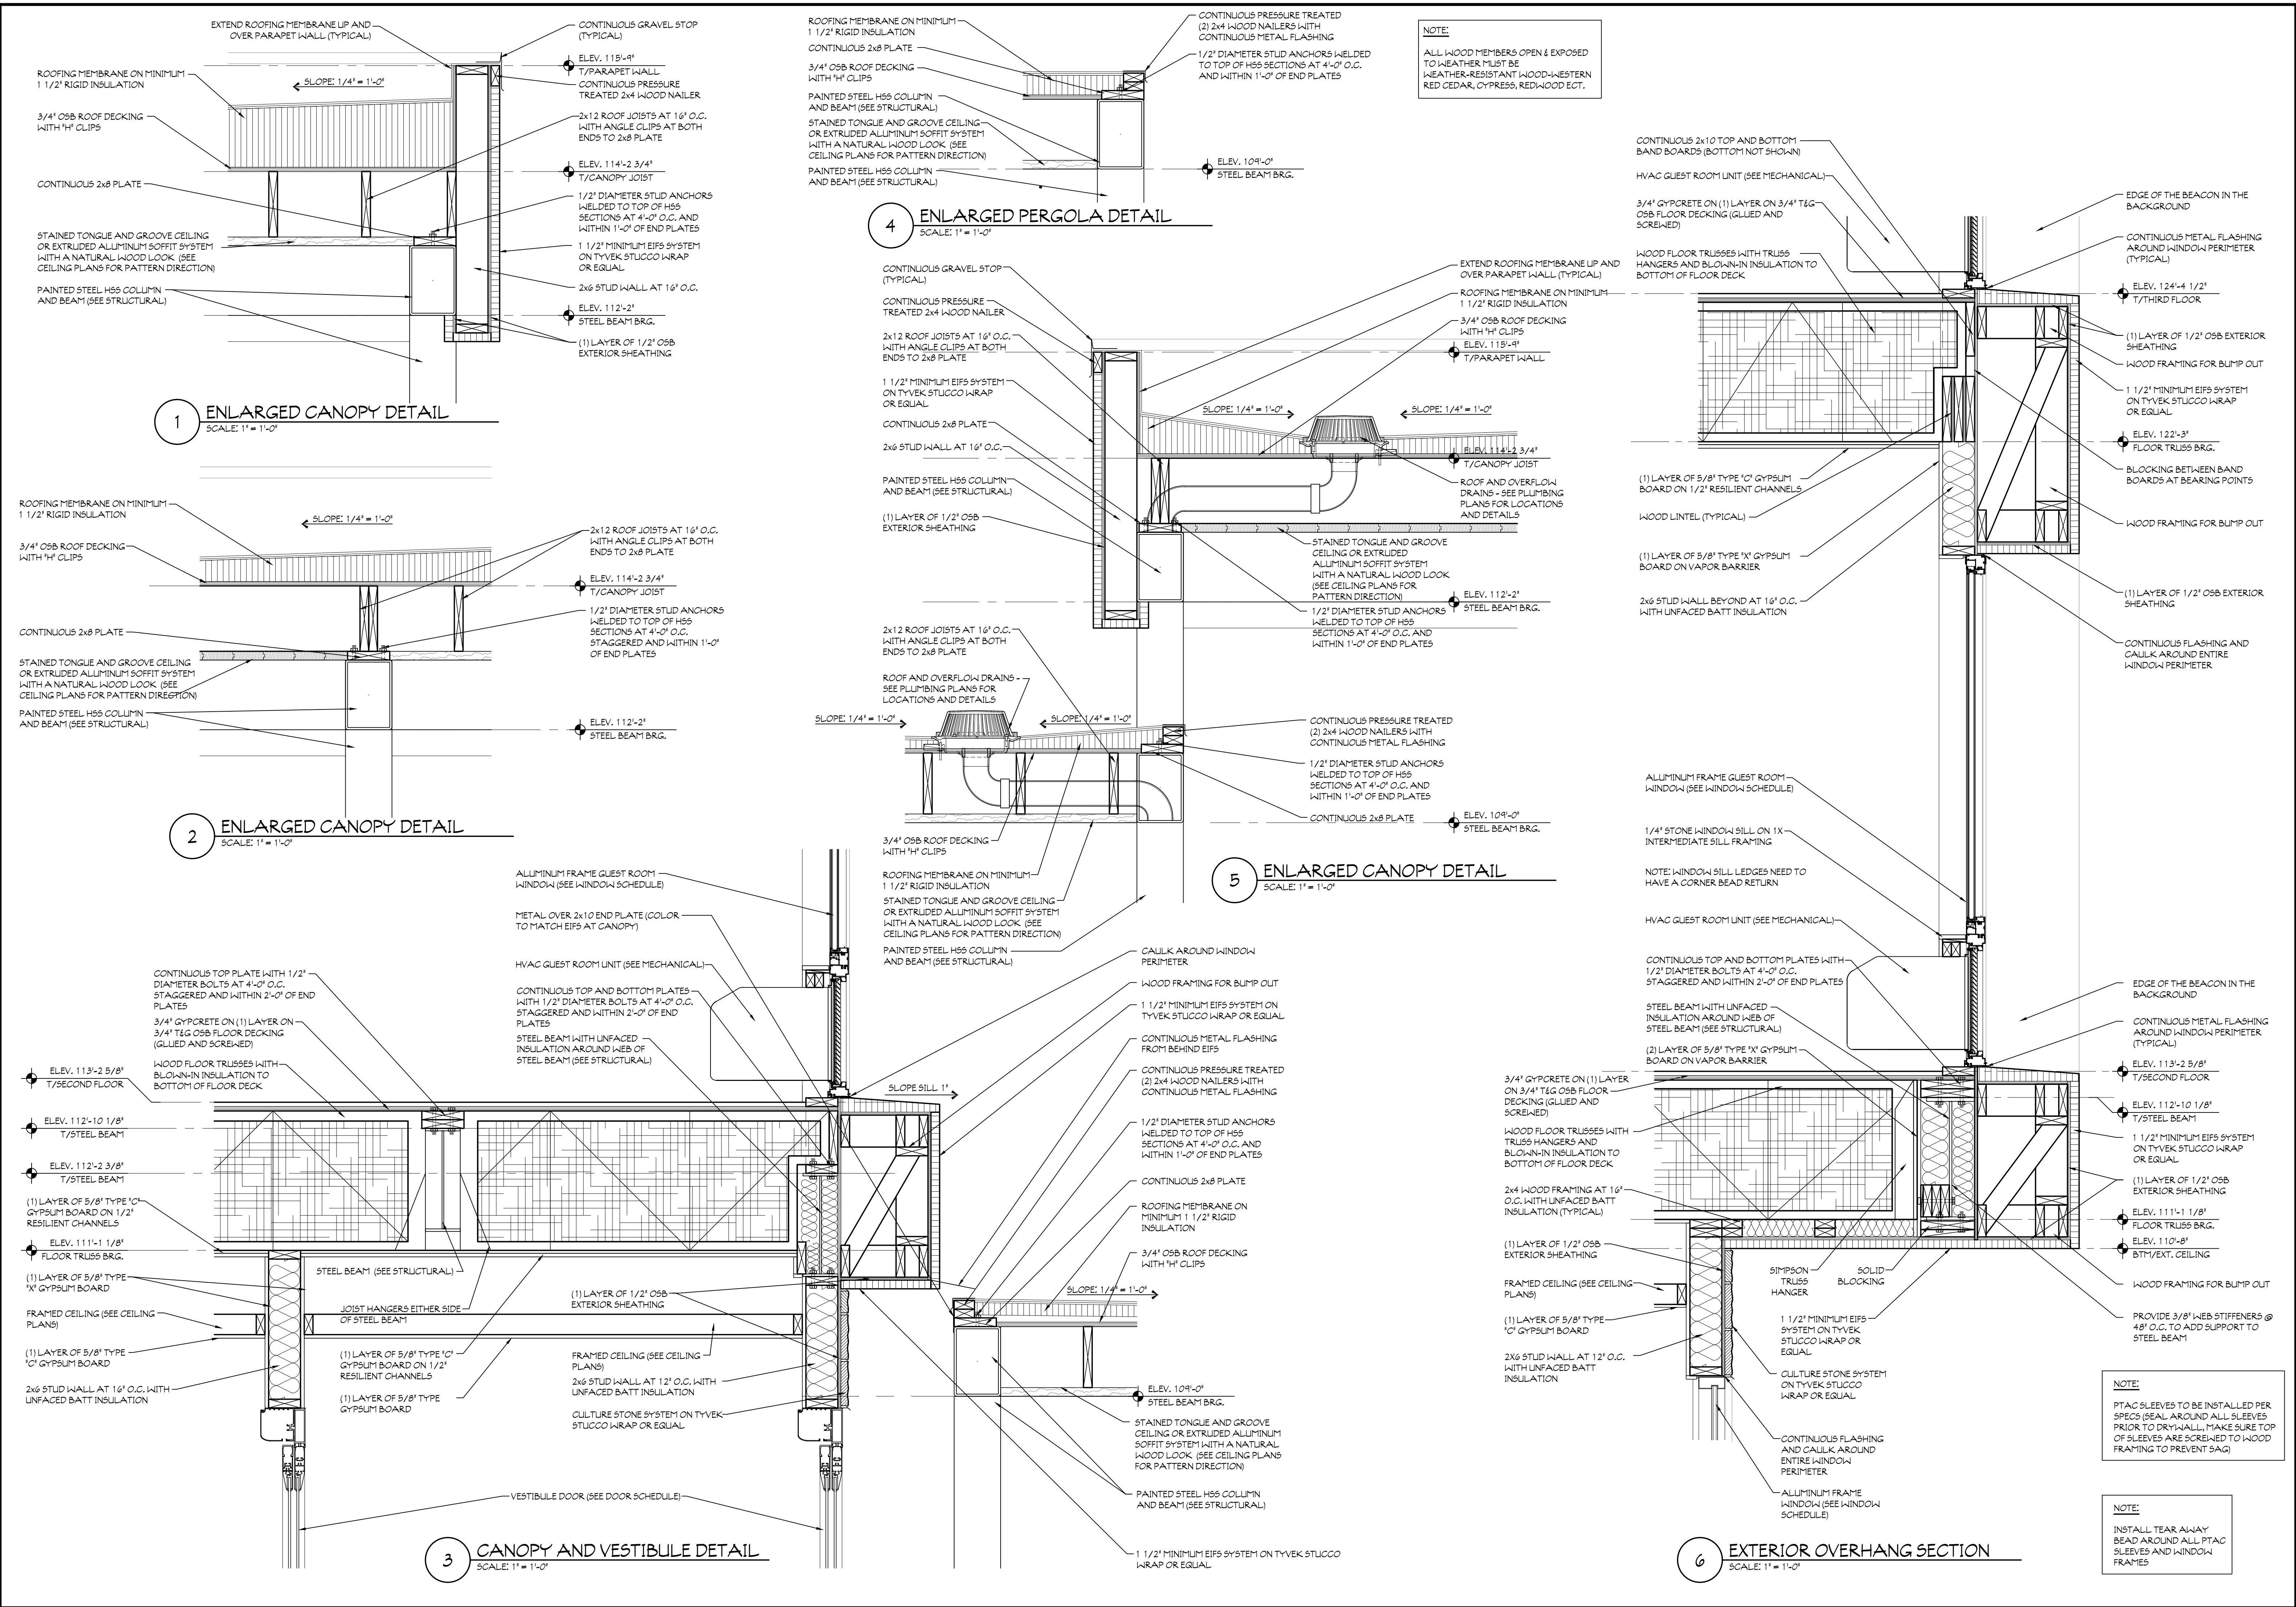

GENERAL NOTES

ALTHOUGH DRAWINGS ARE PREPARED TO SCALE, THE ACCURACY OF THE DRAWINGS CANNOT BE GUARANTEED. DIMENSIONS SHOWN ON THE DRAWINGS SHALL BE USED FOR CONSTRUCTION. DIMENSIONS SHALL BE USED FOR CONSTRUCTION. DIMENSIONS SHALL BE USED FOR CONSTRUCTION.

Architects

Planners

Engineers

Construction Mgmt.

MAUIST ARCHITECTURAL SERVICES, L.L.C.

112 NORTH MAIN STREET

GOSHEN, INDIANA 46526

PHONE: (574) 537-8500

FAX: (574) 537-0808

FT. WAYNE, INDIANA

REVISIONS:

DATE: 05/01/26

JOB NO.: MAS-26-105

NAME: CANOPY AND PERGOLA SECTIONS

SHEET:

A408

PRELIMINARY - NOT FOR CONSTRUCTION