


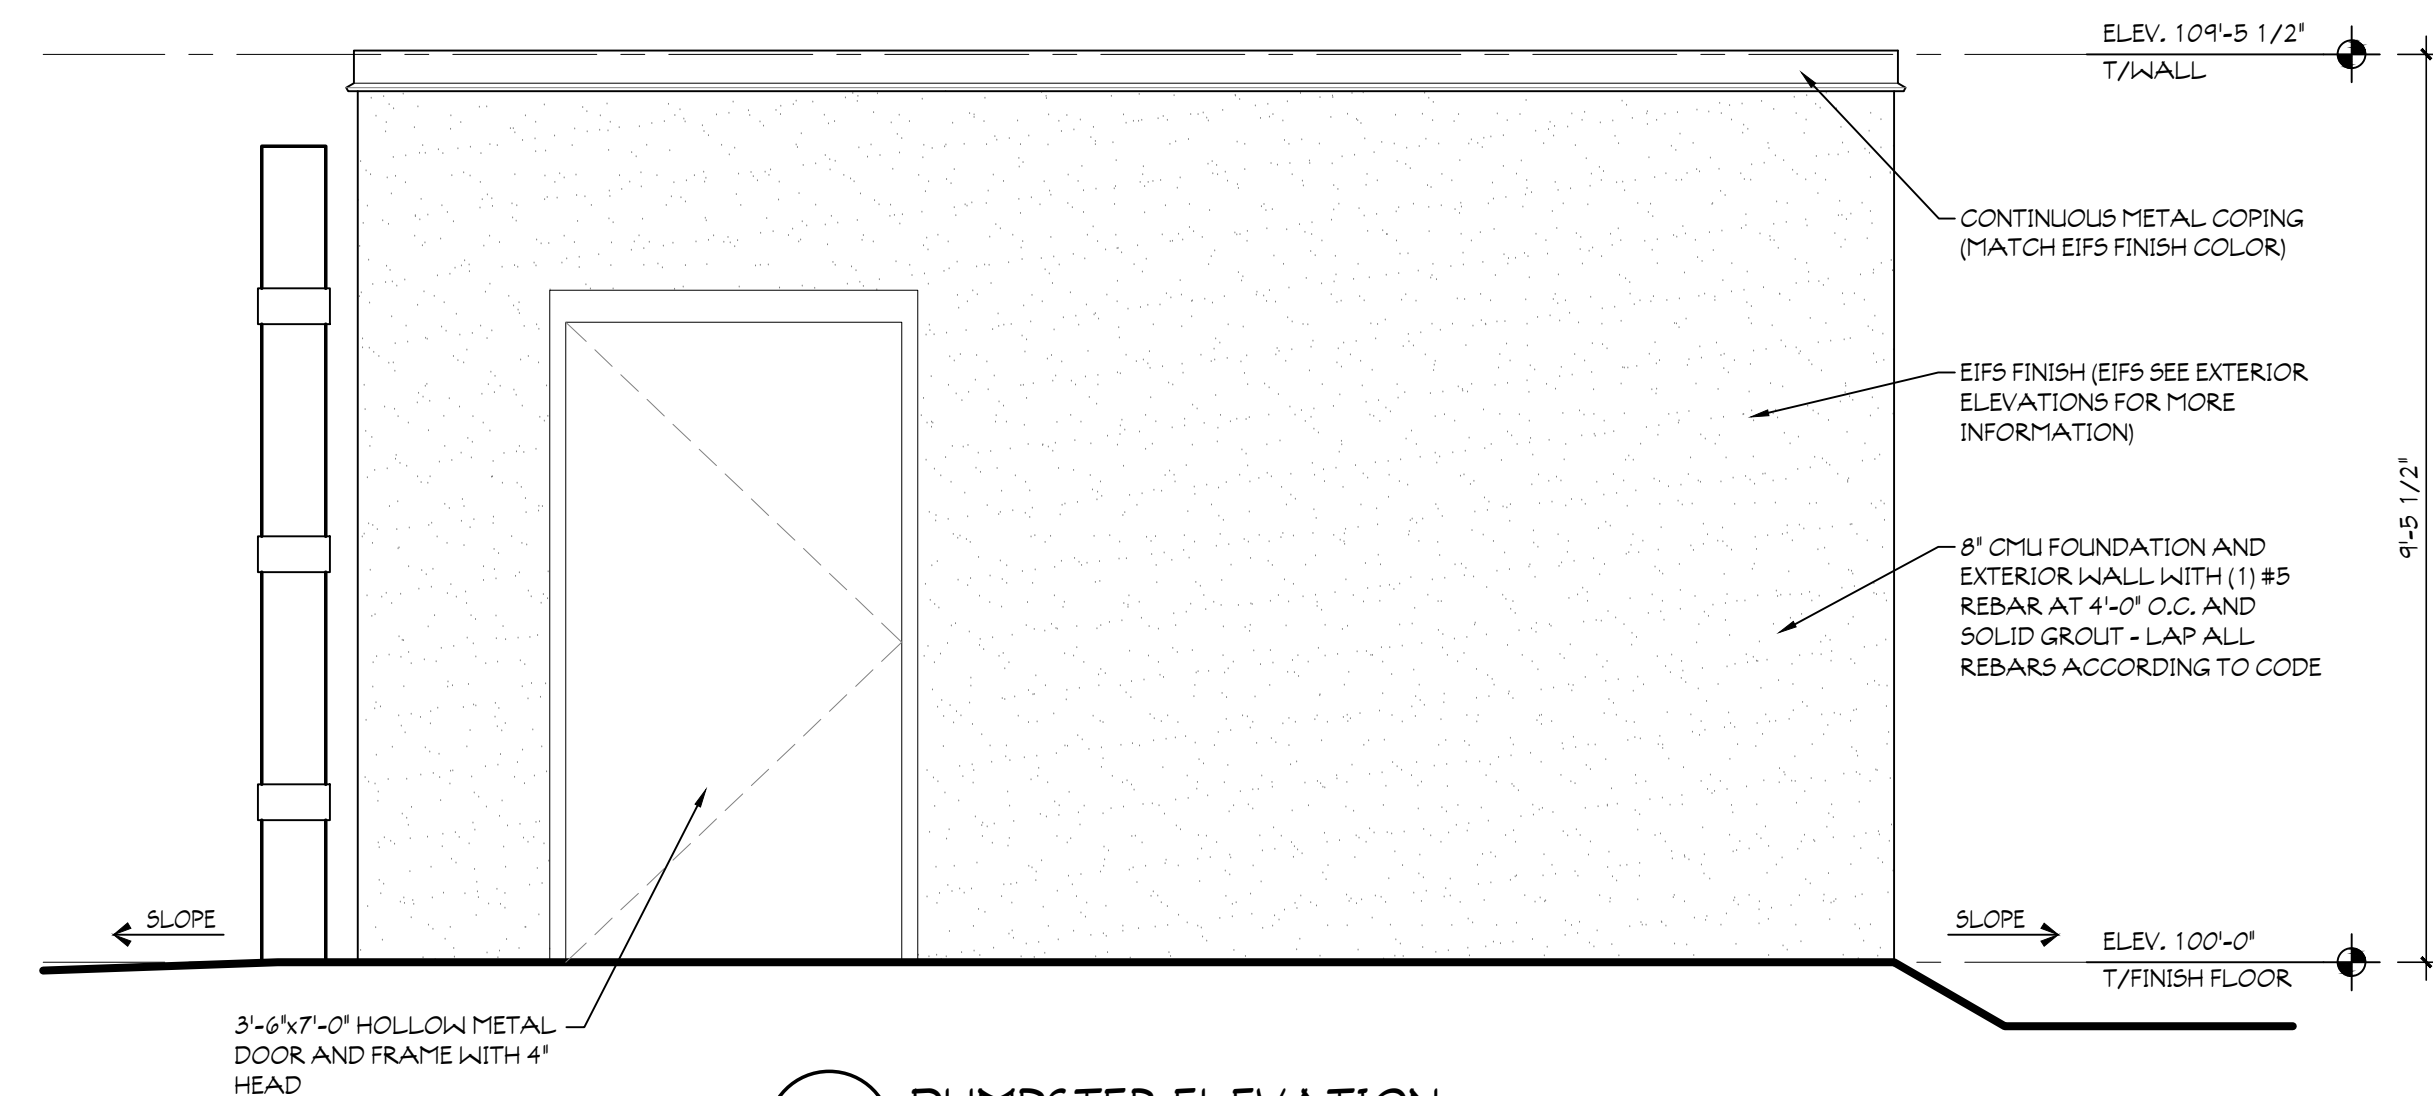

2 DUMPSTER ELEVATION
SCALE: 1/2" = 1'-0" TYPICAL SIDE ELEVATION

SHEET.

A409