


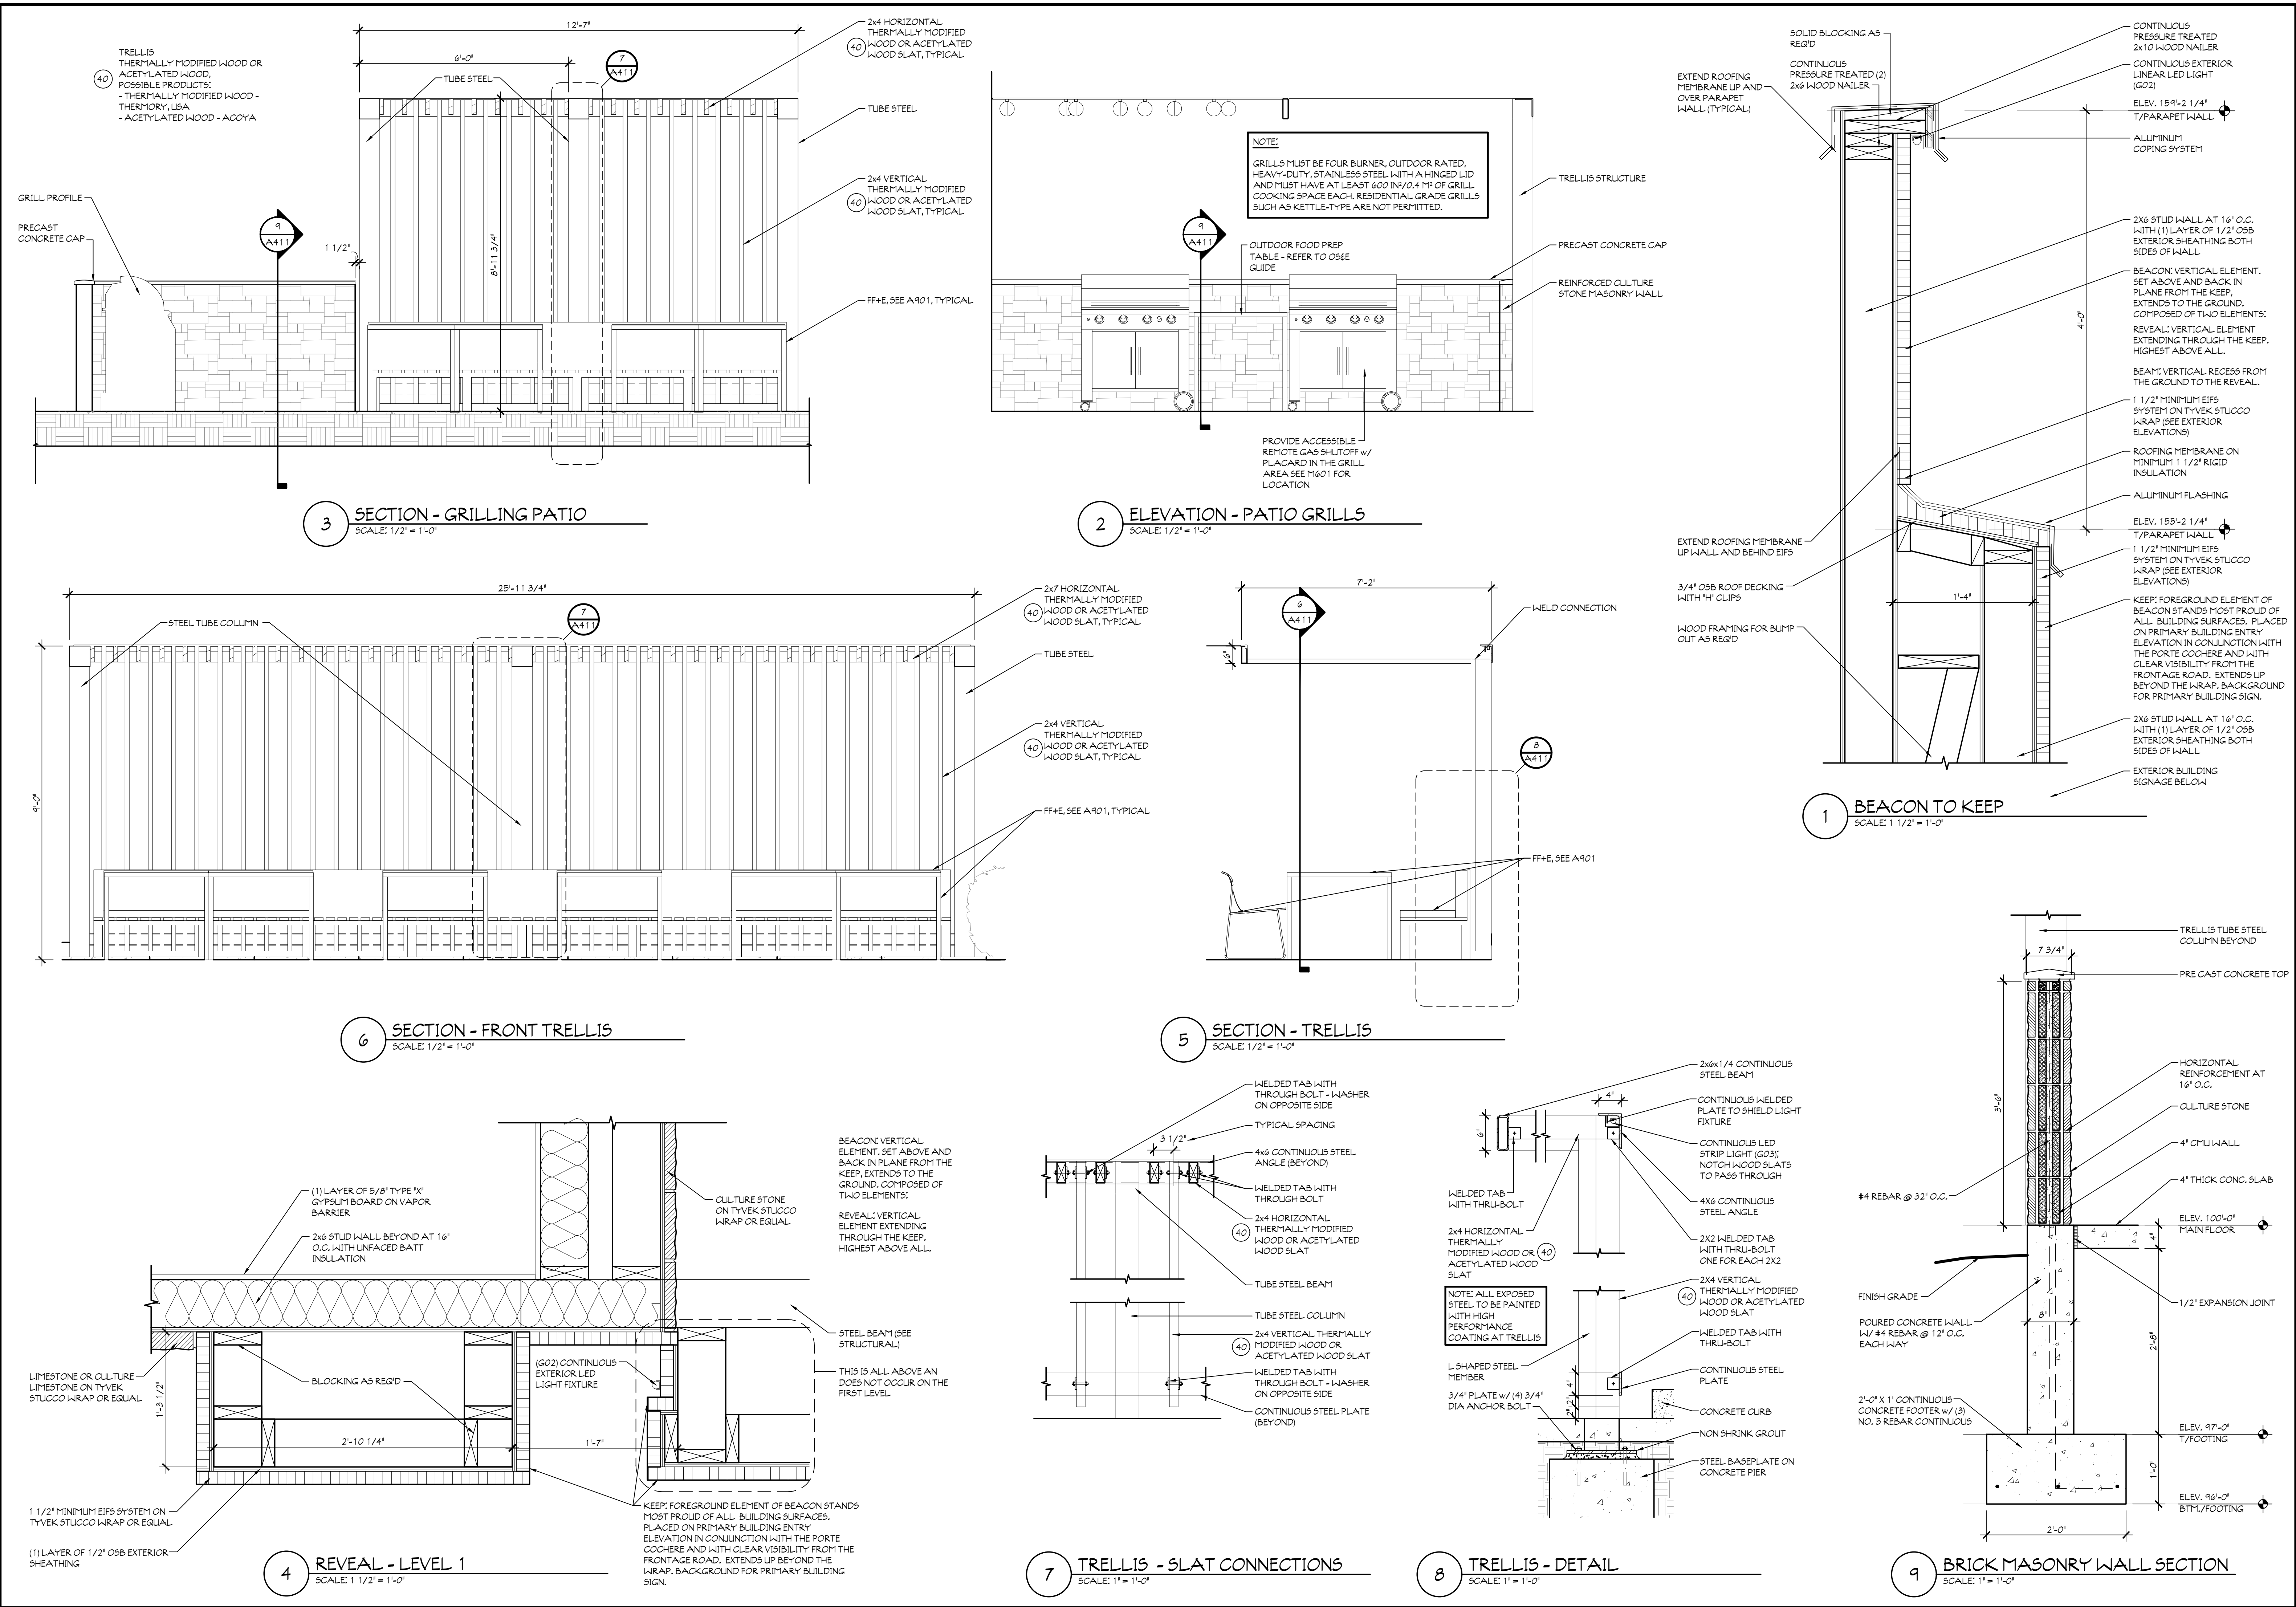

GENERAL NOTES

ALTHOUGH DRAWINGS ARE PREPARED TO SCALE, THE ACCURACY OF THE DRAWINGS CANNOT BE GUARANTEED. THE CONTRACTOR SHALL BE RESPONSIBLE FOR OBTAINING ALL NECESSARY PERMITS AND FOR VERIFYING THE EXISTING CONDITIONS PRIOR TO CONSTRUCTION. DIMENSIONS SHOWN SHALL BE DEEMED TO BE THE MOST ACCURATE.

Architects

Planners

Construction Mgmt.

MAUIST ARCHITECTURAL SERVICES, INC.

Division of L.E.M., INC.

112 NORTH MAIN STREET

GOSHEN, INDIANA 46526

PHONE: (574) 537-8500

FAX: (574) 537-0808

These drawings are the property of Maui Architectural Services, Inc. and may not be reprinted, copied, or otherwise used without the written consent of Maui Architectural Services, Inc.

HOME 2

SUITES BY HILTON

SHEET SIZE 24x36

FT. WAYNE, INDIANA

REVISIONS:

DATE: 05/01/26

JOB NO.: MAS-26-105

NAME: EXTERIOR DETAILS & TRELLIS

SHEET:

PRELIMINARY - NOT FOR CONSTRUCTION

A411