



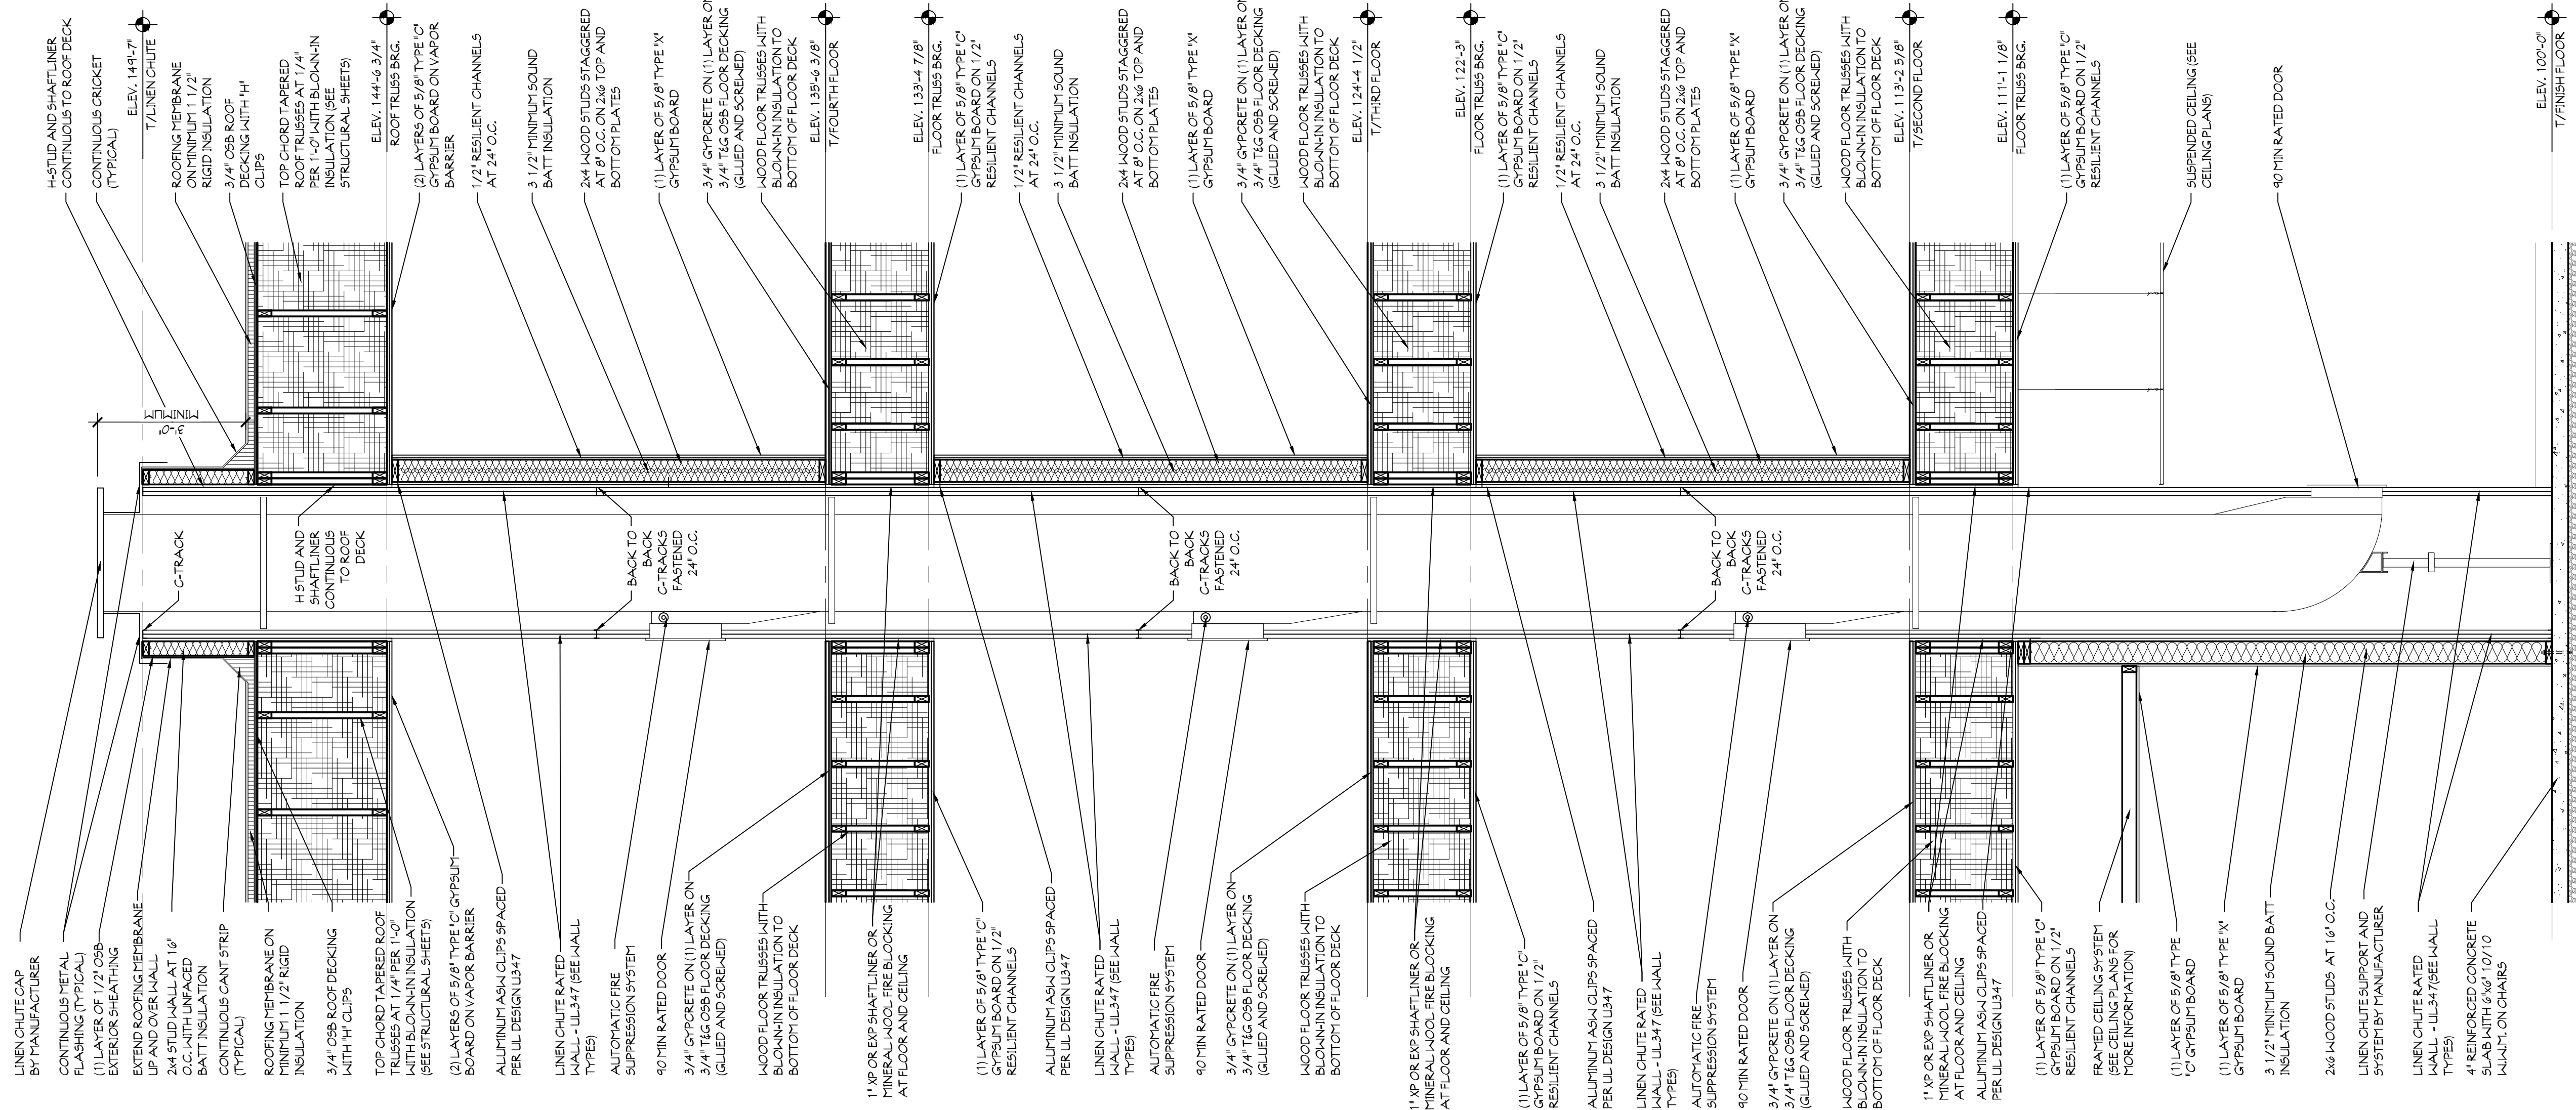


1 LINEN CHUTE SECTION
SCALE: 1/2" = 1'-0"


NOTE:
ELECTRICAL INTERLOCKING
FOR LINEN CHUTE
REQUIRED

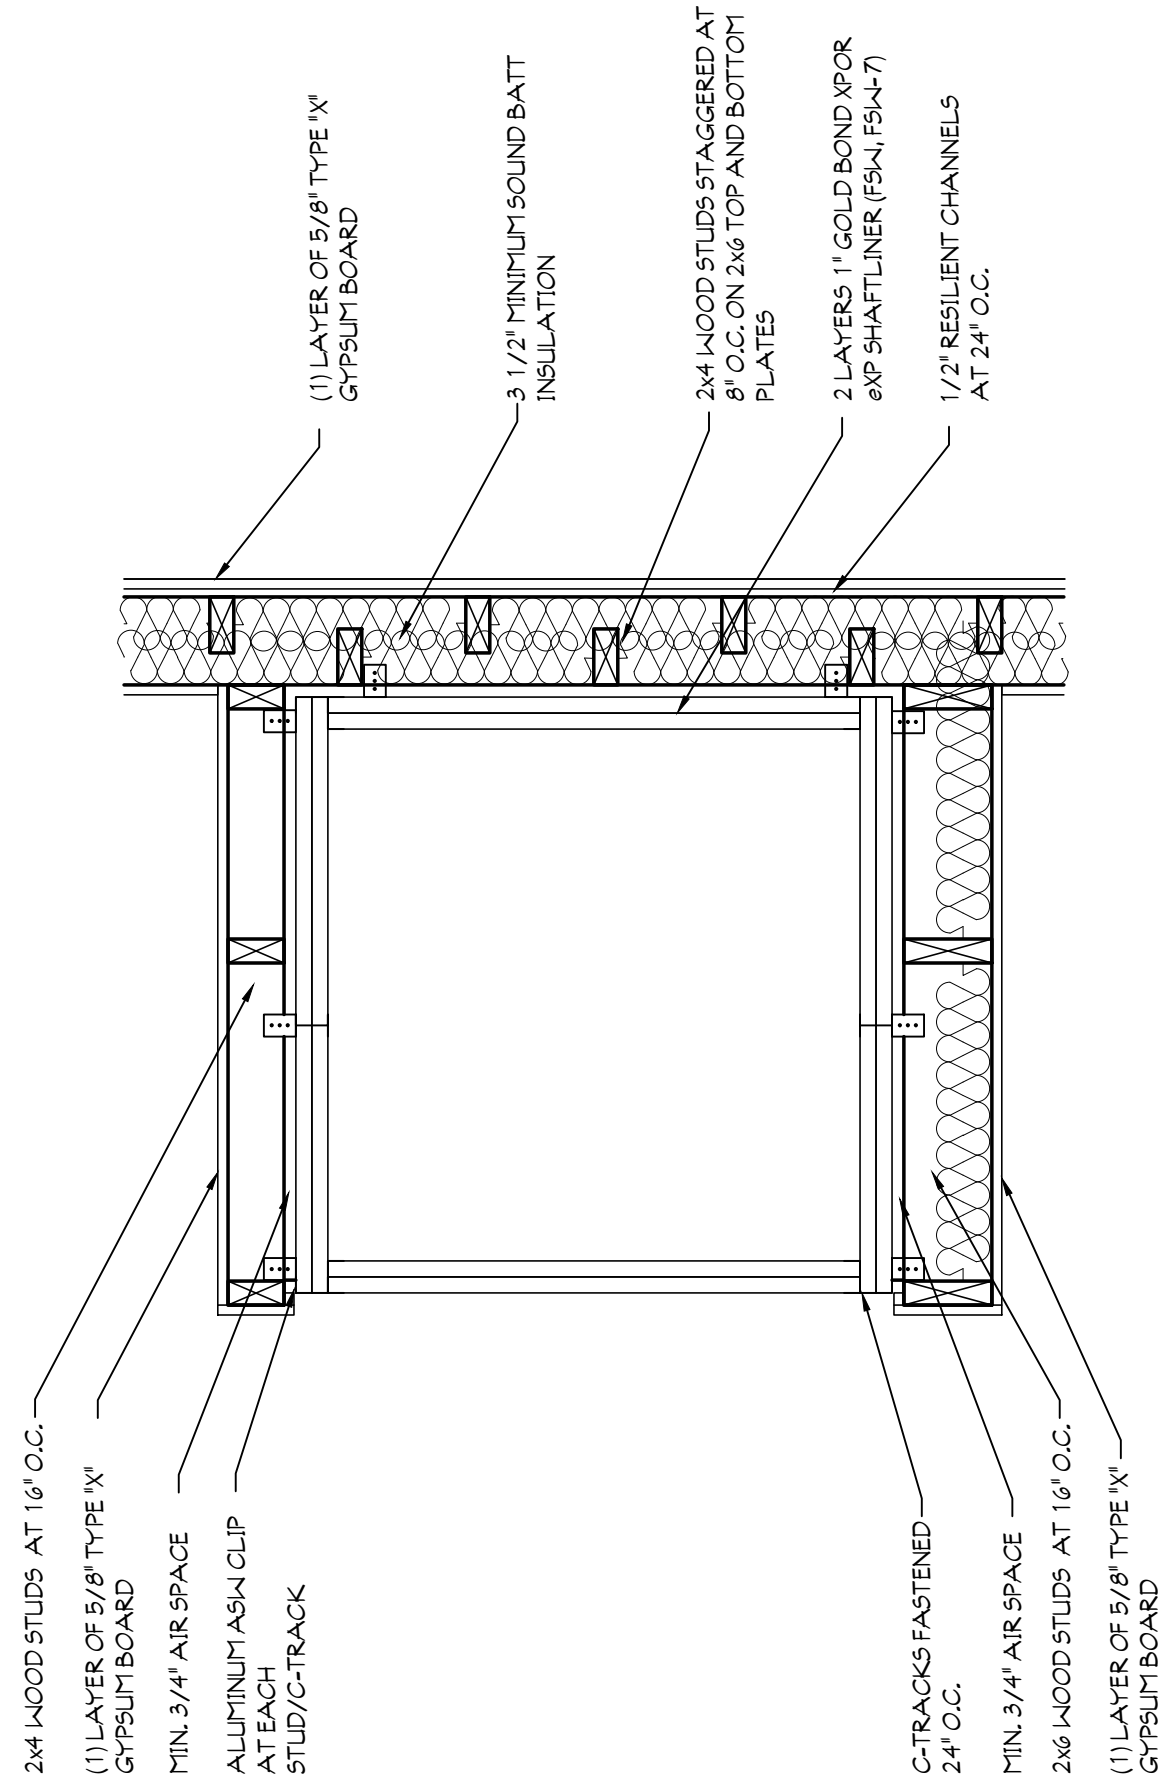


5 4TH FLOOR LINEN CHUTE PLAN
SCALE: 1" = 1'-0"

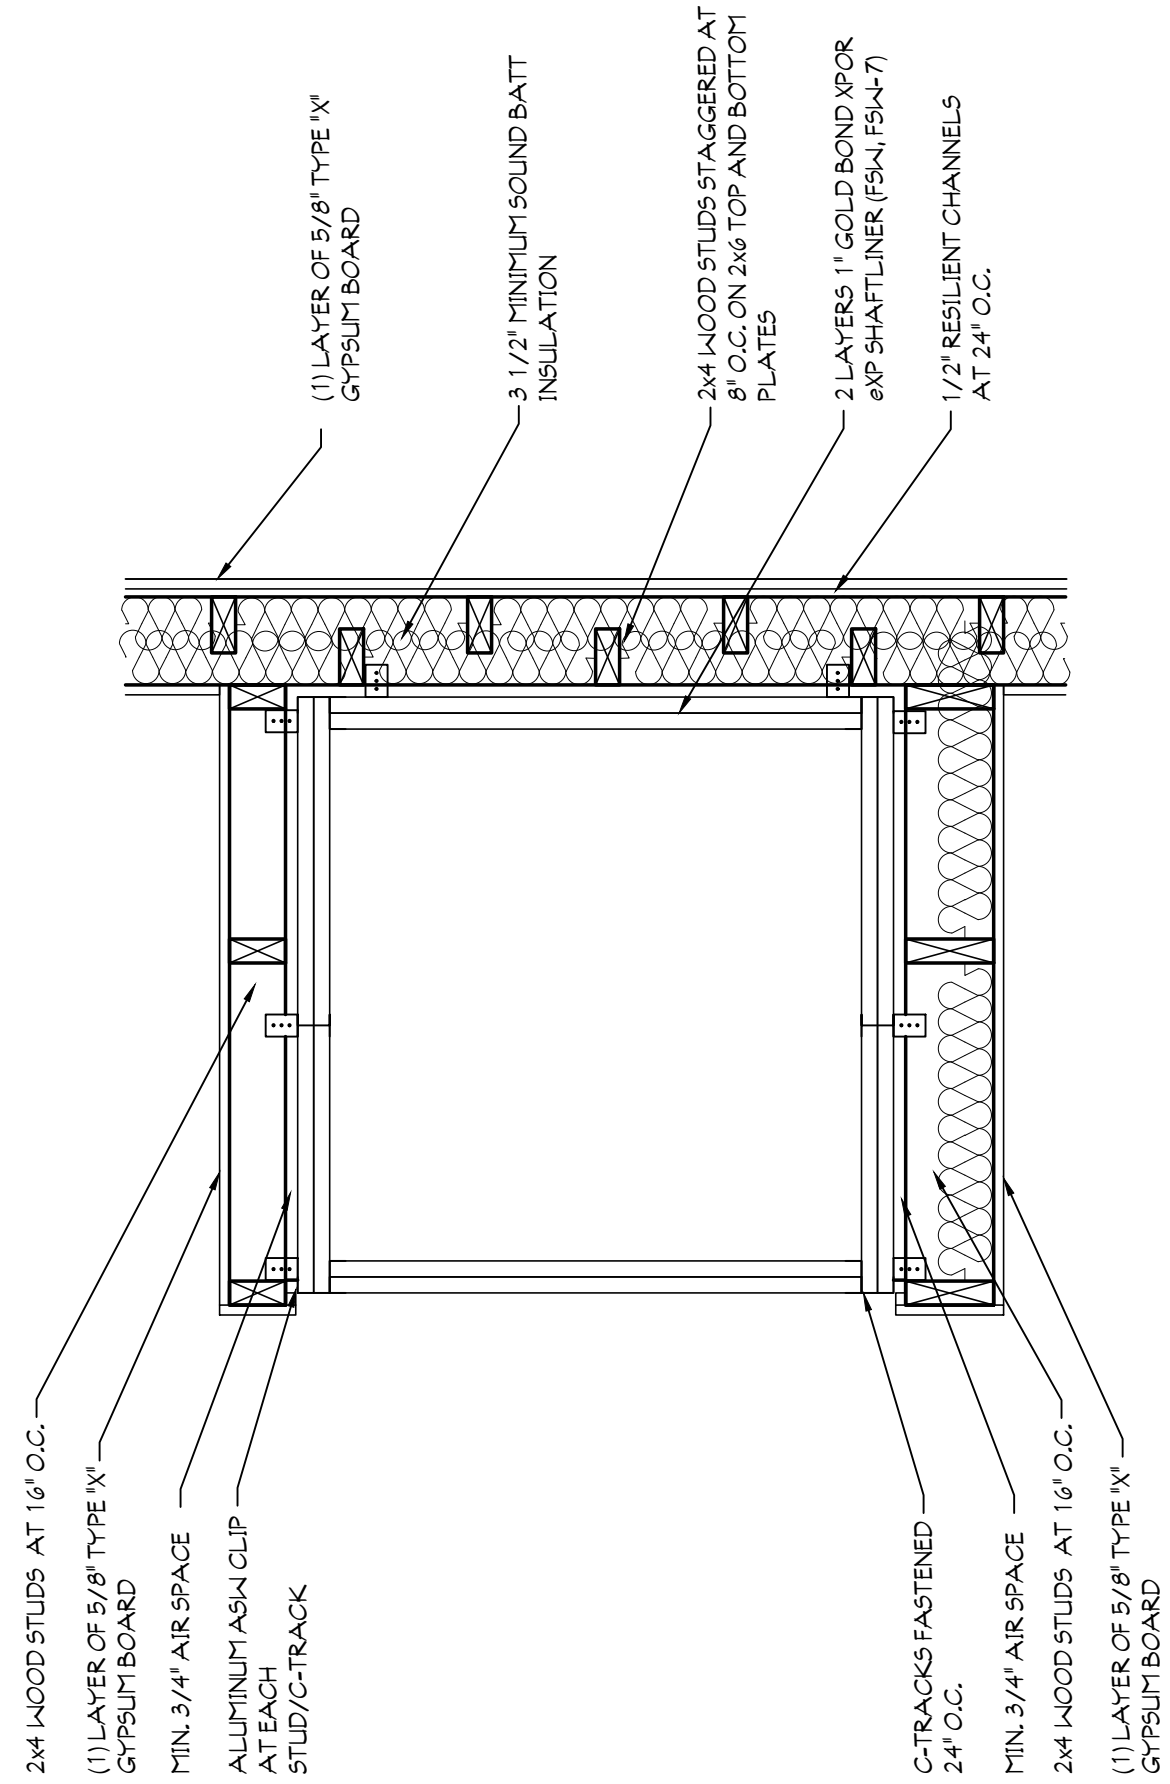

4 3RD FLOOR LINEN CHUTE PLAN
SCALE: 1" = 1'-0"

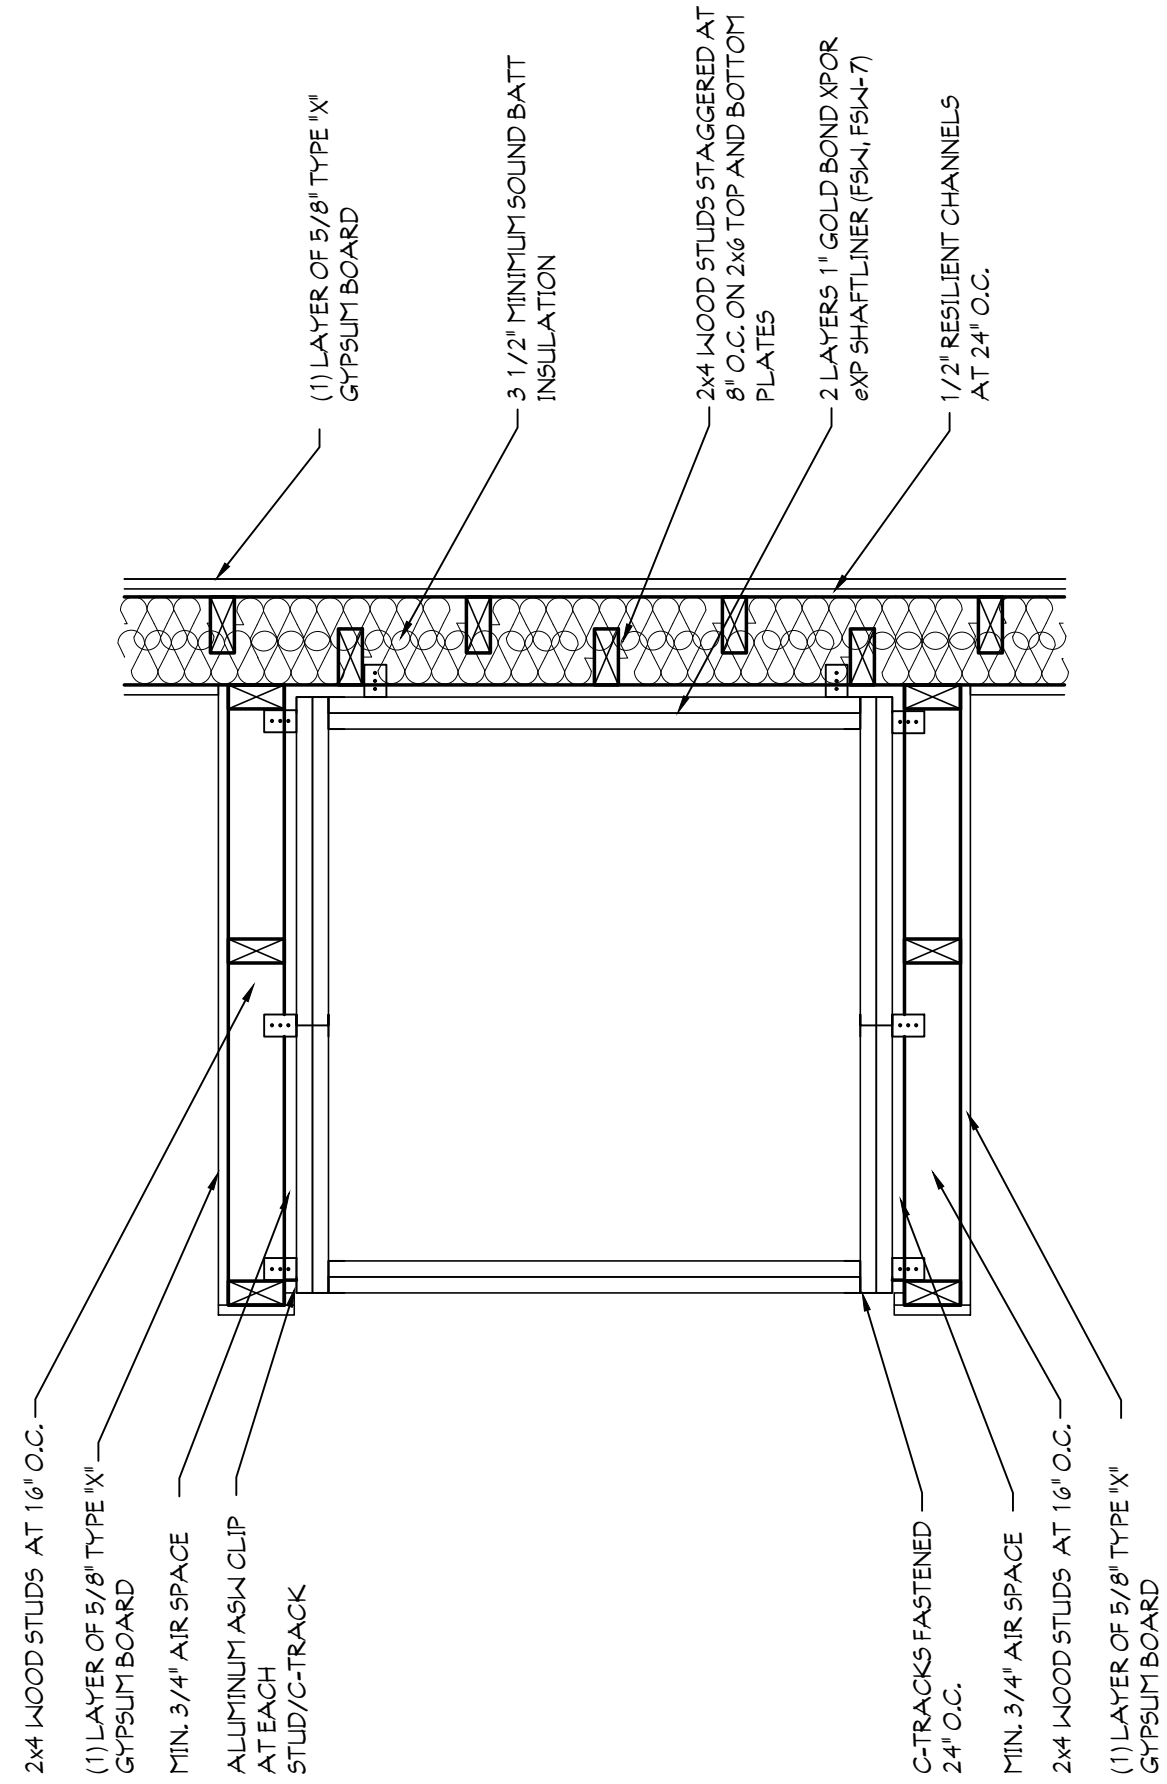

3 2ND FLOOR LINEN CHUTE PLAN
SCALE: 1" = 1'-0"

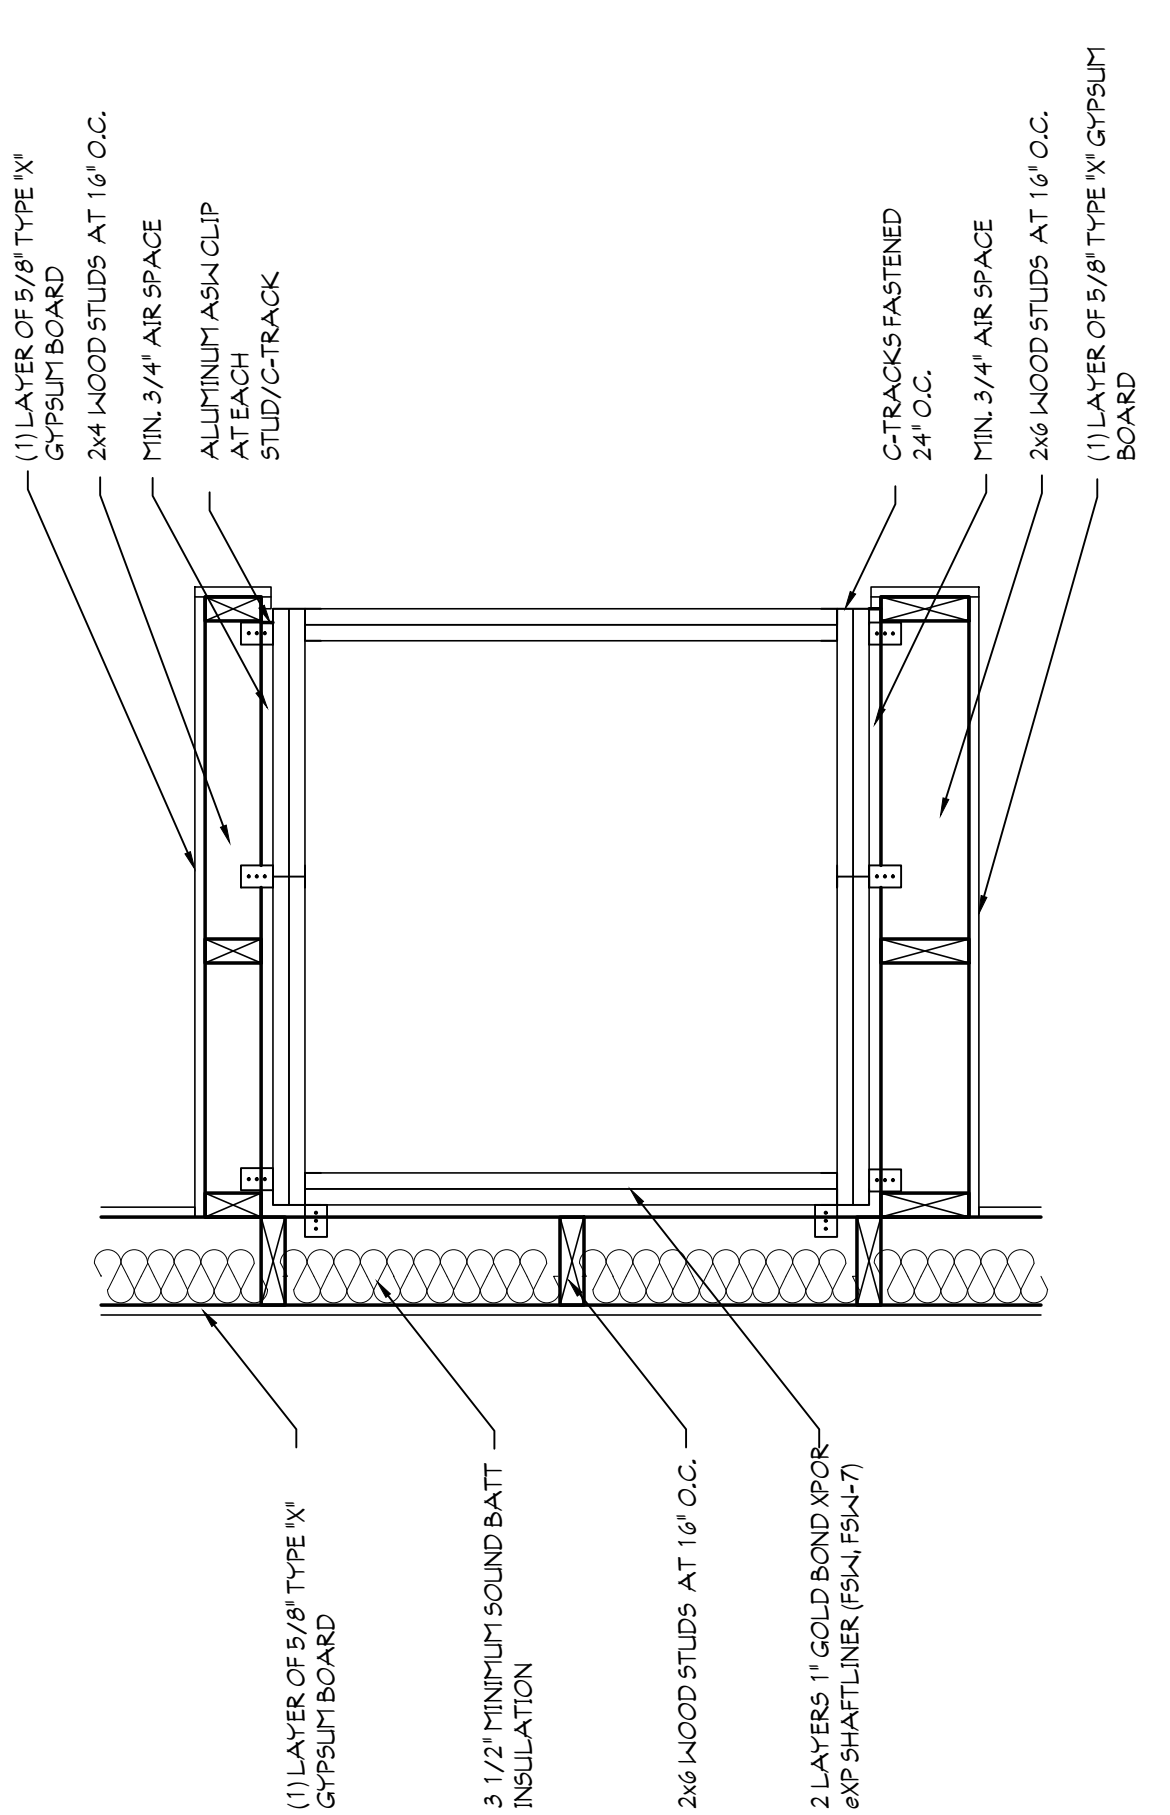

2 1ST FLOOR LINEN CHUTE PLAN
SCALE: 1" = 1'-0"