
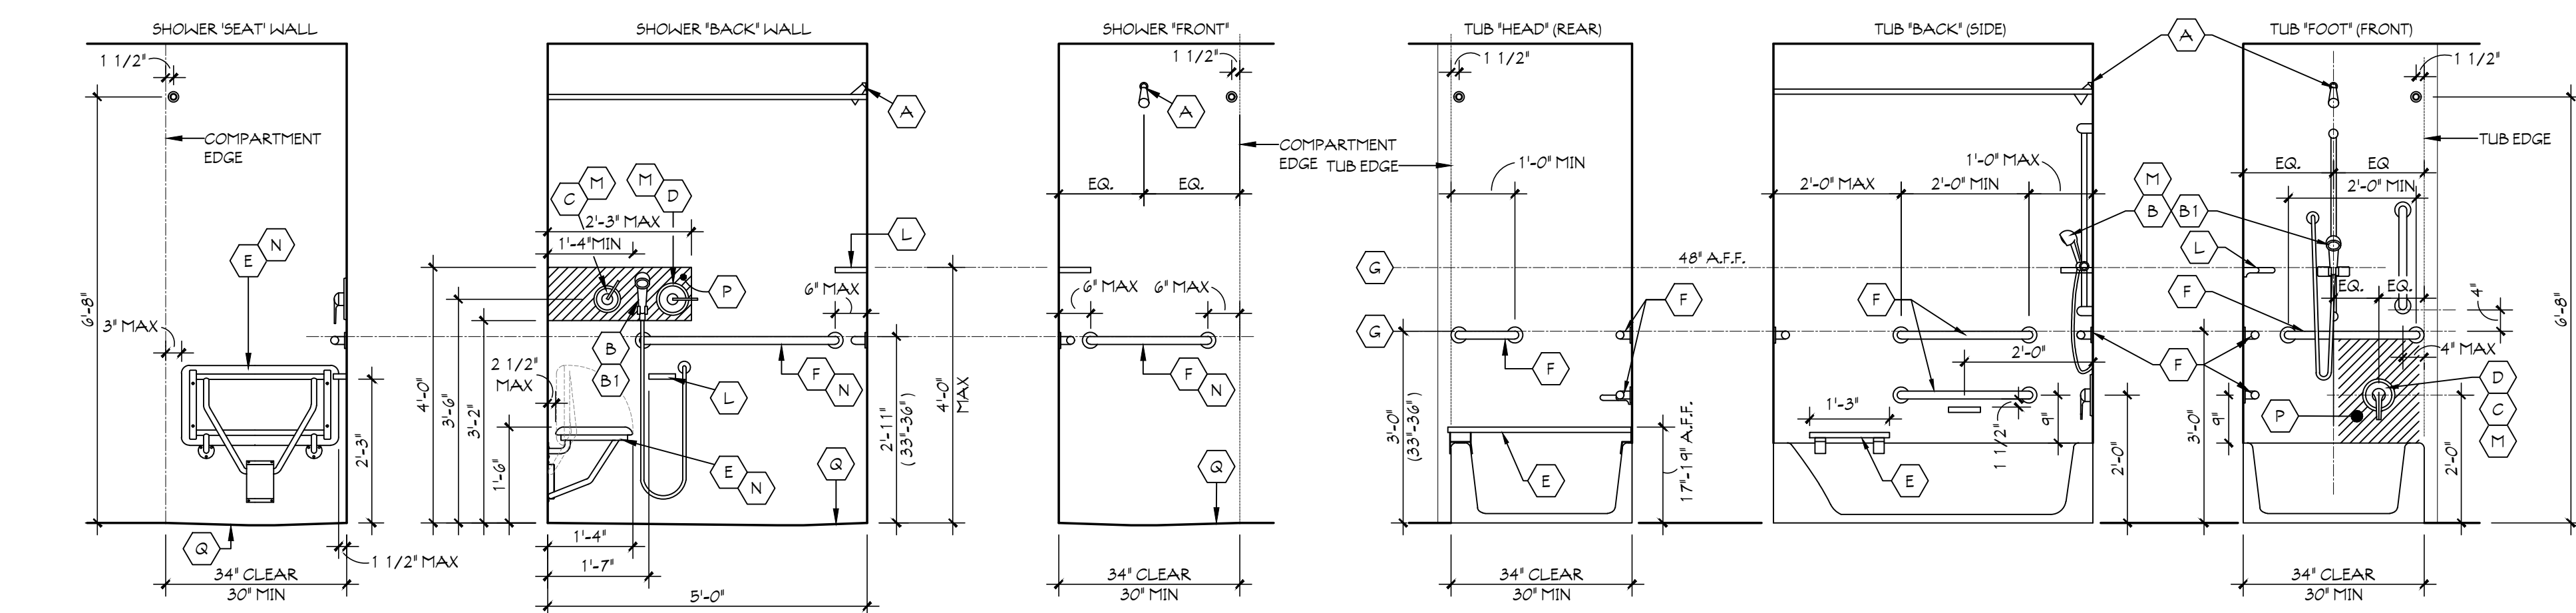
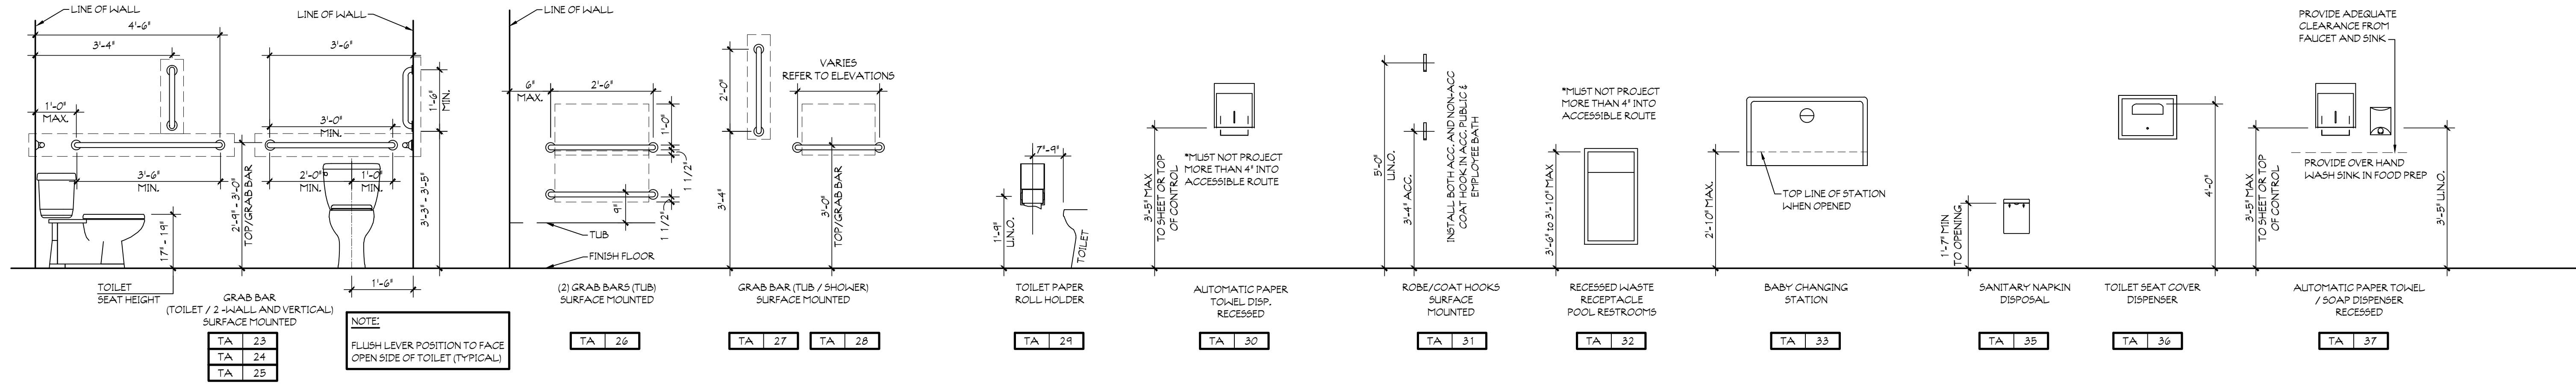


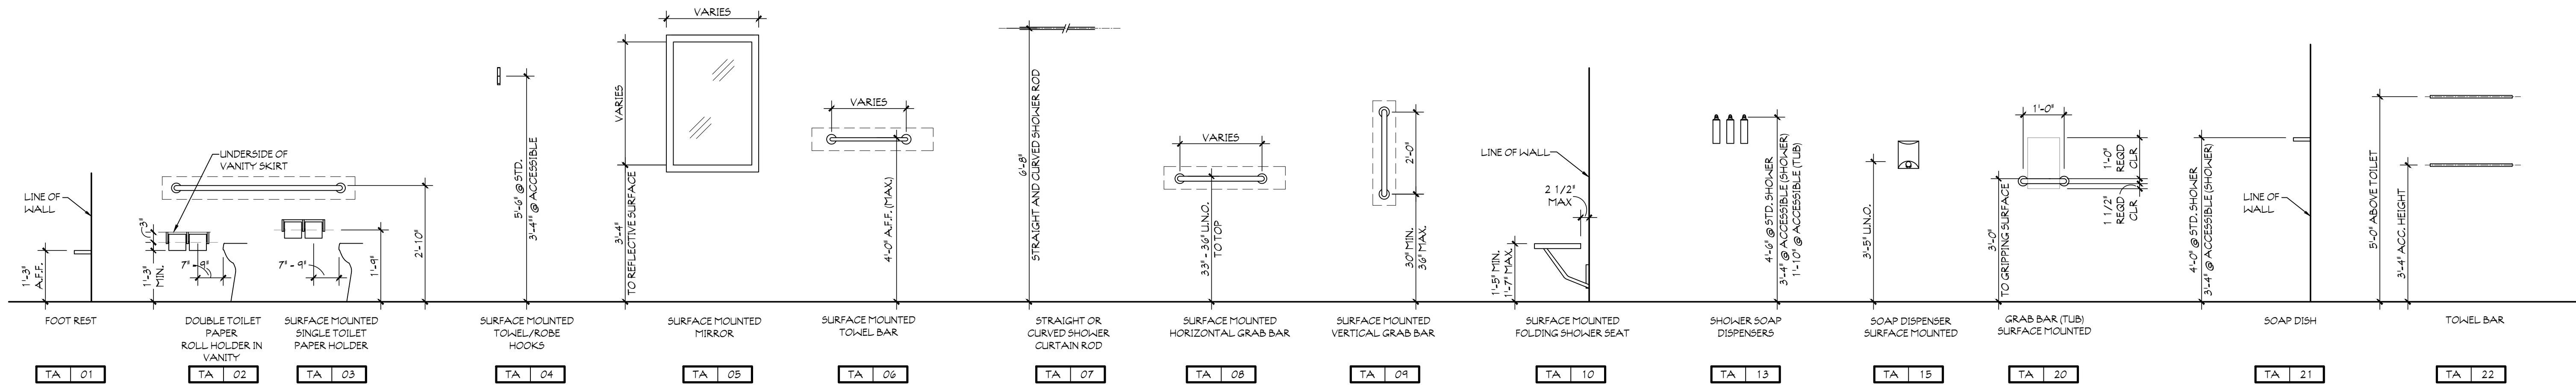

- NOTES:**
1. PROVIDE BLOCKING, OR DIRECT STUD SUPPORT, FOR ALL TOILET ACCESSORIES WITH A MINIMUM OF 250 LB. VERTICAL AND HORIZONTAL FORCE.
 2. APPROVED METAL FINISHES: POLISHED OR BRUSHED CHROME, BRUSHED NICKEL, OR STAINLESS STEEL.
 3. WALL MOUNTED EQUIPMENT, FIXTURE, ETC. BETWEEN 27" AND 80" A.F.F. SHALL NOT PROTRUDE FURTHER THAN 4" FROM WALL. PER ACCESSIBILITY STANDARDS. CONSULT THE HADG FOR FURTHER REQUIREMENTS.
 4. ALL CONTROLS FOR USE BY GUESTS MUST BE MOUNTED AT BETWEEN 15" A.F.F. AND 48" A.F.F. AND PROVIDE A 30"x48" CLEAR FLOOR AREA IN COMPLIANCE WITH ACCESSIBILITY STANDARDS. OPERABLE CONTROLS LOCATED OVER AN OBSTRUCTION DEEPER THAN 10" MUST BE MOUNTED NO HIGHER THAN 46" A.F.F. ACCESSIBLE CONTROLS MUST NOT REQUIRE TIGHT GRASPING, PINCHING OR TWISTING OF THE WRIST. ACCESSIBLE CONTROLS SHALL COMPLY WITH THE HADG.
 5. TYPICAL CLEAR AREA AROUND GRAB BARS TO BE: ABOVE - 1'-0", BELOW - 1 1/2" BETWEEN SHOWER CONTROLS, SHOWER FITTING, AND OTHER GRAB BARS A CLEAR DISTANCE OF 1 1/2" IS PERMITTED.
 6. ALL GRAB BARS MUST BE BLOCKED OR REINFORCED TO WITHSTAND ACCESSIBILITY REQUIREMENTS - REFER HADG.
 7. PROVIDE WOOD BLOCKING FOR ALL TOILET ACCESSORIES MOUNTED IN GYPSUM BOARD PARTITIONS - MAINTAIN INTEGRITY OF FIRE RATING WHERE ACCESSORIES ARE IN RATED WALLS.
 8. PROVIDE 12" CLEAR AREA ABOVE GRAB BARS (TYPICAL).
 9. PROVIDE 1 1/2" CLEAR AREA BETWEEN GRAB BARS AND ADJACENT ACCESSORIES.

ACCESSIBLE ITEM LEGEND	
A	HOTEL STANDARD SHOWER HEAD *
B	HAND HELD SHOWER HEAD WITH 60" HOSE ATTACHED TO ADJUSTABLE HEIGHT BAR. MOUNT BAR TO ALLOW SHOWER HEAD TO BE PLACED WITHIN ACCESSIBLE REACH RANGE. MOUNT ADJUSTABLE BAR SO AS NOT TO CONFLICT WITH GRAB BARS. PROVIDED POSITIVE SHUT OFF SWITCH. UNIT SHALL DELIVER WATER AT 120 DEGREE F. MAXIMUM. *
B1	THE ADJUSTABLE CONTROL ON THE BAR MUST COMPLY WITH THE STANDARDS FOR OPERABLE PARTS. OPERABLE PARTS SHALL BE OPERABLE WITH ONE HAND AND SHALL NOT REQUIRE TIGHT GRASPING, PINCHING, OR TWISTING OF THE WRIST. THE FORCE REQUIRED TO ACTIVATE OPERABLE PARTS SHALL BE (5) POUNDS MAXIMUM.
C	DIVERTER FAUCET WITH PERMANENT LABELS INDICATING OPERATION DIRECTION - WHEN FAUCET IS POINTING TOWARDS STANDARD SHOWER HEAD AS INDICATED IT OPERATES THE STANDARD SHOWER HEAD. WHEN POINTING TOWARD HAND HELD DEVICE AS INDICATED IT OPERATES HAND HELD DEVICE. LABELS SHALL READ: UPPER SHOWER HEAD AND HAND HELD SHOWER HEAD AND BE PERMANENTLY AFFIXED TO WALL.
D	CONTROLS MOUNTED OFF CENTER TOWARDS SHOWER SEAT
E	SHOWER SEAT (FOLDING) - REFER TO TOILET ACCESSORY SCHEDULE
F	GRAB BARS (TYPICAL) - REFER TO MOUNTING HEIGHTS
G	ACCESSIBLE 'REACH' MAXIMUM HEIGHT
L	SOAP DISHES CENTERED AS INDICATED OR PER TILE LAYOUT
M	OPERATION: WATER FLOWS FROM MIXING VALVE TO DIVERTER FAUCET THEN: ACTIVATION OF DIVERTER FAUCET SWITCHES BETWEEN HAND HELD SHOWER AND STANDARD SPOUT / SHOWER
N	PROVIDED BLOCKING AS REQUIRED
P	ACCESSIBLE CONTROLS AREA - PROVIDE MINIMUM DISTANCE PER LOCAL CODE REQUIREMENTS
Q	SLOPE TILE TO FLOOR DRAIN: SLOPE NOT TO EXCEED 1:48
NOTE: ALL GRAB BARS AND SEATS MUST BE BLOCKED / REINFORCED TO SUPPORT MINIMUM OF (250) POUNDS OF VERTICAL AND HORIZONTAL FORCE	

* PROVIDE AN ADJUSTABLE FLOW RATE MULTI-FUNCTION SHOWERHEAD/ HAND SHOWER WITH FINE AND COARSE SPRAY. SHOWERHEAD/ HAND SHOWER MUST INCORPORATE FLOW RATE RESTRICTOR PROVIDING A MAX 2.0 GPM / 7.6 LPM AT MIN. DELIVERED WATER PRESSURE OF 30 PSI / 2.1 BAR. SHOWERHEADS/ HAND SHOWER MUST COMPLY WITH MIN. PERFORMANCE STANDARDS FOR LOW FLOW HEADS SIMILAR TO USEPA WATER SENSE LISTINGS. SHOWERHEAD/ HAND SHOWERS MUST BE APPROVE BY HILTON

GENERAL NOTES

ALL DIMENSIONS UNLESS OTHERWISE NOTED ARE IN INCHES. DIMENSIONS SHOWN IN PARENTHESES ARE FOR INFORMATION ONLY. 

MAUIST ARCHITECTURAL SERVICES
DIVISION OF L.E.M., INC.
112 NORTH MAIN STREET
GOSHEN, INDIANA 46526
PHONE: (574) 537-8500
FAX: (574) 537-0808

HOME 2
SUITES BY HILTON

SHEET SIZE 24x36

FT. WAYNE, INDIANA

REVISIONS:

PRELIMINARY - NOT FOR CONSTRUCTION

DATE: 05/01/26
JOB NO.: MAS-26-105
NAME:
TYPICAL MOUNTING HEIGHTS
SHEET:

A500