
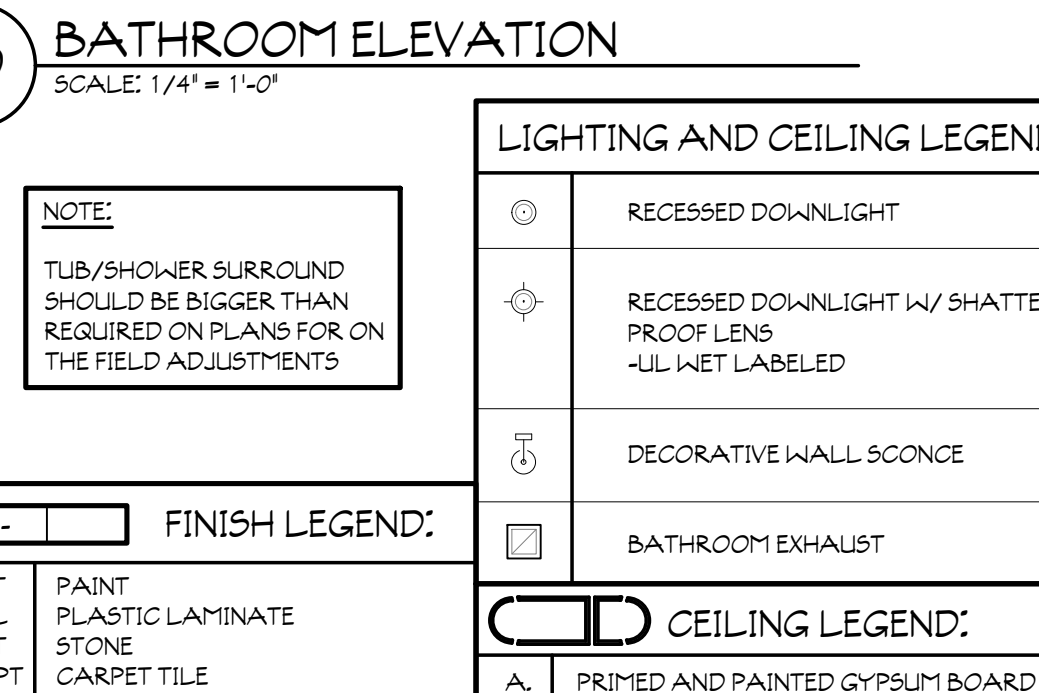
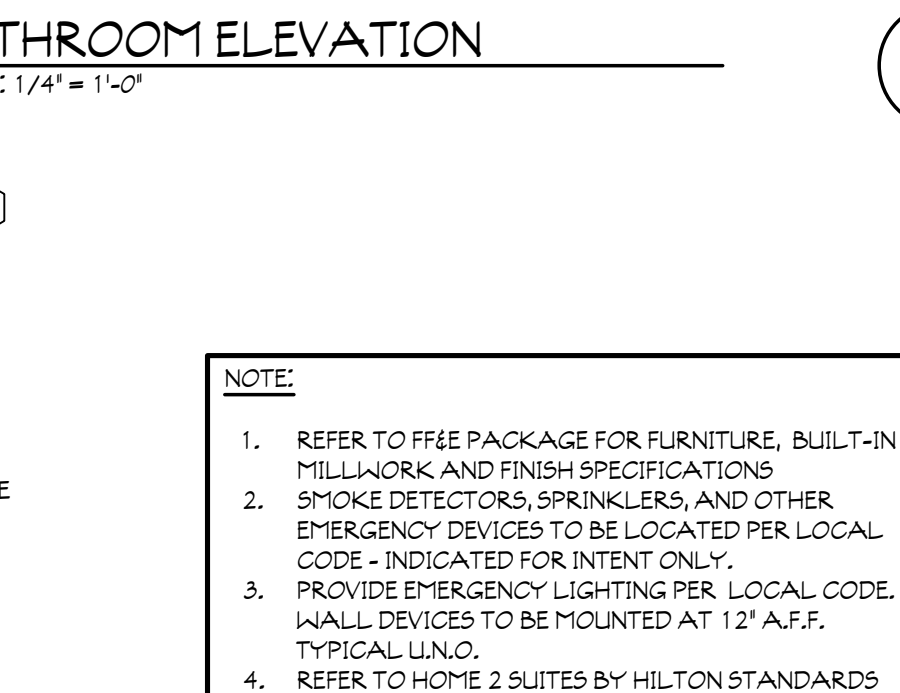
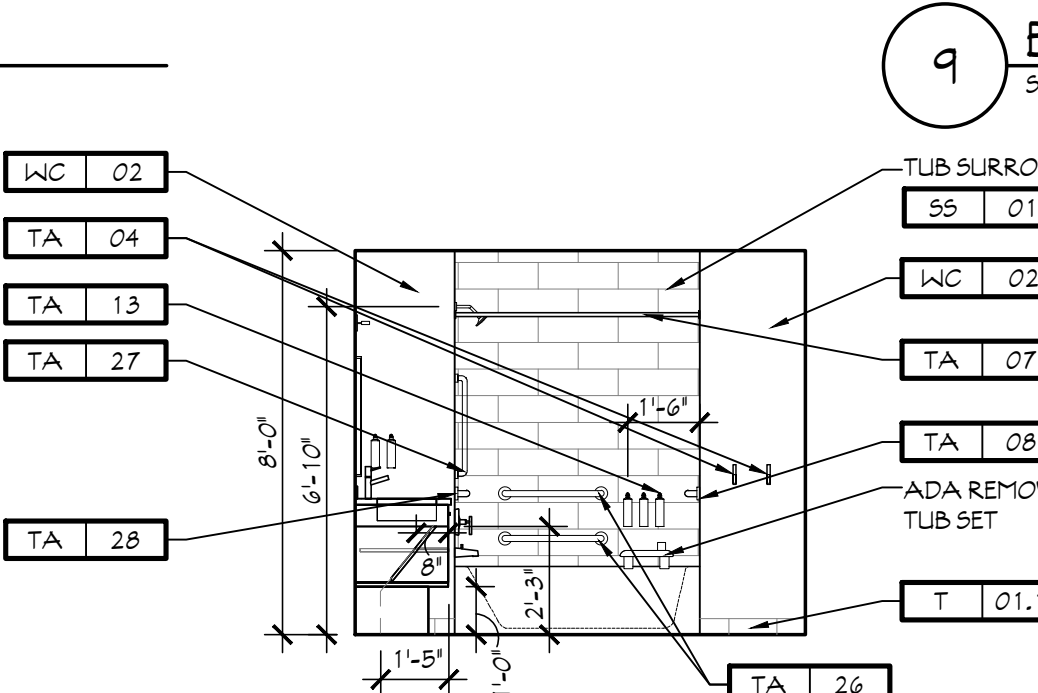
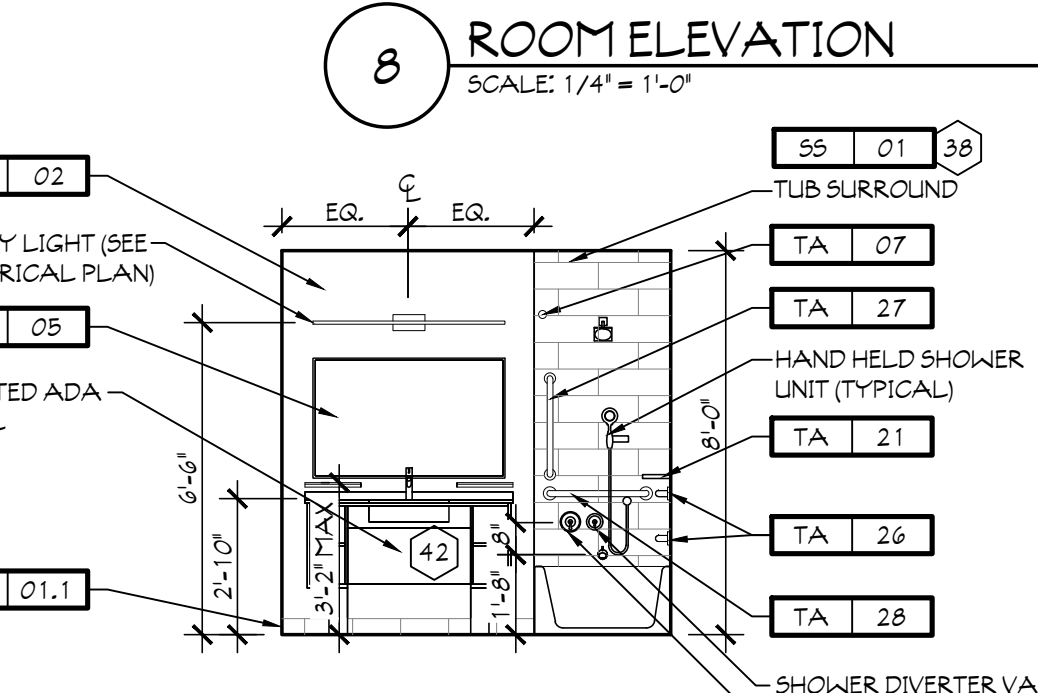
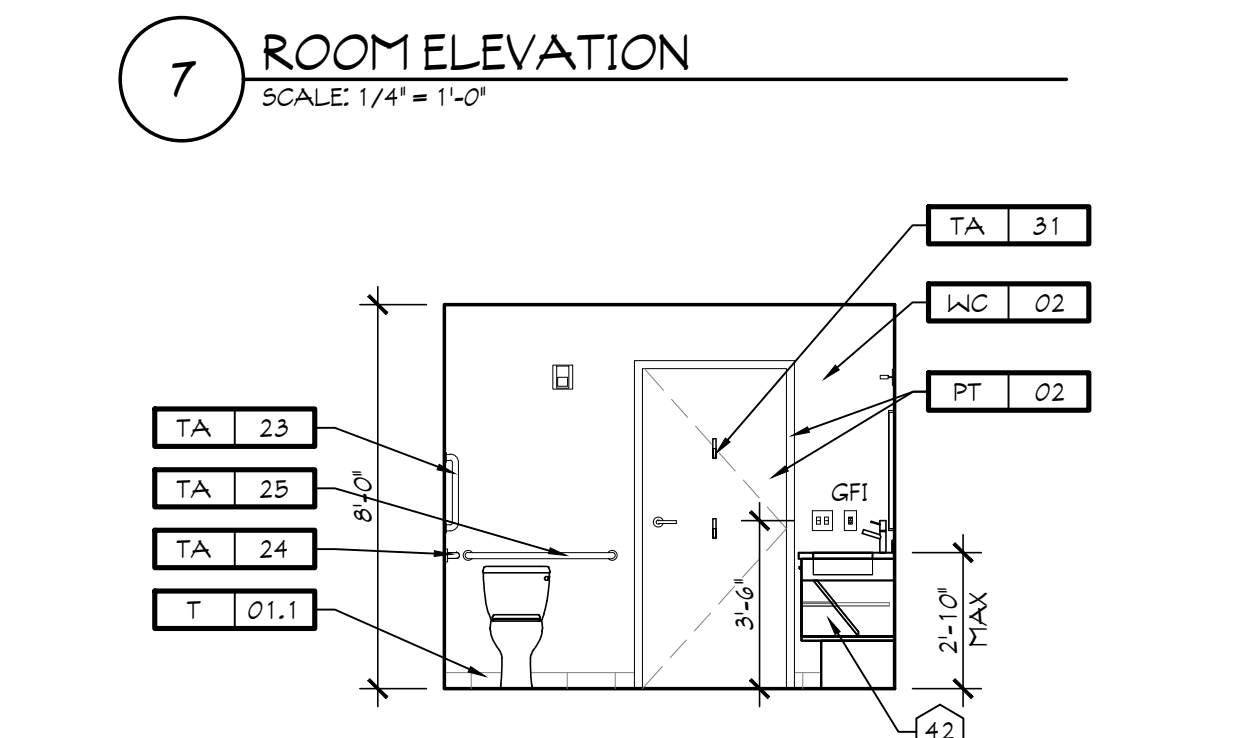
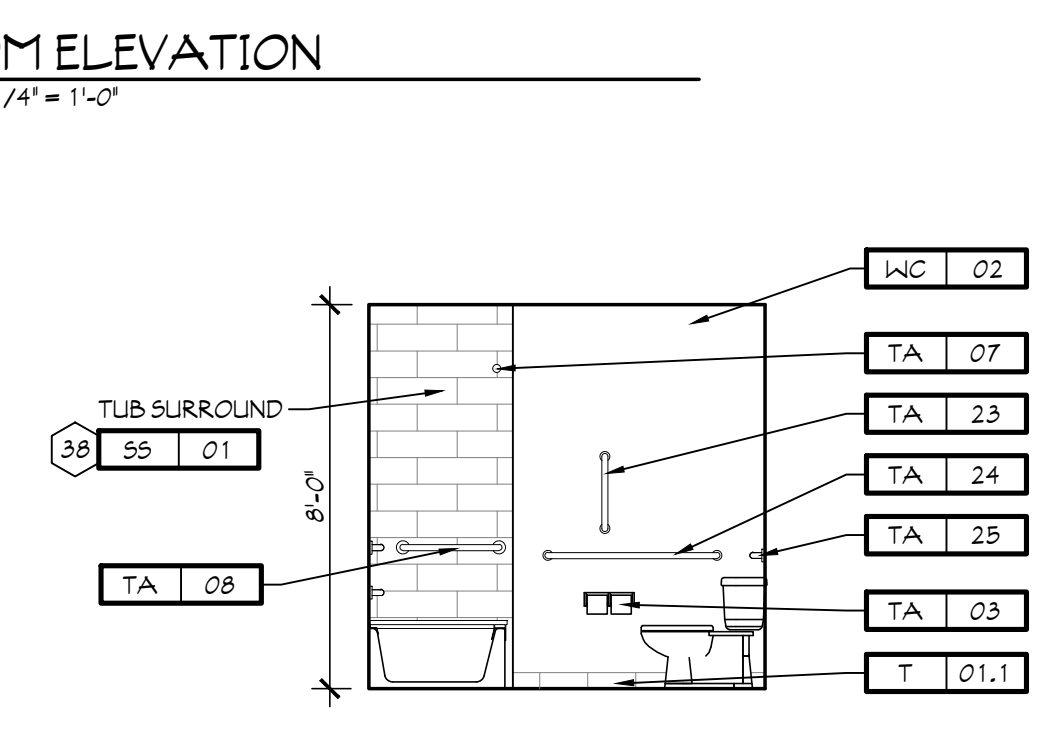
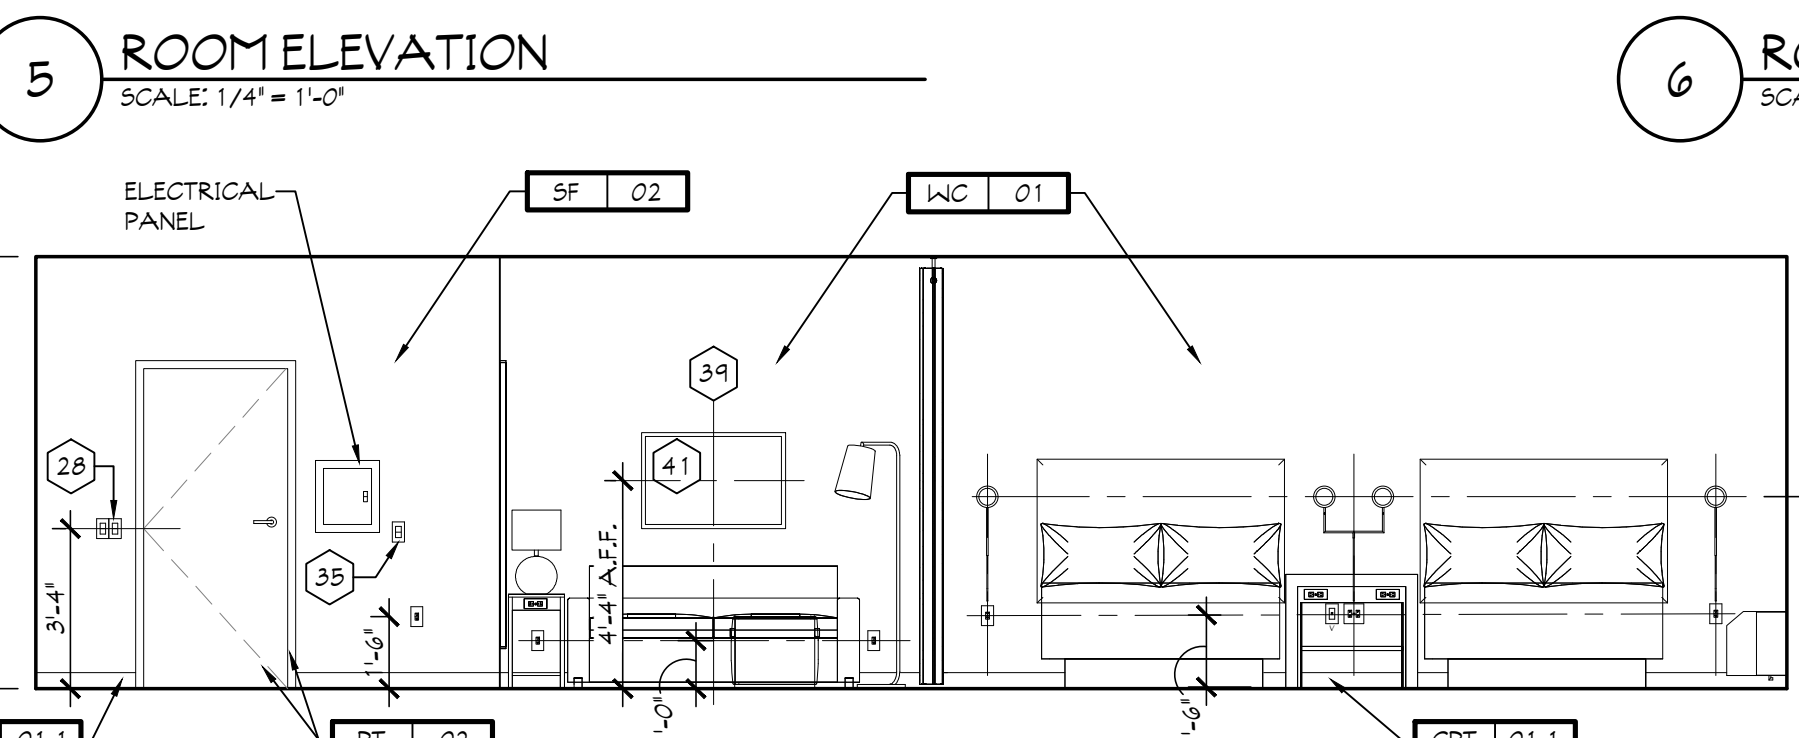
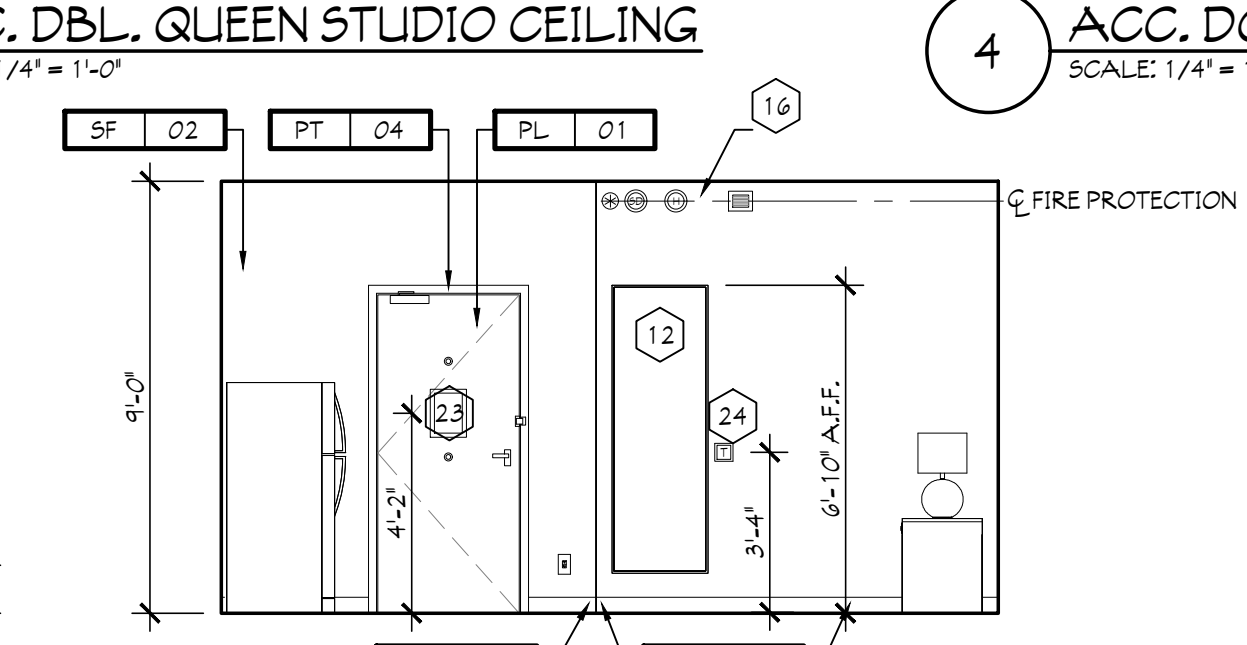
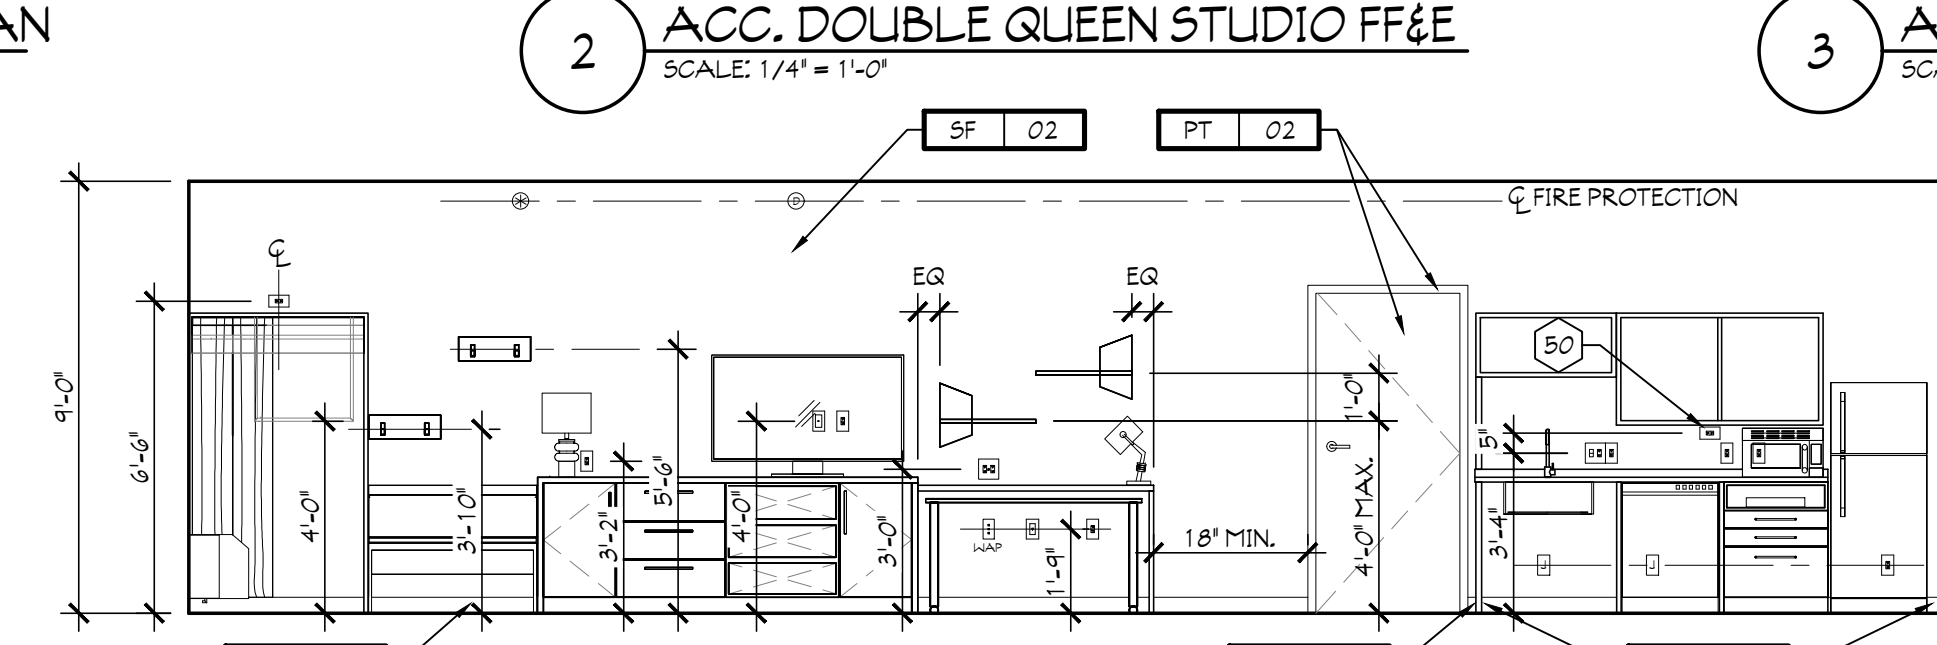
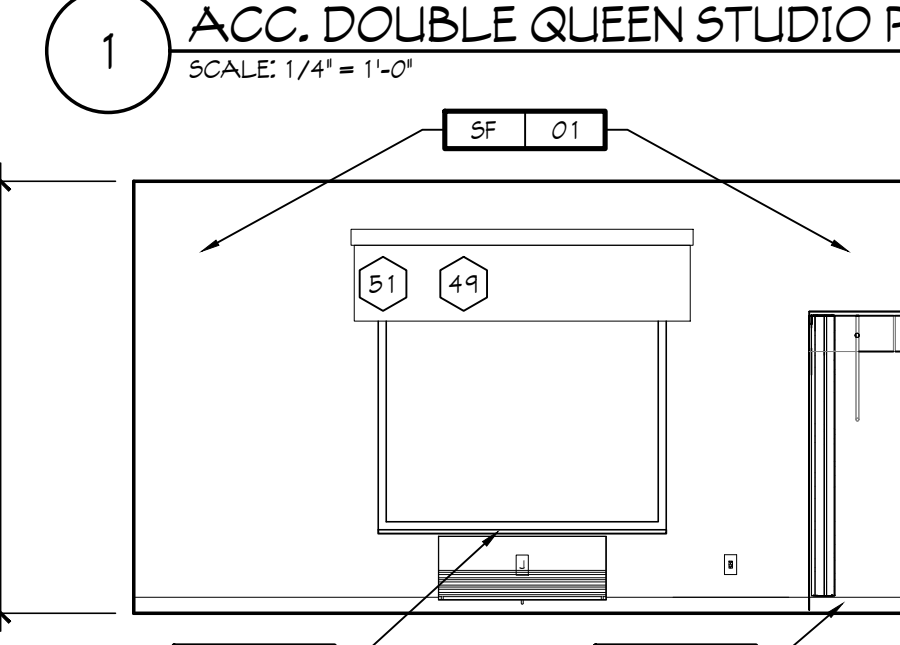
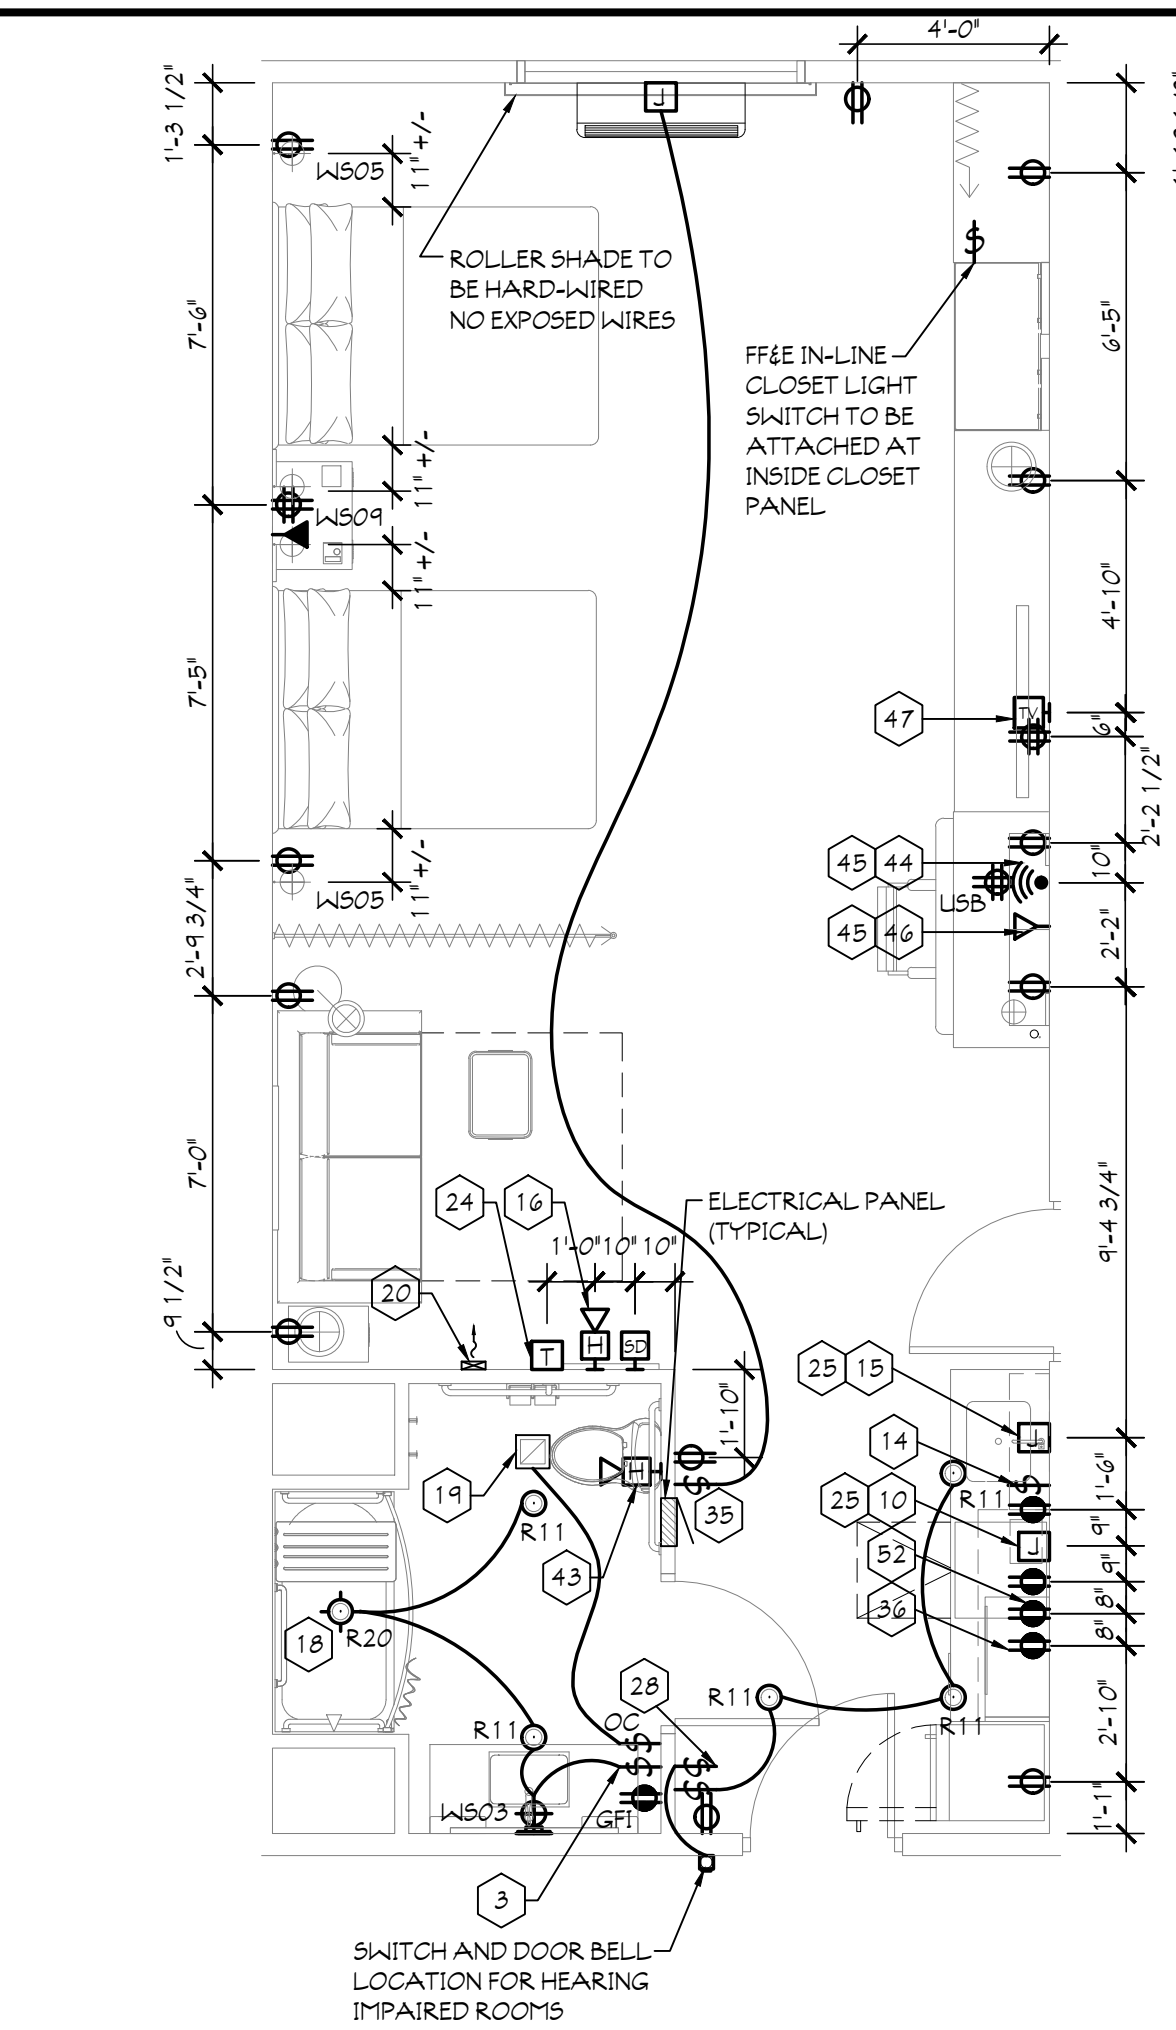
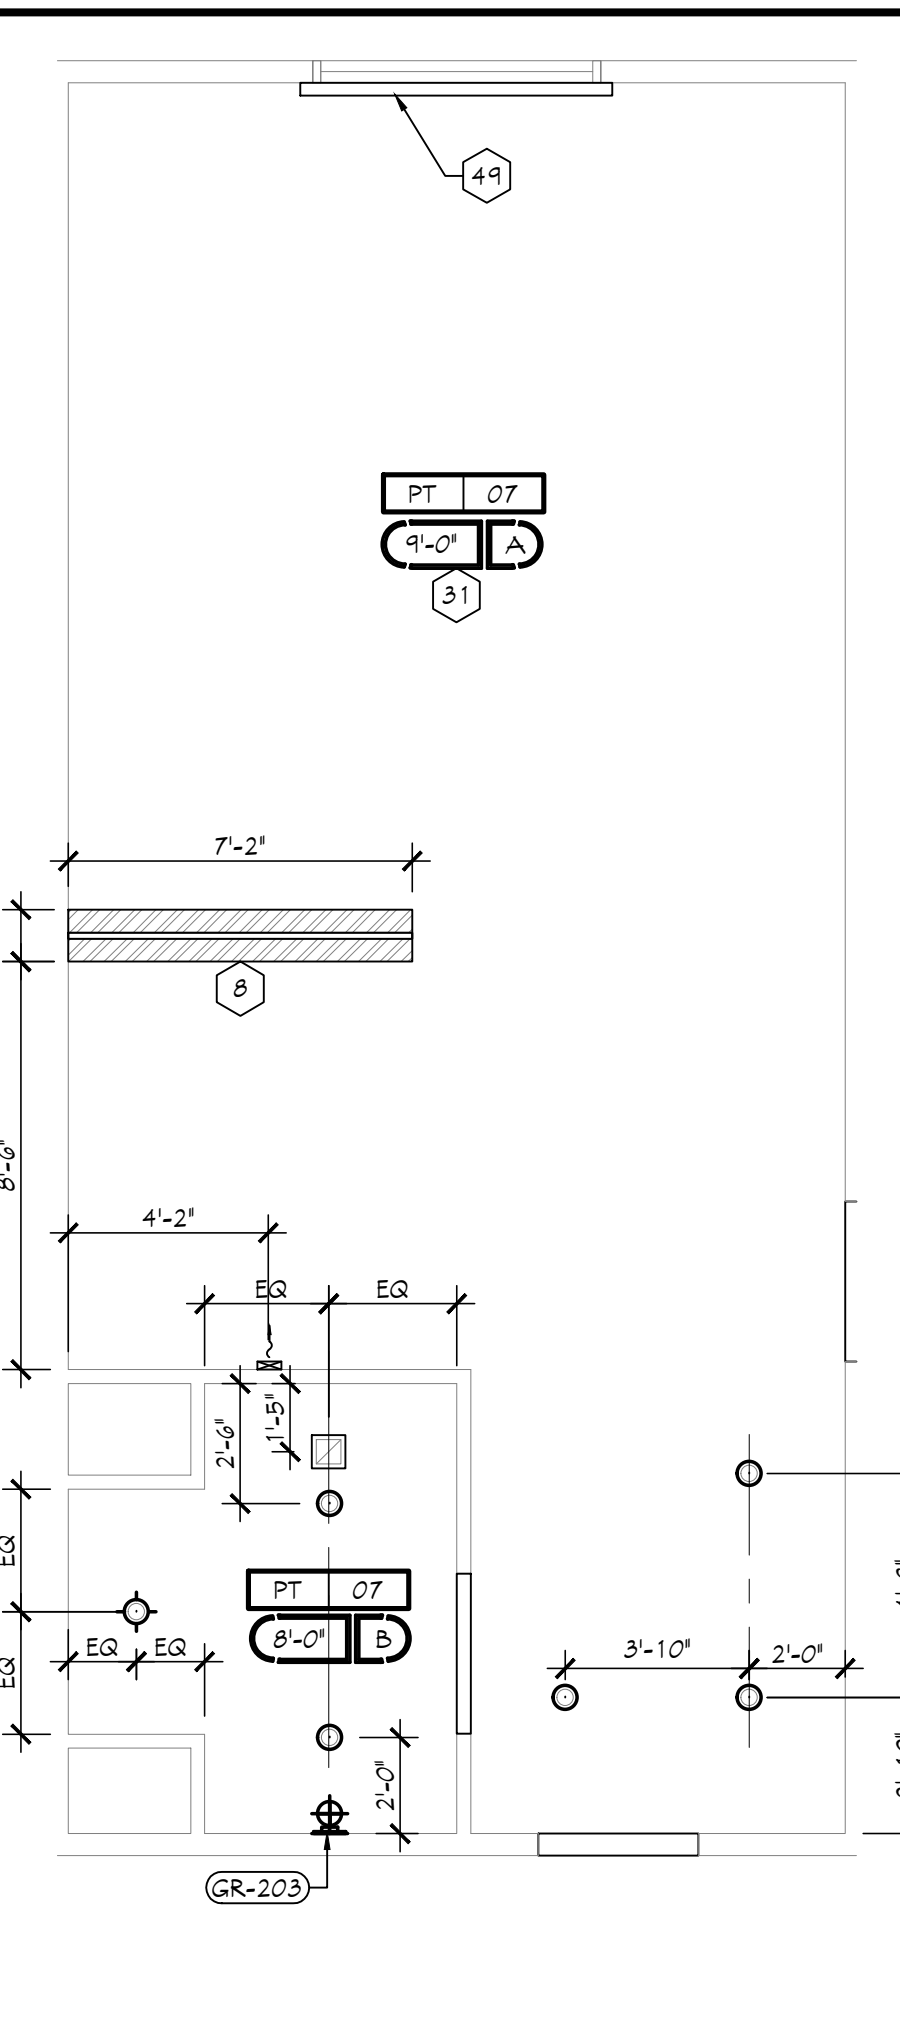
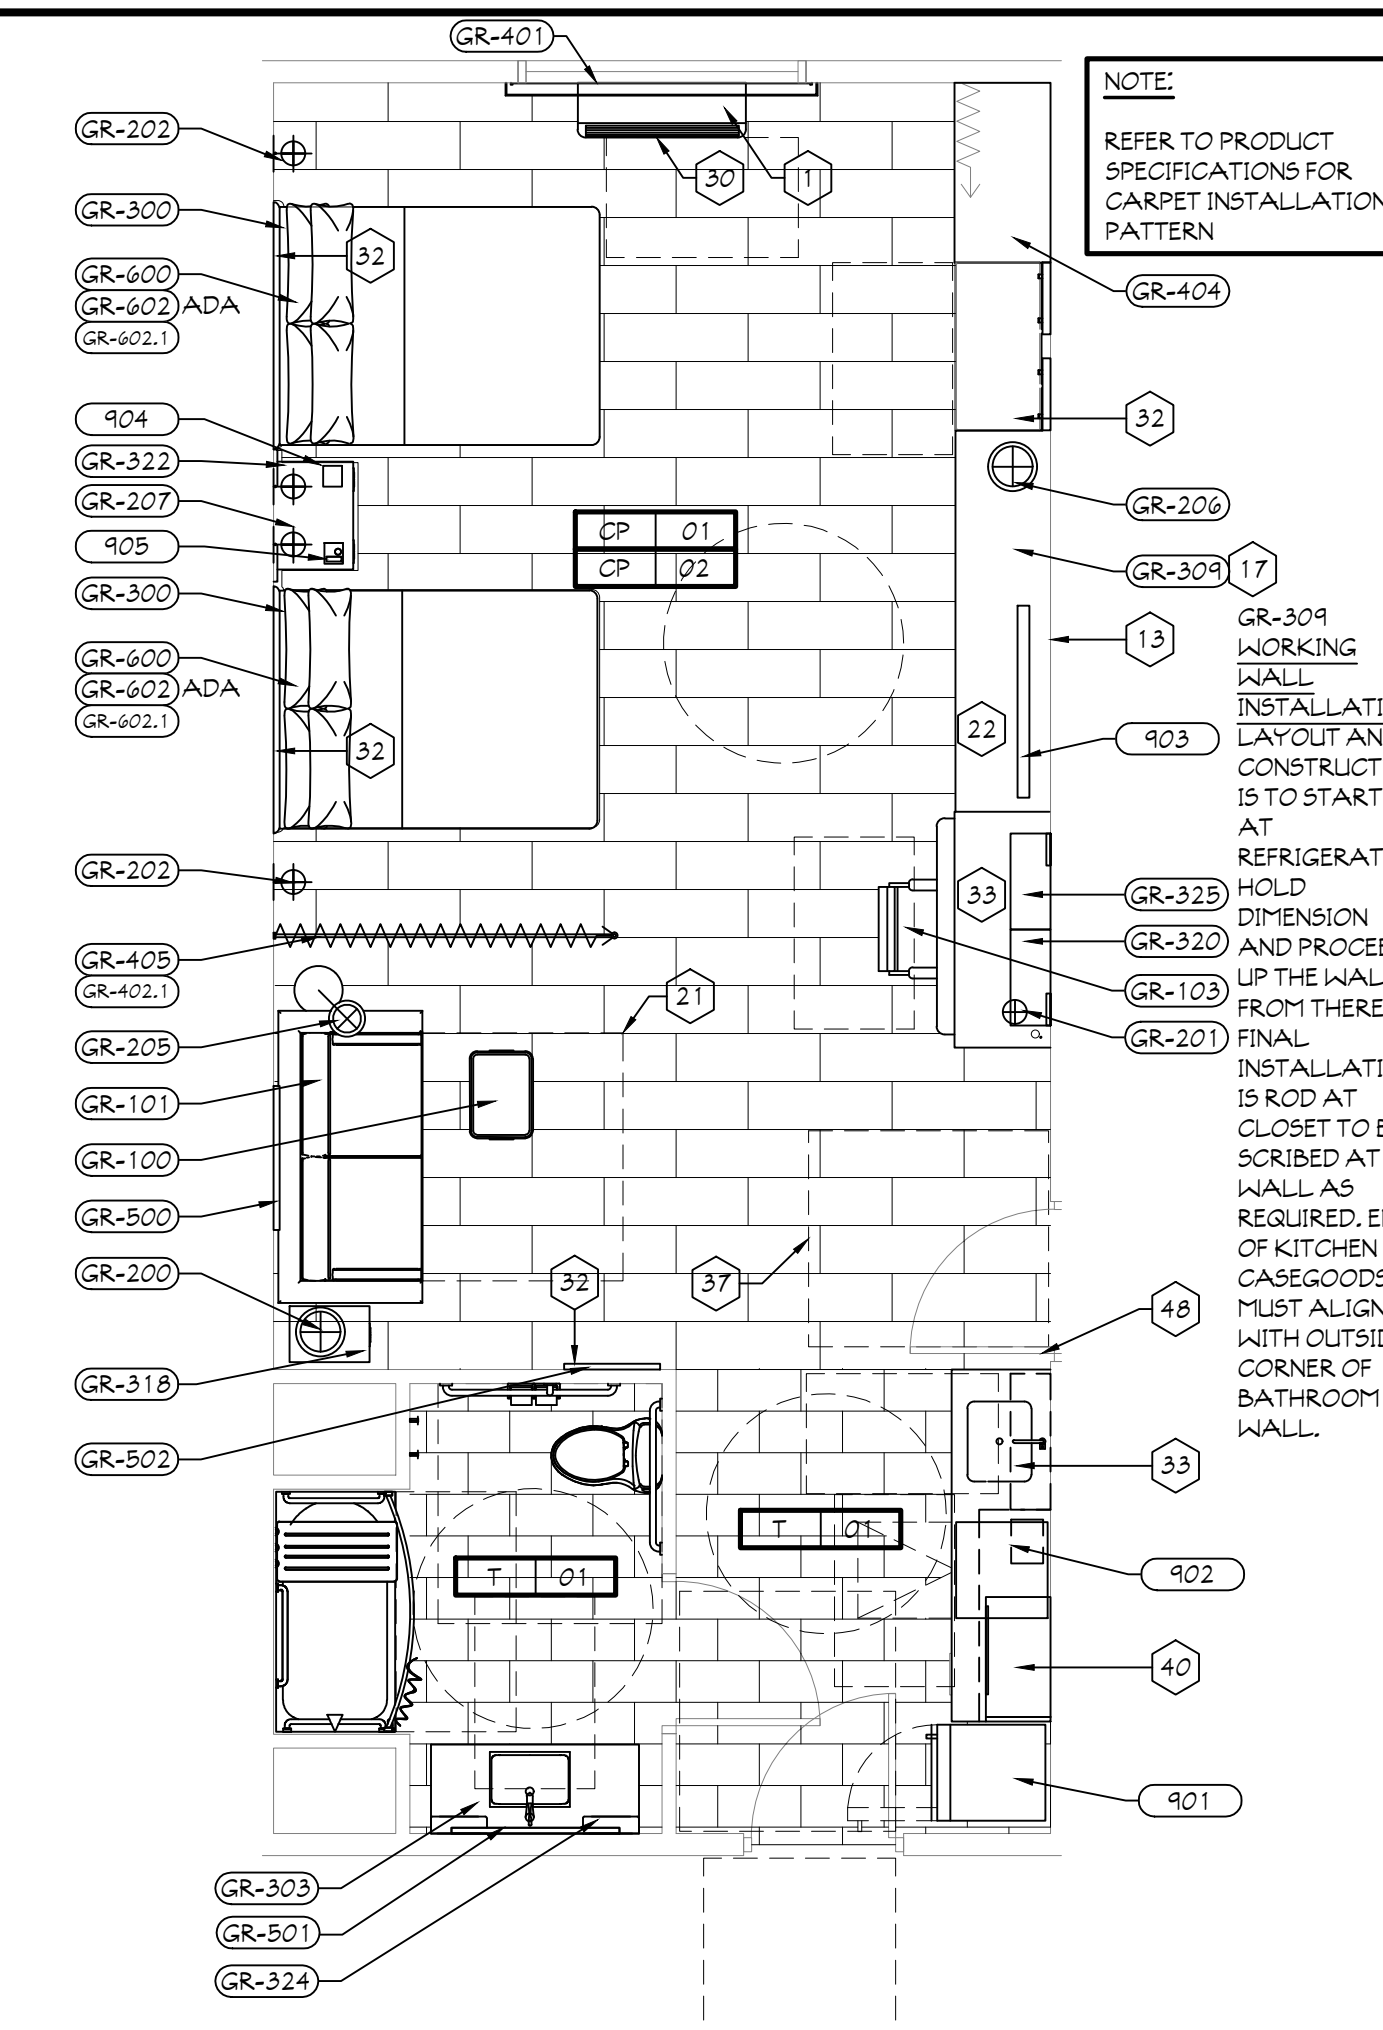


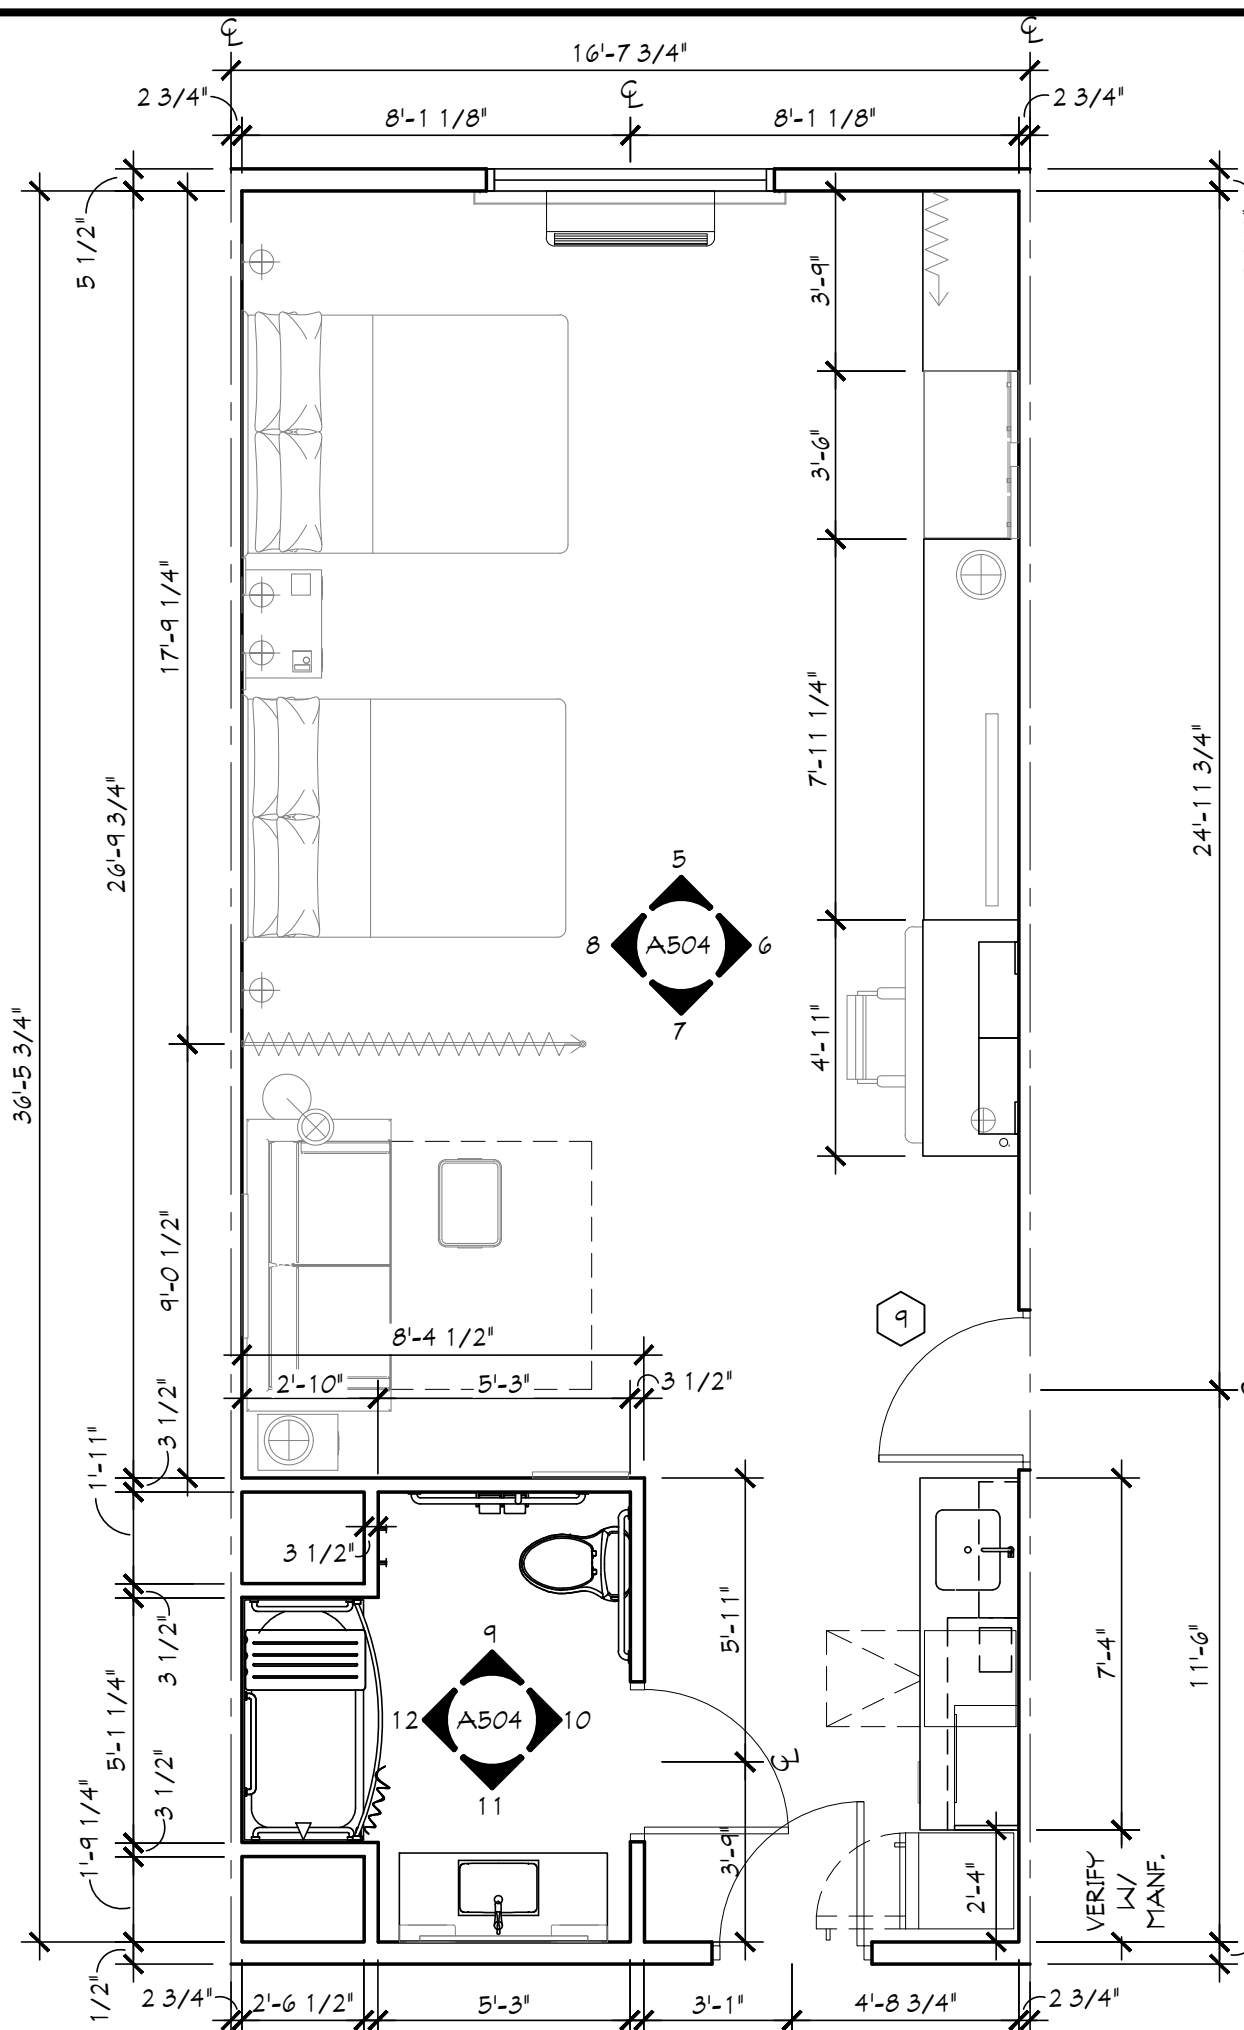

| FURNISHINGS LEGEND: |                                   |
|---------------------|-----------------------------------|
| GR-100              | OTTOMAN @ SOFA                    |
| GR-101              | SLEEPER SOFA                      |
| GR-102              | DINING CHAIR @ ONE BEDROOM SUITE  |
| GR-103              | ERGONOMIC TASK CHAIR              |
| GR-200              | SIDE TABLE LAMP                   |
| GR-201              | DESK LAMP                         |
| GR-202              | NIGHTSTAND SCONCE                 |
| GR-203              | VANITY SCONCE                     |
| GR-204              | SCONCE @ WALL HOOKS               |
| GR-205              | FLOOR LAMP                        |
| GR-206              | TABLE LAMP (ADA)                  |
| GR-207              | NIGHTSTAND SCONCE (DO)            |
| GR-208              | NOT USED                          |
| GR-300              | QUEEN HEADBOARD                   |
| GR-301              | KING HEADBOARD                    |
| GR-302              | VANITY                            |
| GR-303              | ACCESSIBLE VANITY                 |
| GR-304-316          | WORKING WALL                      |
| GR-317              | DINING TABLE                      |
| GR-318              | SOFA SIDE TABLE                   |
| GR-319              | NIGHTSTAND @ RIGHT                |
| GR-320              | RIGHT DECORATIVE SHELF ABOVE DESK |
| GR-321              | WALL SHELF @ BATHROOM             |
| GR-322              | DOUBLE QUEEN NIGHTSTAND           |
| GR-323              | NIGHTSTAND @ LEFT                 |
| GR-324              | WALL SHELF @ ADA BATHROOM         |
| GR-325              | LEFT DECORATIVE SHELF ABOVE DESK  |
| GR-400              | BLACKOUT & SHEER ROLLER SHADE     |
| GR-401              | MOTORIZED ADA ROLLER SHADE        |
| GR-402              | DIVIDER DRAPERY                   |
| GR-402.1            | DIVIDER DRAPERY - HARDWARE        |
| GR-403              | CLOSET DRAPERY                    |
| GR-404              | CLOSET DRAPERY (ADA)              |
| GR-405              | DIVIDER DRAPERY (ADA)             |
| GR-500              | ARTWORK AT SLEEPER SOFA           |
| GR-501              | VANITY MIRROR                     |
| GR-502              | FULL LENGTH MIRROR                |
| GR-600              | QUEEN MATTRESS SET                |
| GR-600.1            | KING MATTRESS SET                 |
| GR-601              | KING BEDWRAP                      |
| GR-602              | QUEEN BED BASE                    |
| GR-602.ADA          | QUEEN ACCESSIBLE BED BASE         |
| GR-603              | ACCESSIBLE QUEEN BED SKIRT (ADA)  |
| GR-603.ADA          | KING ACCESSIBLE BED BASE          |
| GR-603.1            | ACCESSIBLE KING BED SKIRT (ADA)   |
| GR-604              | REFRIGERATOR                      |
| GR-605              | DISHWASHER                        |
| GR-606              | TELEVISION                        |
| GR-607              | CLOCK/RADIO                       |
| GR-608              | TELEPHONE                         |

| LIGHTING AND CEILING LEGEND: |                                                            |
|------------------------------|------------------------------------------------------------|
| ⊙                            | RECESSED DOWNLIGHT                                         |
| ⊙                            | RECESSED DOWNLIGHT W/ SHATTER PROOF LENS - JUL WET LABELED |
| ⊙                            | DECORATIVE WALL SCONCE                                     |
| ⊙                            | BATHROOM EXHAUST                                           |

| CEILING LEGEND: |                                                      |
|-----------------|------------------------------------------------------|
| A.              | PRIMED AND PAINTED GYPSUM BOARD                      |
| B.              | PRIMED AND PAINTED GYPSUM BOARD - MOISTURE RESISTANT |

NOTE:  
TUB/SHOWER SURROUND SHOULD BE BIGGER THAN REQUIRED ON PLANS FOR ON THE FIELD ADJUSTMENTS

- NOTE:
- REFER TO FREE PACKAGE FOR FURNITURE, BUILT-IN MILLWORK AND FINISH SPECIFICATIONS. SMOKE DETECTORS, SPRINKLERS, AND OTHER EMERGENCY DEVICES TO BE LOCATED PER LOCAL CODE - INDICATED FOR INTENT ONLY.
  - PROVIDE EMERGENCY LIGHTING PER LOCAL CODE. WALL DEVICES TO BE MOUNTED AT 12" A.F.F. TYPICAL UNLO.
  - REFER TO HILTON 2 SUITES BY HILTON STANDARDS MANUAL FOR ADDITIONAL GUESTROOM, GUESTROOM BATH, GUESTROOM KITCHEN AND INDOOR POOL REQUIREMENTS.

| FINISH LEGEND: |                   |
|----------------|-------------------|
| PT             | PAINT             |
| PL             | PLASTIC LAMINATE  |
| ST             | STONE             |
| CP             | CARPET TILE       |
| T              | CARPET BASE       |
| WC             | TILE WALLCOVERING |

| KEY NOTES: |   |
|------------|---|
| 1          | PTAC UNIT   |
| 3          | IN BATHROOM LOCATIONS ONLY, LIGHT SWITCH EQUIPPED WITH NIGHTLIGHT, MOUNTED 50 TOP OF SWITCH IS 48" MAX A.F.F.   |
| 4          | MANUAL BLACK OUT ROLLER SHADE TO EXTEND 6" BEYOND WINDOW OPENING; SHEER ROLLER SHADE TO BE MOUNTED INSIDE WINDOW OPENING   |
| 5          | SHOWER ENCLOSURE WITH TEMPERED GLASS DOOR   |
| 6          | FLOOR DRAIN   |
| 7          | PRE-MANUFACTURED SHOWER PAN   |
| 8          | CEILING MOUNTED DRAPERY ROD - PROVIDE BLOCKING AS REQUIRED   |
| 9          | ALTERNATE LOCATION OF DOOR FOR CONNECTING ROOMS TO ACCESSIBLE ROOMS - REFER TO OVERALL PLANS FOR LOCATION OF ACCESSIBLE ROOMS   |
| 10         | DEDICATED CIRCUIT FOR DISHWASHER   |
| 11         | RANGE TOP STYLE MICROWAVE AFFIXED TO WALL   |
| 12         | MIRROR   |
| 13         | BEGIN CARPET TILE THIS SIDE WITH FULL TILE - FIRST TWO ROWS OF TILE TO BE INSTALLED AROUND BUILT-IN CASEGOODS   |
| 14         | SWITCH CONTROLLING GARBAGE DISPOSAL GANGED WITH DUPLEX REFER TO HADG FOR ACCESSIBLE ROOM REQUIREMENTS.   |
| 15         | DEDICATED CIRCUIT FOR GARBAGE DISPOSAL   |
| 16         | FIRE HORN IN STANDARD ROOMS. FIRE HORN/STROBE IN COMMUNICATION FEATURES ROOMS   |
| 17         | LAYOUT AND CONSTRUCTION IS TO START AT REFRIGERATOR HOLD DIM. & PROCEED UP THE WALL FROM THAT END-FINAL INSTALLATION IS ROD AT CLOSET, TO BE SCRIBED AT WALL AS REQUIRED. END OF KITCHEN MUST TERMINATE AT OUTSIDE FACE OF BATHROOM WALL.   |
| 18         | RECESSED CEILING LIGHT FOR WET LOCATIONS WITH SHATTER PROOF LENS   |
| 19         | TOILET EXHAUST GRILLE   |
| 20         | MAKE-UP AIR DIFFUSER   |
| 21         | EXTENT OF SLEEPER SOFA   |
| 22         | APPROXIMATE LOCATIONS OF MILLWORK SUPPORTS ON FLOOR. PROVIDE SHIMS OR LEVELERS UNDER SUPPORTS TO PREVENT CARPET CRUSHING   |
| 23         | ROOM SIGNAGE   |
| 24         | HARD WIRED THERMOSTAT FOR PTAC, MOUNTED 48" MAX TO TOP OF DEVICE. COMMUNICATION BETWEEN THERMOSTAT AND PTAC MAY BE WIRELESS.   |
| 25         | EXTEND J-BOX, DEVICE AND COVER PLATE FLUSH WITH MILLWORK BACK PANEL   |
| 26         | DROPPED GYPSUM BOARD BULKHEAD @ ROUGH OPENING - WHERE PRE-MANUFACTURED SHOWER INSERT IS INDICATED MEASURE ROUGH OPENING FROM FACE OF GYPSUM BOARD   |
| 28         | DOORBELL ON/OFF SWITCH (COMMUNICATION FEATURES ROOMS ONLY) SIGNAGE AS REQ'D.   |
| 30         | EDGE OF PTAC ABOVE CARPET TILES   |
| 31         | MIN. CEILING HEIGHT MUST BE MAINTAINED - REFER TO HOME 2 SUITES BY HILTON STANDARDS MANUAL   |
| 32         | FRAMING SUBCONTRACTOR TO PROVIDE 3/4" F.R.T. PLYWOOD BLOCKING TO RECEIVE ITEM INDICATED - EXTEND FULL LENGTH OF OBJECT   |
| 33         | GENERAL CONTRACTOR TO COORDINATE WITH FIXTURE FABRICATOR WHERE NECESSARY TO PROVIDE PROPER BLOCKING IN WALL FOR ITEM KEYNOTED   |
| 34         | BI-PASS SLIDING GLASS DOOR, BRUSHED ALUMINUM FINISH, CLEAR GLASS, WITH 24" BAR PULL HARDWARE   |
| 35         | SWITCHES CONTROLLING MECHANICAL SHADES - REFER TO FFE MANUAL   |
| 36         | OUTLET ABOVE FOR MICROWAVE - REFER TO ROOM ELEVATION MOUNT DEVICE HORIZONTALLY - FACE PLATE TO BE WHITE   |
| 37         | REQUIRED ACCESSIBLE FLOOR AREA DESIGNATION   |
| 39         | CENTER ARTWORK OVER SOFA   |
| 40         | COUNTERTOP MICROWAVE   |
| 41         | GRAPHIC ART REFER TO ACCESSORIES LEGEND AND CONSTRUCTION PLAN   |
| 42         | ACCESSIBLE VANITY; CLEAR AREA OF SINK/VANITY MUST BE ACCESSIBLE   |
| 43         | ADDITIONAL HORN STROBE; LOCATED IN C.F. BATHROOMS ONLY   |
| 44         | WAP IN 3-GANG BOX MOUNTED VERTICALLY UNDER DESK; MAINTAIN 6" BETWEEN ALL BOXES. TYP. ALL GUESTROOMS. COORDINATE WALL LOCATION WITH CASEGOODS TO AVOID CONFLICTS. VISIT CONNECTED ROOM HILTON.COM FOR CURRENT WIRELESS INTERNET REQ'S AND LIST OF APPROVED INTEGRATORS.   |
| 45         | EACH CABLE MUST HOMERUN BETWEEN THE GUESTROOM AND THE IDF ON EACH FLOOR. VISIT CONNECTED ROOM HILTON.COM FOR CURRENT REQUIREMENTS AND OPTIONS.   |
| 46         | OPTION WIRELESS DATA CONNECTION FOR GUEST USE: A) ADD CAT6 RJ-45 CABLE JACK AND PATCH CORD THROUGH DESKTOP GROMMET - OR - B) PATCH CORD FROM WAP PORT THROUGH DESKTOP GROMMET, IF OUTLET IS LOCATED ABOVE THE DESK, REMOVE GROMMET AND PATCH CORD.   |
| 47         | TV CONNECTIONS FOR FREE-TO-GUEST CONTENT: A) NO SMART TV: COAX CABLE BEHIND TV. CAT6 RJ-45 JACK BEHIND TV, RUN IN SHURF TUBE IN WALL TO WAP UNDER DESK. PATCH CORD TO EDGE CONTROLLER FOR CONNECTED ROOM. MIN. 6" CLEARANCE FROM WALL BOXES - OR - B) SMART TV: INTERNET PROTOCOL TELEVISION COAX NOT REQ'D. CAT6 RJ-45 JACK BEHIND TV, RUN IN SHURF TUBE IN WALL TO WAP UNDER DESK. PATCH CORD TO EDGE CONTROLLER FOR CONNECTED ROOM. CAT6 RJ-45 JACK BEHIND TV IN ONE-BEDROOM TV, MIN. 6" CLEARANCE FROM WALL BOXES. VISIT HILTONHDTV.COM FOR ADDITIONAL INFORMATION. |
| 48         | PROVIDE HINGE STOP AT DOOR   |
| 49         | HARDWIRED BLACK OUT ROLLER SHADE WITH NO EXPOSED WIRES   |
| 50         | PROVIDE OUTLET FOR UNDER CABINET LIGHTING BY OTHERS. COORDINATE WITH ELECTRICAL AT ACC. GUESTROOMS; THE COOK LIGHT AT MOUNTED MICROWAVE FOR NON-ACC ROOMS WILL SUFFICE   |
| 51         | ROLLER SHADE TO EXTEND PAST WINDOW FRAME TO REDUCE LIGHT LEAK - REFER TO SPECIFICATION AND MANUFACTURER'S INSTALLATION REQUIREMENTS   |
| 52         | DEDICATED CIRCUIT FOR INDUCTION BURNER   |

GENERAL NOTES

ALTHOUGH DIMENSIONS ARE GIVEN TO SCALE, THE ACCURACY OF THE DRAWINGS CANNOT BE GUARANTEED. DIMENSIONS SHALL BE DELETED OF REPRODUCTION. DIMENSIONS SHOULD BE DELETED OF REPRODUCTION.

ALL DIMENSIONS UNLESS OTHERWISE NOTED. ALL DIMENSIONS SHALL BE IN FEET AND INCHES. ALL DIMENSIONS SHALL BE TO FACE UNLESS OTHERWISE NOTED. ALL DIMENSIONS SHALL BE TO FACE UNLESS OTHERWISE NOTED.

MAINTENANCE SHALL NOT BE HELD RESPONSIBLE FOR ANY DAMAGE TO THE PROPERTY OF THE GENERAL CONTRACTOR. MAINTENANCE SHALL NOT BE HELD RESPONSIBLE FOR ANY DAMAGE TO THE PROPERTY OF THE GENERAL CONTRACTOR.

MAINTENANCE SHALL NOT BE HELD RESPONSIBLE FOR ANY DAMAGE TO THE PROPERTY OF THE GENERAL CONTRACTOR. MAINTENANCE SHALL NOT BE HELD RESPONSIBLE FOR ANY DAMAGE TO THE PROPERTY OF THE GENERAL CONTRACTOR.

Architects  
Planners  
Construction Mgmt.  
Rule 5 and MS4 Filing

MAUIST ARCHITECTURAL SERVICES  
DIVISION OF  
L.E.M., INC.  
112 NORTH MAIN STREET  
GOSHEN, INDIANA 46526

PHONE: (574) 537-8500  
FAX: (574) 537-0808

HOME 2  
SUITES BY HILTON

SHEET SIZE 24x36

FT. WAYNE, INDIANA

REVISIONS:

DATE: 05/01/26  
JOB NO.: MAS-26-105  
NAME:  
ACCESSIBLE DOUBLE QUEEN STUDIO  
SHEET:

PRELIMINARY - NOT FOR CONSTRUCTION

A504