



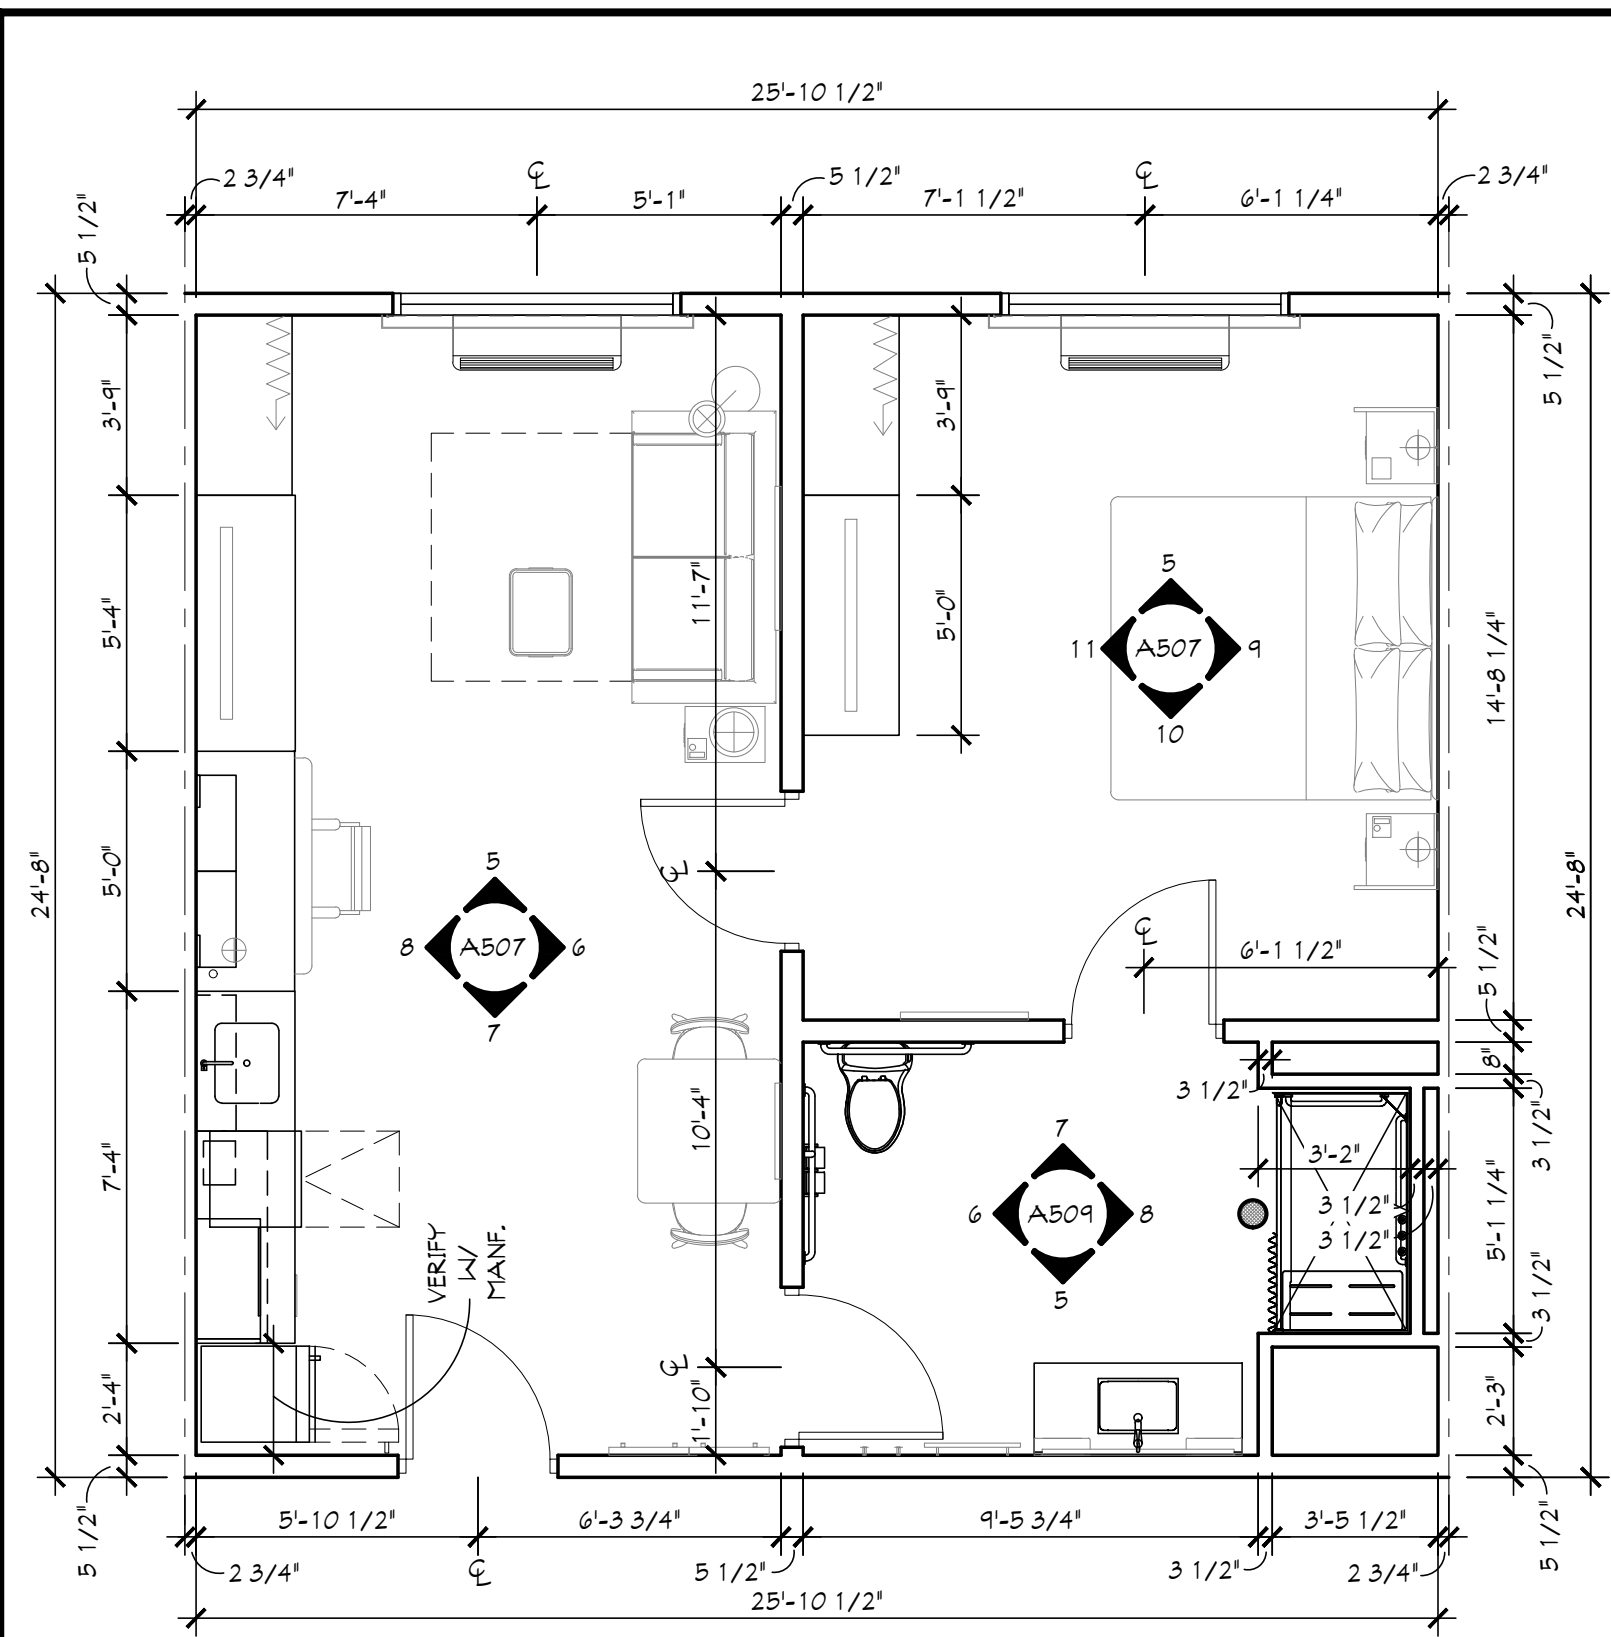


1 ACC. ONE BEDROOM ROLL-IN PLAN
SCALE: 1/4" = 1'-0"


GR-316
WORKING WALL INSTALLATION:
LAYOUT AND CONSTRUCTION IS TO
START AT REFRIGERATOR HOLD
DIMENSION AND PROCEED UP THE WALL
FROM THERE. FINAL INSTALLATION IS
ROD AT CLOSET TO BE SCRIBED AT
WALL AS REQUIRED.

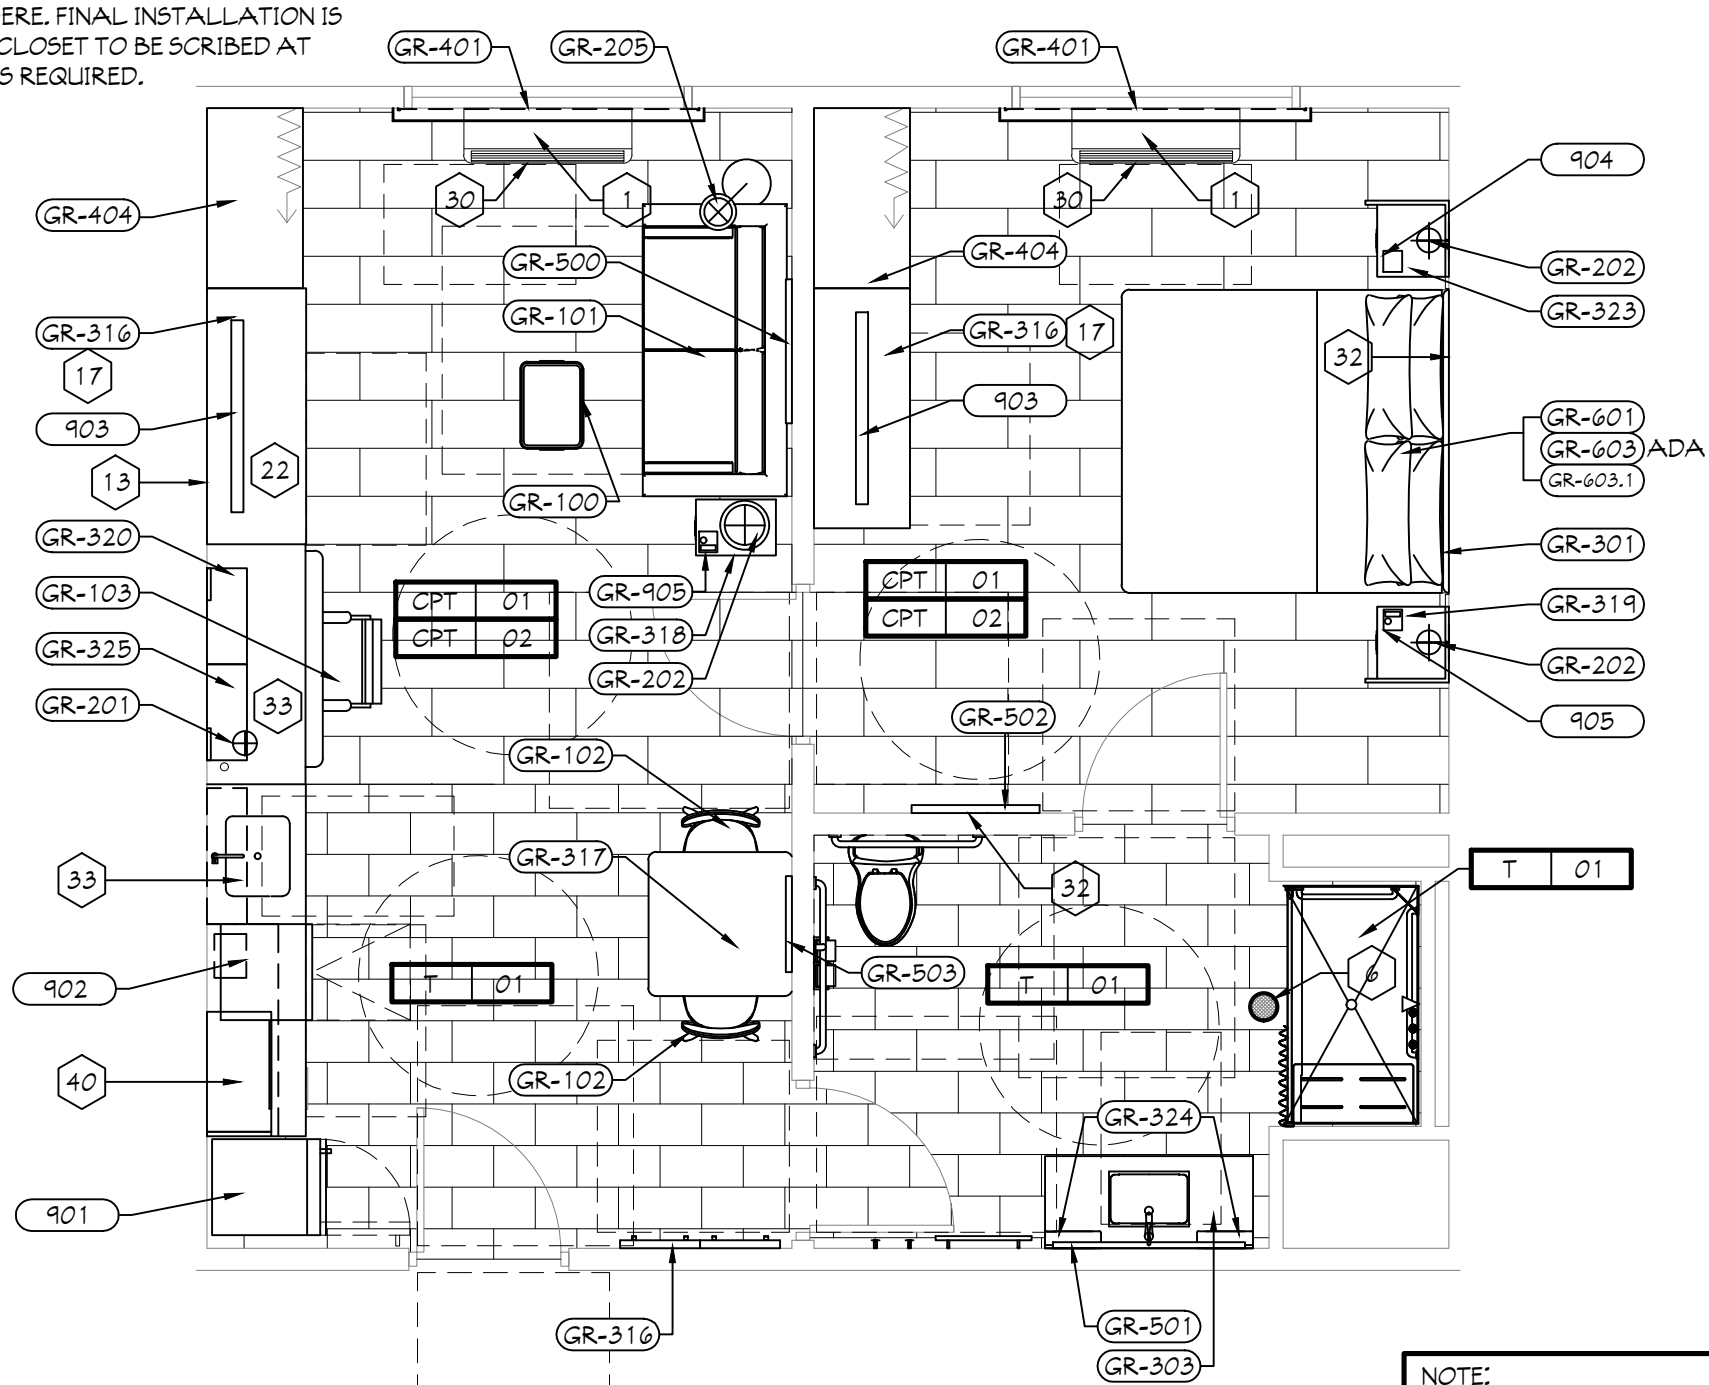


2 ACC. ONE BEDROOM ROLL-IN FF&E
SCALE: 1/4" = 1'-0"

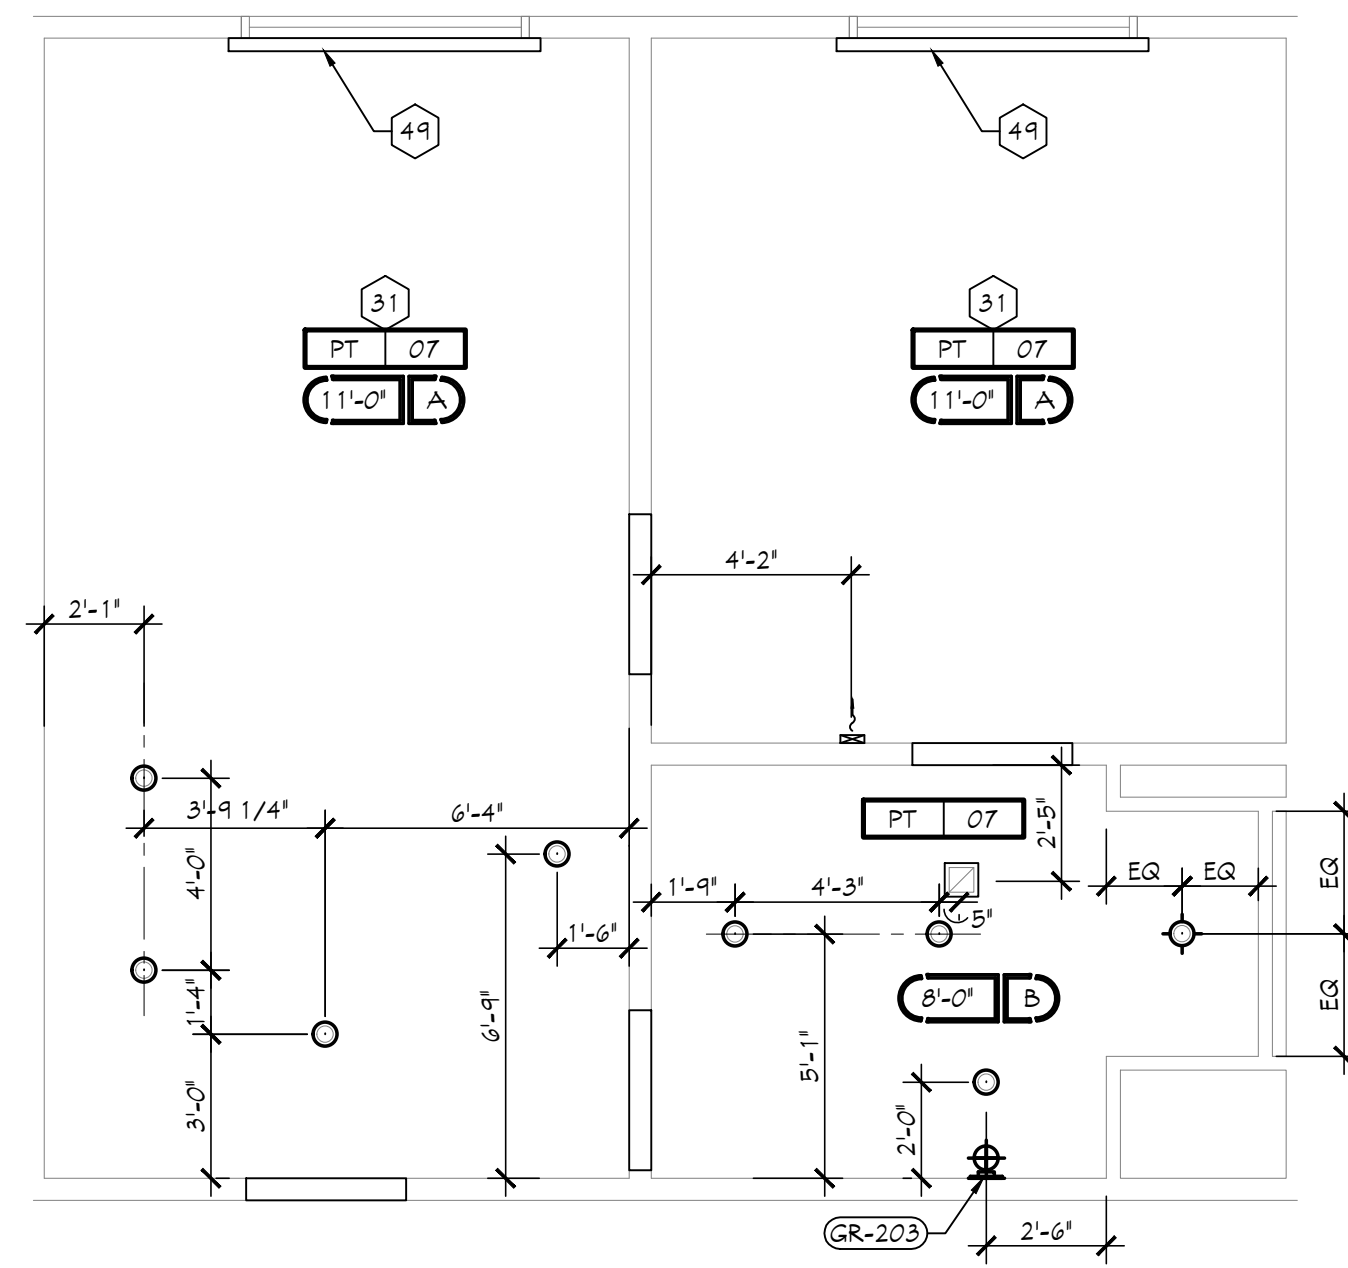


3 ACC. ONE BEDROOM ROLL-IN CEILING
SCALE: 1/4" = 1'-0"

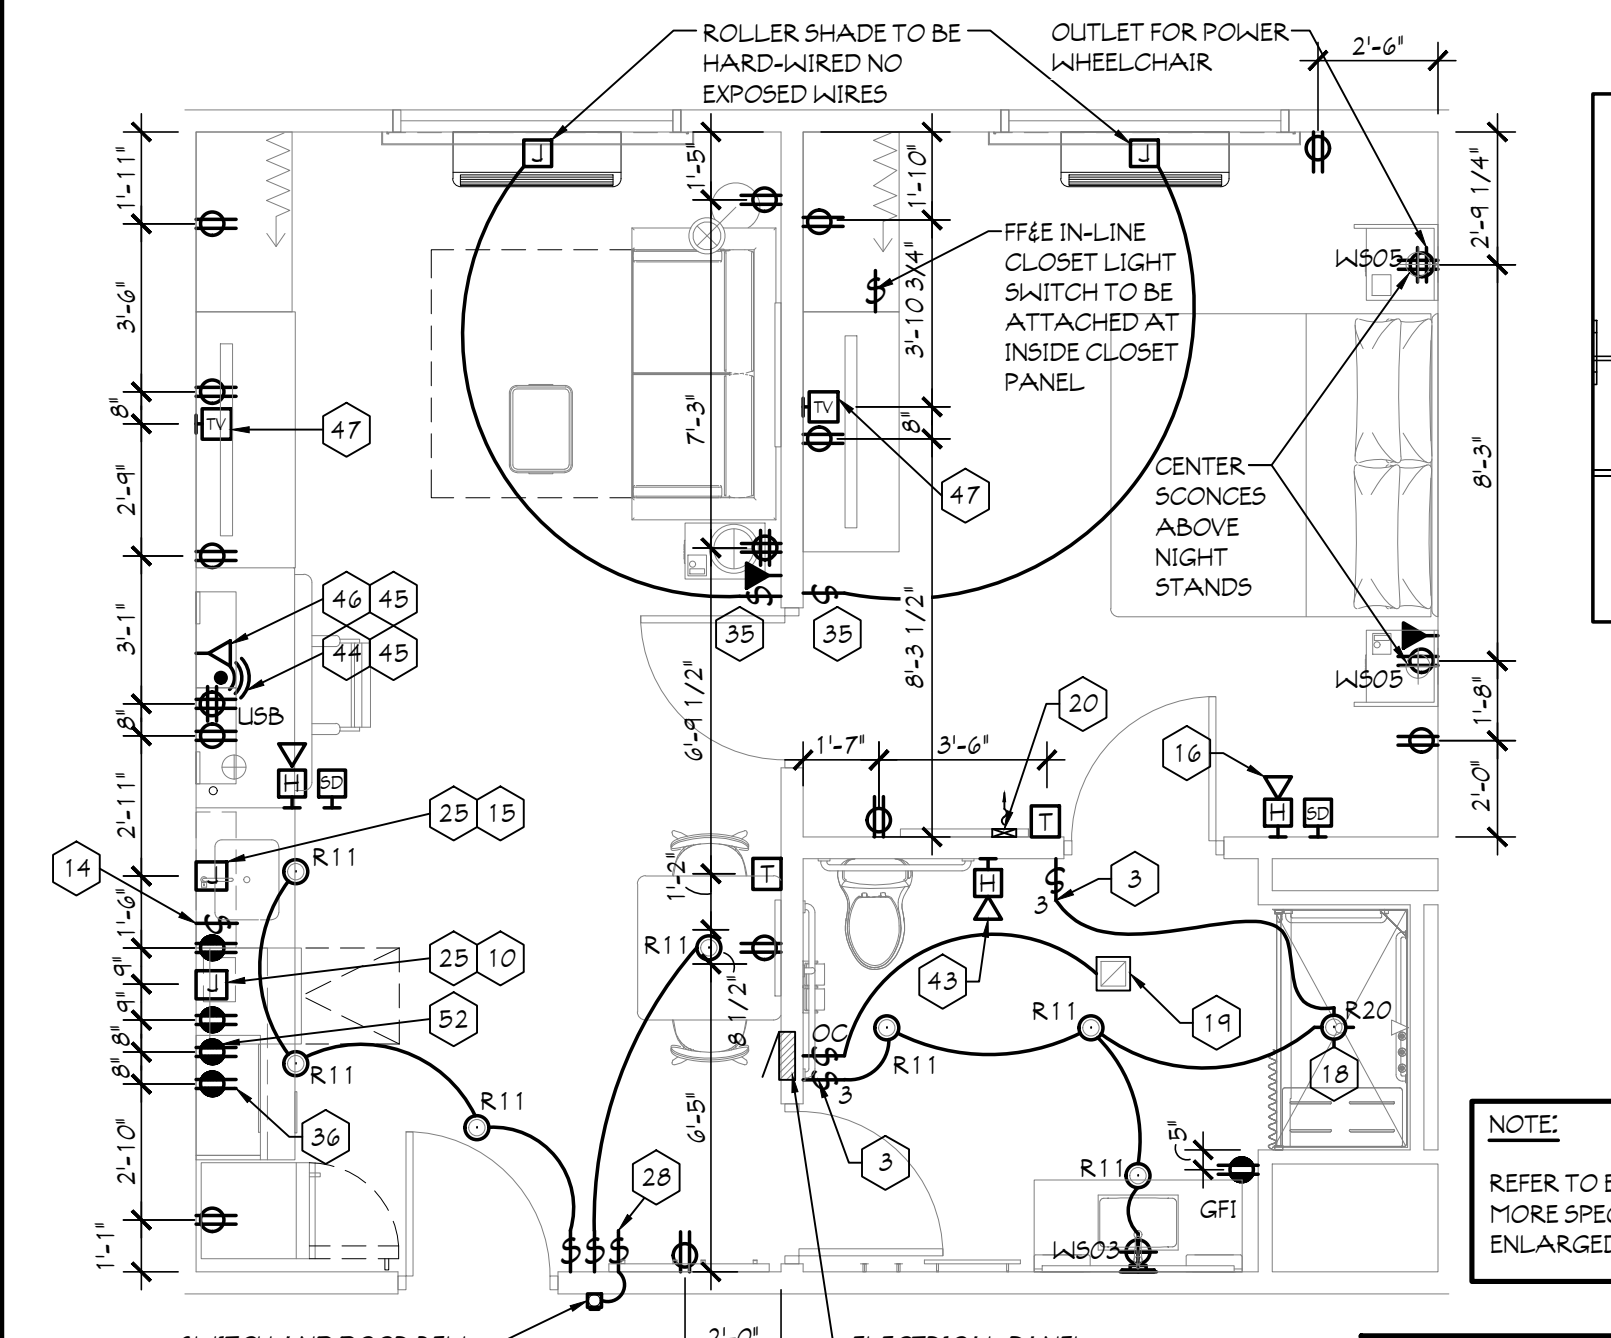


4 ACC. ONE BEDROOM ROLL-IN ELEC.
SCALE: 1/4" = 1'-0"

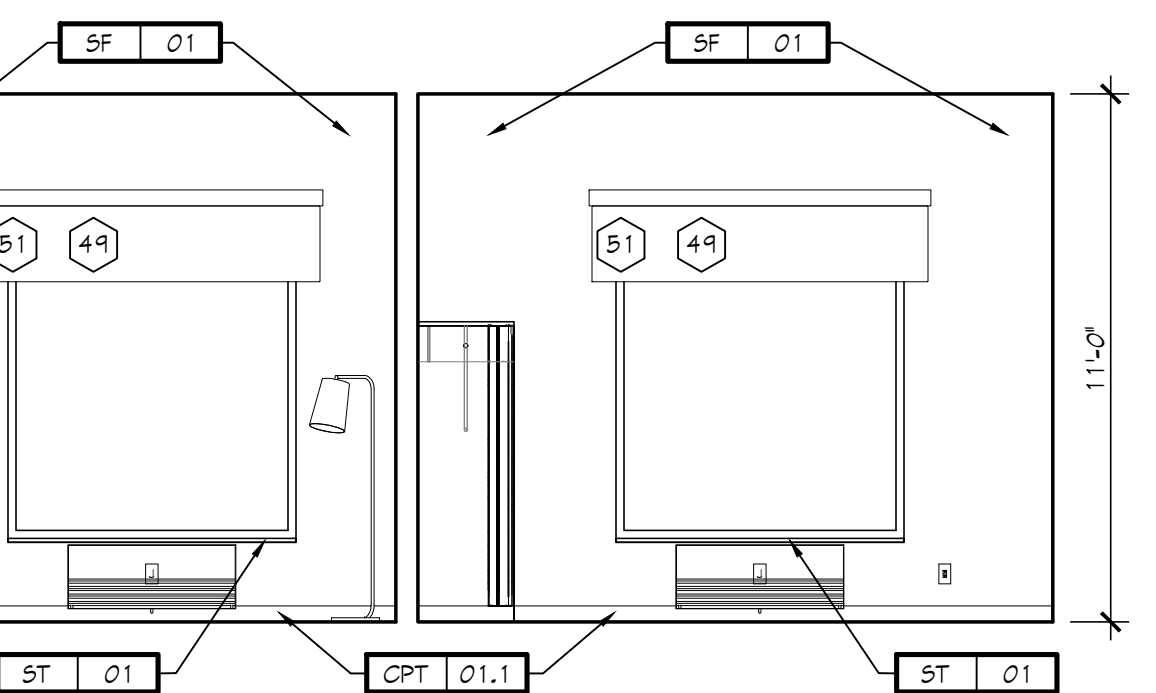


5 ROOM ELEVATION
SCALE: 1/4" = 1'-0"

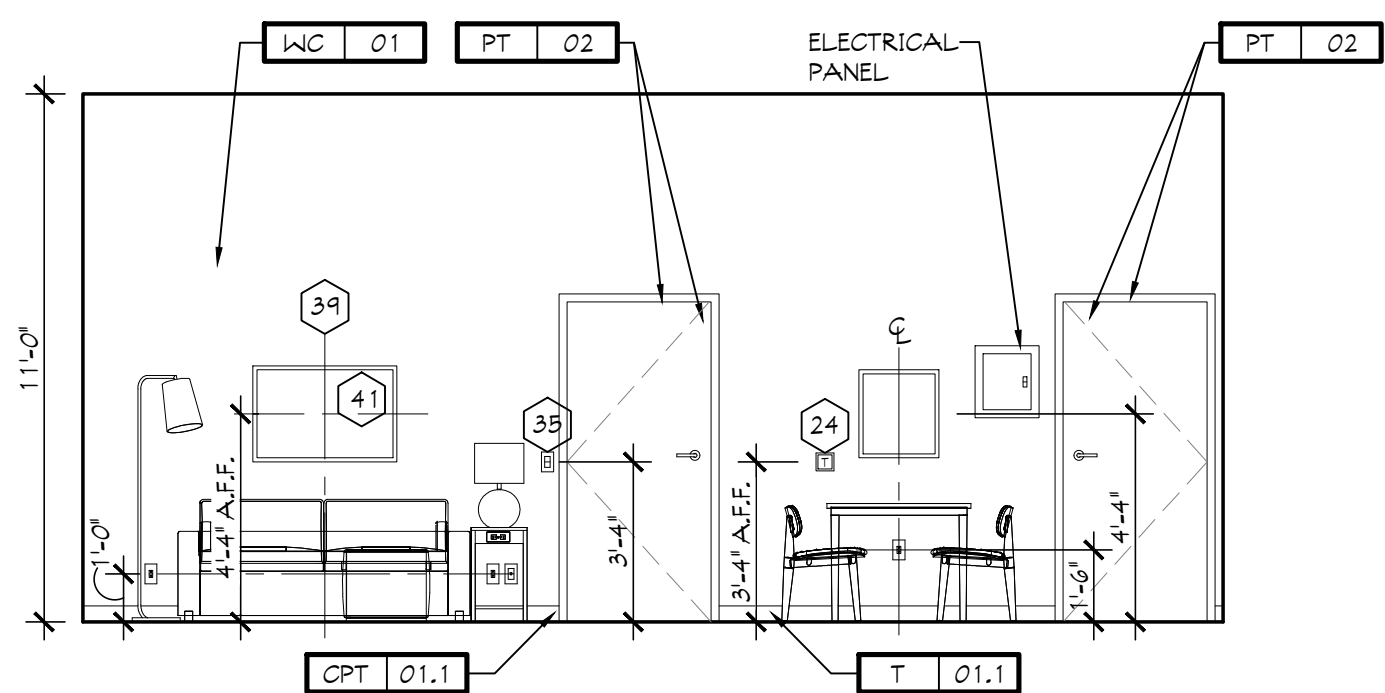


6 ROOM ELEVATION
SCALE: 1/4" = 1'-0"

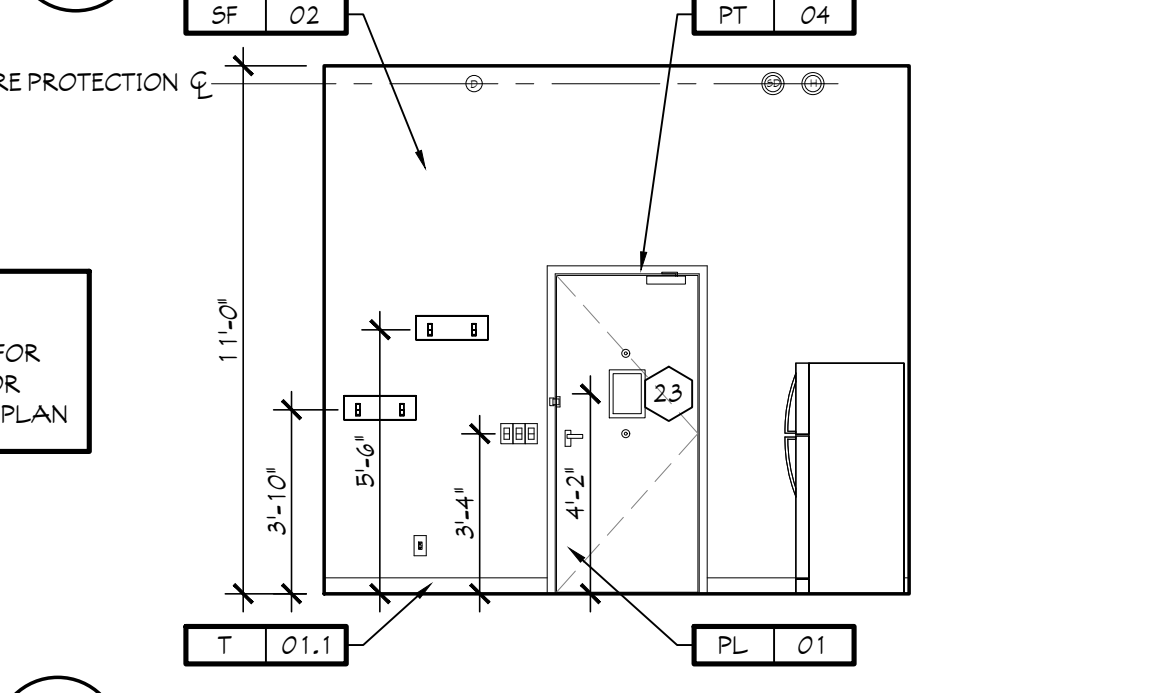


7 ROOM ELEVATION
SCALE: 1/4" = 1'-0"

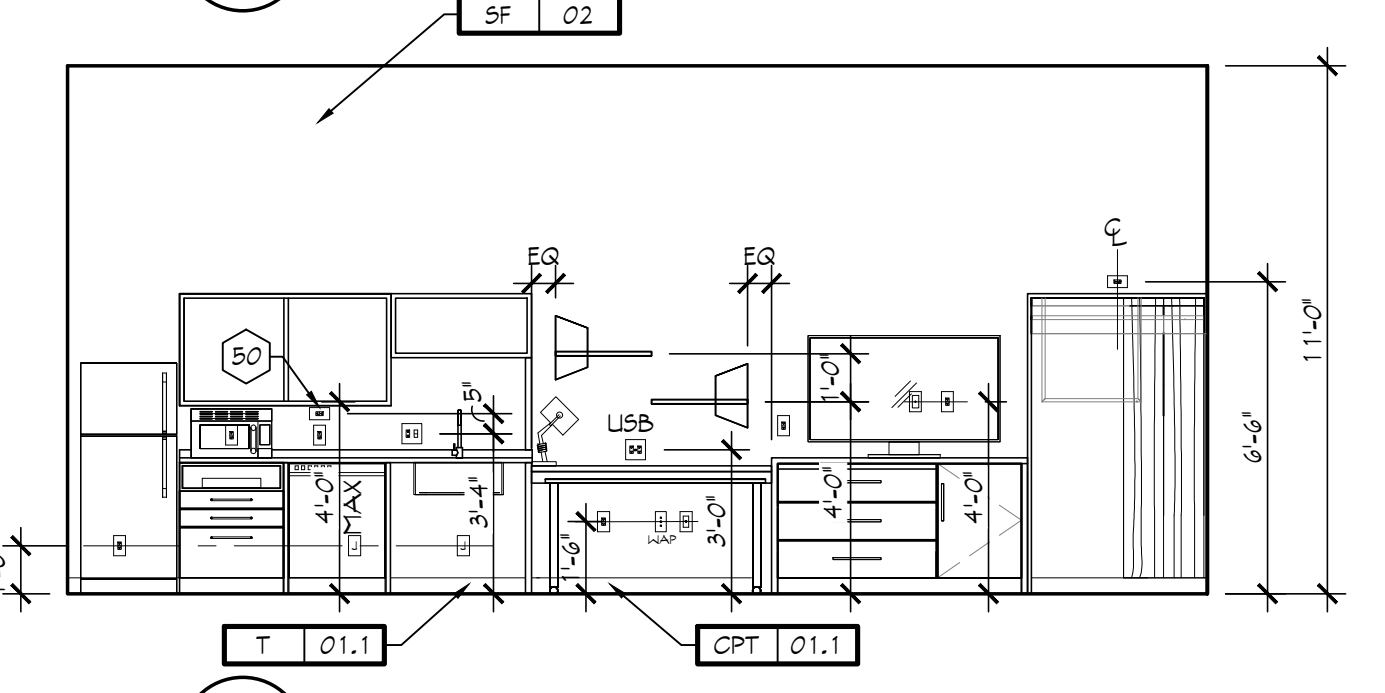


8 ROOM ELEVATION
SCALE: 1/4" = 1'-0"

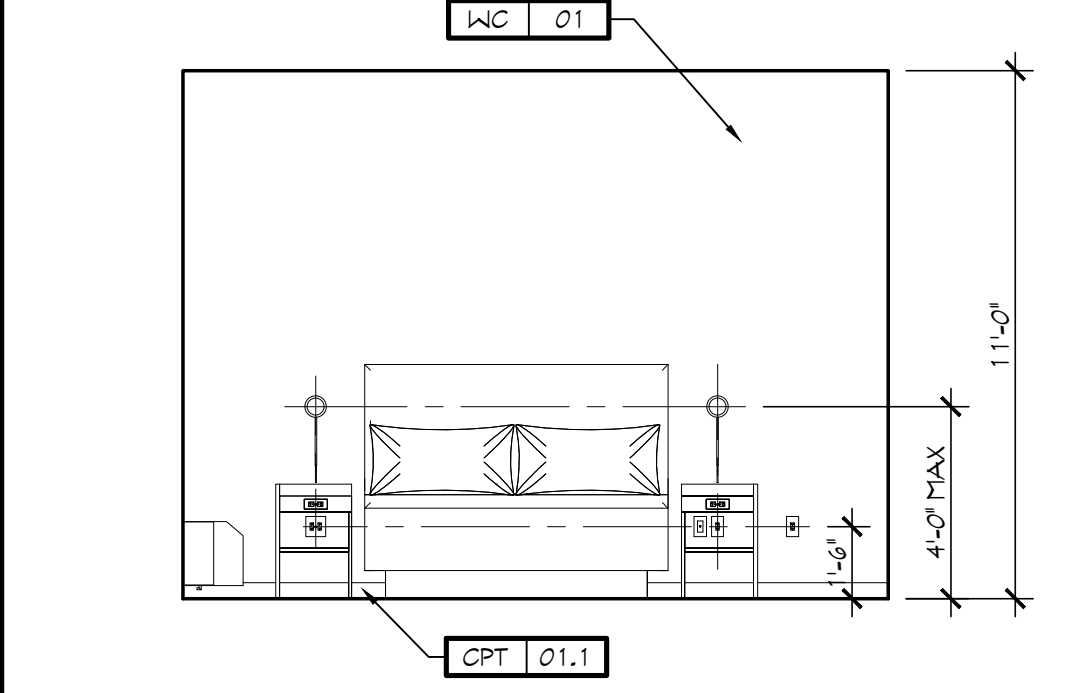

9 ROOM ELEVATION
SCALE: 1/4" = 1'-0"

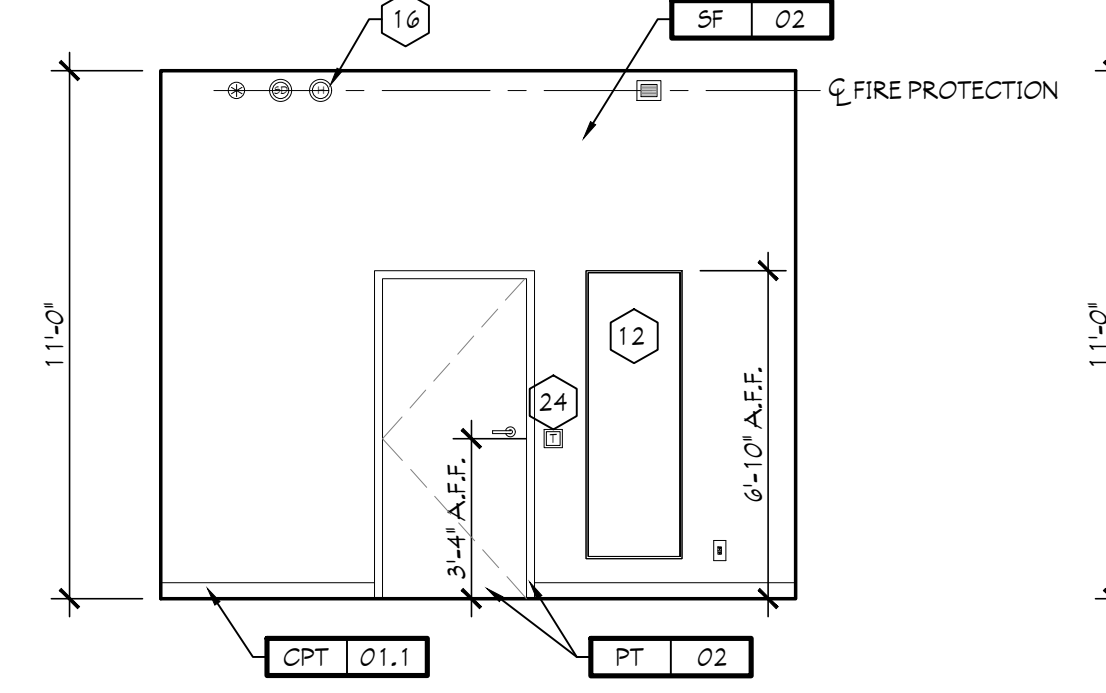

10 ROOM ELEVATION
SCALE: 1/4" = 1'-0"

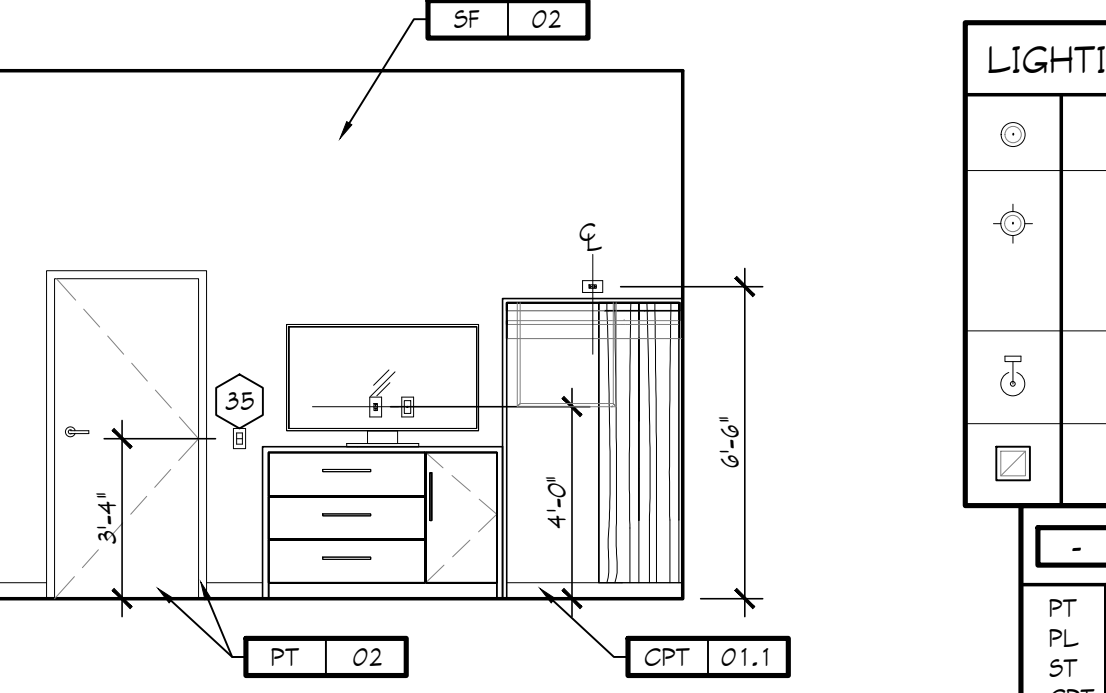

11 ROOM ELEVATION
SCALE: 1/4" = 1'-0"

LIGHTING AND CEILING LEGEND:

⊙	RECESSED DOWNLIGHT
⊙	RECESSED DOWNLIGHT W/ SHATTER PROOF LENS
⊙	DECORATIVE WALL SCONCE
⊙	BATHROOM EXHAUST

FINISH LEGEND:

PT	PAINT
ST	STONE
PL	PLASTIC LAMINATE
CPT	CARPET TILE
T	TILE
WC	WALLCOVERING

CEILING LEGEND:

A.	PRIMED AND PAINTED GYPSUM BOARD
B.	PRIMED AND PAINTED GYPSUM BOARD - MOISTURE RESISTANT

FURNISHINGS LEGEND:

GR-100	OTTOMAN @ SOFA
GR-101	SLEEPER SOFA
GR-102	DINING CHAIR @ ONE BEDROOM SUITE
GR-103	ERGONOMIC TASK CHAIR
GR-200	SIDE TABLE LAMP
GR-201	DESK LAMP
GR-202	NIGHTSTAND AND SCONCE
GR-203	VANITY SCONCE
GR-204	SCONCE @ WALL HOOKS
GR-205	FLOOR LAMP
GR-206	TABLE LAMP (ADA)
GR-207	NIGHTSTAND SCONCE (DO)
GR-208	NOT USED
GR-300	QUEEN HEADBOARD
GR-301	KING HEADBOARD
GR-302	VANITY
GR-303	ACCESSIBLE VANITY
GR-304-316	WORKING WALL
GR-317	DINING TABLE
GR-318	SOFA SIDE TABLE
GR-319	NIGHTSTAND @ RIGHT
GR-320	RIGHT DECORATIVE SHELF ABOVE DESK
GR-321	WALL SHELF @ BATHROOM
GR-322	DOUBLE QUEEN NIGHTSTAND
GR-323	NIGHTSTAND @ LEFT
GR-324	WALL SHELF @ ADA BATHROOM
GR-325	LEFT DECORATIVE SHELF ABOVE DESK
GR-400	BLACKOUT & SHEER ROLLER SHADE
GR-401	MOTORIZED ADA ROLLER SHADE
GR-402	DIVIDER DRAPERY
GR-402.1	DIVIDER DRAPERY - HARDWARE
GR-403	CLOSET DRAPERY
GR-404	CLOSET DRAPERY (ADA)
GR-405	DIVIDER DRAPERY (ADA)
GR-500	ARTWORK AT SLEEPER SOFA
GR-501	VANITY MIRROR
GR-502	FULL LENGTH MIRROR
GR-600	QUEEN MATTRESS SET
GR-600.1	QUEEN BEDDING
GR-601	KING MATTRESS SET
GR-601.1	KING BEDDING
GR-602	QUEEN BED BASE
GR-602.ADA	ACCESSIBLE QUEEN BED BASE
GR-603	ACCESSIBLE QUEEN BED SKIRT (ADA)
GR-603.ADA	KING BED BASE
GR-603.1	ACCESSIBLE KING BED SKIRT (ADA)
GR-603.ADA	KING ACCESSIBLE BED BASE
GR-603.1	ACCESSIBLE KING BED SKIRT (ADA)
GR-603.1	REFRIGERATOR
GR-603.1	DISHWASHER
GR-603.1	TELEVISION
GR-603.1	CLOCK/RADIO
GR-603.1	TELEPHONE

KEY NOTES:

1	PTAC UNIT
3	IN BATHROOM LOCATIONS ONLY, LIGHT SWITCH EQUIPPED WITH NIGHTLIGHT, MOUNTED 50 TOP OF SWITCH IS 48" MAX A.F.F.
4	MANUAL BLACK OUT ROLLER SHADE TO EXTEND 6" BEYOND WINDOW OPENING; SHEER ROLLER SHADE TO BE MOUNTED INSIDE WINDOW OPENING
5	SHOWER ENCLOSURE WITH TEMPERED GLASS DOOR
6	FLOOR DRAIN
7	PRE-MANUFACTURED SHOWER PAN
8	CEILING MOUNTED DRAPERY ROD - PROVIDE BLOCKING AS REQUIRED
9	ALTERNATE LOCATION OF DOOR FOR CONNECTING ROOMS TO ACCESSIBLE ROOMS - REFER TO OVERALL PLANS FOR LOCATION OF ACCESSIBLE ROOMS
10	DEDICATED CIRCUIT FOR DISHWASHER
11	RANGE TOP STYLE MICROWAVE AFFIXED TO WALL
12	MIRROR
13	BEGIN CARPET TILE THIS SIDE WITH FULL TILE - FIRST TWO ROWS OF TILE TO BE INSTALLED AROUND BUILT-IN CASEGOODS
14	SWITCH CONTROLLING GARBAGE DISPOSAL GANGED WITH DUPLEX REFER TO HADG FOR ACCESSIBLE ROOM REQUIREMENTS.
15	DEDICATED CIRCUIT FOR GARBAGE DISPOSAL
16	FIRE HORN IN STANDARD ROOMS. FIRE HORN/STROBE IN COMMUNICATION FEATURES ROOMS
17	LAYOUT AND CONSTRUCTION IS TO START AT REFRIGERATOR HOLD DIM. & PROCEED UP THE WALL FROM THAT END-FINAL INSTALLATION IS ROD AT CLOSET, BE SCRIBED AT WALL AS REQUIRED. END OF KITCHEN MUST TERMINATE AT OUTSIDE FACE OF BATHROOM WALL.
18	RECESSED CEILING LIGHT FOR WET LOCATIONS WITH SHATTER PROOF LENS
19	TOILET EXHAUST GRILLE
20	MAKE-UP AIR DIFFUSER
21	EXTENT OF SLEEPER SOFA
22	APPROXIMATE LOCATIONS OF MILLWORK SUPPORTS ON FLOOR. PROVIDE SHIMS OR LEVELERS UNDER SUPPORTS TO PREVENT CARPET CRUSHING
23	ROOM SIGNAGE
24	HARD WIRED THERMOSTAT FOR PTAC, MOUNTED 48" MAX TO TOP OF DEVICE. COMMUNICATION BETWEEN THERMOSTAT AND PTAC MAY BE WIRELESS.
25	EXTEND J-BOX, DEVICE AND COVER PLATE FLUSH WITH MILLWORK BACK PANEL
26	DROPPED GYPSUM BOARD BULKHEAD @ ROUGH OPENING - WHERE PRE-MANUFACTURED SHOWER INSERT IS INDICATED MEASURE ROUGH OPENING FROM FACE OF GYPSUM BOARD
28	DOORBELL ON/OFF SWITCH (COMMUNICATION FEATURES ROOMS ONLY) SIGNAGE AS REQ'D.
30	EDGE OF PTAC ABOVE CARPET TILES
31	MIN. CEILING HEIGHT MUST BE MAINTAINED - REFER TO HOME 2 SUITES BY HILTON STANDARDS MANUAL
32	FRAMING SUBCONTRACTOR TO PROVIDE 3/4" F.R.T. PLYWOOD BLOCKING TO RECEIVE ITEM INDICATED - EXTEND FULL LENGTH OF OBJECT
33	GENERAL CONTRACTOR TO COORDINATE WITH FURNITURE FABRICATOR WHERE NECESSARY TO PROVIDE PROPER BLOCKING IN WALL FOR ITEM KEYNOTED
34	BI-PASS SLIDING GLASS DOOR, BRUSHED ALUMINUM FINISH, CLEAR GLASS, WITH 24" BAR PULL HARDWARE
35	SWITCHES CONTROLLING MECHANICAL SHADES - REFER TO FFE MANUAL
36	OUTLET ABOVE FOR MICROWAVE - REFER TO ROOM ELEVATION MOUNT DEVICE HORIZONTALLY - FACE PLATE TO BE WHITE
37	REQUIRED ACCESSIBLE CLEAR FLOOR AREA DESIGNATION
39	CENTER ARTWORK OVER SOFA
40	COUNTERTOP MICROWAVE
41	GRAPHIC ART REFER TO ACCESSORIES LEGEND AND CONSTRUCTION PLAN
42	ACCESSIBLE VANITY; CLEAR AREA OF SINK/VANITY MUST BE ACCESSIBLE
43	ADDITIONAL HORN STROBE; LOCATED IN C.F. BATHROOMS ONLY
44	WAP IN 3-GANG BOX MOUNTED VERTICALLY UNDER DESK; MAINTAIN 6" BETWEEN ALL BOXES, TYP. ALL GUESTROOMS. COORDINATE WALL LOCATION WITH CASEGOODS TO AVOID CONFLICTS. VISIT CONNECTED ROOM HILTON.COM FOR CURRENT WIRELESS INTERNET REQ'S AND LIST OF APPROVED INTEGRATORS.
45	EACH CABLE MUST HOMERUN BETWEEN THE GUESTROOM AND THE IDF ON EACH FLOOR. VISIT CONNECTED ROOM HILTON.COM FOR CURRENT REQUIREMENTS AND OPTIONS.
46	OPTION WIRELESS DATA CONNECTION FOR GUEST USE: A) ADD CAT6 RJ-45 CABLE BEHIND TV. CAT6 RJ-45 JACK BEHIND TV, RUN IN 5/8" RFT TUBE IN WALL TO WAP UNDER DESK. PATCH CORD TO EDGE CONTROLLER FOR CONNECTED ROOM. MIN. 6" CLEARANCE FROM WALL BOXES - OR - B) SMART TV-INTERNET PROTOCOL TELEVISION COAX NOT REQ'D. CAT6 RJ-45 JACK BEHIND TV RUN IN 5/8" RFT TUBE IN WALL TO WAP UNDER DESK. PATCH CORD TO EDGE CONTROLLER FOR CONNECTED ROOM. CAT6 RJ-45 JACK BEHIND TV IN ONE-BEDROOM TV, MIN. 6" CLEARANCE FROM WALL BOXES. VISIT HILTONHDTV.COM FOR ADDITIONAL INFORMATION.
48	PROVIDE HINGE STOP AT DOOR
49	HARDWIRED BLACK OUT ROLLER SHADE WITH NO EXPOSED WIRES
50	PROVIDE OUTLET FOR UNDER CABINET LIGHTING BY OTHERS, COORDINATE WITH ELECTRICAL AT ACC. GUESTROOMS; THE COOK LIGHT AT MOUNTED MICROWAVE FOR NON-ACC ROOMS WILL SUFFICE
51	ROLLER SHADE TO EXTEND PAST WINDOW FRAME TO REDUCE LIGHT LEAKAGE - REFER TO SPECIFICATION AND MANUFACTURER'S INSTALLATION REQUIREMENTS
52	DEDICATED CIRCUIT FOR INDUCTION BURNER

GENERAL NOTES:

ALTHOUGH DRAWINGS ARE PREPARED TO SCALE, THE ACCURACY OF THE DRAWINGS CANNOT BE GUARANTEED. DIMENSIONS SHALL BE DELETED OF REPRODUCTION. DIMENSIONS SHALL BE DELETED OF REPRODUCTION. DIMENSIONS SHALL BE DELETED OF REPRODUCTION.

ALL DIMENSIONS UNLESS OTHERWISE NOTED SHALL BE IN FEET AND INCHES. DIMENSIONS SHALL BE IN FEET AND INCHES. DIMENSIONS SHALL BE IN FEET AND INCHES.

GENERAL CONTRACTOR SHALL BE RESPONSIBLE FOR THE VERIFICATION OF ALL DIMENSIONS AND CONDITIONS PRIOR TO CONSTRUCTION.

MAUIST ARCHITECTURAL SERVICES, INC.
112 NORTH MAIN STREET
GOSHEN, INDIANA 46526
PHONE: (574) 537-8500
FAX: (574) 537-0808

HOME 2 SUITES BY HILTON

FT. WAYNE, INDIANA

REVISIONS:

DATE:	05/01/26
JOB NO.:	MA5-26-105
NAME:	ACCESSIBLE ONE BEDROOM STUDIO ROLL-IN SHEET

A507