



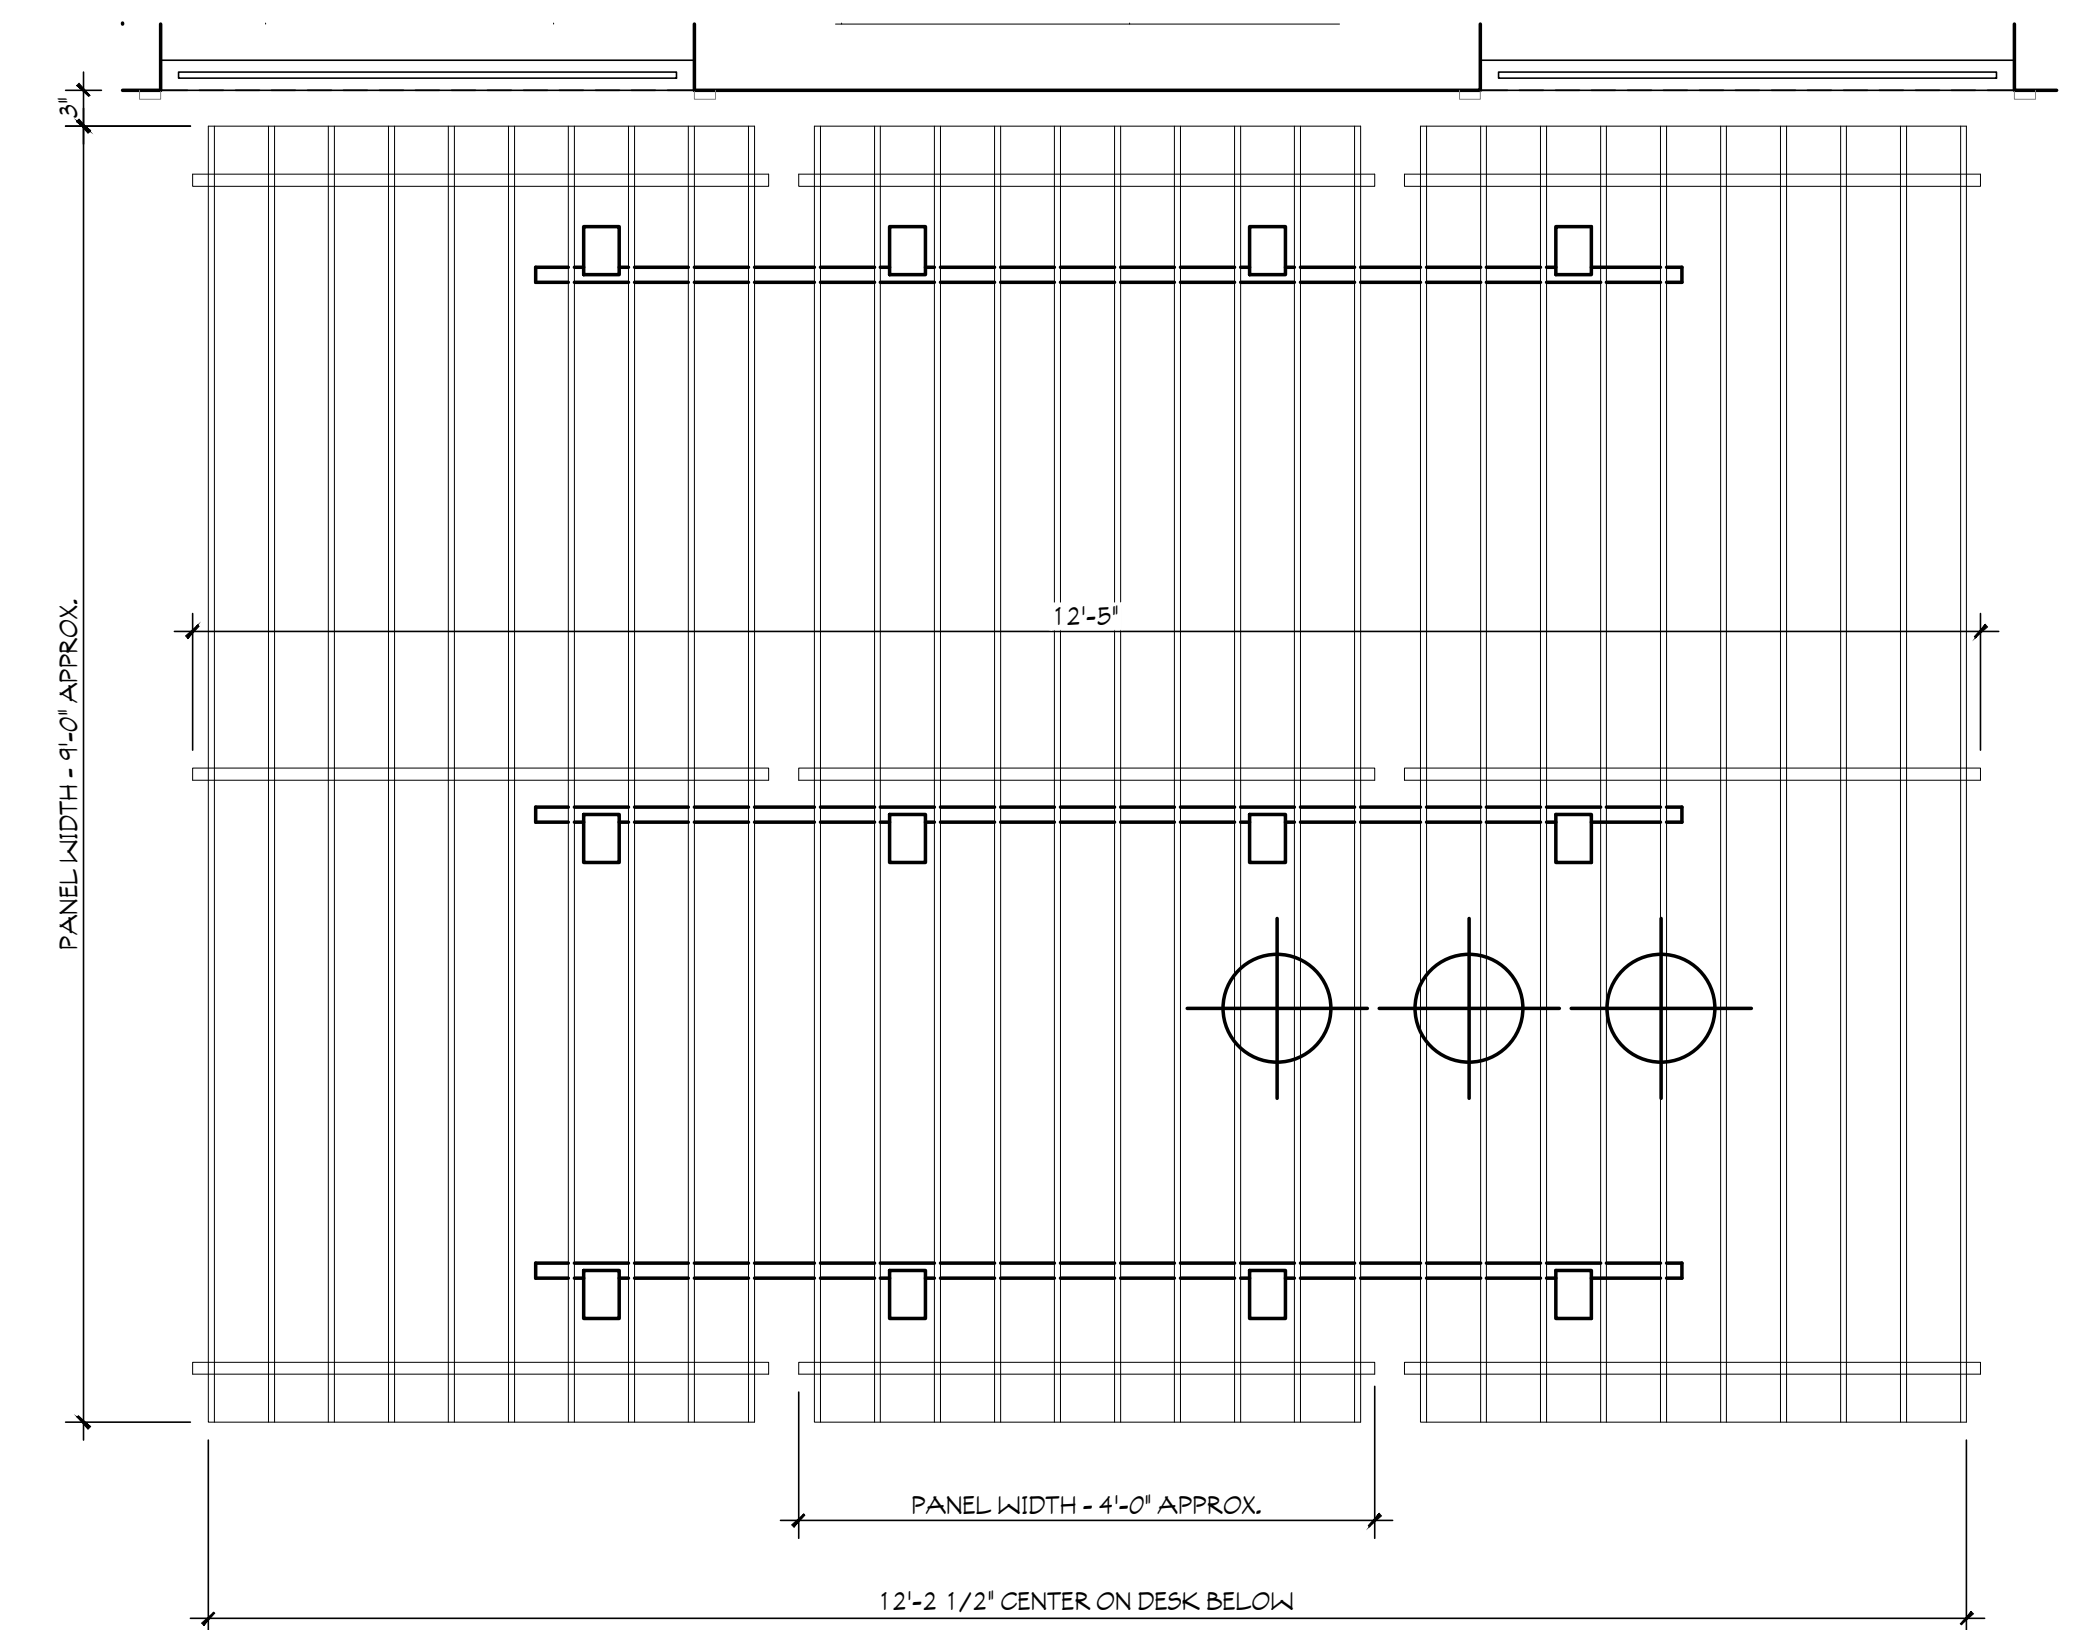

1 RCP - RECEPTION BAFFLE CEILING
SCALE: 3/4" = 1'-0"

5 ELEVATION - RECEPTION
SCALE: 3/4" = 1'-0"

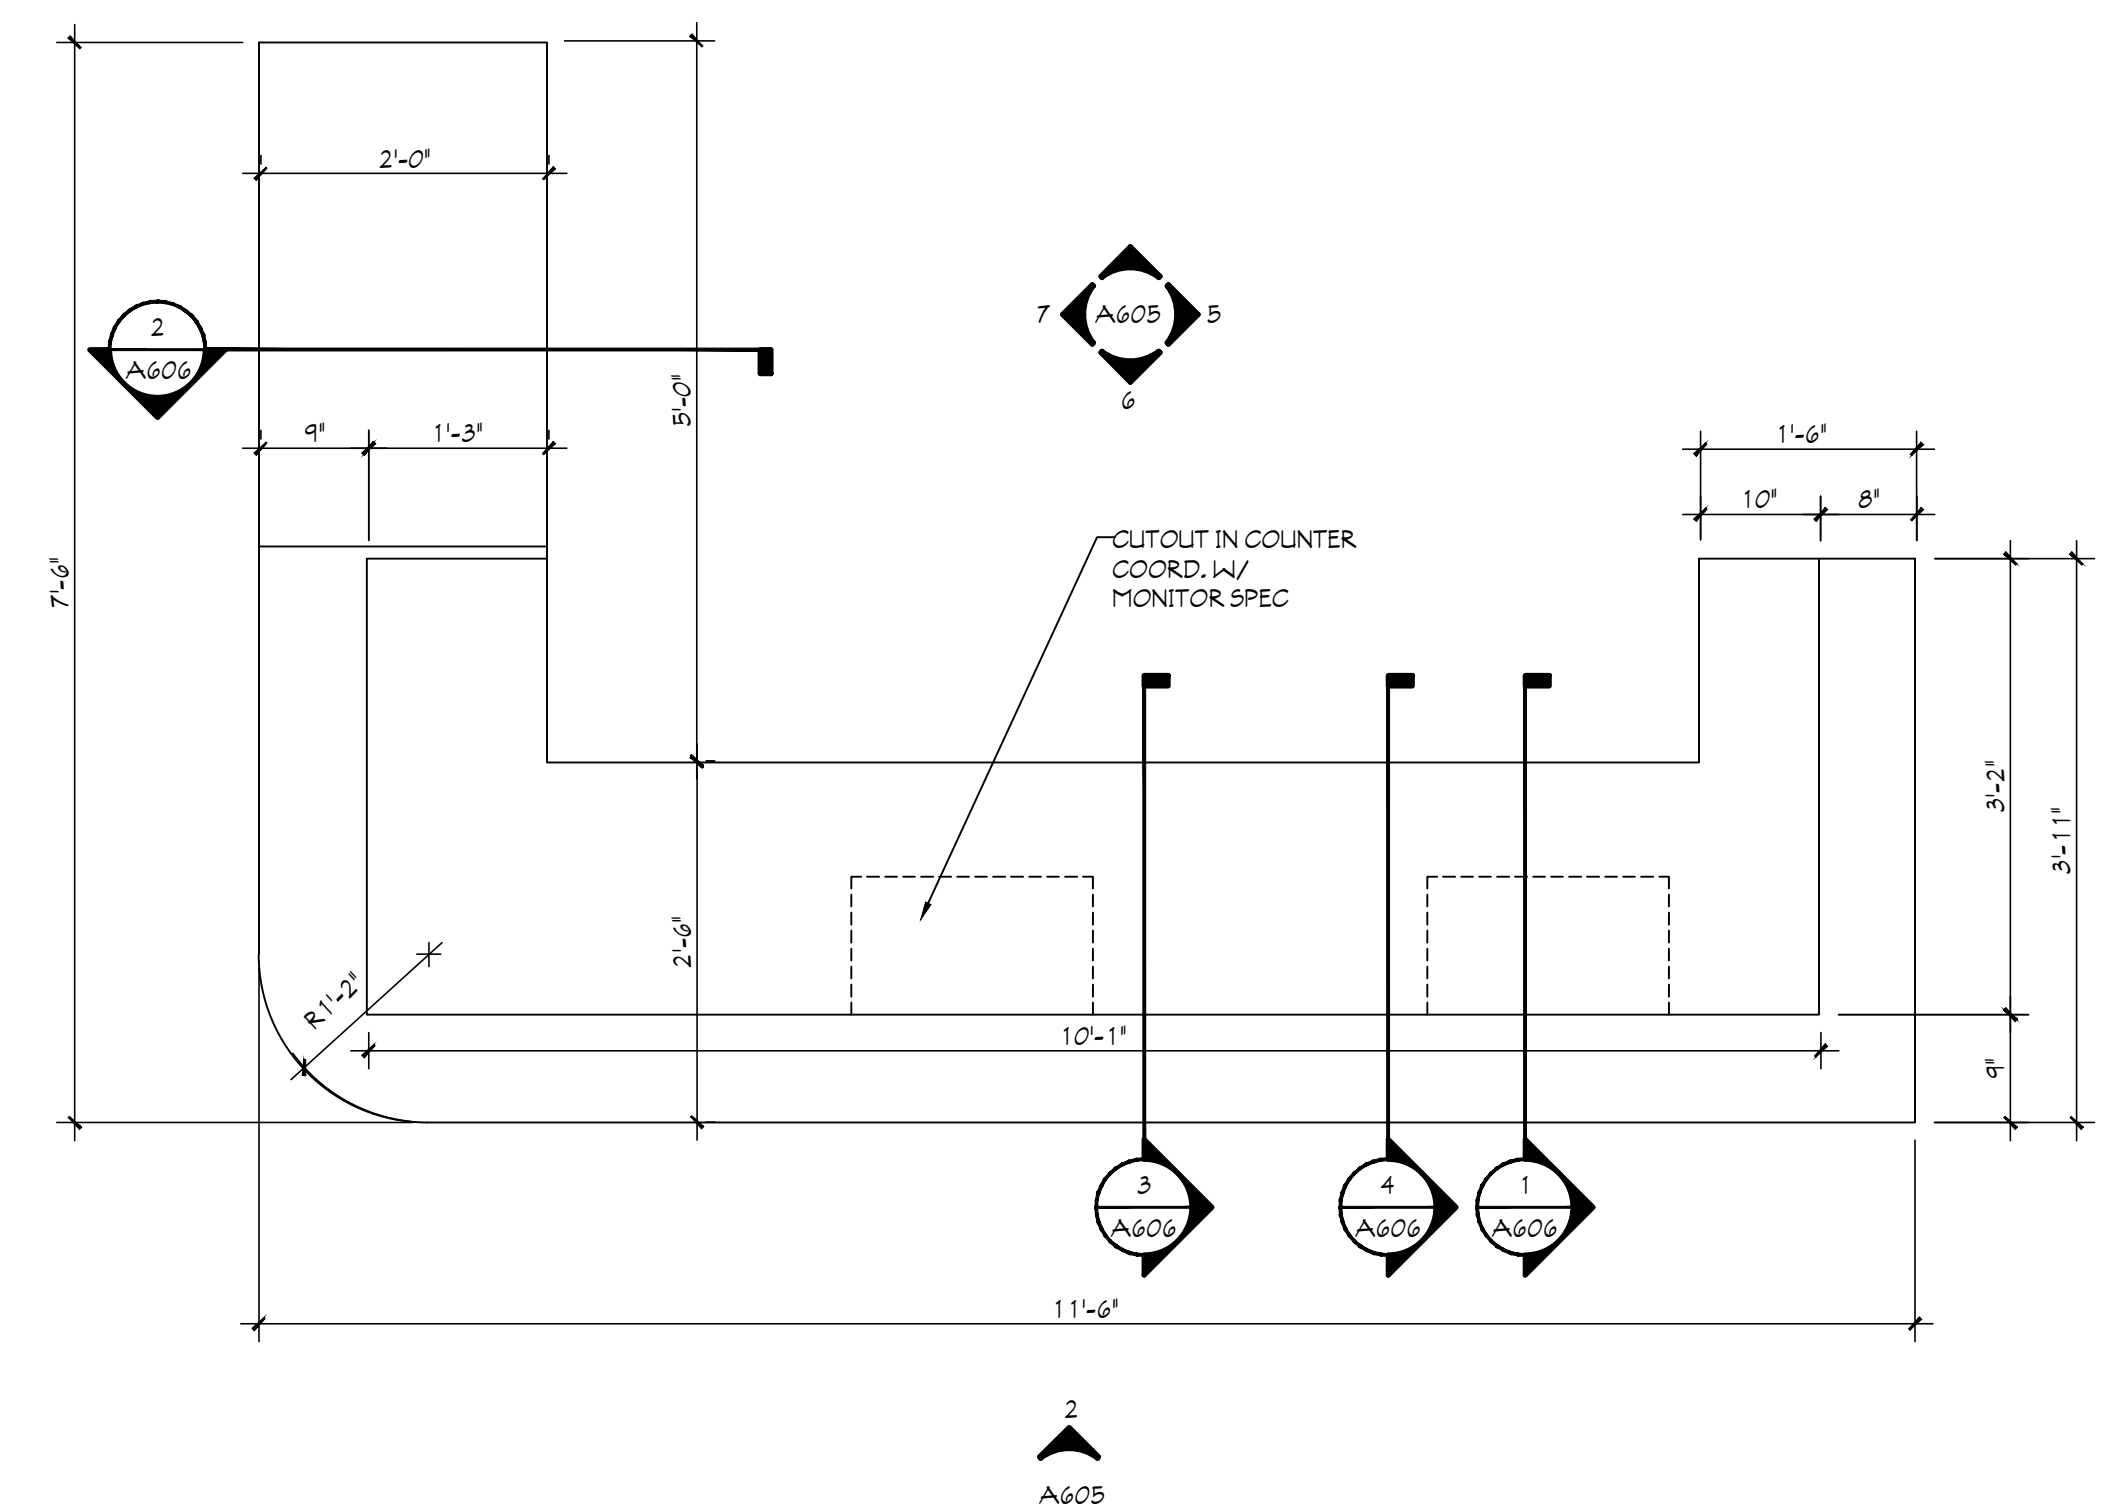

7 ELEVATION - RECEPTION
SCALE: 3/4" = 1'-0"

SHEET:

A605