



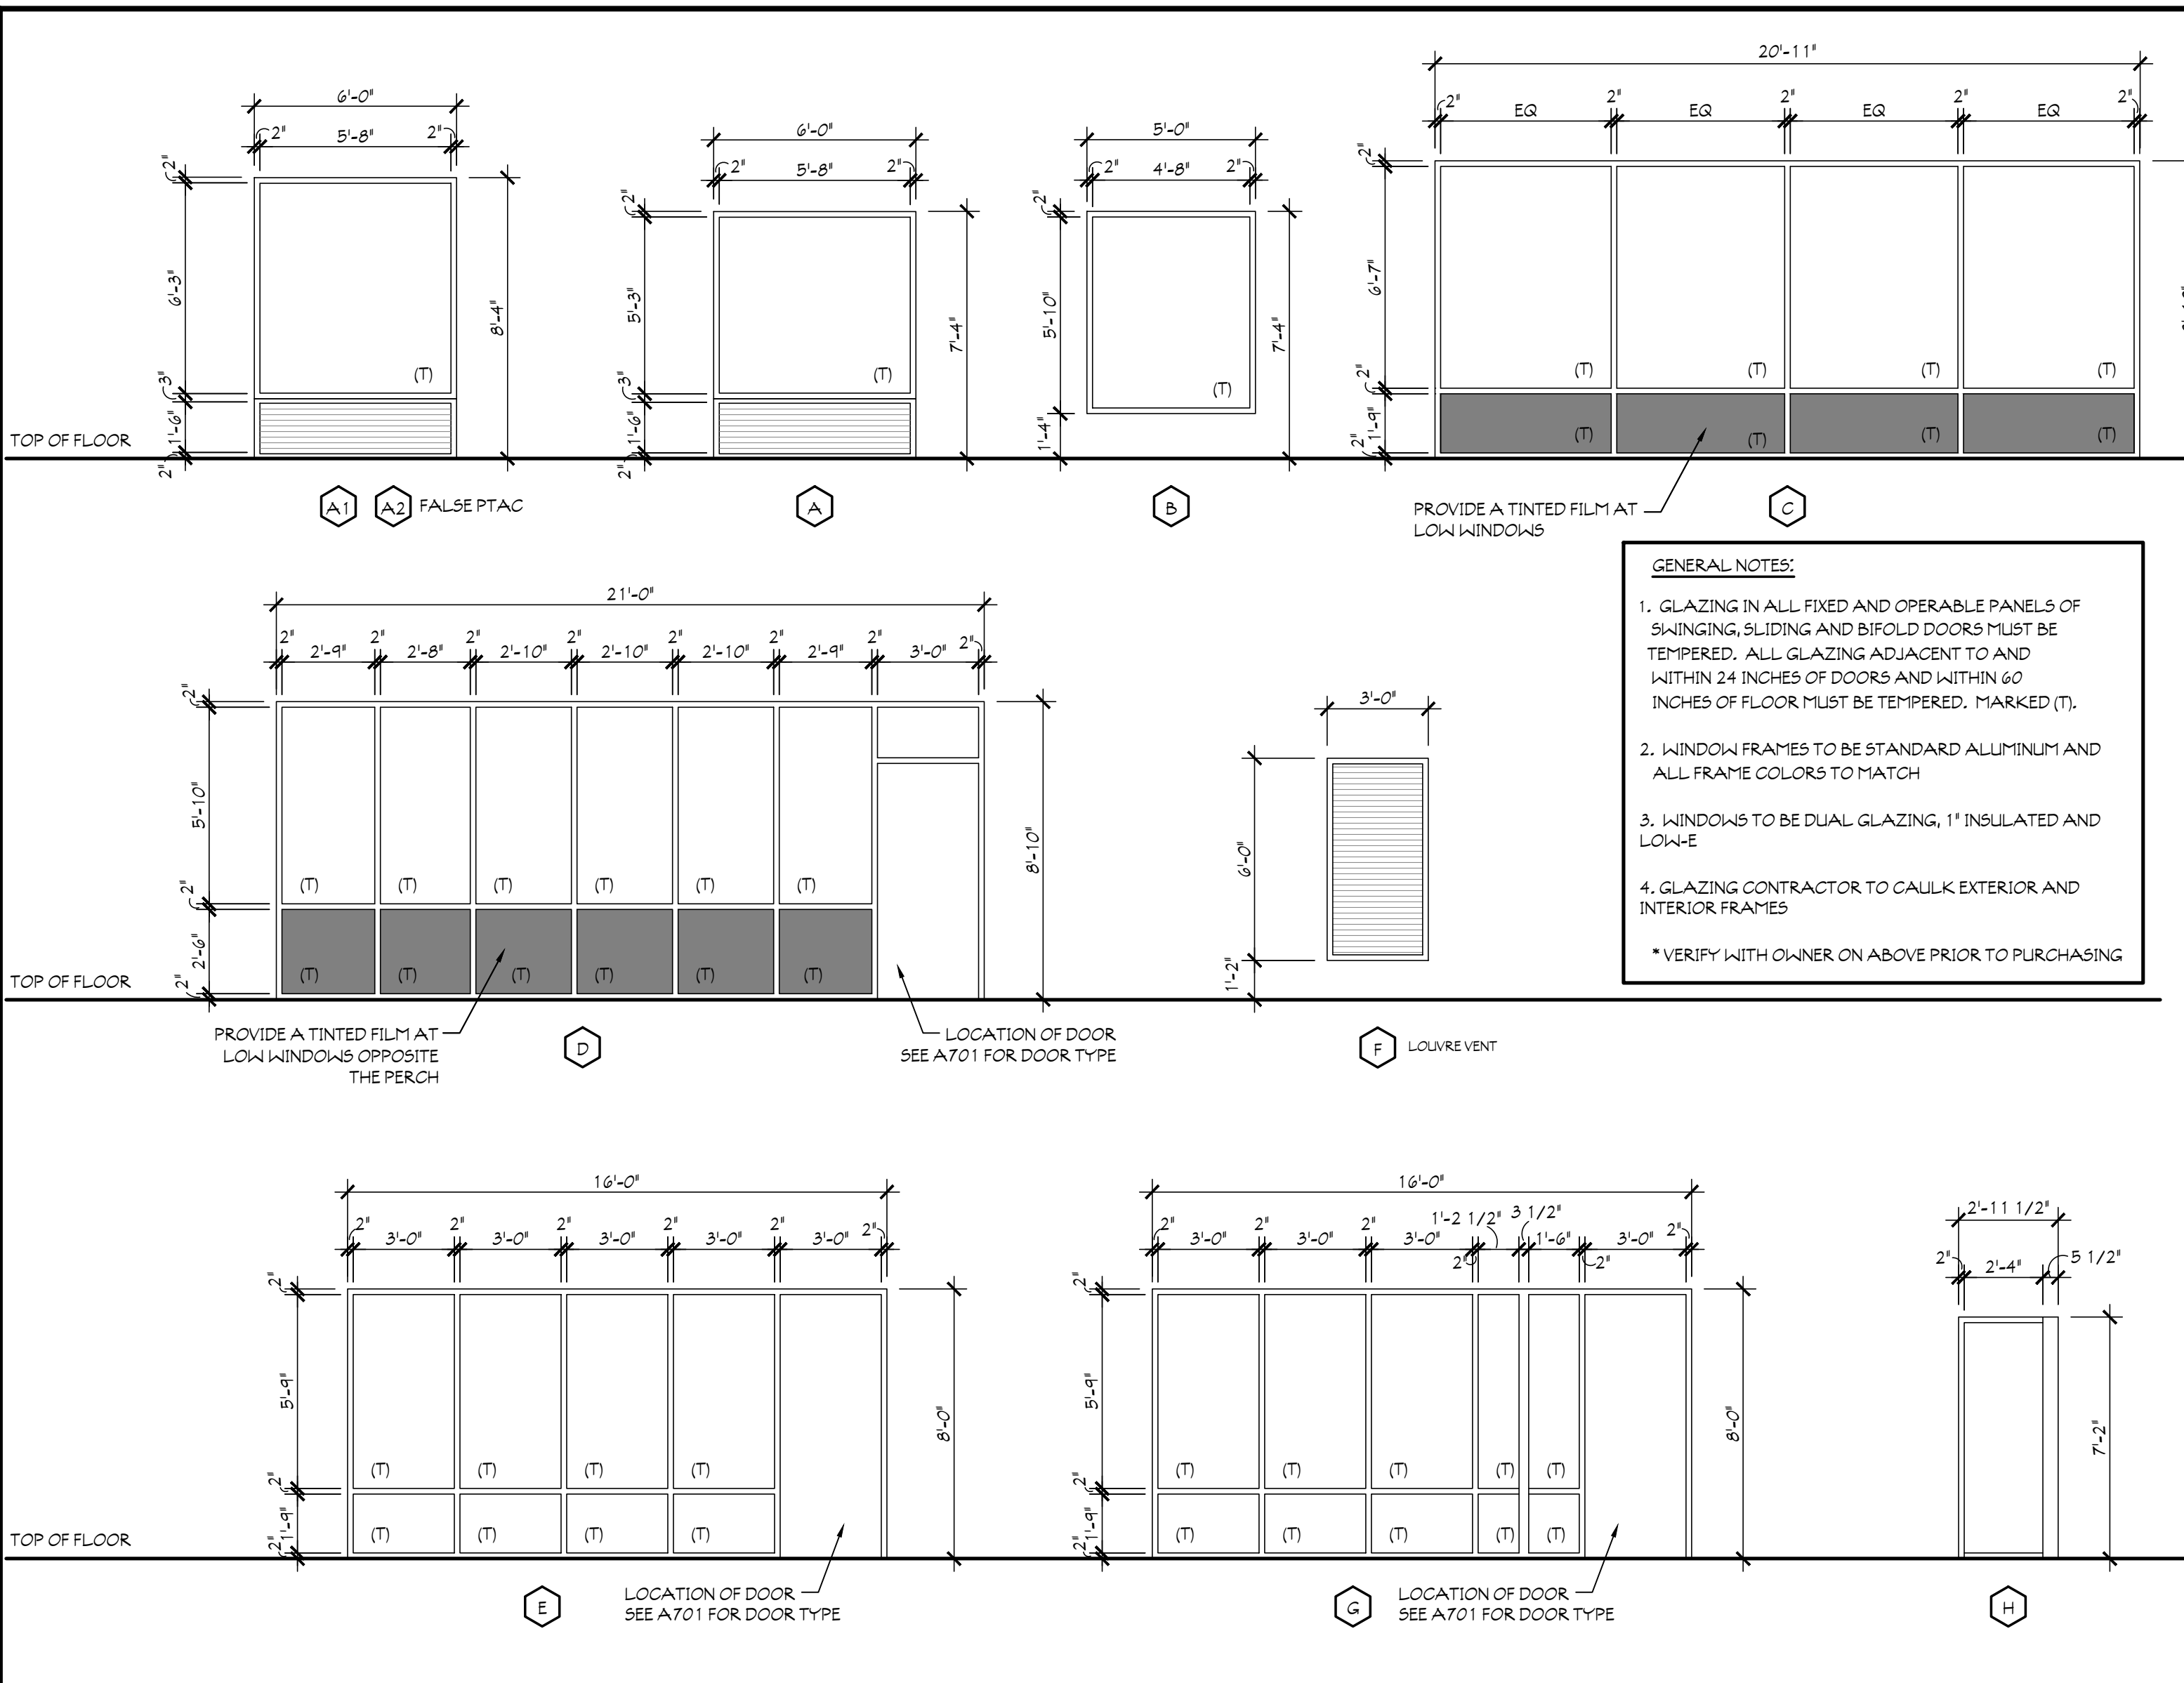

ROOM FINISH SCHEDULE														
ROOM		FLOOR		WALLS DIRECTIONS ARE PLAN NORTH)								CEILING		REMARKS
				NORTH		EAST		WEST		SOUTH				
NO.	NAME	FLOOR	BASE	MATL	FINISH	MATL	FINISH	MATL	FINISH	MATL	FINISH	MATL	FINISH	
GUESTROOMS														
--	ENTRY	T	T	GNB	SF/WC	GNB	SF/WC	GNB	SF/WC	GNB	SF/WC	SGB	PTD	SEE NOTE #2 & 3; WALL MATERIAL VARIES
--	LIVING AREA	CPT	CB	GNB	SF/WC	GNB	SF/WC	GNB	SF/WC	GNB	SF/WC	SGB	PTD	SEE NOTE #2 & 3; WALL MATERIAL VARIES
--	BEDROOM	CPT	CB	GNB	SF/WC	GNB	SF/WC	GNB	SF/WC	GNB	SF/WC	SGB	PTD	SEE NOTE #2 & 3; WALL MATERIAL VARIES
--	BATH	T	T	GNB	WC	GNB	WC	GNB	WC	GNB	WC	SGB	AK	SEE NOTE #2 & 3
FIRST FLOOR														
101	STAIR #1	CT/CPT	CT/ CB	GNB	PTD	GNB	PTD	GNB	PTD	GNB	PTD	GNB	PTD	RUBBER NOSING; SEE NOTE #1
104A	STORAGE	QT/ 5C	QT	GNB	FRP	GNB	FRP	GNB	FRP	GNB	FRP	SACT	--	SC UNDER WALK IN UNITS
104B	STORAGE	SC	VB	GNB	PTD	GNB	PTD	GNB	PTD	GNB	PTD	GNB	PTD	--
104C	ICE	CT	CT	GNB	WC	GNB	WC	GNB	WC	GNB	WC	SGB	PTD	--
106A	FOOD PREP	QT	QT	GNB	FRP	GNB	FRP	GNB	FRP	GNB	FRP	SACT	--	FRP FULL HEIGHT
106B	EMPLOYEE BREAK ROOM	RF	VB	GNB	WC	GNB	WC	GNB	WC	GNB	WC	SACT	--	--
107A	STORAGE	SC	VB	GNB	PTD	GNB	PTD	GNB	PTD	GNB	PTD	GNB	PTD	--
107B	MEETING ROOM	CPT	CB	GNB	WC	GNB	WC	GNB	WC	GNB	WC	SACT/SGB	--/PTD	SEE NOTE #3 & #4
108A	BREAKFAST	CT	CT	GNB	WC	GNB	WC	GNB	WC	GNB	WC	SGB	PTD	SEE NOTE #3 & 4
108B	SERVERY	CT	CT	GNB	WC	GNB	WC	GNB	WC	GNB	WC	SGB	PTD	SEE NOTE #3 & 4
108C	POOL EQUIPMENT	SC	VB	DG	PTD/SDE	DG	PTD/SDE	DG	PTD/SDE	DG	PTD/SDE	DG	SDE	--
108D	DRYERS	SC	VB	GNB	PTD	GNB	PTD	GNB	PTD	GNB	PTD	GNB	PTD	--
109A	WOMEN	CT	CT	GNB	CT	GNB	WC	GNB	WC	GNB	WC	SGB	PTD	SEE NOTE #4
109B	MEN	CT	CT	GNB	CT	GNB	WC	GNB	WC	GNB	WC	SGB	PTD	SEE NOTE #4
109C	MECHANICAL	SC	VB	GNB	PTD	GNB	PTD	GNB	PTD	GNB	PTD	GNB	PTD	--
109D	SALES	CPT	CB	GNB	PTD	GNB	PTD	GNB	PTD	GNB	PTD	SACT	--	--
110	LAUNDRY	SC	VB	FRP/PTD	GNB	PTD	GNB	PTD	GNB	FRP/PTD	SACT	--	FRP TO 4'-0" A.F.F. NOTE 1 & 4	
112A	MARKET	CT	CT	GNB	WC	--	--	GNB	WC	--	--	PTD	SEE NOTE #3	
112B	WORK STATIONS	CT	CT	GNB	WC	GNB	WC	GNB	WC	GNB	WC	SGB	PTD	SEE NOTE #4
112C	STORAGE	SC	VB	GNB	PTD	GNB	PTD	GNB	PTD	GNB	PTD	GNB	PTD	--
112D	POOL	PT	PT	DG	PTD/SDE	DG	PTD/SDE	DG	PTD/SDE	DG	TILE/PTD	DG	SDE	SEE NOTE #3 & 4
113	LOBBY	CT/ CPT	CT	GNB	WC	GNB	WC	GNB	WC	GNB	WC	SACT/SGB	--/PTD	SEE NOTE #1, 3 & 4
114A	REGISTRATION	CT	CT	GNB	WIP/WC/G	GNB	WC	GNB	WC	--	--	ACB/SGB	--/PTD	SEE NOTE #1, 3 & 4
114B	MANAGER	CPT	CB	GNB	PTD	GNB	PTD	GNB	PTD	GNB	PTD/G	SACT	--	--
114C	LAUNDRY DISCHARGE	SC	VB	GNB	PTD	GNB	PTD	GNB	PTD	GNB	PTD	SACT	--	--
114D	CLOSET	VCT	VB	GNB	PTD	GNB	PTD	GNB	PTD	GNB	PTD	GNB	PTD	--
114E	POOL VESTIBULE	PT	PT	GNB	PTD	GNB	PTD	GNB	PTD	GNB	PTD	SGB	PTD	--
114F	STORAGE	SC	VB	GNB	PTD	GNB	PTD	GNB	PTD	GNB	PTD	GNB	PTD	--
115	VESTIBULE	CT	CT	GNB	WC	GNB	WC	GNB	WC	GNB	WC	SGB	PTD	WALK-OFF MATT
116	ELEVATOR LOBBY	CT	CT	GNB	WC	GNB	WC	GNB	WC	--	--	SGB	PTD	SEE ELEVATION FOR FEATURE WALL
117	TV LOUNGE	CPT	CB	--	--	GNB	WC	GNB	WC	GNB	WC	SGB	PTD	--
118A	UNISEX	CT	CT	GNB	WC	GNB	WC	GNB	WC	GNB	WC	CT	SGB	PTD
118B	ELECTRICAL	SC	VB	GNB	PTD	GNB	PTD	GNB	PTD	GNB	PTD	GNB	PTD	--
118C	OUTDOOR STORAGE	SC	VB	GNB	PTD	GNB	PTD	GNB	PTD	GNB	PTD	GNB	PTD	--
118D	STORAGE	SC	VB	GNB	PTD	GNB	PTD	GNB	PTD	GNB	PTD	SGB	PTD	--
118E	PBX	VCT	VB	GNB	PTD	GNB	PTD	GNB	PTD	GNB	PTD	GNB	PTD	--
119A	FITNESS	RF	VB	GNB	WC	GNB	WC	GNB	WC	GNB	WC	TECTUP/SGB	--/PTD	SEE NOTE #1, 3, 4 & 5
119B	GUEST LAUNDRY	CT	CT	GNB	WC	GNB	SF	GNB	WC	GNB	WC	SGB	PTD	--
120A	MAINTENANCE STORAGE	VCT	VB	GNB	PTD	GNB	PTD	GNB	PTD	GNB	PTD	GNB	PTD	--
120B	WATER	SC	VB	GNB	PTD	GNB	PTD	GNB	PTD	GNB	PTD	GNB	PTD	--
130	STAIR #2	CT/ CPT	CT/ CB	GNB	PTD	GNB	PTD	GNB	PTD	GNB	PTD	GNB	PTD	RUBBER NOSING; SEE NOTE #1
132	CORRIDOR	CT/ CPT	CT/ CB	GNB	WC	GNB	WC	GNB	WC	GNB	WC	SACT	--	SEE NOTE #1
134	CORRIDOR	CT/ CPT	CT/ CB	GNB	WC	GNB	WC	GNB	WC	GNB	WC	SACT	--	SEE NOTE #1
136	HALL	CT	CT	GNB	WC	GNB	WC	GNB	WC	GNB	WC	SGB	PTD	--
UPPER FLOORS														
-01	STAIR #1	CPT	CB	GNB	PTD	GNB	PTD	GNB	PTD	GNB	PTD	GNB	PTD	RUBBER NOSING
-16	ELEVATOR LOBBY	CT	CT	GNB	WC	GNB	WC	GNB	WC	GNB	WC	GNB	PTD	SEE NOTE #1 & 4
-18A	HOUSE KEEPING	VCT	VB	GNB	PTD	GNB	PTD	GNB	PTD	GNB	PTD	GNB	PTD	--
-18B	ICE	CT	CT	GNB	WC	GNB	WC	GNB	WC	GNB	WC	GNB	PTD	--
-18C	ELECTRICAL	SC	VB	GNB	PTD	GNB	PTD	GNB	PTD	GNB	PTD	GNB	PTD	--
-30	STAIR #2	CPT	CB	GNB	PTD	GNB	PTD	GNB	PTD	GNB	PTD	GNB	PTD	RUBBER NOSING
-30	CORRIDOR	CPT	CB	GNB	WC	GNB	WC	GNB	WC	GNB	WC	SACT/SGB	--/PTD	SEE NOTE #1, #3 & #4
-31	CORRIDOR	CPT	CB	GNB	WC	GNB	WC	GNB	WC	GNB	WC	SACT/SGB	--/PTD	SEE NOTE #1, #3 & #4

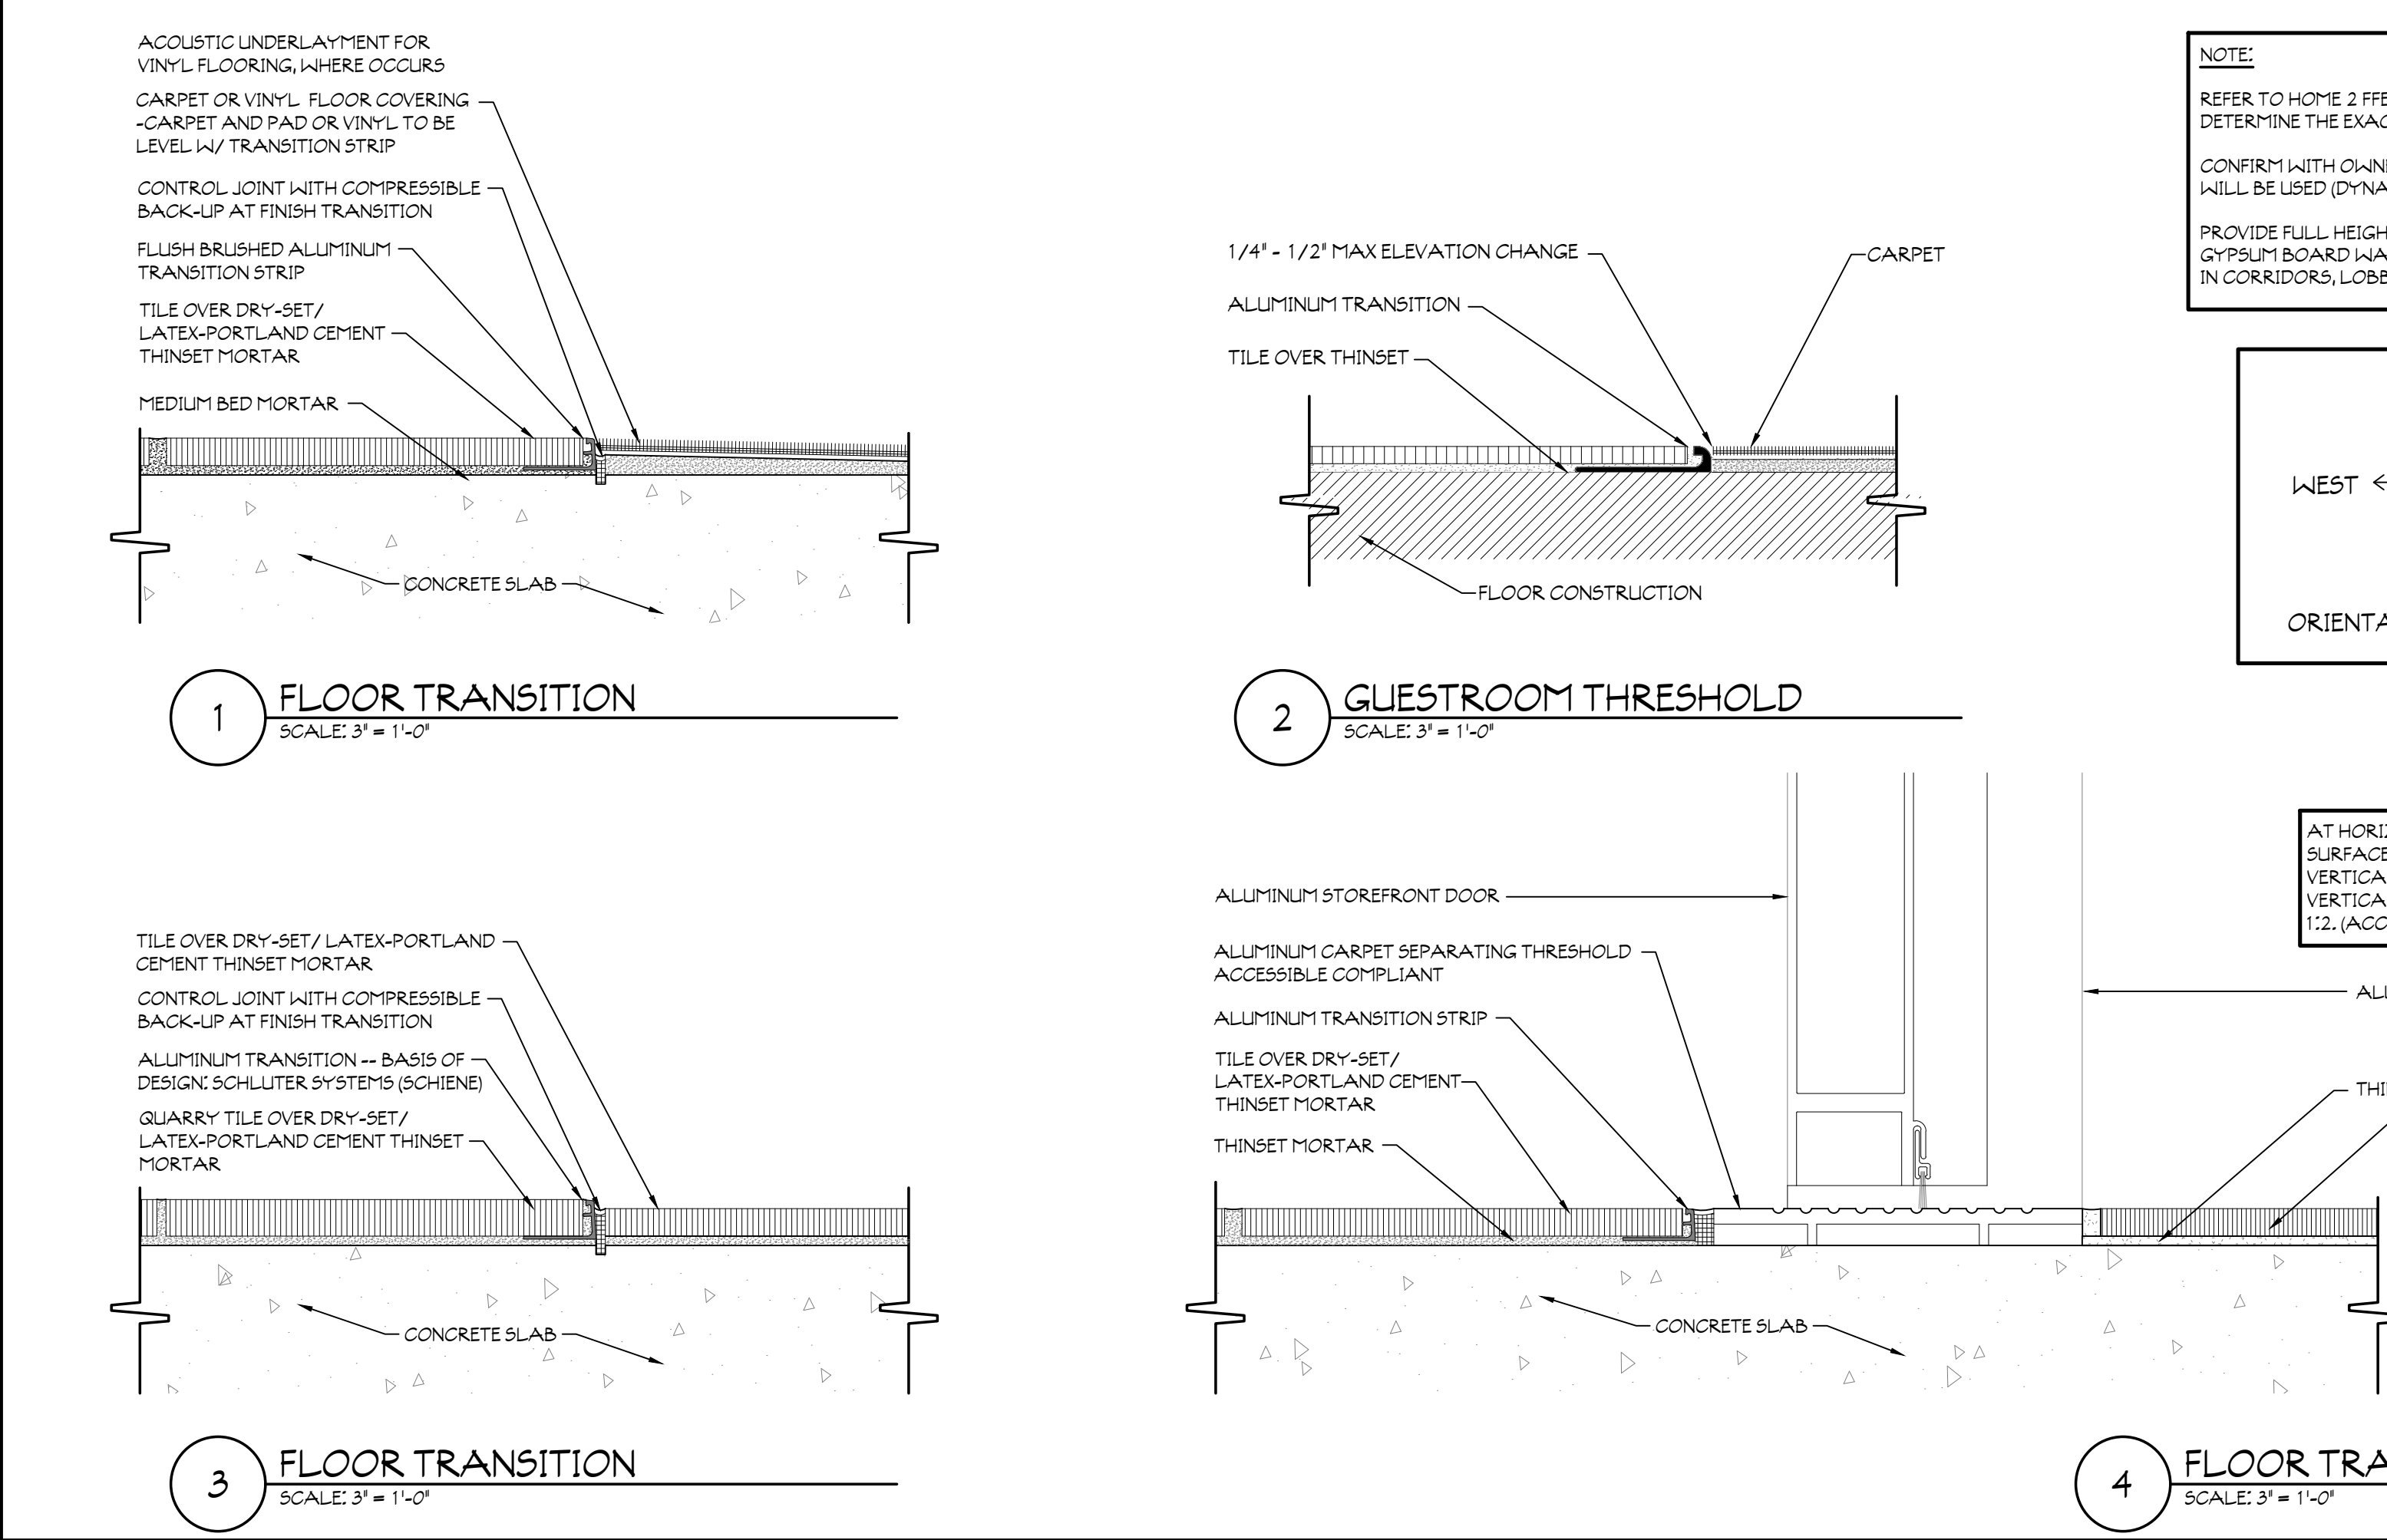

ROOM FINISH SCHEDULE NOTES

#1) SEE SHEETS (A901, A902, & A903) FOR LOCATION OF FLOOR FINISHES AT COMMON AREAS

#2) SEE SHEETS (A801-A809), INTERIOR ELEVATIONS FOR LOCATION OF WALL AND FLOOR FINISHES AT UNITS

#3) SEE SHEETS (A801-A809) FOR REFLECTED CEILING PLANS AT UNITS AND (A801A-A804) FOR CEILING AND BULKHEAD INFORMATION AT COMMON AREAS

#4) SEE SHEETS (A161, A162, A163 & A164) FOR INTERIOR ELEVATIONS

#5) REFER TO HOME2 SPIN2CYCLE FITNESS CENTER MANUAL FOR FLOOR SPECIFICATION

ABBREVIATIONS

CODE	DESCRIPTION	CODE	DESCRIPTION
PTD	PAINTED	CB	CARPET BASE
CPT	CARPET	SACT	SUSPENDED ACOUSTICAL CEILING TILE
SC	CONCRETE - SEALED	SCB	SUSPENDED GYPSUM BOARD
CT	CERAMIC TILE	VCT	VINYL COMPOSITION TILE
GT	QUARRY TILE	WC	WALL COVERING
FRP	FIBERGLASS REINFORCED PLASTIC PANEL	WP	WALL PANEL
	COLOR - WHITE	RF	RESILIENT FLOORING
GNB	GYPSUM WALL BOARD	DG	DENSGLOSS
PT	PORCELAIN TILE	SDE	STO DECO EIFS
VB	VINYL BASE	AK	ACRYLIC KNOCK DOWN TEXTURED FINISH
G	GLASS	SF	SPECIAL FINISH

GENERAL NOTES:

1. GLAZING IN ALL FIXED AND OPERABLE PANELS OF SWINGING, SLIDING AND BIFOLD DOORS MUST BE TEMPERED. ALL GLAZING ADJACENT TO AND WITHIN 24 INCHES OF DOORS AND WITHIN 60 INCHES OF FLOOR MUST BE TEMPERED. MARKED (T).

2. WINDOW FRAMES TO BE STANDARD ALUMINUM AND ALL FRAME COLORS TO MATCH

3. WINDOWS TO BE DUAL GLAZING, 1" INSULATED AND LOW-E

4. GLAZING CONTRACTOR TO CAULK EXTERIOR AND INTERIOR FRAMES

* VERIFY WITH OWNER ON ABOVE PRIOR TO PURCHASING

NOTE:

REFER TO HOME 2 FFE SPEC'S/ FINISH INDEX TO DETERMINE THE EXACT FINISH IN EACH ROOM

CONFIRM WITH OWNER WHICH SCHEME WILL BE USED (DYNAMIC OR VIBRANT)

PROVIDE FULL HEIGHT CORNER GUARDS AT ALL GYPSUM BOARD WALL SUSCEPTIBLE TO DAMAGE IN CORRIDORS, LOBBY, PUBLIC AREAS ECT.

NOTE:

USE (MGB) MOISTURE GYPSUM WALL BOARD IN WET AREAS IN LIEU OF (GNB) GYPSUM WALL BOARD UNLESS OTHERWISE NOTED

GENERAL NOTES

ALTHOUGH DRAWINGS ARE PREPARED TO SCALE, THE ACCURACY OF THE DRAWINGS CANNOT BE GUARANTEED. FIELD DIMENSIONS SHALL BE DEEMED TO TAKE PRECEDENCE OVER DIMENSIONS SHOWN ON THE DRAWINGS.

ALL DIMENSIONS UNLESS OTHERWISE NOTED SHALL BE IN FEET AND INCHES. DIMENSIONS SHALL BE ROUNDED UP TO THE NEXT WHOLE INCH.

THESE DRAWINGS ARE THE PROPERTY OF MAUST ARCHITECTURAL SERVICES, INC. AND ARE NOT TO BE REPRODUCED, COPIED, OR TRANSMITTED IN ANY FORM OR BY ANY MEANS, ELECTRONIC OR MECHANICAL, WITHOUT THE WRITTEN PERMISSION OF MAUST ARCHITECTURAL SERVICES, INC.

Architects
Planners
* MAUST ARCHITECTURAL SERVICES, INC.
* Construction Mgmt.
* Rule 5 and MS4 Filing
L.E.M., INC.
112 NORTH MAIN STREET
GOSHEN, INDIANA 46526
PHONE: (574) 537-8500
FAX: (574) 537-0808

HOME 2 SUITES BY HILTON

FT. WAYNE, INDIANA

REVISIONS:

NO.	DATE	DESCRIPTION

DATE: 05/01/26
JOB NO.: MAS-26-105
NAME: ROOM FINISH SCHEDULE & WINDOW TYPES
SHEET: A702