


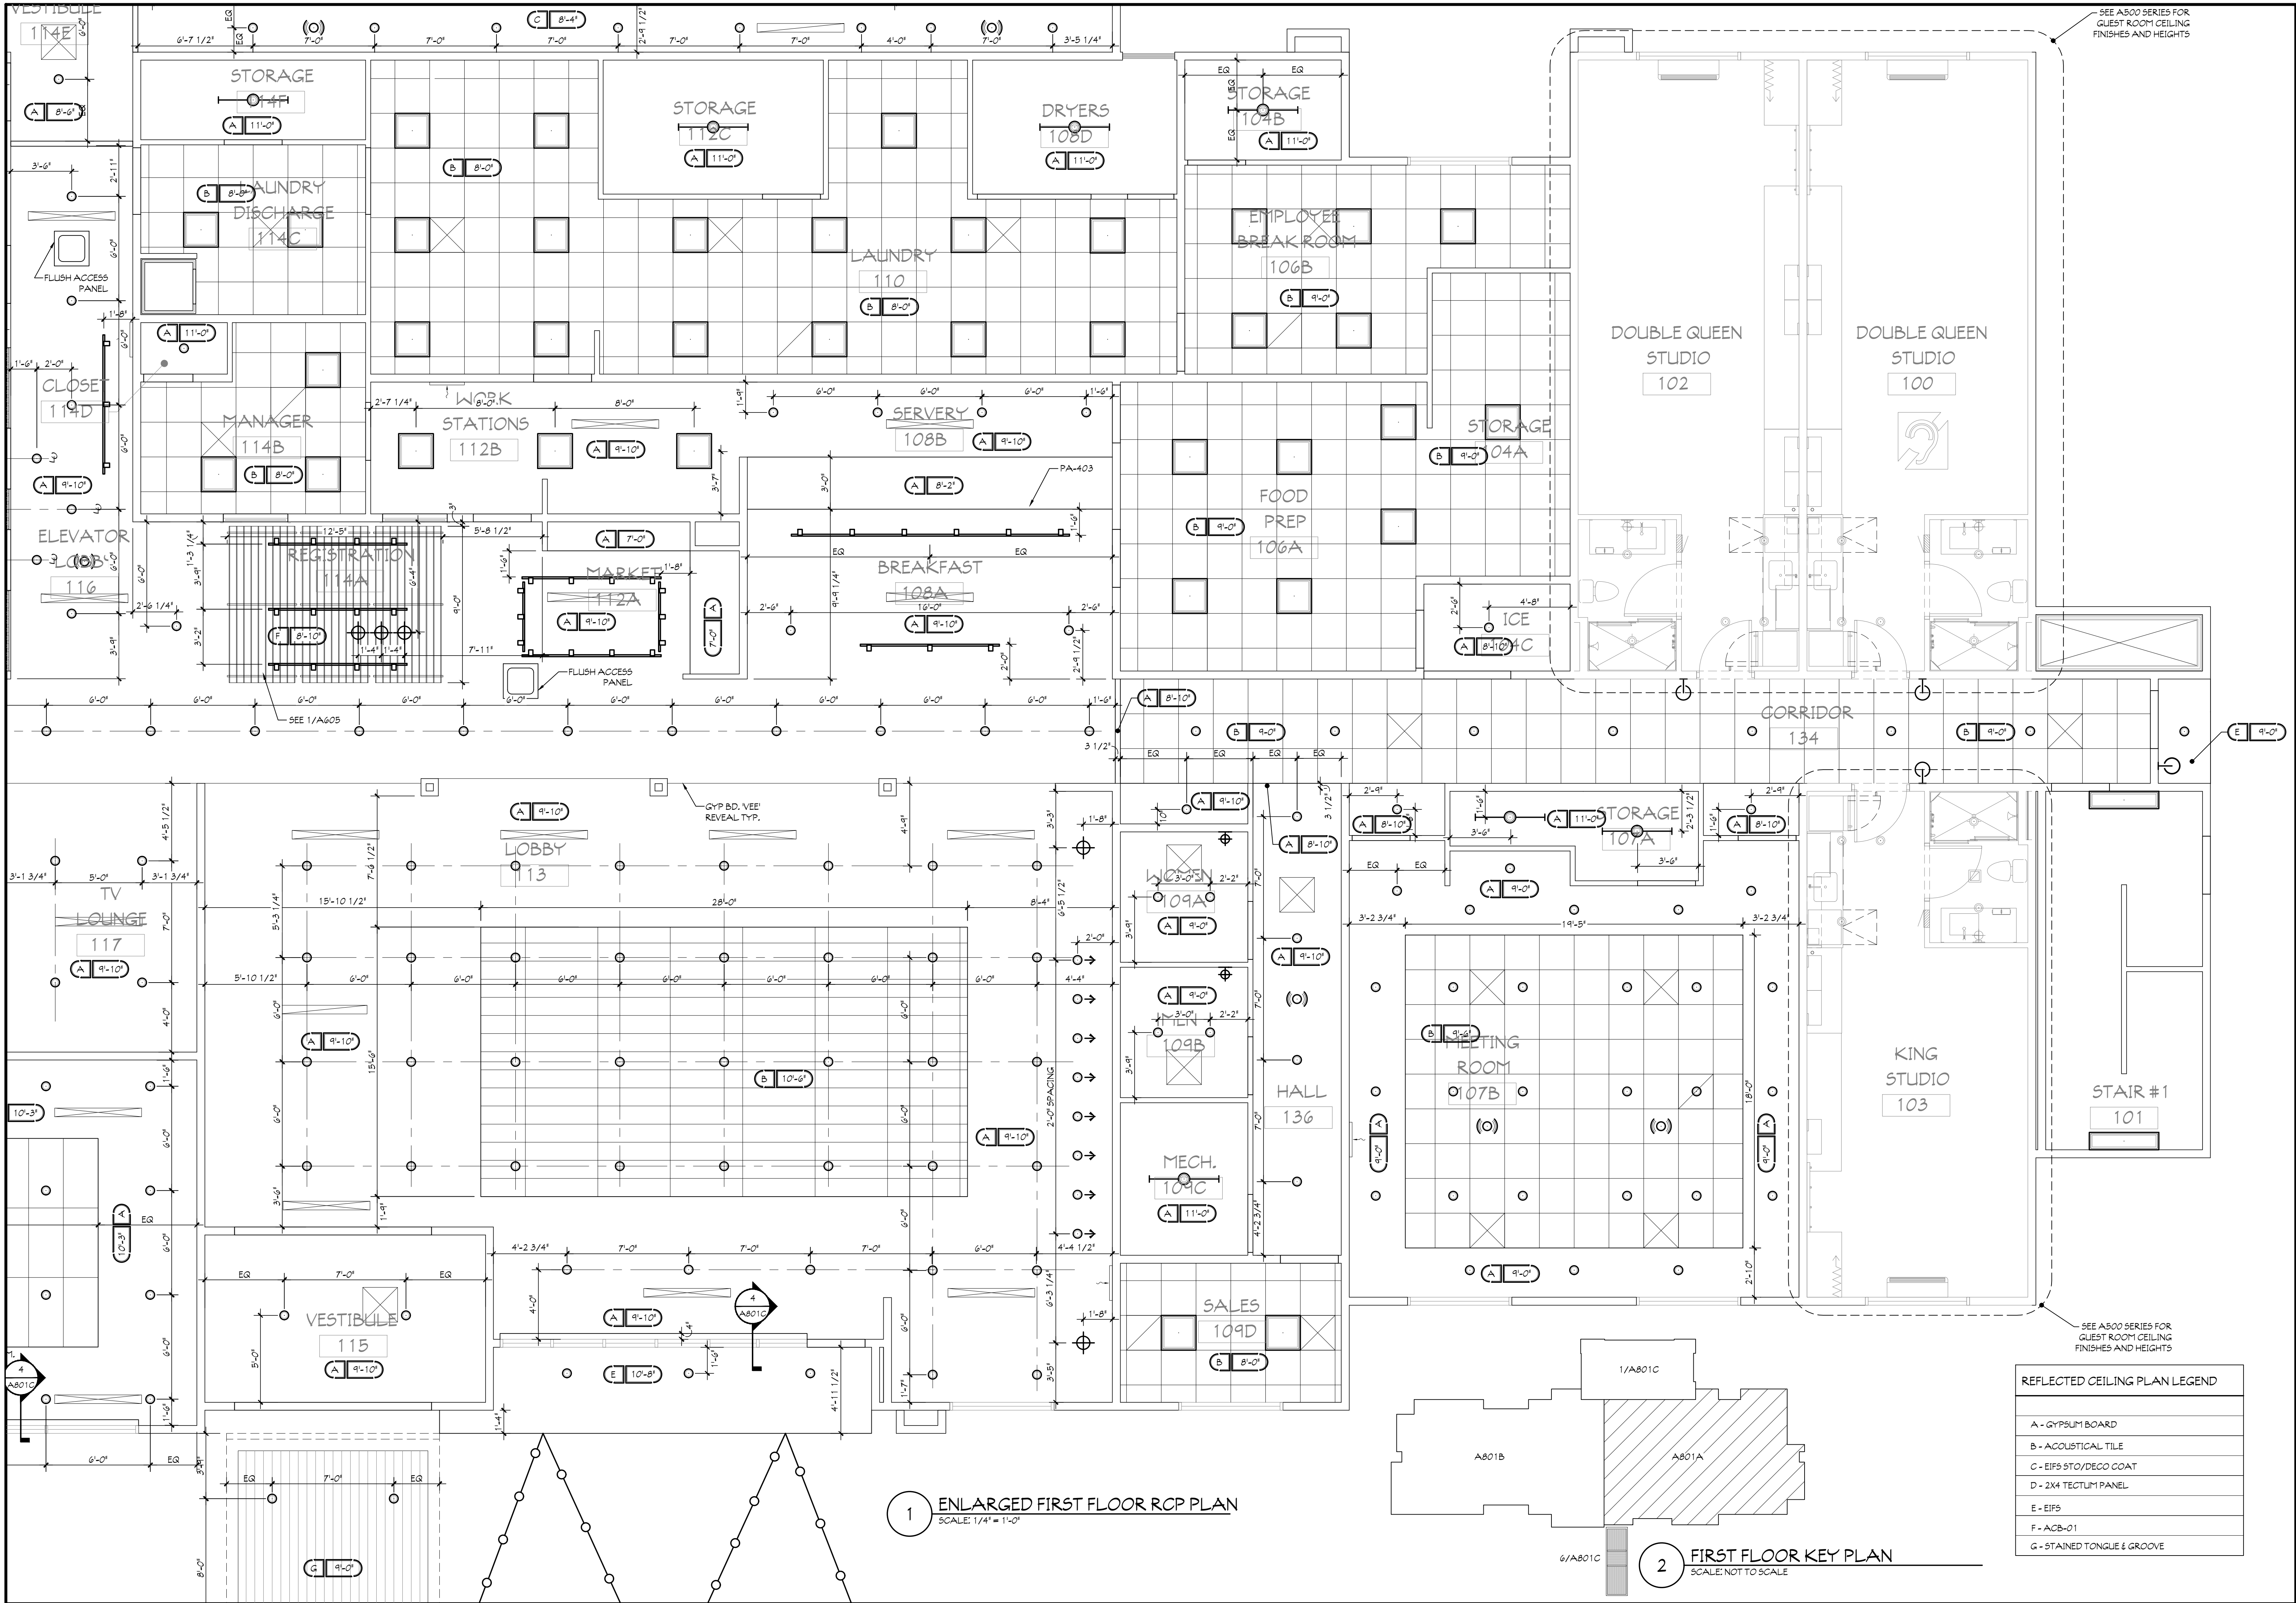

GENERAL NOTES

ALTHOUGH DIMENSIONS ARE GIVEN TO SCALE, THE ACCURACY OF THE DRAWINGS CANNOT BE GUARANTEED. DIMENSIONS SHALL BE DEEMED TO BE THE MOST PRECISE. ALL DIMENSIONS SHALL BE IN FEET AND INCHES. UNLESS OTHERWISE NOTED, ALL DIMENSIONS SHALL BE TO THE FACE OF THE MEMBER. DIMENSIONS SHALL NOT BE FIELD RESPONSIBLE FOR ANY DISCREPANCIES. GENERAL CONTRACTOR MUST VERIFY ALL DIMENSIONS PRIOR TO CONSTRUCTION.

MAUIST ARCHITECTURAL SERVICES

PLANNERS

ARCHITECTS

CONSTRUCTION MGMT.

L.E.M., INC.

112 NORTH MAIN STREET

GOSHEN, INDIANA 46526

PHONE (574) 537-8500

FAX (574) 537-0808

HOME 2

SUITES BY HILTON

FT. WAYNE, INDIANA

REVISIONS:

DATE: 05/01/26

JOB NO.: MAS-26-105

NAME: ENLARGED FIRST FLOOR REFLECTED CEILING PLAN

SHEET:

PRELIMINARY - NOT FOR CONSTRUCTION

A801A

REFLECTED CEILING PLAN LEGEND	
A - GYPSUM BOARD	
B - ACOUSTICAL TILE	
C - EIFS STO/DECO COAT	
D - 2X4 TECTUM PANEL	
E - EIFS	
F - ACB-01	
G - STAINED TONGUE & GROOVE	