


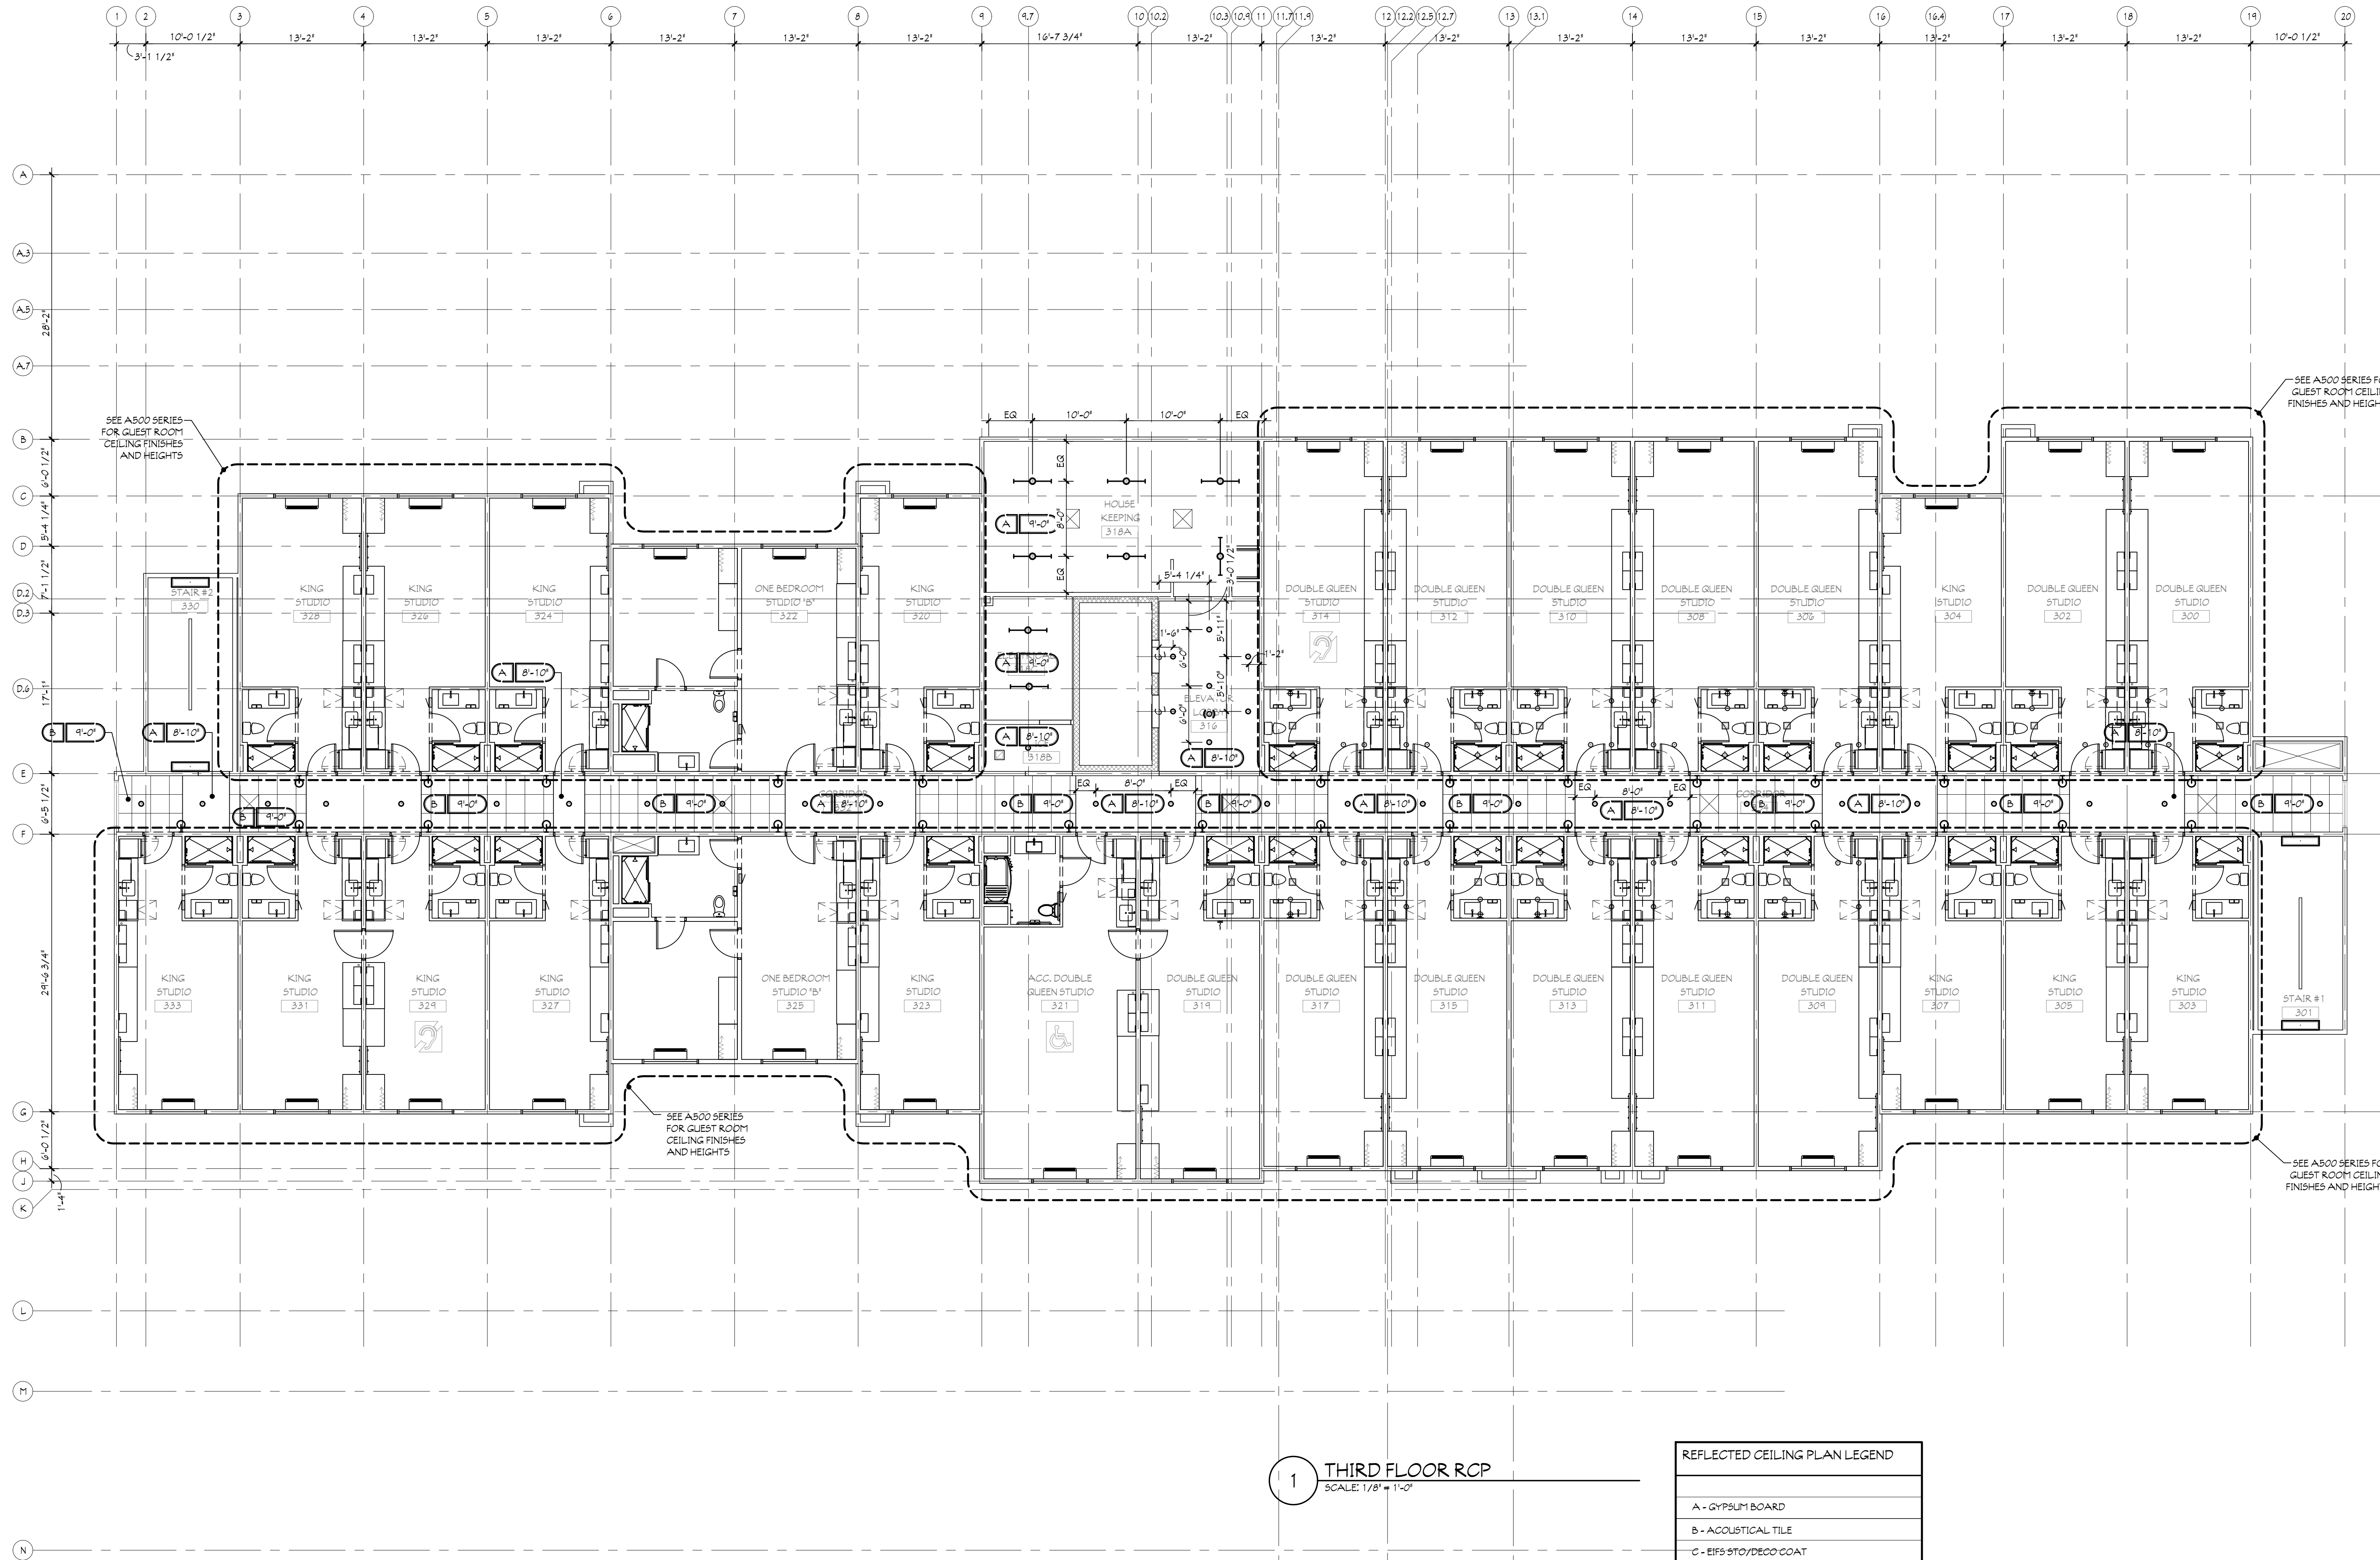

1 THIRD FLOOR RCP
SCALE: 1/8" = 1'-0"

REFLECTED CEILING PLAN LEGEND	
A - GYPSUM BOARD	
B - ACOUSTICAL TILE	
C - EIFS STO/DECO COAT	

GENERAL NOTES

ALTHOUGH DRAWINGS ARE PREPARED TO SCALE, THE
ACCURACY OF THE DRAWINGS CANNOT BE
GUARANTEED. THE USER SHALL BE RESPONSIBLE FOR
OBTAINING ALL NECESSARY PERMITS AND
RIGHTS OF REPRODUCTION. DIMENSIONS SHALL BE DELETED
FROM DIMENSIONED PLANS.

ALL DIMENSIONS TO FACE UNLESS OTHERWISE NOTED.
SERVICES SHALL NOT BE HELD RESPONSIBLE FOR ANY
GENERAL CONTRACTOR, "HAST" ARCHITECTURAL,
112 NORTH MAIN STREET, 46526
GOSHEN, INDIANA 46526
PHONE: (574) 537-8500
FAX: (574) 537-0808

Architects
Planners
Engineers
Construction Mgmt.
* Rule 5 and MS4 Filing
L.E.M., INC.
112 NORTH MAIN STREET
GOSHEN, INDIANA 46526
PHONE: (574) 537-8500
FAX: (574) 537-0808

MAUST ARCHITECTURAL
SERVICES
DIVISION OF
L.E.M., INC.
112 NORTH MAIN STREET
GOSHEN, INDIANA 46526
PHONE: (574) 537-8500
FAX: (574) 537-0808

These drawings are the property of Maust Architectural Services and may not be reprinted, copied
or used in any manner without the express written consent of Maust Architectural Services.

HOME 2
SUITES BY HILTON

SHEET SIZE 24x36

FT. WAYNE, INDIANA

REVISIONS:

PRELIMINARY - NOT
FOR CONSTRUCTION

DATE: 05/01/26
JOB NO.: MAS-26-105
NAME:
THIRD FLOOR
REFLECTED CEILING PLAN
SHEET:
A803