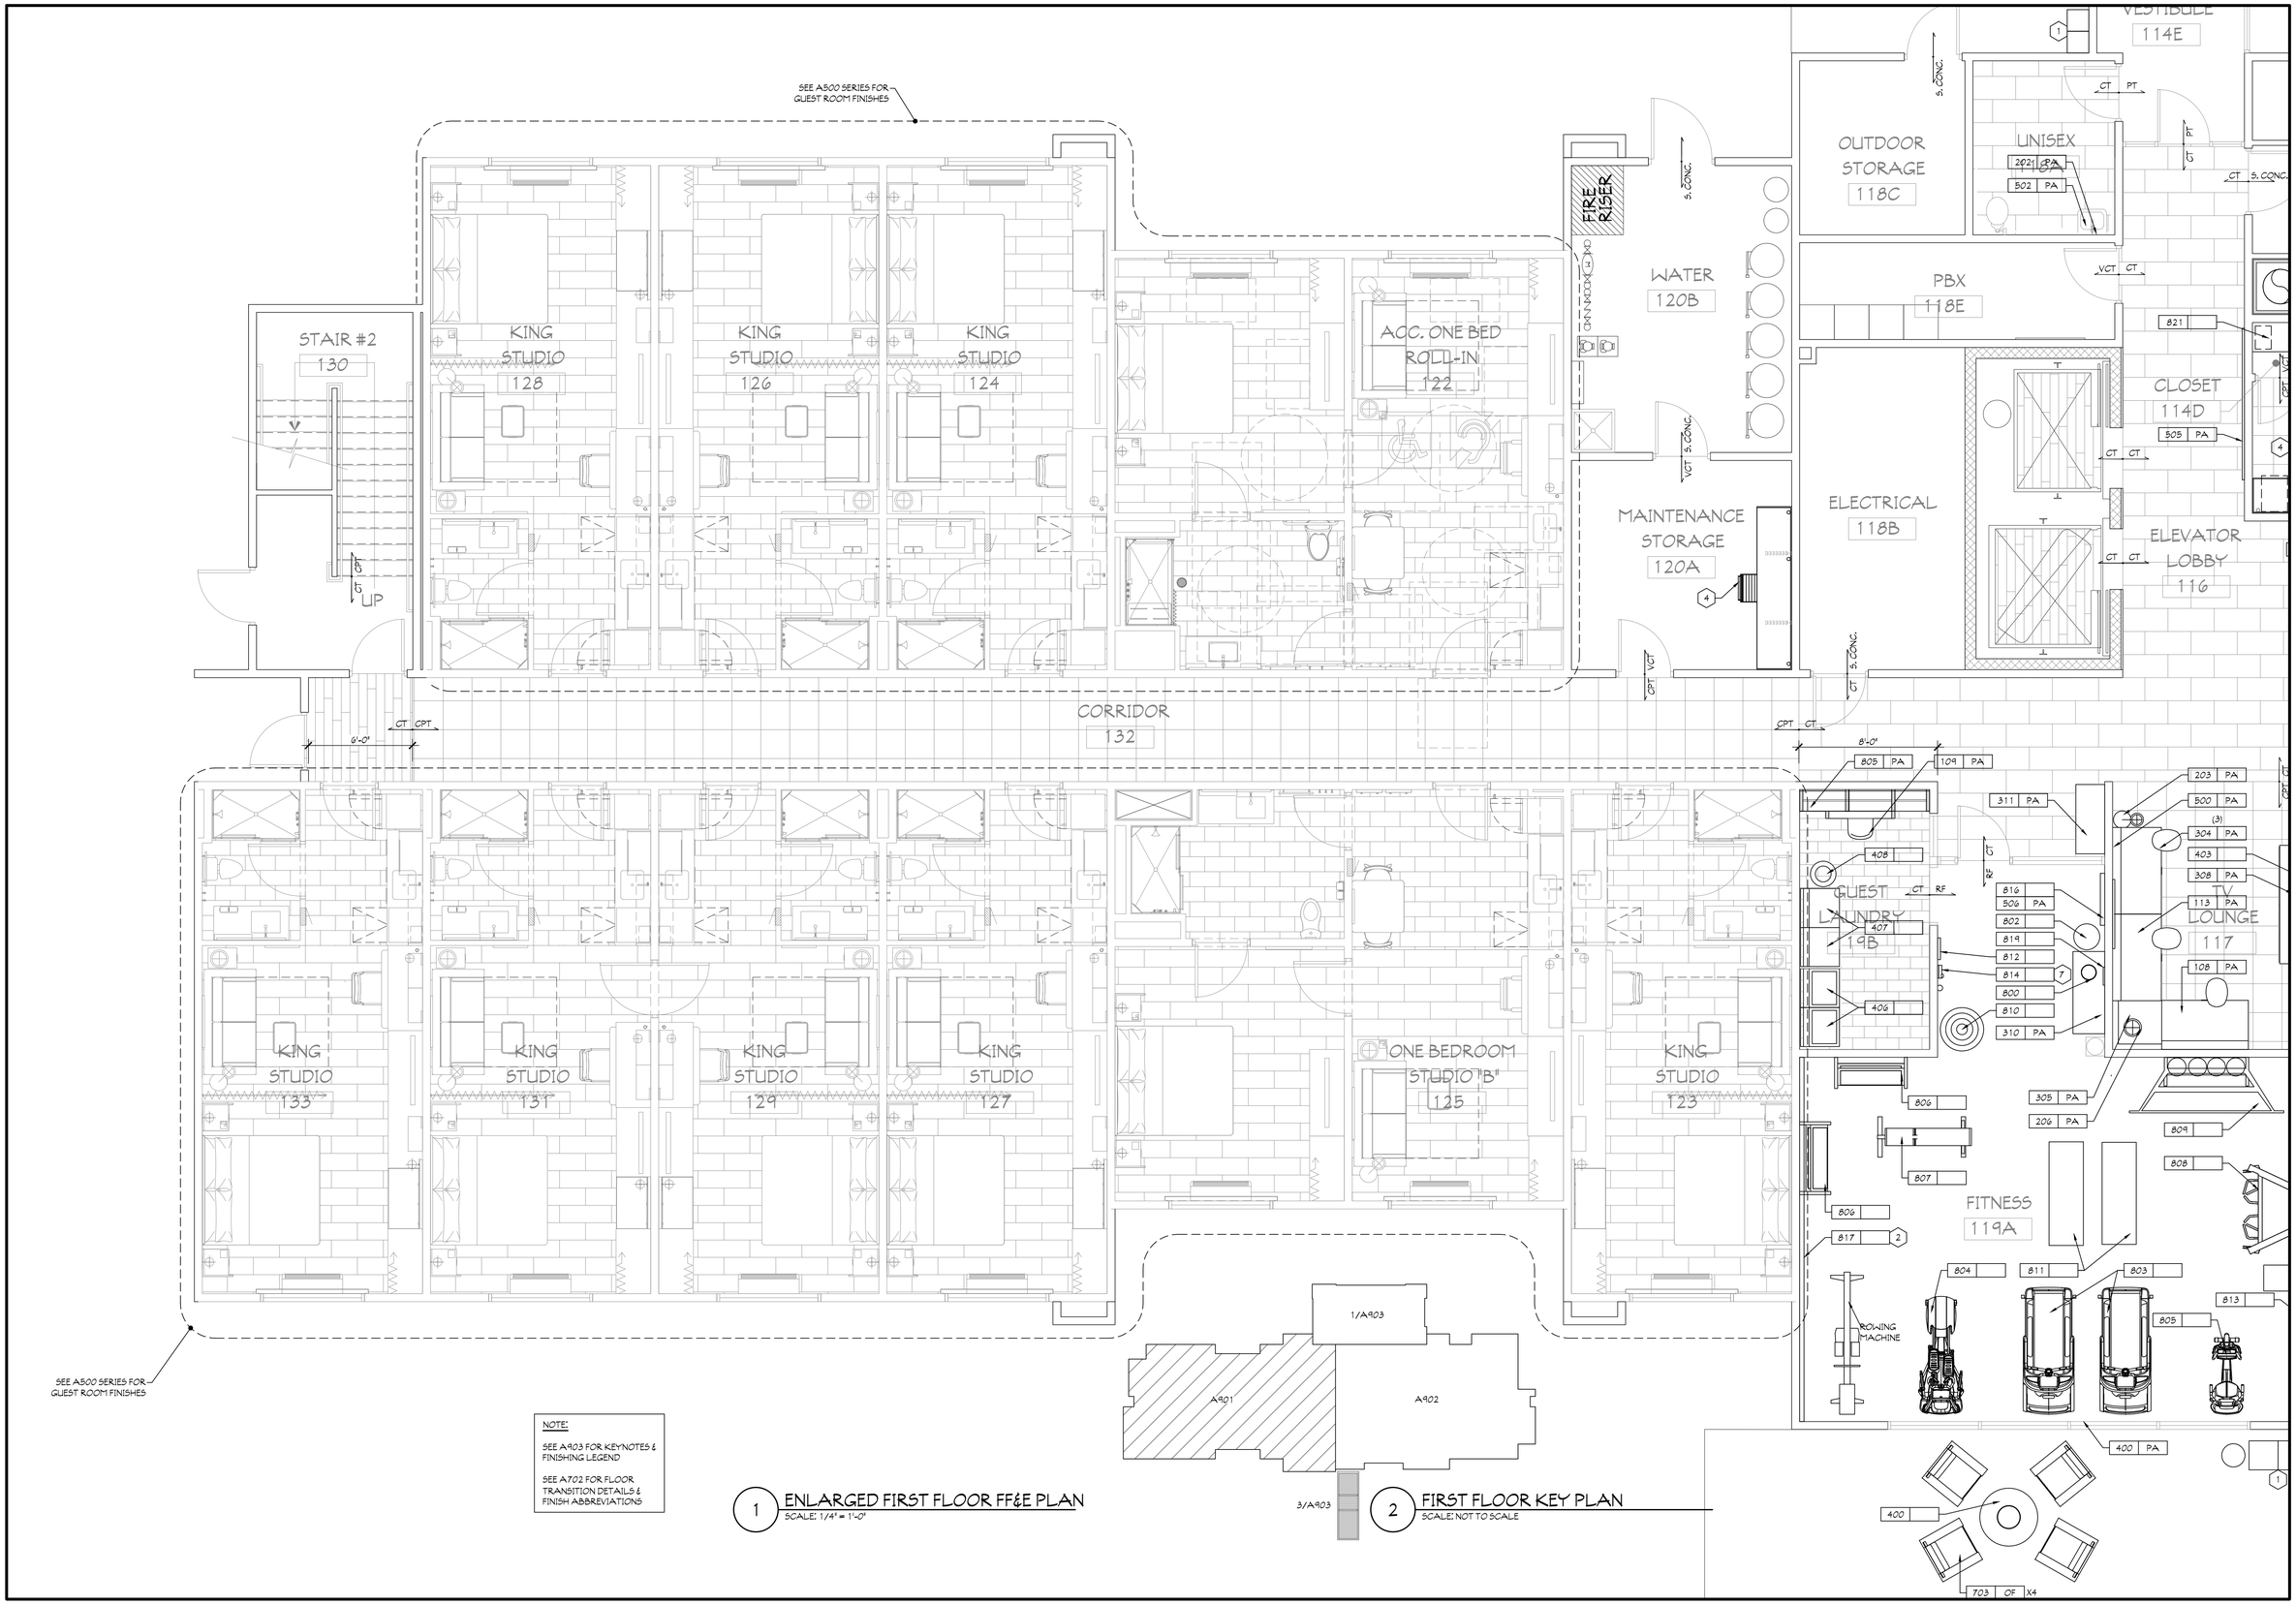

NOTE:

SEE A903 FOR KEYNOTES & FINISHING LEGEND

SEE A702 FOR FLOOR TRANSITION DETAILS & FINISH ABBREVIATIONS

1 ENLARGED FIRST FLOOR FF&E PLAN
SCALE: 1/4" = 1'-0"

2 FIRST FLOOR KEY PLAN
SCALE: NOT TO SCALE

GENERAL NOTES

-ALL DIMENSIONS, ROUGH OPENING SIZES, AND ELEVATION MARKERS MUST BE FIELD VERIFIED BY THE GENERAL CONTRACTOR. MAUST ARCHITECTURAL SERVICES SHALL NOT BE HELD RESPONSIBLE FOR ANY DIMENSIONAL DISCREPANCIES WHICH HAVE NOT BEEN BROUGHT TO THEIR ATTENTION PRIOR TO CONSTRUCTION.

MAUST ARCHITECTURAL SERVICES
DIVISION OF L.E.M., INC.
112 NORTH MAIN STREET
GOSHEN, INDIANA 46526

* Architects
* Planners
* Consultants
* Construction Mgmt.
* Rule 5 and MS4 Filing

PHONE (574) 537-8500
FAX (574) 537-0808

These drawings are the property of Maust Architectural Services and may not be reprinted, copied or reused in any manner without the expressed written consent of Maust Architectural Services.

HOME 2 SUITES BY HILTON

SHEET SIZE 24x36

FT. WAYNE, INDIANA

REVISIONS:

PRELIMINARY - NOT FOR CONSTRUCTION

DATE: 05/01/26

JOB NO.: MAS-26-105

NAME: ENLARGED FIRST FLOOR FF&E PLAN

SHEET: A901