


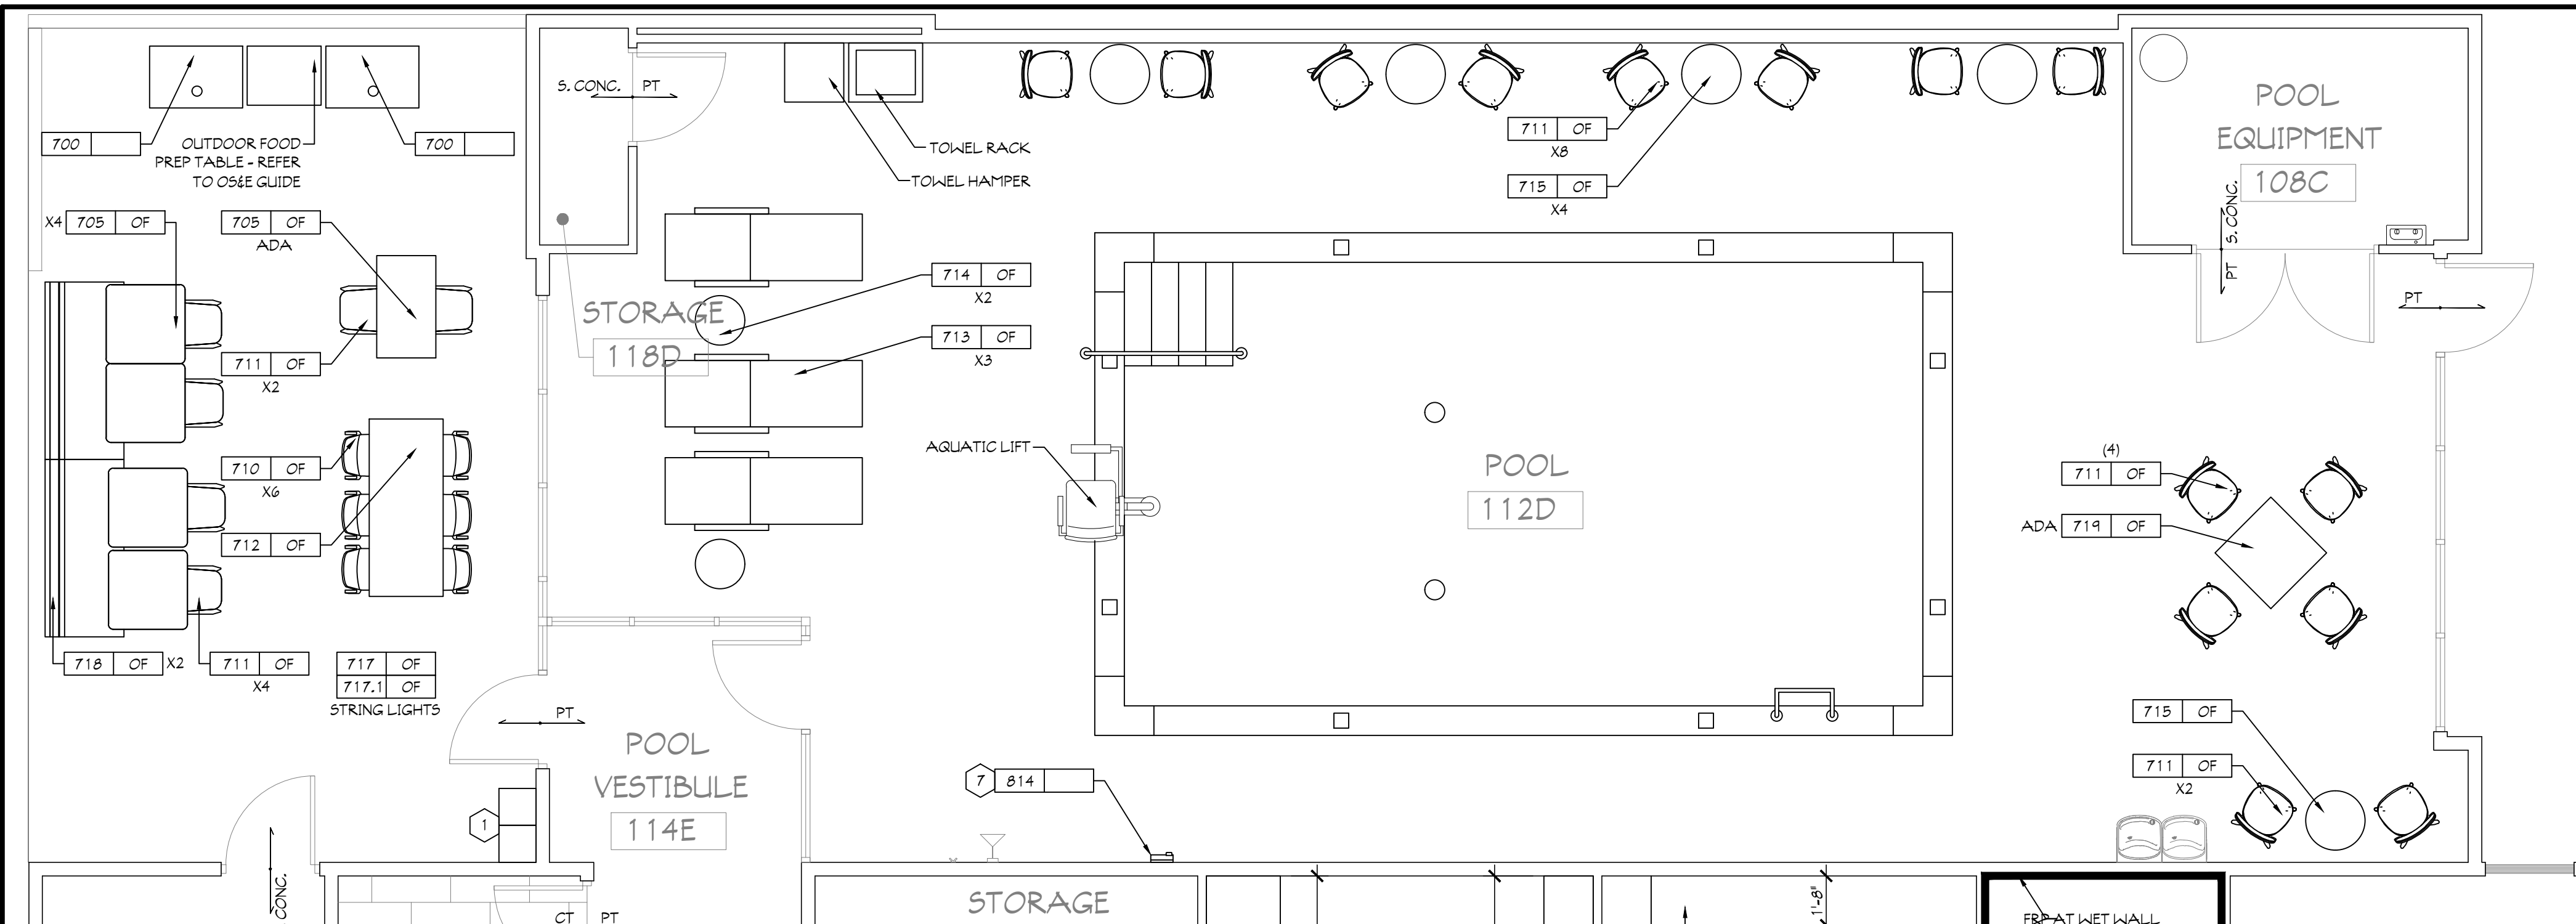


FURNISHINGS LEGEND:		CONFIRM WITH OWNER WHICH SCHEME WILL BE USED (DYNAMIC OR VIBRANT)	
SEATING		300	SHELVING
PA-100 CENTRAL BANQUETTE		301	OFFICE FURNITURE
PA-101 DINING CHAIR @ 2 TOP SQUARE TABLE		302	WORK STATION
PA-102 DINING CHAIR @ BANQUETTE		303	SAFE
PA-103 LOUNGE CHAIR @ BANQUETTE		304	LOCKERS
PA-104 HIGH BACK LOUNGE CHAIR		400	FIRE PIT WITH FITTED SCREEN
PA-105 FOCUS BOOTH		401	COMMERCIAL WASHER
PA-106 DINING CHAIR @ 4 TOP TABLE		402	COMMERCIAL DRYER
PA-107 COUNTER STOOL @ PERCH TABLE		403	WALL MOUNTED TELEVISION
PA-108 LARGE SOFA @ TV LOUNGE		404	WALL SHELVING
PA-109 COUNTER STOOL @ LAUNDRY ROOM		405	BREAKROOM SINK
PA-110 EMPLOYEE BREAKROOM CHAIR		406	COIN OPERATED WASHER
PA-111 MEETING ROOM STACK CHAIR		407	COIN OPERATED DRYER
PA-112 TASK CHAIR		408	DECORATIVE TRASH CAN
PA-113 LARGE SOFA @ TV LOUNGE		409	DISHWASHER
LIGHTING		410	MOBILE TABLE
PA-201 PENDANT LIGHTING @ FOCUS BOOTH		411	REACH-IN COOLER
PA-202 BATHROOM VANITY LIGHT		412	REACH-IN FREEZER
PA-203 FLOOR LAMP @ TV LOUNGE		413	WORK STATION
PA-204 WALL SCONCE @ GUEST CORRIDOR		414	MOBILE SHELVING
PA-205 PENDANT LIGHTING @ RECEPTION		415	COFFEE MACHINE
PA-206 TABLE LAMP @ TV LOUNGE		416	3-COMPARTMENT SINK
CASEGOODS		417	HAND SINK
PA-300 SQUARE 2 TOP DINING TABLE		418	RACK/SHELF
PA-301 ROUND 2 TOP DINING TABLE		419	PRE-RINSE WITH FAUCET
PA-302 RECTANGULAR 4 TOP DINING TABLE		420	WATER FILTER
PA-303 TEA HEIGHT ROUND TABLE @ HIGH BACK LOUNGE CHAIR		421	WALL MOUNTED SHELVING
PA-304 LAPTOP TABLE		422	UNDER COUNTER REFRIGERATOR
PA-305 SQUARE SIDE TABLE @ TV LOUNGE		423	UPPER CABINETS
PA-306 DINING TABLE @ BOOTH		424	BATTER MIX STARTER KIT
PA-307 ADA DINING TABLE		425	CONVEYOR OVEN
PA-308 MEDIA CREDENZA @ TV LOUNGE		426	JUICE DISPENSER
PA-309 BREAKROOM DINING TABLE @ EMPLOYEE BREAKROOM		427	REFRIGERATOR
PA-310 TOWEL STATION @ FITNESS		428	WAFFLE IRON
PA-311 FOOD DELIVERY PICK-UP CONSOLE		429	MERCHANDISER REFRIGERATOR
PA-312 MEETING ROOM CONFERENCE TABLE		430	MERCHANDISER FREEZER
PA-313 MEETING ROOM TRAINING TABLE		431	WALL MOUNTED TELEVISION
PA-314 RETAIL TABLE - LARGE (MARKET TABLE)		432	ICE DISPENSER
PA-315 RETAIL TABLE - SMALL (MARKET TABLE)		433	KETTLE REHEAT/ALIZER
PA-316 RETAIL DISPLAY SYSTEM		434	WAFFLE MAKER - FUTURE
PA-320 RIGHT DECORATIVE SHELF ABOVE		436	WARMING DISPLAY CABINET
PA-325 LEFT DECORATIVE SHELF ABOVE		437	MICROWAVE OVEN (BELOW)
WINDOW TREATMENT		700	GAS GRILL
PA-400 ROLLER SHADE @ LOBBY & FITNESS ROOM (CURTAIN WALL)		800	TOWEL HAMPER
PA-401 ROLLER SHADE @ FITNESS (FRAMED WINDOWS) & BREAKROOM		801	WATER & CUP DISPENSER
PA-402 ROLLER SHADE @ SALES, BOARDROOM, & MEETING ROOM		802	GYM WIPES DISPENSER w/TRASH BIN
PA-403 ROLLER SHADE @ BREAKFAST SERVERY		803	TREADMILL
ARTWORK & MIRRORS		804	FITNESS TRAINER ELLIPTICAL
PA-500 TV LOUNGE ARTWORK		805	RECUMBENT CYCLE
PA-502 BATHROOM MIRROR		806	FREE WEIGHTS & RACK
PA-503 MEETING SPACE ARTWORK		807	WEIGHT BENCH
PA-504 BOARDROOM ARTWORK		808	STRENGTH SYSTEM
PA-505 GUEST ENGAGEMENT WALL ARTWORK		809	MEDICINE BALLS & RACK
PA-506 FITNESS WALL HOOKS		810	EXERCISE BALL
PA-507 TRIPTYCH ARTWORK		811	EXERCISE MAT
POOL AND PATIO		812	RULES SIGN
OF-700 BENCH SEATING @ OUTDOOR LOUNGE & GRILLING PATIO		813	WALL MOUNTED TELEVISION
OF-701 BENCH SEATING @ OUTDOOR LOUNGE FIREPIT		814	EMERGENCY TELEPHONE
OF-702 ARM CHAIR @ OUTDOOR LOUNGE		816	WALL HOOKS
OF-703 LOUNGE CHAIR @ OUTDOOR LOUNGE FIREPIT		817	WALL MOUNTED MIRRORS
OF-704 OTTOMAN @ OUTDOOR LOUNGE FIREPIT		819	WALL MOUNTED CLOCK
OF-705 2 TOP TABLE @ OUTDOOR LOUNGE & GRILLING PATIO		820	PLYO BOX
OF-706 ADA ADA TABLE @ GRILLING PATIO		821	SAFETY DEPOSIT BOX
OF-707 FOOD PREP TABLE @ GRILLING PATIO		822	LINEN CART
OF-708 COCKTAIL TABLE @ OUTDOOR LOUNGE		823	RATIONAL OVEN
OF-709 LOUNGE CHAIR @ OUTDOOR LOUNGE		824	BOTTLE FILLER
OF-710 ROUND SIDE TABLE @ OUTDOOR LOUNGE		825	WALL MOUNTED SHELVING
OF-711 DINING CHAIR @ OUTDOOR LOUNGE, GRILLING PATIO, & POOL		826	STORAGE CABINET
OF-712 COUNTER HEIGHT TABLE @ GRILLING PATIO		830	HYDRATION STATION
OF-713 CHaise LOUNGE @ POOL			
OF-714 ROUND SIDE TABLE @ POOL			
OF-715 ROUND 2 TOP TABLE @ POOL			
OF-716 PLANTER			
OF-717 STRING LIGHTS @ OUTDOOR LOUNGE & GRILLING PATIO			
OF-718 LIGHT BULBS @ STRING LIGHTS			
OF-719 BENCH SEATING @ GRILLING PATIO			
OF-714 TOP ADA DINING TABLE			
MILLWORK			
PA-800 PERCH TABLE			
PA-801 RECEPTION DESK			
PA-802 BREAKFAST SERVERY			
PA-803 COFFEE & HYDRATION STATION			
PA-804 TRASH & RECYCLING			
PA-805 GUEST LAUNDRY TABLE			
PA-806 ONE BAY BOARDROOM CASEWORK			
PA-807 THREE BAY MEETING ROOM CASEWORK			
PA-808 BREAKFAST PERCH TABLE			

1 ENLARGED FIRST FLOOR FF&E PLAN
SCALE: 1/4" = 1'-0"

NOTE:
SEE A702 FOR FLOOR
TRANSITION DETAILS &
FINISH ABBREVIATIONS

FURNISHINGS LEGEND: UPPER FLOORS	
PA-501	ART WORK
PA-404	ROMAN SHADE @ END OF CORRIDOR WINDOWS
404	SHELVING
432	ICE MACHINE

- KEYNOTES:
- TRASH CAN, RECYCLING BIN, & ASH BIN
 - GENERAL CONTRACTOR TO PROVIDE PLATE MIRROR FOR RECEIPT OF DECORATIVE FRAME (REFER TO HOME 2 FITNESS GUIDE FOR ADDITIONAL INFO.)
 - THIS UNIT CONTAINS A DISH RECOVERY CART & (2) TRASH CANS. THESE ITEMS MUST COORDINATE W/ MILLWORK VENDOR
 - OFFICE FURNITURE BY OWNER AS REQ'D.
 - PROVIDE ACCESSIBLE POWER & DATA AT EACH WORKSTATION
 - EMPLOYEE LOCKERS SHALL COMPLY W/ ACCESSIBILITY STANDARDS FOR PERCENTAGE OF ACCESSIBLE STORAGE - REFER TO HADG FOR REQ'S.
 - AN EMERGENCY TELEPHONE MUST BE PROVIDED. MOUNT W/IN ACCESSIBLE REACH RANGE. PHONE MUST BE EQUIPPED W/ VOLUME CONTROL & A MIN. 28" LONG CORD. AN ACCESSIBLE ROUTE MUST BE PROVIDED TO THE EMERGENCY HOUSE PHONE W/ A CLEAR FLOOR SPACE @ THE PHONE.
 - PROVIDE OPENINGS FOR TRASH, RECYCLING AND COMPOST AS NECESSARY
 - SEE FOOD SERVICE DRAWINGS FOR EQUIPMENT INFORMATION
 - OS&E DISH RECOVERY CART

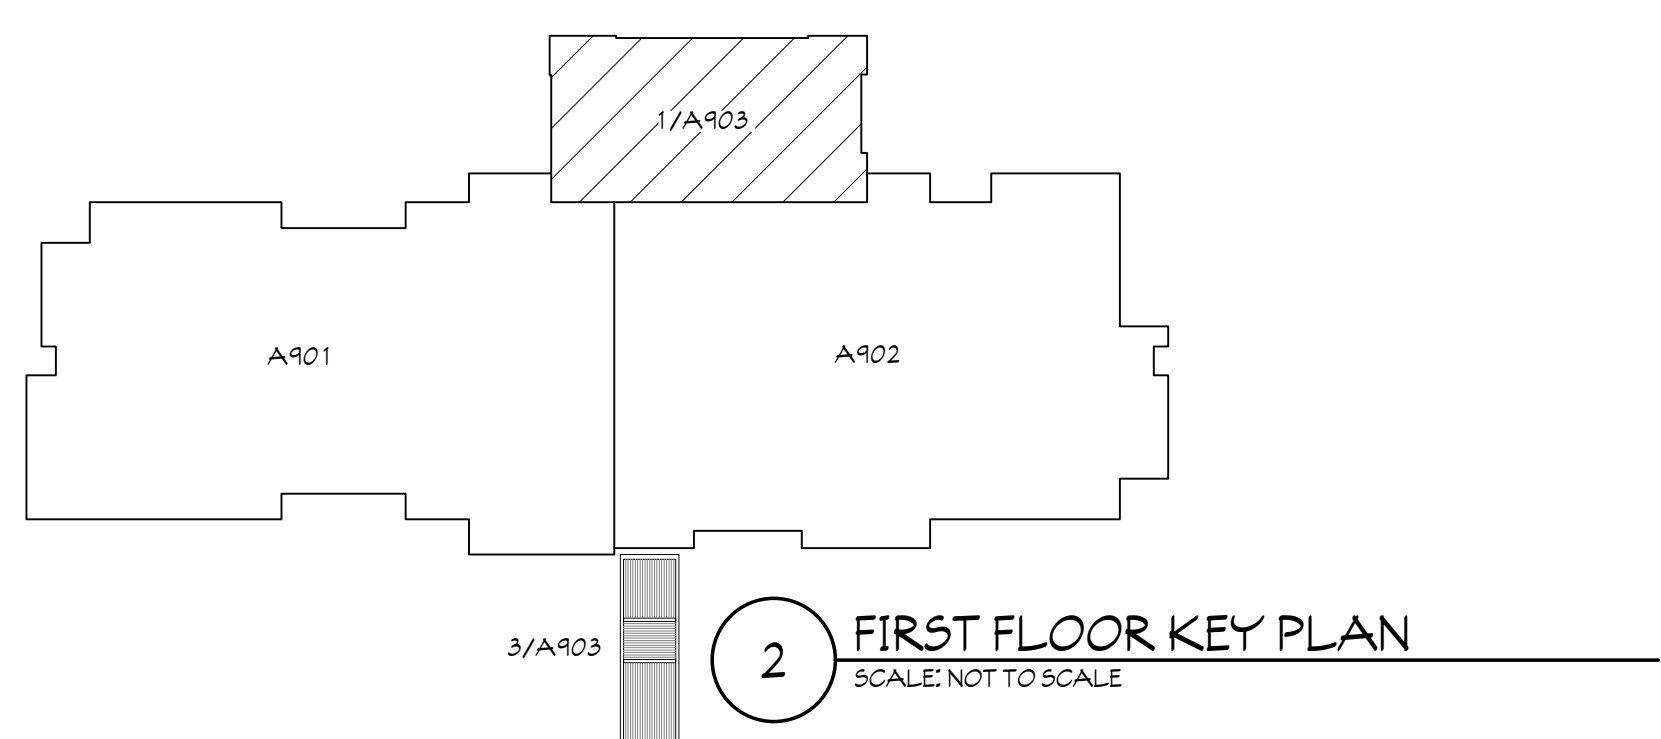

2 FIRST FLOOR KEY PLAN
SCALE: NOT TO SCALE

