


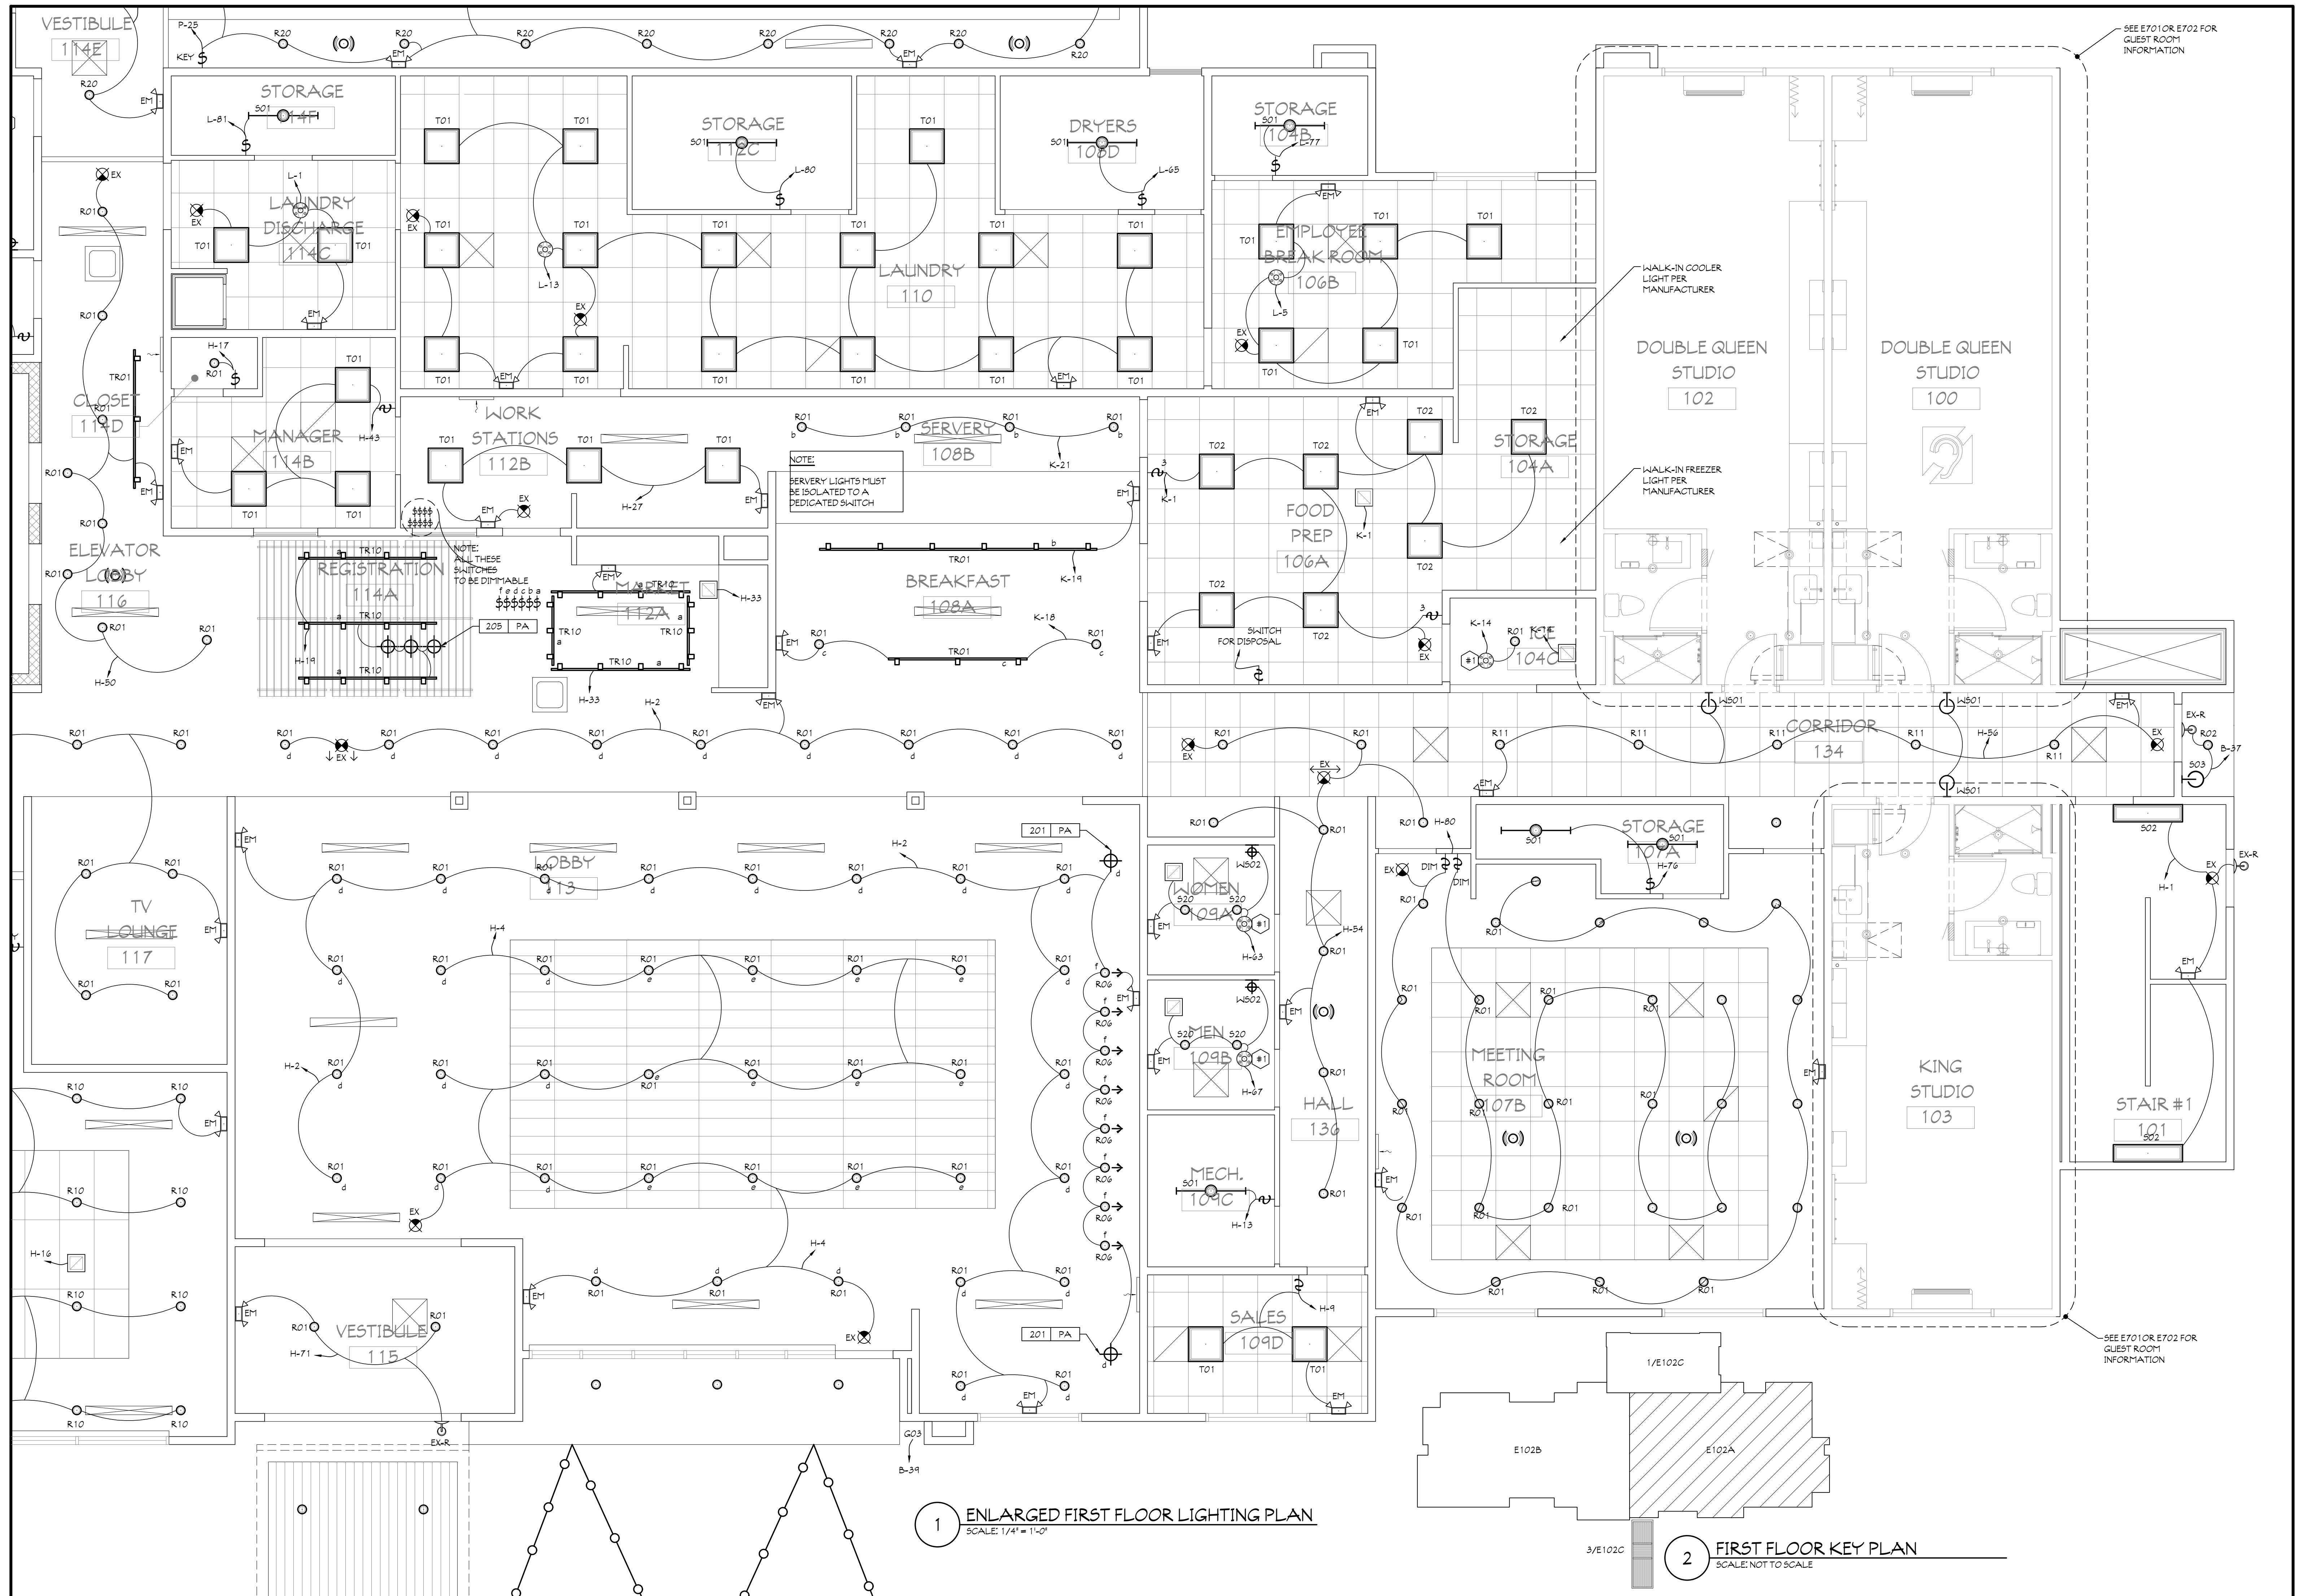

ALL DRAWINGS ARE DRAWN TO SCALE UNLESS OTHERWISE NOTED

M MAUS ARCHITECTURAL
SERVICES
DIVISION OF
L.E.M., INC.
112 NORTH MAIN STREET
GOSHEN, INDIANA 46526

* Planners
* Consultants
* Construction Mgmt.
* Rule 5 and MS4 Filing

PHONE (574) 537-8500
FAX (574) 537-0808

These drawings are the property of Maus Architectural Services and may not be reprinted, copied or otherwise used without written permission.



SHEET SIZE 24x36

FT. WAYNE, INDIANA

VISIONS:

DATE: 05/01/26
 SUB NO.: MAS-26-105
 NAME: ENLARGED FIRST
 FLOOR LIGHTING PLAN
 SHEET:

E102A