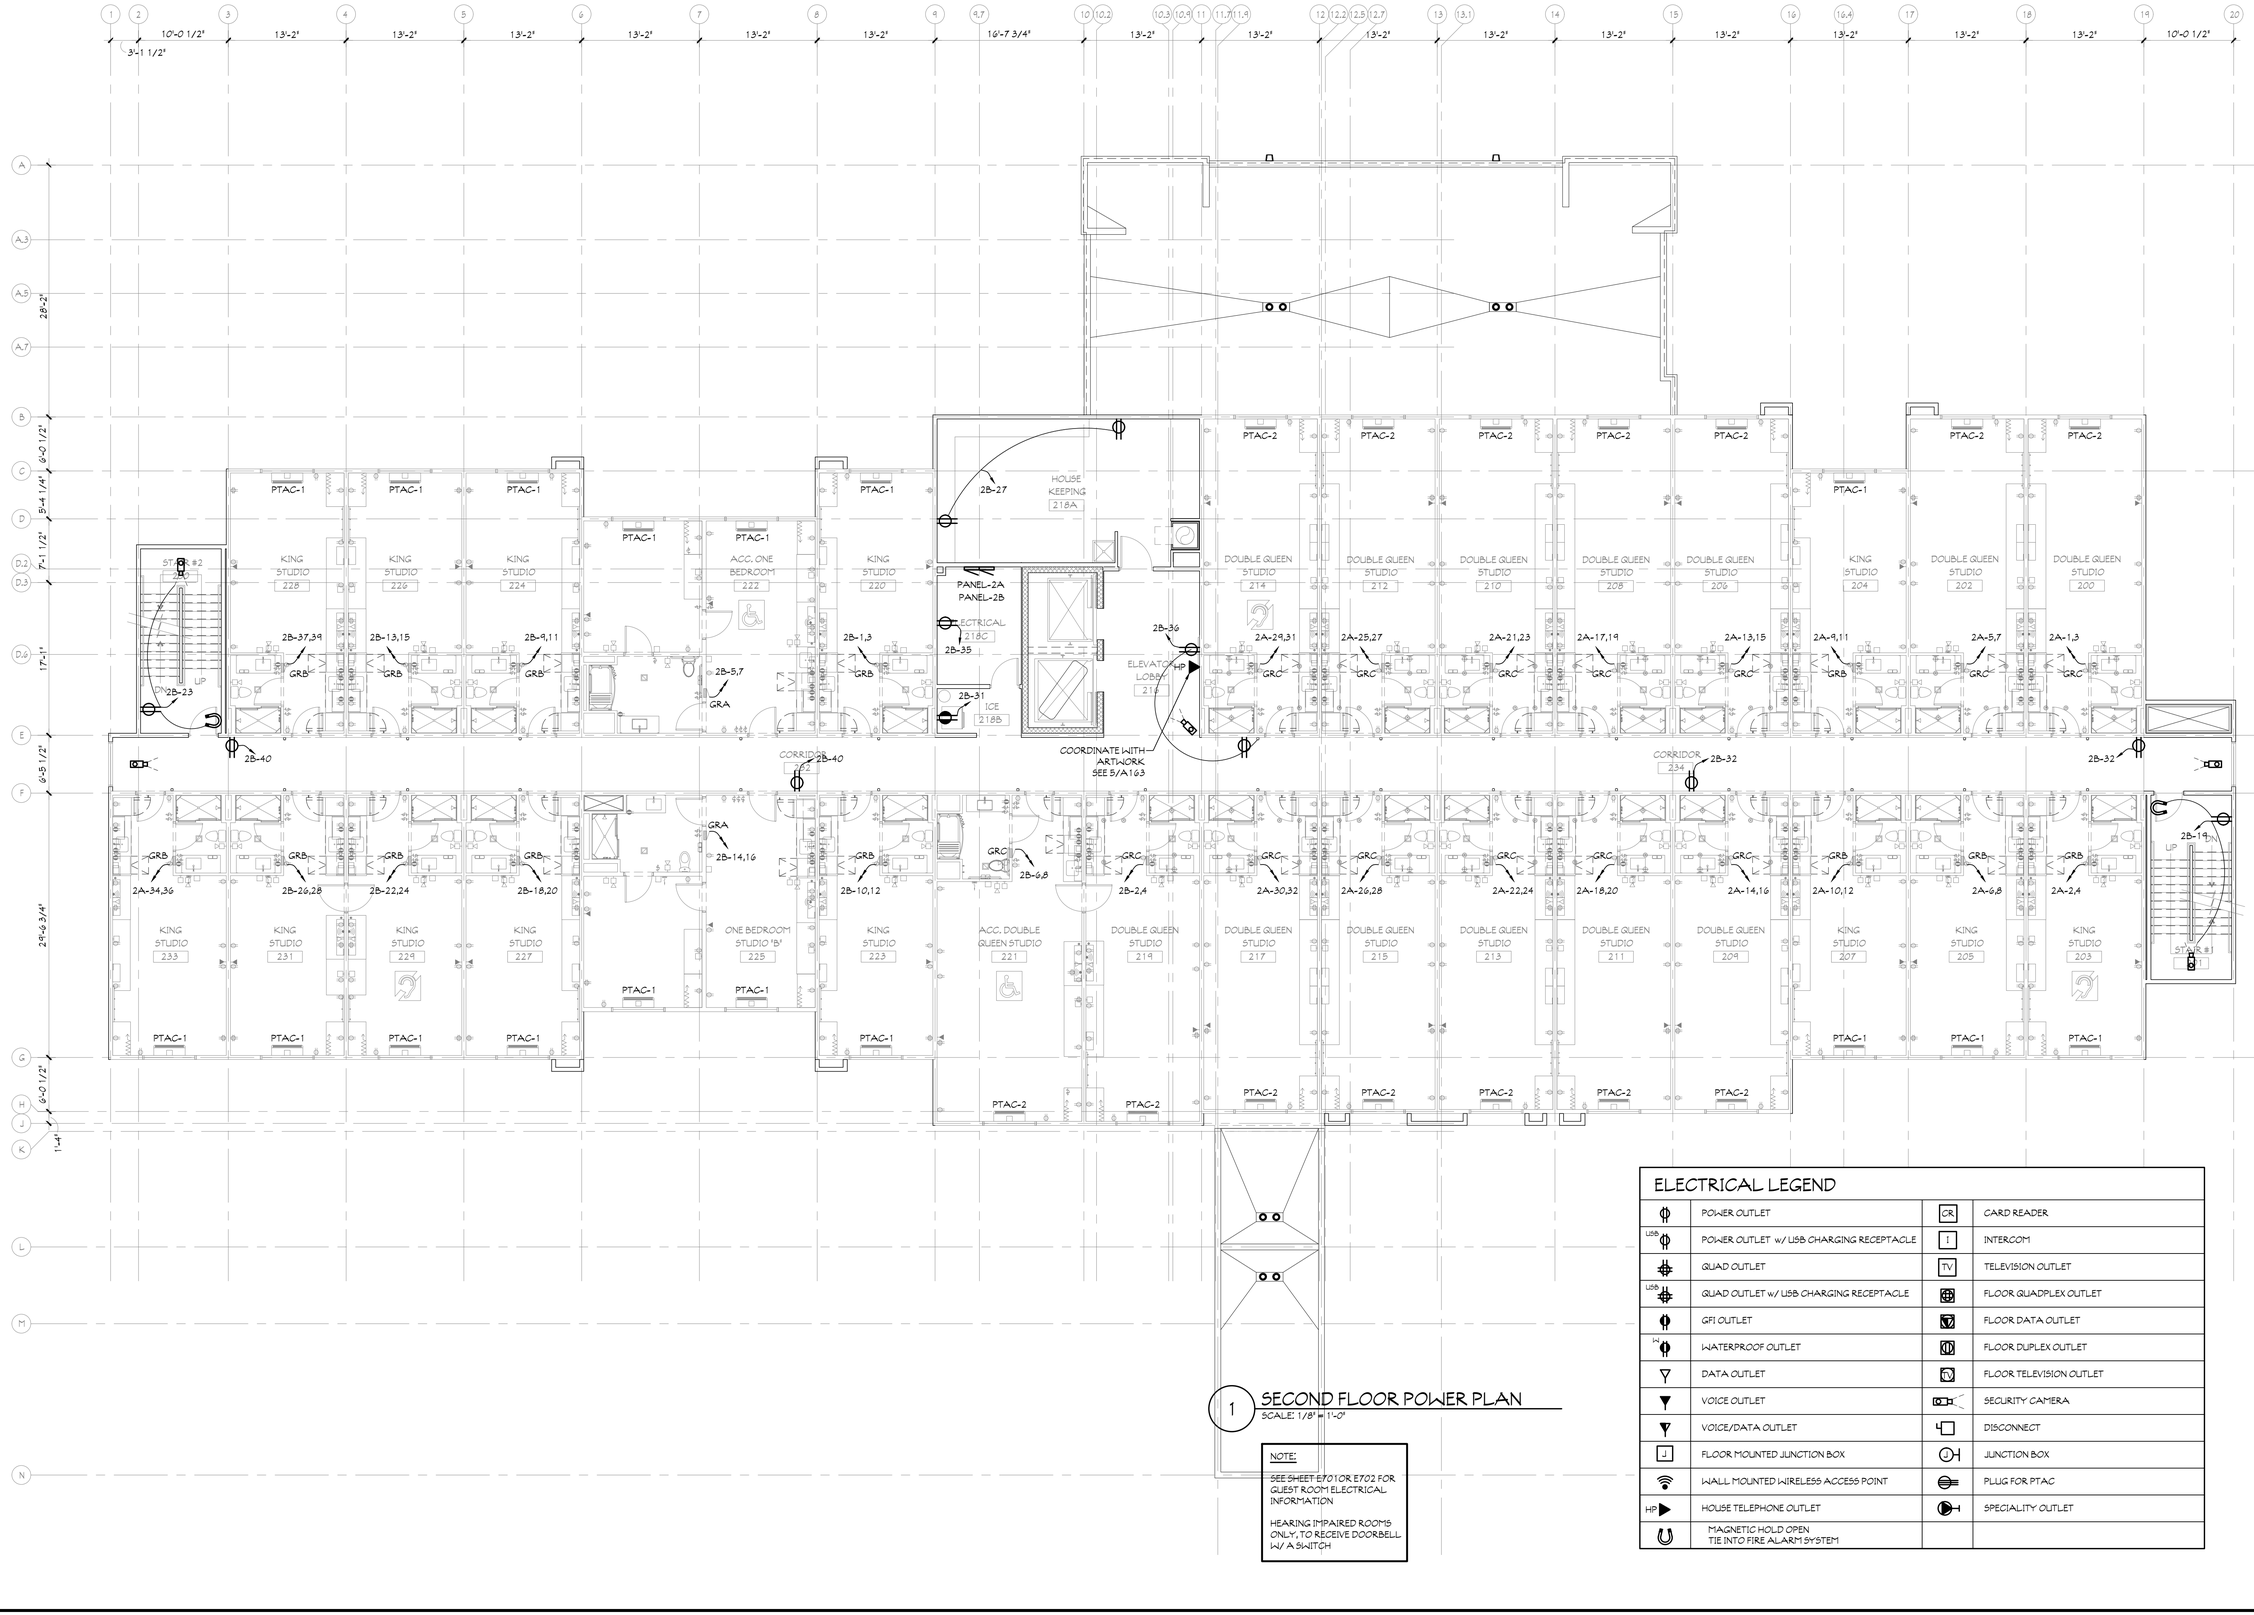


1 SECOND FLOOR POWER PLAN
SCALE: 1/8" = 1'-0"

NOTE:

SEE SHEET E701 OR E702 FOR GUEST ROOM ELECTRICAL INFORMATION

HEARING IMPAIRED ROOMS ONLY, TO RECEIVE DOORBELL W/ A SWITCH

ELECTRICAL LEGEND

	POWER OUTLET	CR	CARD READER
USB	POWER OUTLET w/ USB CHARGING RECEPTACLE	I	INTERCOM
	QUAD OUTLET	TV	TELEVISION OUTLET
USB	QUAD OUTLET w/ USB CHARGING RECEPTACLE		FLOOR QUADPLEX OUTLET
	GFI OUTLET		FLOOR DATA OUTLET
W	WATERPROOF OUTLET		FLOOR DUPLEX OUTLET
	DATA OUTLET	TV	FLOOR TELEVISION OUTLET
	VOICE OUTLET		SECURITY CAMERA
	VOICE/DATA OUTLET		DISCONNECT
J	FLOOR MOUNTED JUNCTION BOX	J	JUNCTION BOX
	WALL MOUNTED WIRELESS ACCESS POINT		PLUG FOR PTAC
HP	HOUSE TELEPHONE OUTLET		SPECIALITY OUTLET
	MAGNETIC HOLD OPEN TIE INTO FIRE ALARM SYSTEM		

GENERAL NOTES

- ALTHOUGH DRAWINGS ARE DRAWN TO SCALE, THE ACCURACY OF THE DRAWING CANNOT BE GUARANTEED DUE TO DISCREPANCIES IN THE METHODS OF REPRODUCTION. DIMENSIONS SHALL ALWAYS BE FIGURED FROM DIMENSIONED PLANS.
- ALL DIMENSIONS, ROUGH OPENING SIZES, AND ELEVATION MARKERS MUST BE FIELD VERIFIED BY THE CONTRACTOR PRIOR TO CONSTRUCTION. ANY DISCREPANCIES SHALL NOT BE HELD RESPONSIBLE FOR ANY ERRORS, OMISSIONS, OR CONFLICTS THAT HAVE NOT BEEN BROUGHT TO THEIR ATTENTION PRIOR TO CONSTRUCTION.

MAUST ARCHITECTURAL SERVICES DIVISION OF L.E.M., INC.
112 NORTH MAIN STREET
GOSHEN, INDIANA 46526
* Architects
* Planners
* Consultants
* Construction Mgmt.
* Rule 5 and MS4 Filing
PHONE (574) 537-8500
FAX (574) 537-0808

These drawings are the property of Maust Architectural Services and may not be reprinted, copied or stored in any manner without the expressed written consent of Maust Architectural Services.

HOME2 SUITES BY HILTON

SHEET SIZE 24x36

FT. WAYNE, INDIANA

REVISIONS:

PRELIMINARY - NOT FOR CONSTRUCTION

DATE: 05/01/26
JOB NO.: MAS-26-105
NAME: SECOND FLOOR POWER PLAN
SHEET: E201