


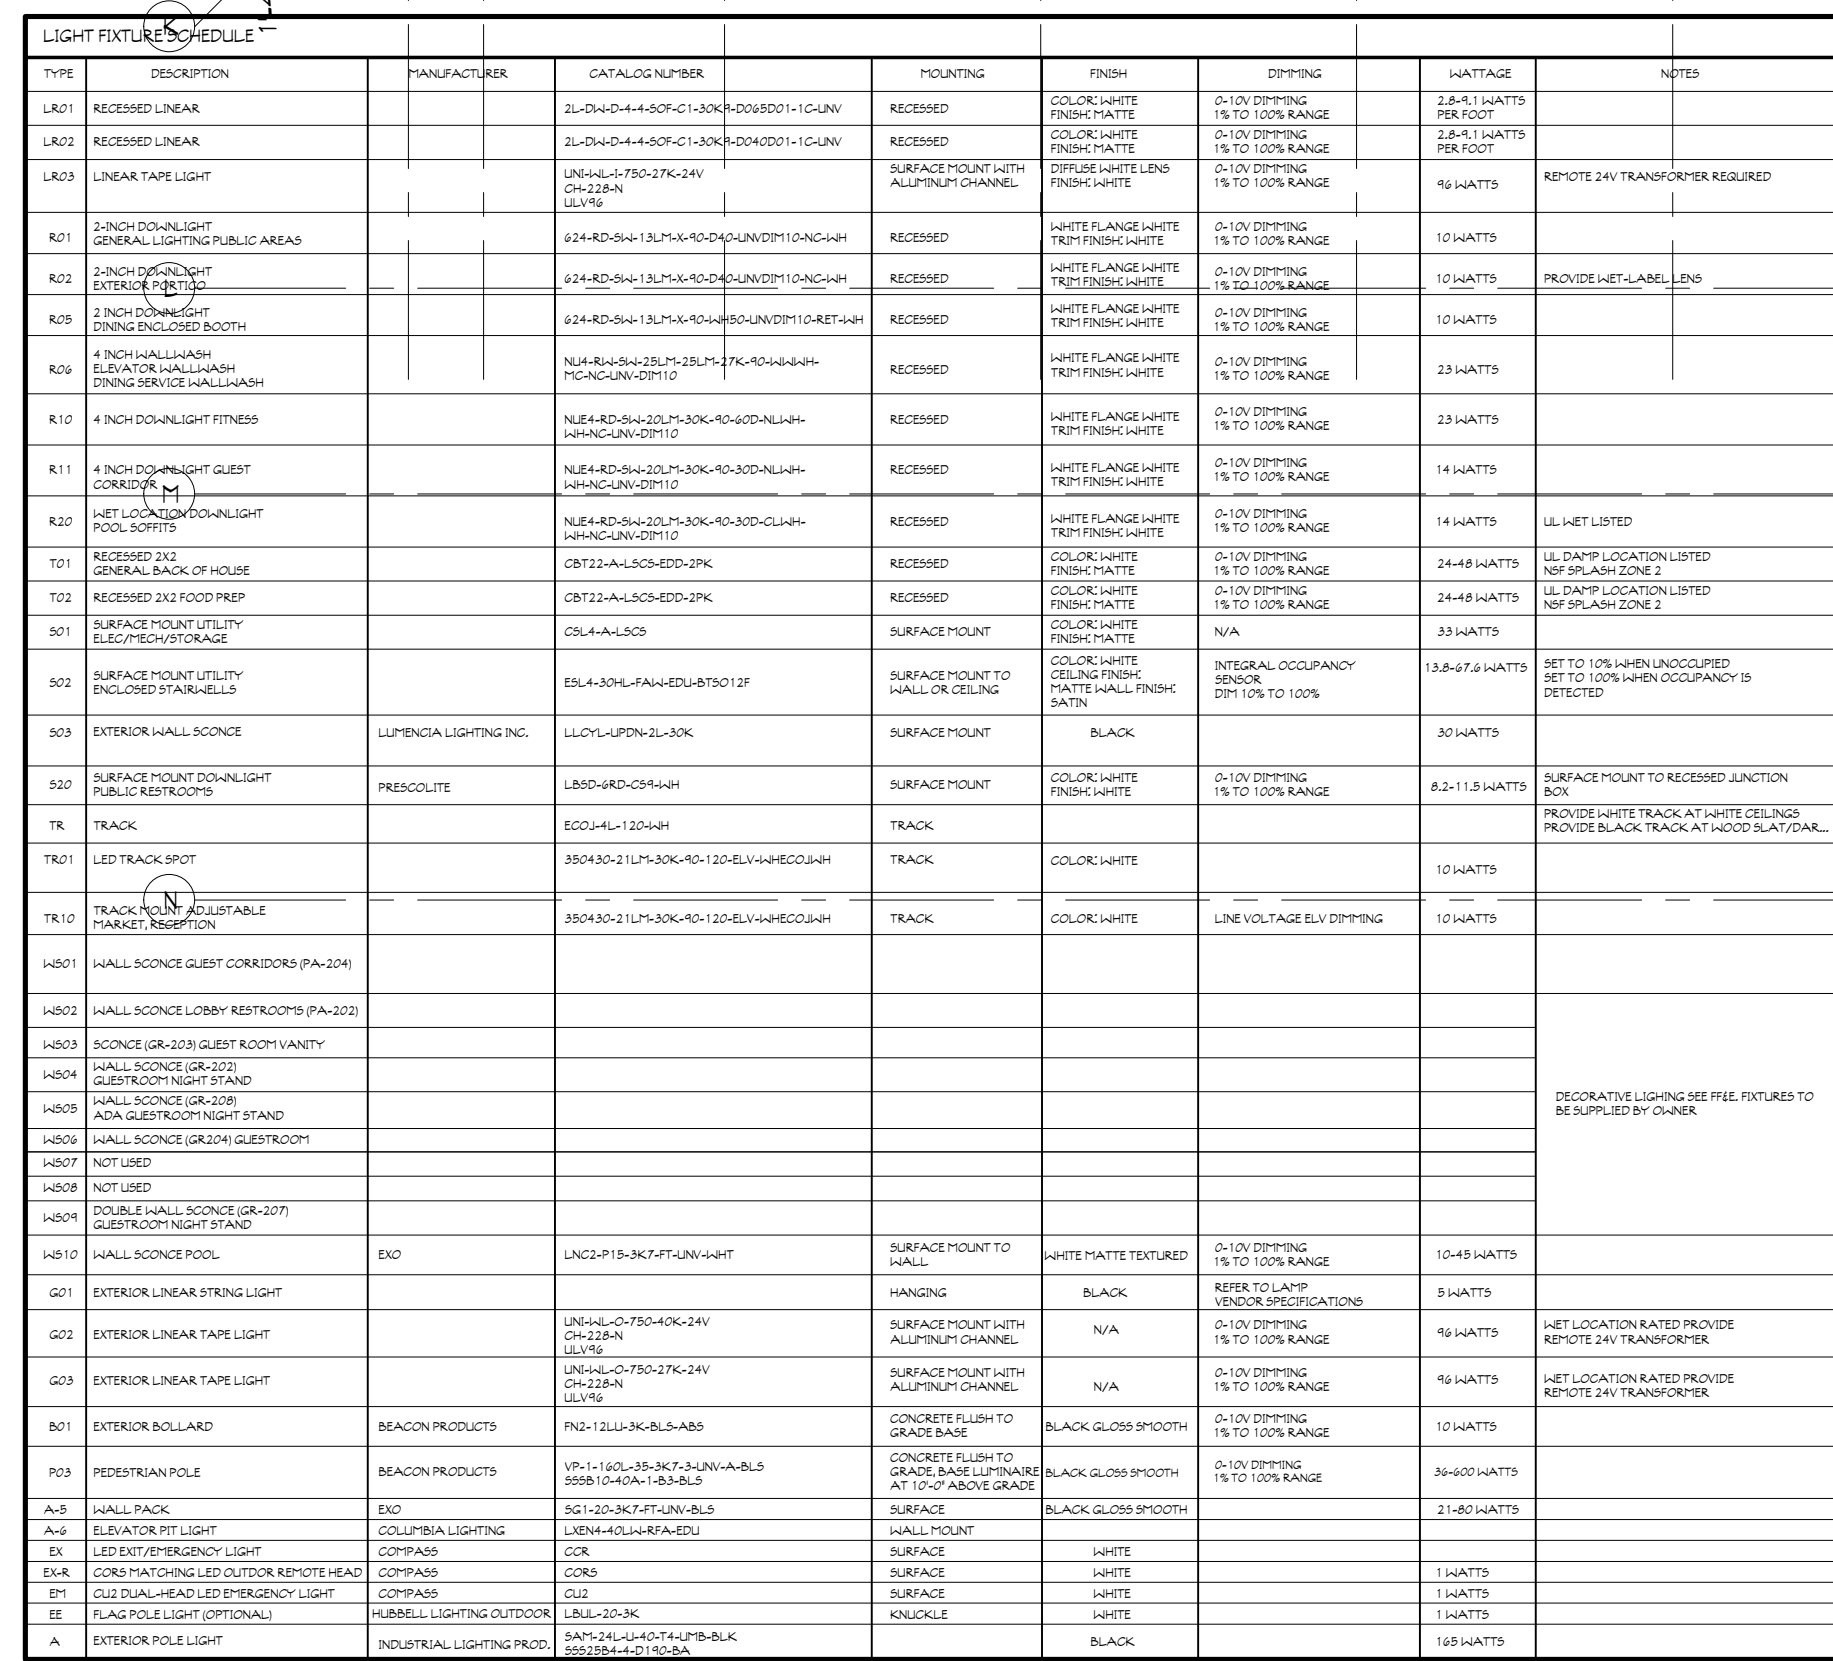

1 SECOND FLOOR LIGHTING PLAN
SCALE: 1/8" = 1'-0"

CEILING FIXTURE LEGEND:		SWITCH LEGEND:	
	2' x 2' LIGHT FIXTURE		CEILING MOUNTED OCCUPANCY SENSOR
	2' x 4' LIGHT FIXTURE		OCCUPANCY SWITCH
	1' x 4' LIGHT FIXTURE		SWITCH
	WALL MOUNTED LIGHT FIXTURE		DIMMING SWITCH
	WALL MOUNTED DECORATIVE SCONCE		KEYED SWITCH
	DOWN LIGHT		3-WAY SWITCH
	DOWN LIGHT, DIMMABLE, HOUSING TO MATCH STANDARD DOWN LIGHT		
	PENDANT LIGHT	EMERGENCY LIGHT LEGEND:	
	TRACK LIGHT		EMERGENCY EXIT LIGHT
	SMALL RECESSED DOWN LIGHT, NARROW BEAM SPREAD		EMERGENCY LIGHT
	EXTERIOR LIGHT STRING		EMERGENCY EXIT REMOTE HEAD
	EXTERIOR RECESS DOWN-LIGHT WALL WASHER (UL-WET LABELED)		SPEAKER
	EXTERIOR WALL PACK		VOLUME CONTROL



EFT'

E202