


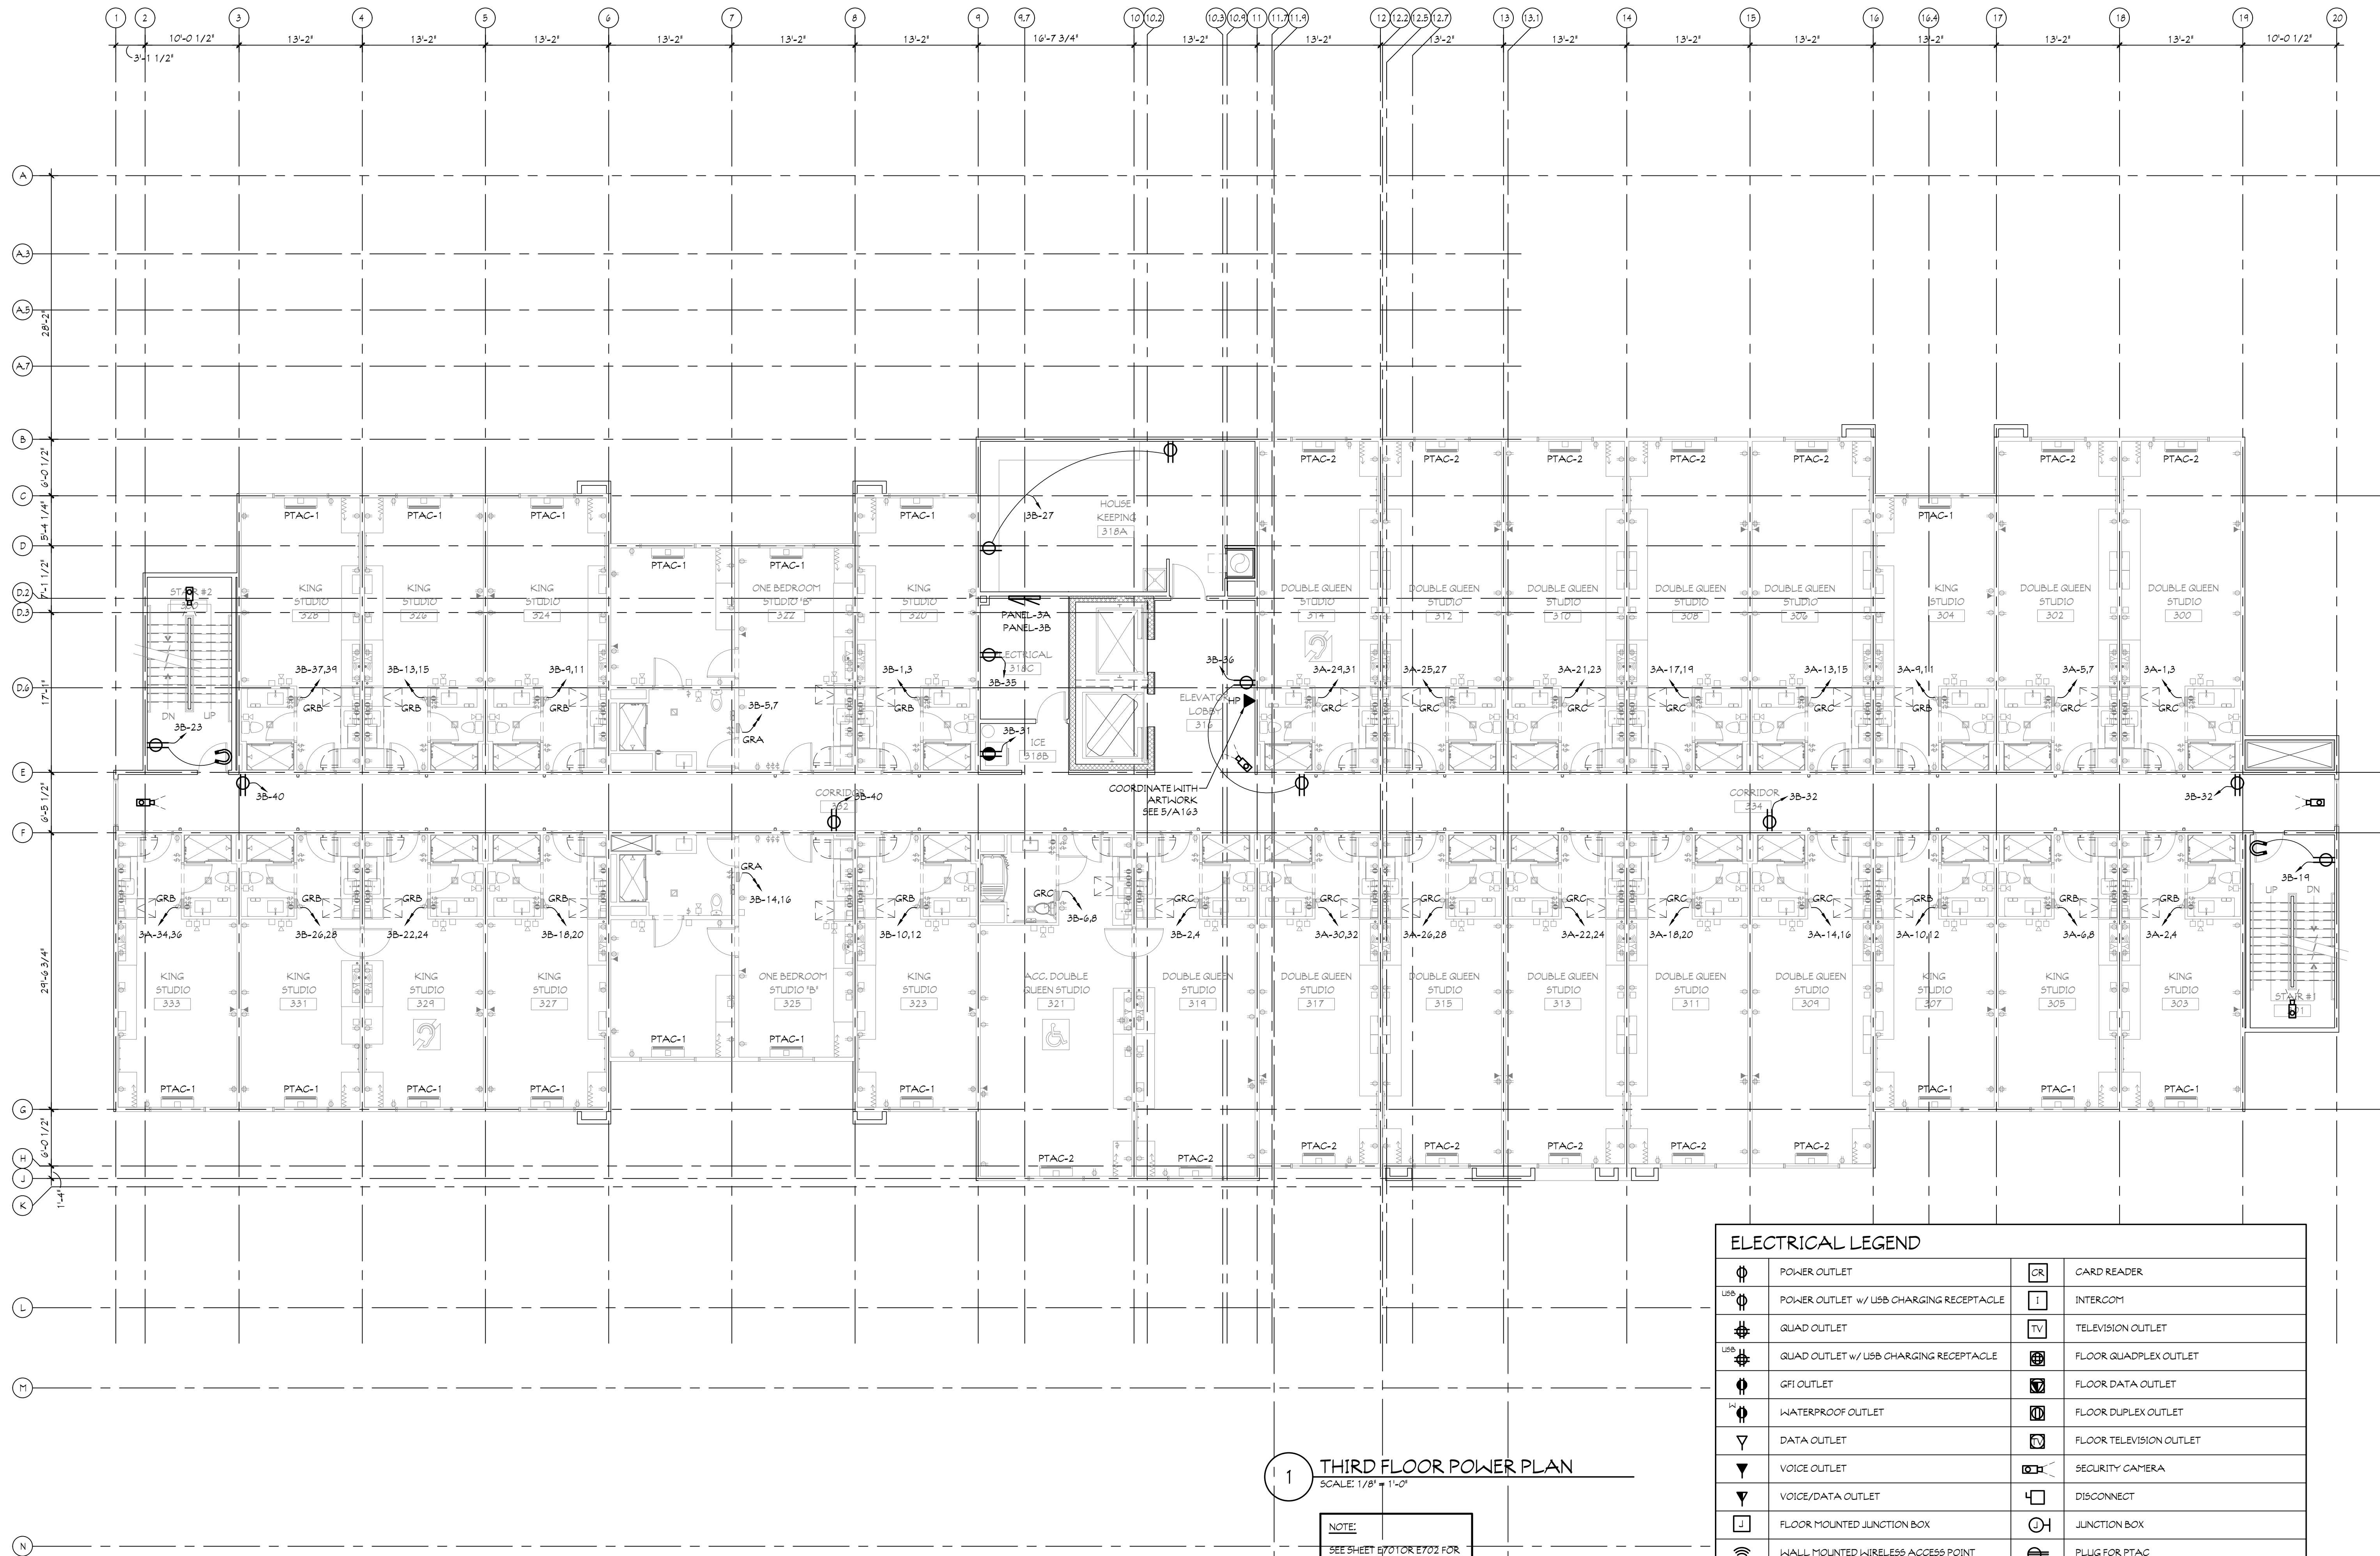

1 THIRD FLOOR POWER PLAN
SCALE: 1/8" = 1'-0"

NOTE:
SEE SHEET 670701E702 FOR
GUEST ROOM ELECTRICAL
INFORMATION
HEARING IMPAIRED ROOMS
ONLY TO RECEIVE DOORBELL
W/ A SWITCH

ELECTRICAL LEGEND			
	POWER OUTLET		CARD READER
	POWER OUTLET w/ USB CHARGING RECEPTACLE		INTERCOM
	QUAD OUTLET		TELEVISION OUTLET
	QUAD OUTLET w/ USB CHARGING RECEPTACLE		FLOOR QUADPLEX OUTLET
	GFI OUTLET		FLOOR DATA OUTLET
	WATERPROOF OUTLET		FLOOR DUPLEX OUTLET
	DATA OUTLET		FLOOR TELEVISION OUTLET
	VOICE OUTLET		SECURITY CAMERA
	VOICE/DATA OUTLET		DISCONNECT
	FLOOR MOUNTED JUNCTION BOX		JUNCTION BOX
	WALL MOUNTED WIRELESS ACCESS POINT		PLUG FOR PTAC
	HOUSE TELEPHONE OUTLET		SPECIALTY OUTLET
	MAGNETIC HOLD OPEN TIE INTO FIRE ALARM SYSTEM		

GENERAL NOTES

ALTHOUGH DRAWINGS ARE PREPARED TO SCALE, THE
ACCURACY OF THE DRAWINGS CANNOT BE
GUARANTEED. THE USER SHALL BE RESPONSIBLE FOR
OBTAINING ALL NECESSARY PERMITS AND
RIGHTS OF REPRODUCTION. DIMENSIONS SHOULD BE DELETED
FROM DIMENSIONED PLANS.
ALL DIMENSIONS INDICATED OPENING SIZES AND
LOCATIONS SHALL BE THE RESPONSIBILITY OF THE
GENERAL CONTRACTOR. "FAST ARCHITECTURAL"
SERVICES SHALL NOT BE HELD RESPONSIBLE FOR ANY
CONSTRUCTION DEFECTS OR OMISSIONS.
BROUGHT TO THEIR ATTENTION PRIOR TO
CONSTRUCTION.

Architects
Planners
Engineers
Construction Mgmt.
Rule 5 and MS4 Filing
PHONE: (574) 537-4500
FAX: (574) 537-0808

MAUST ARCHITECTURAL
SERVICES
DIVISION OF
L.E.M., INC.
112 NORTH MAIN STREET
GOSHEN, INDIANA 46526

These drawings are the property of Maust Architectural Services and may not be reprinted, copied
or used in any manner without the express written consent of Maust Architectural Services.

HOME 2
SUITES BY HILTON

SHEET SIZE 24x36

FT. WAYNE, INDIANA

REVISIONS:

PRELIMINARY - NOT
FOR CONSTRUCTION

DATE: 05/01/26
JOB NO.: MAS-26-105
NAME:
THIRD FLOOR POWER
PLAN
SHEET:
E301