


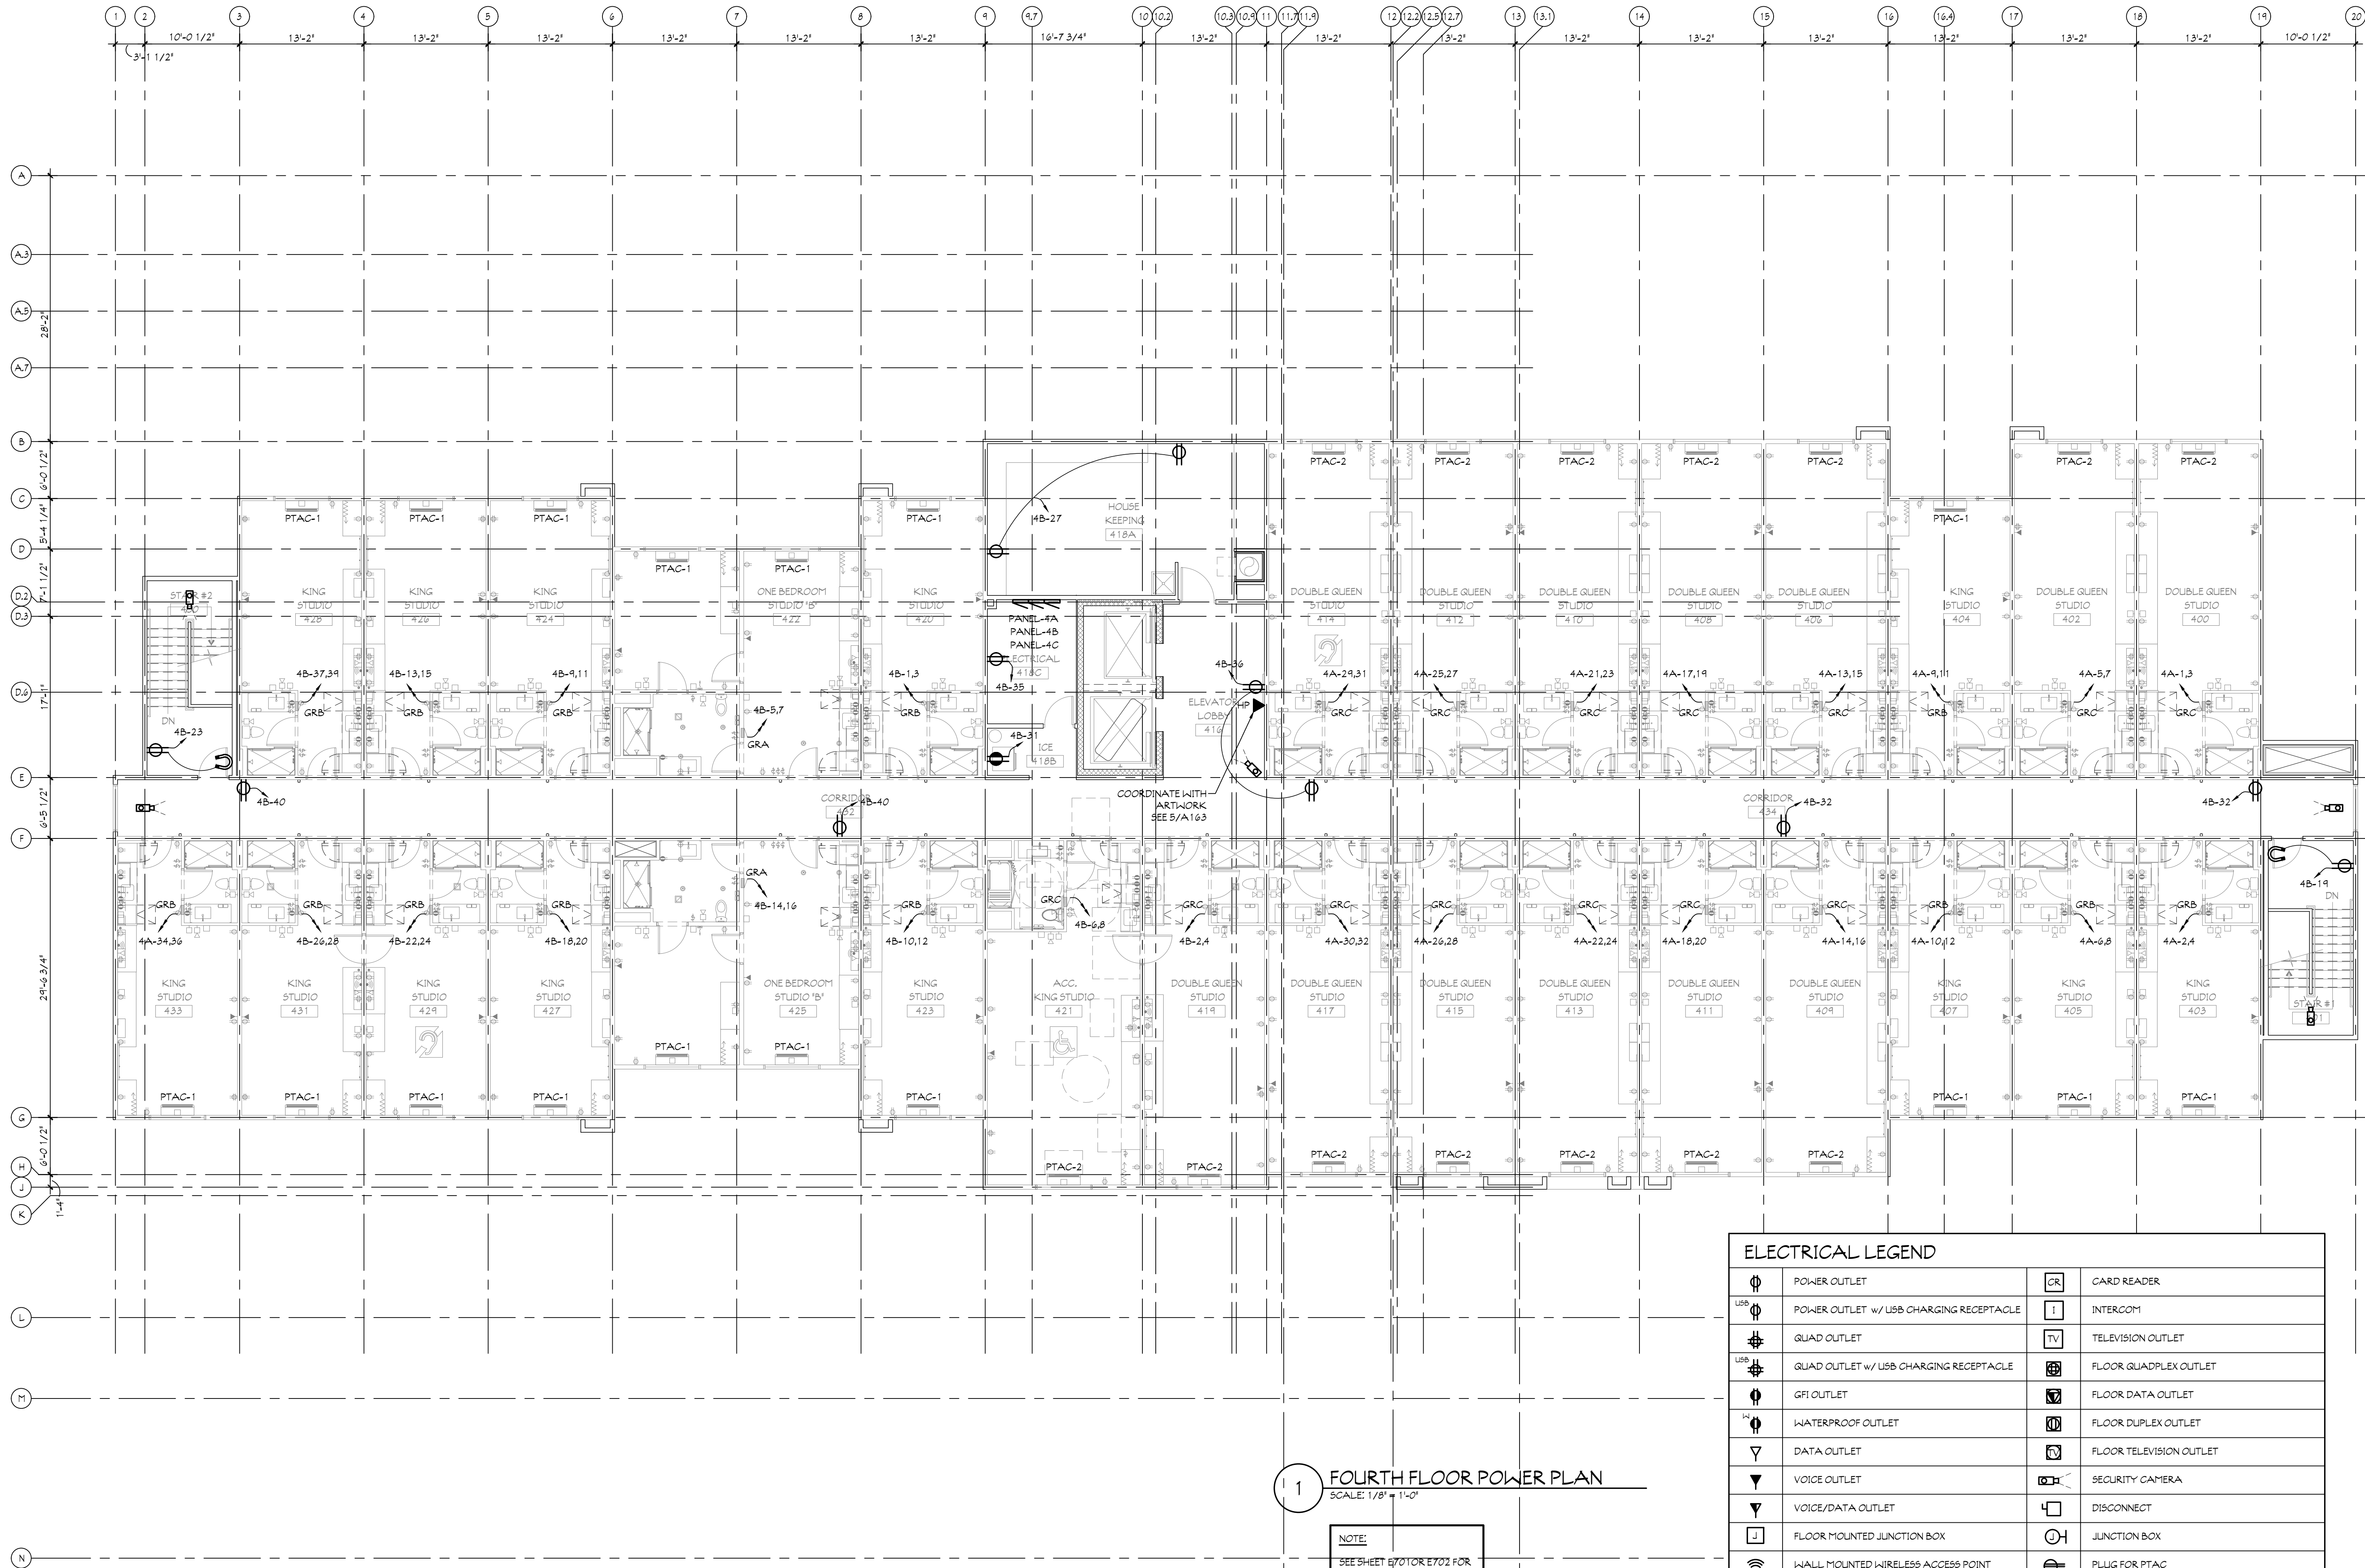

1 FOURTH FLOOR POWER PLAN
SCALE: 1/8" = 1'-0"

NOTE:
SEE SHEET E701 FOR GUEST ROOM ELECTRICAL INFORMATION.
HEARING IMPAIRED ROOMS ONLY TO RECEIVE DOORBELL W/ A SWITCH

ELECTRICAL LEGEND			
	POWER OUTLET		CARD READER
	POWER OUTLET w/ USB CHARGING RECEPTACLE		INTERCOM
	QUAD OUTLET		TELEVISION OUTLET
	QUAD OUTLET w/ USB CHARGING RECEPTACLE		FLOOR QUADPLEX OUTLET
	GFI OUTLET		FLOOR DATA OUTLET
	WATERPROOF OUTLET		FLOOR DUPLEX OUTLET
	DATA OUTLET		FLOOR TELEVISION OUTLET
	VOICE OUTLET		SECURITY CAMERA
	VOICE/DATA OUTLET		DISCONNECT
	FLOOR MOUNTED JUNCTION BOX		JUNCTION BOX
	WALL MOUNTED WIRELESS ACCESS POINT		PLUG FOR PTAC
	HOUSE TELEPHONE OUTLET		SPECIALTY OUTLET
	MAGNETIC HOLD OPEN TIE INTO FIRE ALARM SYSTEM		

GENERAL NOTES

ALTHOUGH DRAWINGS ARE PREPARED TO SCALE, THE ACCURACY OF THE DRAWINGS CANNOT BE GUARANTEED. THE USER SHALL BE RESPONSIBLE FOR VERIFYING ALL DIMENSIONS AND CONDITIONS PRIOR TO CONSTRUCTION. DIMENSIONS SHOWN ON THE DRAWINGS SHALL TAKE PRECEDENCE OVER ANY CONFLICTING DIMENSIONS ON ANY OTHER DRAWINGS.

ALL DIMENSIONS ARE TO FACE UNLESS OTHERWISE NOTED. 

MAUST ARCHITECTURAL SERVICES, INC.
112 NORTH MAIN STREET
GOSHEN, INDIANA 46526
PHONE: (574) 537-4500
FAX: (574) 537-0808

Architects
Planners
Engineers
Construction Mgmt.
Rule 5 and MS4 Filing

MAUST ARCHITECTURAL SERVICES, INC.
DIVISION OF L.E.M., INC.
112 NORTH MAIN STREET
GOSHEN, INDIANA 46526
PHONE: (574) 537-4500
FAX: (574) 537-0808

These drawings are the property of Maust Architectural Services, Inc. and may not be reprinted, copied, or used in any manner without the express written consent of Maust Architectural Services, Inc.

FT. WAYNE, INDIANA

REVISIONS:

DATE: 05/01/26
JOB NO.: MAS-26-105
NAME: FOURTH FLOOR POWER PLAN
SHEET: E401