



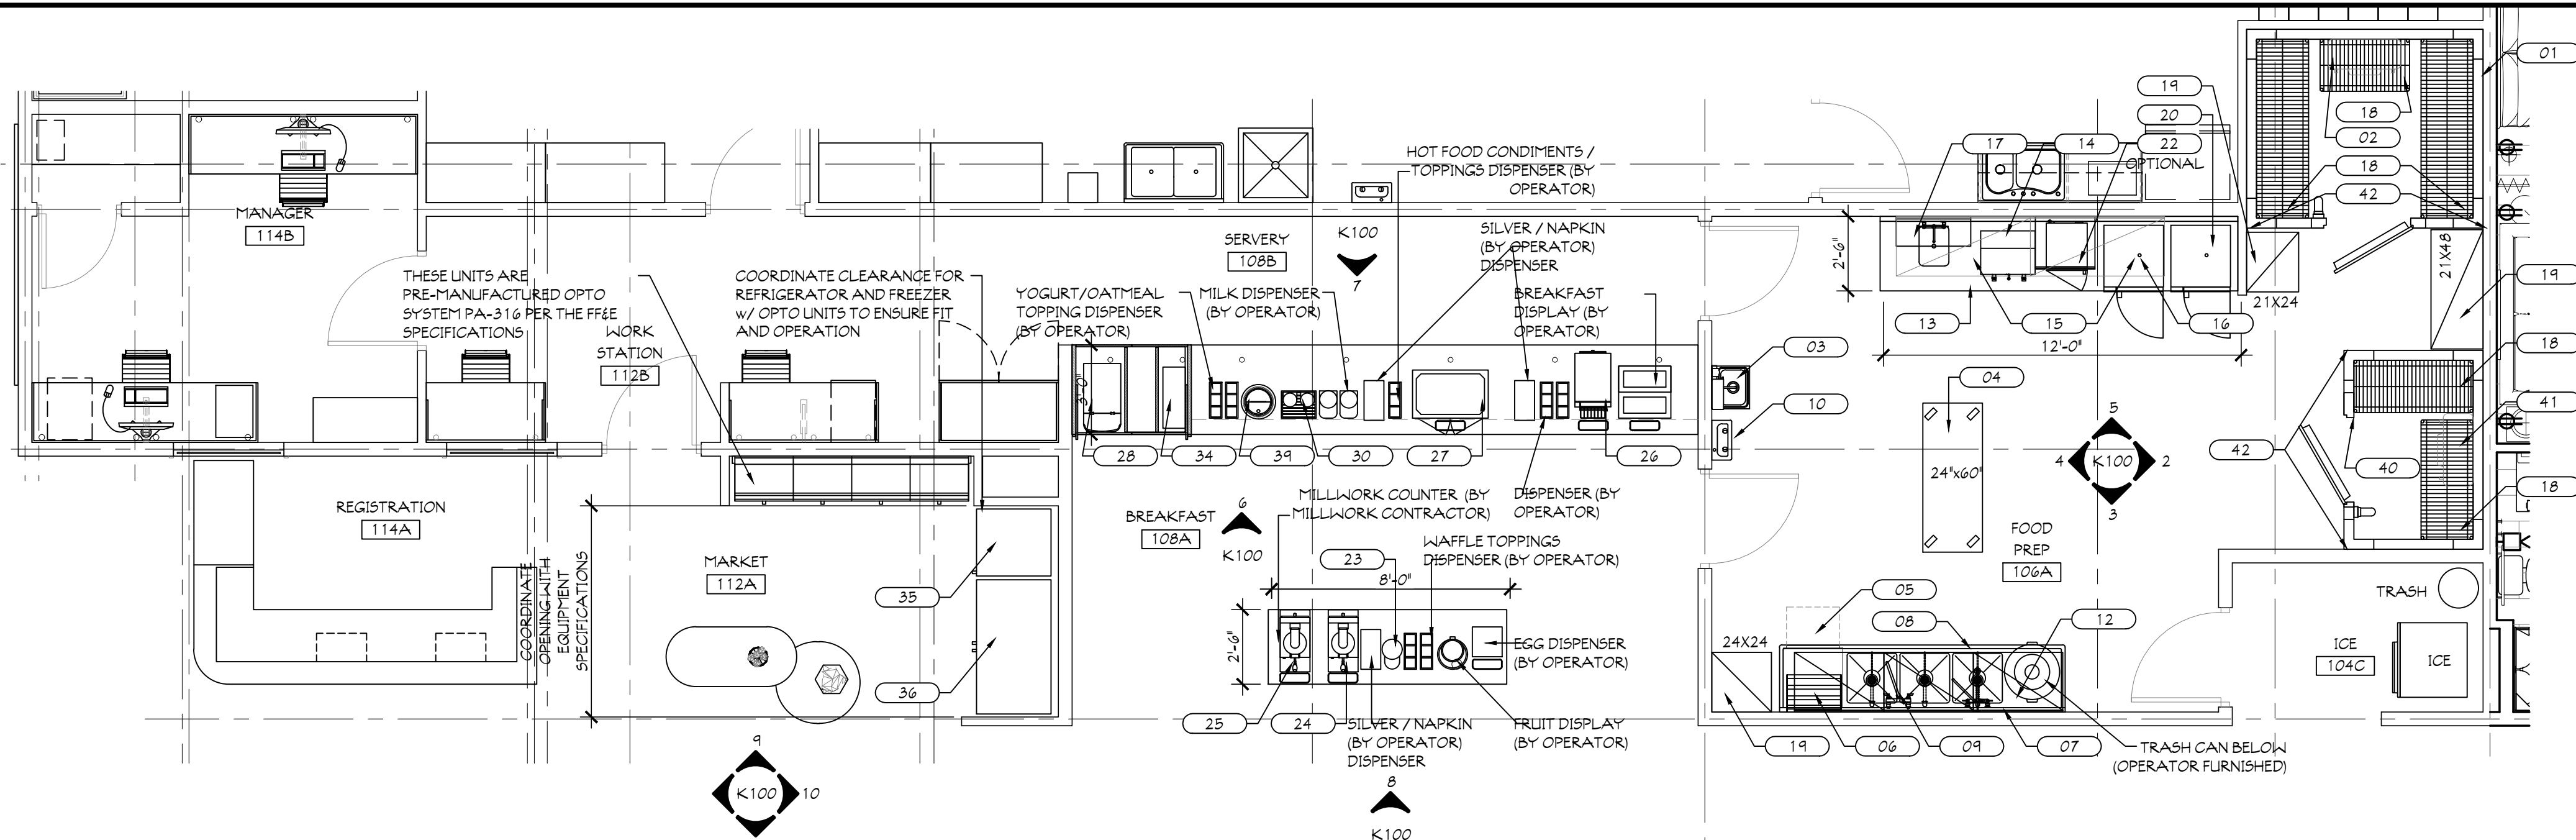


1 ENLARGED EQUIPMENT FLOOR PLAN
SCALE: 1/4" = 1'-0"


ITEM	QTY	DESCRIPTION	MANUFACTURER	MODEL
01	1	WALK-IN COOLER	AMERICAN PANEL / PER PLAN	
02	1	REFRIGERATION SYSTEM +35F	AMERICAN PANEL / PER PLAN	
03	1	HAND SINK W/ AUTO. SOAP AND TOWEL DISPENSER	ADVANCE TABCO	7-PS-87
04	1	MOBILE WORK TABLE	CUSTOM FABRICATED	
05	1	UNDERCOUNTER DISHWASHER (HIGH TEMP)	CHAMPION	UH-230B
06	1	DISH TABLE RACK SHELF	ADVANCE TABCO	DT-6R-11
07	3	WALL SHELF (HIGH MOUNT)	METRO	1ND24K3/2ND24K3/2436NK3
08	1	DISH / POT WASHING SINKS	CUSTOM FABRICATED	
09	1	PRE-RINSE W/ FAUCET	T15 BRASS	B-2278-A12-E1
10	1	EYE WASH STATION	HAAS	7360BT-7460BT
11	-	SPARE NUMBER		
12	1	UTENSIL RACK W/ SHELF	ADVANCE TABCO	PS-12-60
13	1	WORKTABLE WITH SINK	CUSTOM FABRICATED	
14	1	COFFEE MAKER (OPERATOR FURNISHED)	FETCO	CB5-2152XT5
15	2	WALL SHELF (HIGH MOUNT)	METRO	1ND24K3/2436NK3
16	1	CONVECTION OVEN (VENT LESS)	MOFFAT (TURBOFAN)	E33D5H2
17	2	WALL SHELF	CUSTOM FABRICATED	
18	5	SHELVING - DRY STORAGE SHELVING	METRO / SUPER ERECT A BRITE	
19	3	STORAGE SHELVING	METRO	METROMAX G
20	1	CONVECTION OVEN (VENTLESS) (OPTIONAL)	MOFFAT (TURBOFAN)	E33D5H2
21	-	SPARE NUMBER		
22	1	MICROWAVE OVEN WITH SHELF (OPTIONAL)	AMANA	HDC12A2/BN152024
23	1	BATTER MIX STARTER KIT (OPERATOR FURNISHED)		
24	1	WAFFLE MAKER	GOLDEN MALTED	RT SERIES
25	1	WAFFLE MAKER (FUTURE)	GOLDEN MALTED	RT SERIES
26	1	CONVEYOR TOASTER	APIA WYOTT	ECO 4000-350L-HILTON
27	1	DISPLAY SHOWCASE	EQUIPEX	WD780B-2/1
28	1	JUICE DISPENSER (BY VENDOR)	NESTLE VITALITY	EXPRE55
29	-	WARMING KETTLE (OPTIONAL)	VOLLRATH	72017
30	1	CEREAL DISPENSER	ROSETTO	EZP2135
31	-	SPARE NUMBER	PERLICK	HD24R54
32	-	SPARE NUMBER		
33	-	SPARE NUMBER		
34	1	YOGURT DISPENSER (BY VENDOR)	PERFECT PARFAIT	PPHG1BK
35	1	REACH-IN DISPLAY FREEZER	TRUE	T5-23FG-HC-FGD01
36	1	REACH-IN DISPLAY REFRIGERATOR	TRUE	T5D-47G-HC-LD
37	1	WATER DISPENSER	MARCO	FR1A HC5
38	2	COFFEE DISPENSER (OPERATOR FURNISHED)	FETCO	D449
39	1	WARMING KETTLE (DROP-IN)	VOLLRATH	741101DW
40	1	WALK-IN FREEZER	AMERICAN PANEL / PER PLAN	
41	1	FREEZER SYSTEM -80F TO +32F	AMERICAN PANEL / PER PLAN	
42	-	CORNER GUARDS AND FLASH TRIM	FABRICATORY / SS	

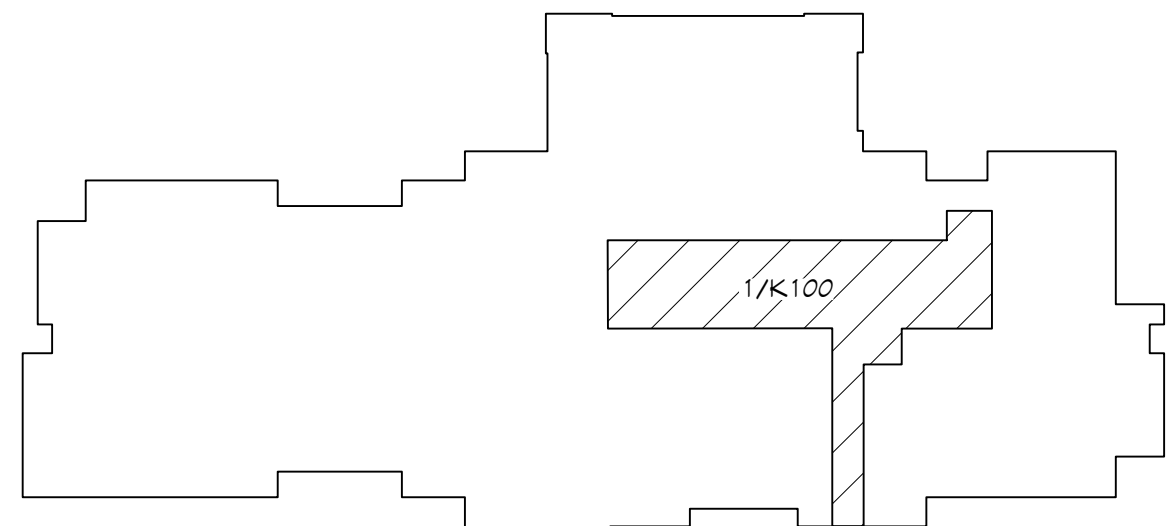


11 FIRST FLOOR KEY PLAN
SCALE: NOT TO SCALE

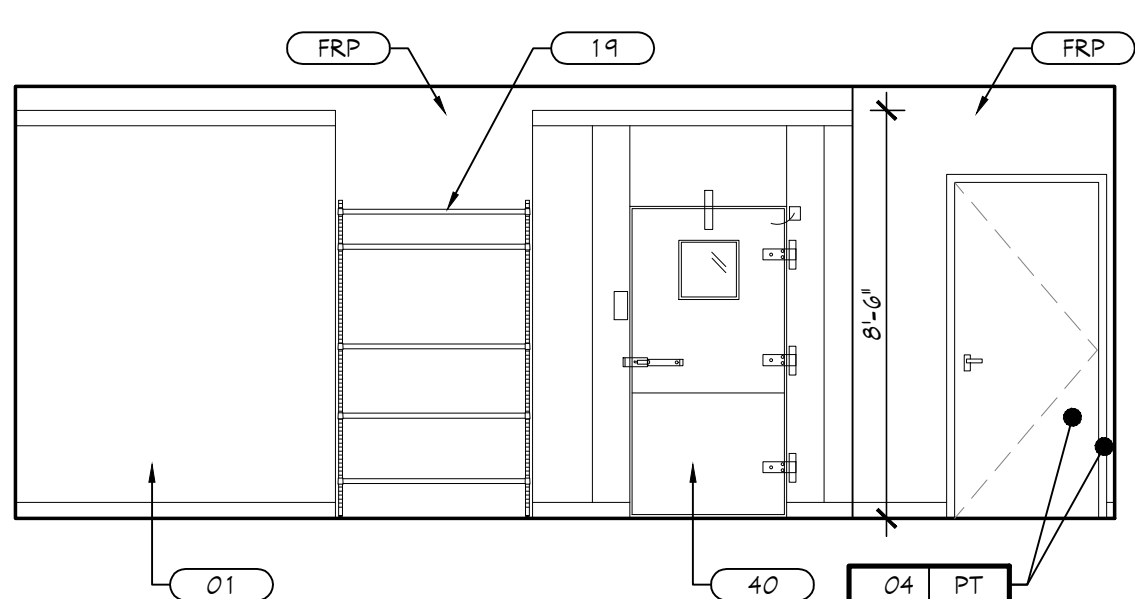


2 ELEVATION
SCALE: 1/4" = 1'-0"

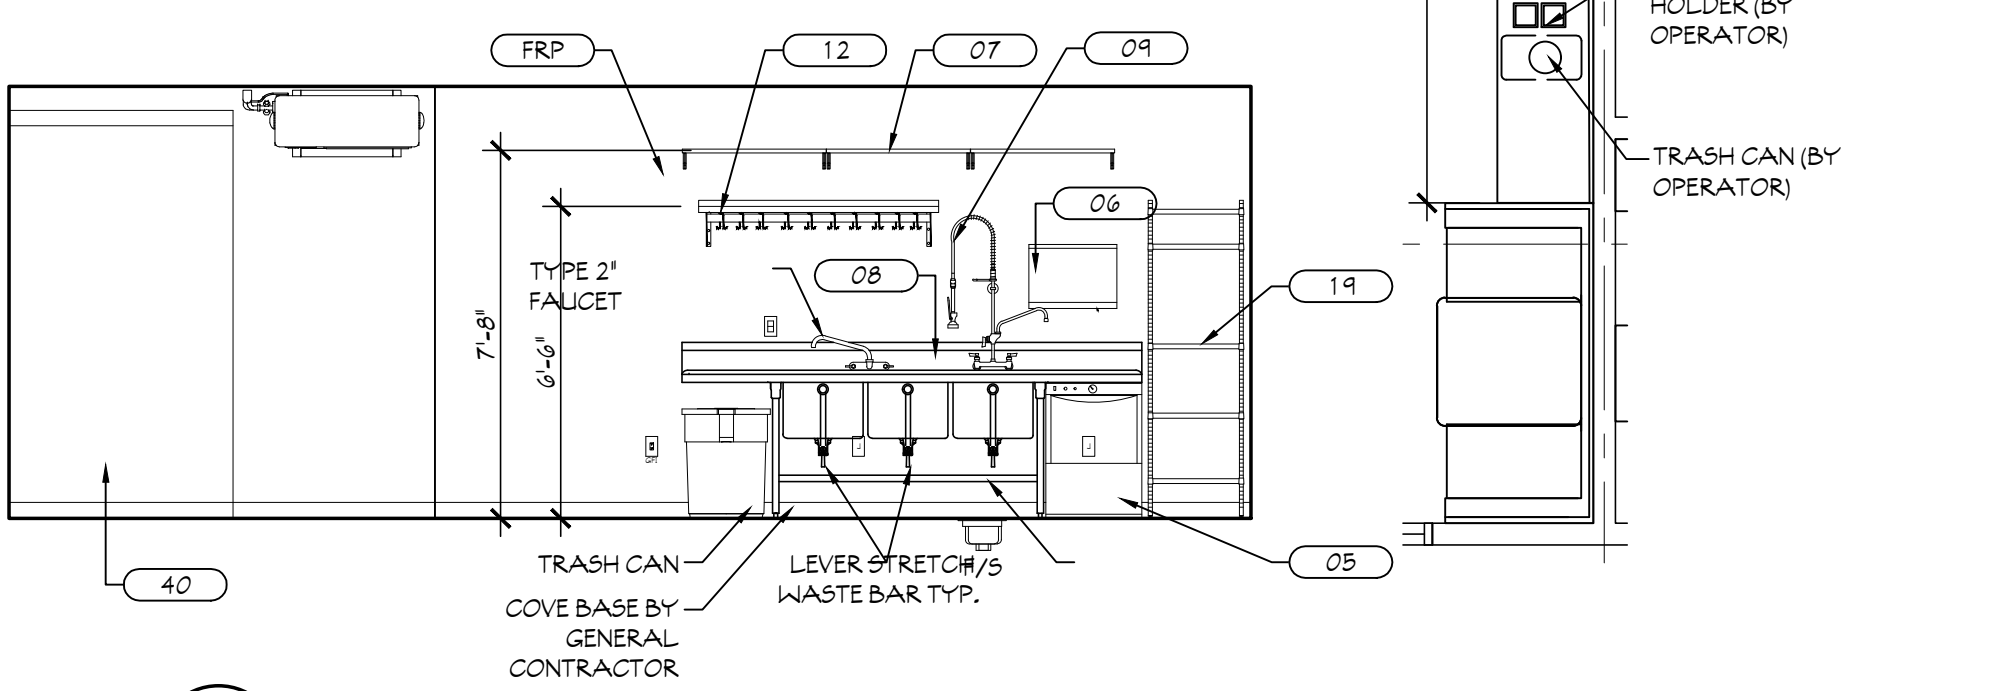


3 ELEVATION
SCALE: 1/4" = 1'-0"

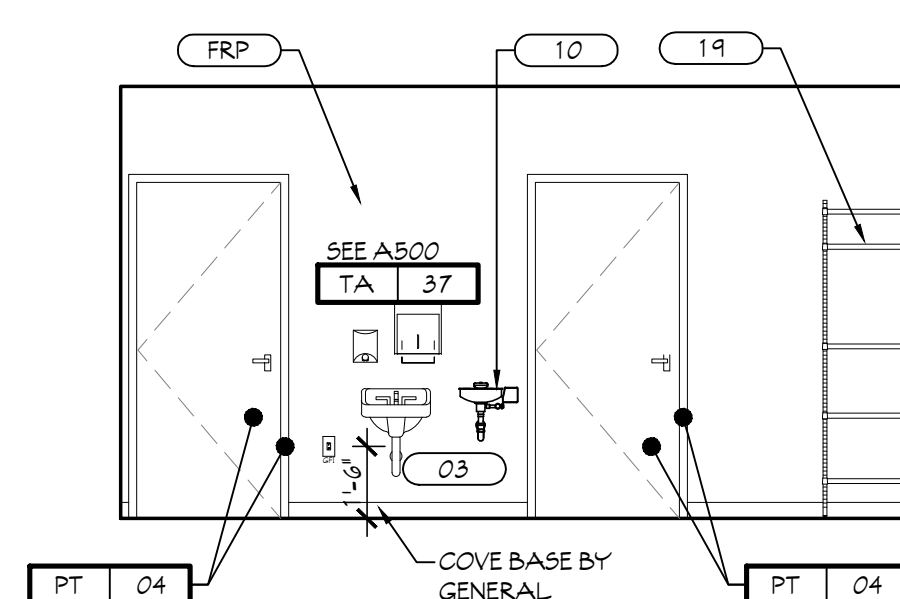


4 ELEVATION
SCALE: 1/4" = 1'-0"

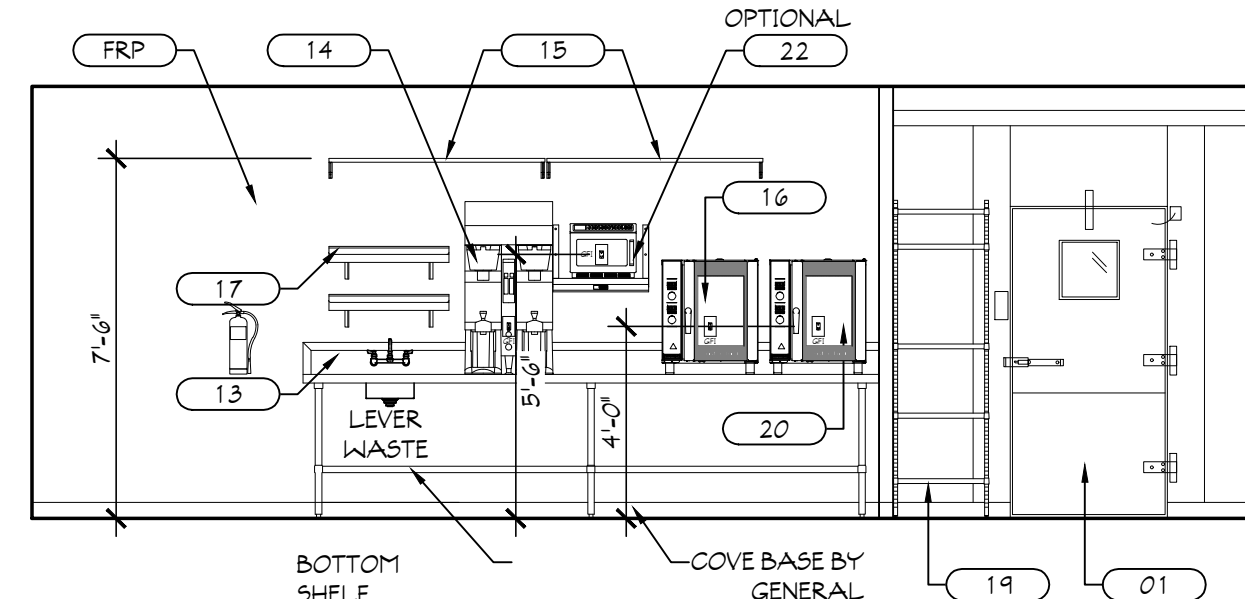


5 ELEVATION
SCALE: 1/4" = 1'-0"

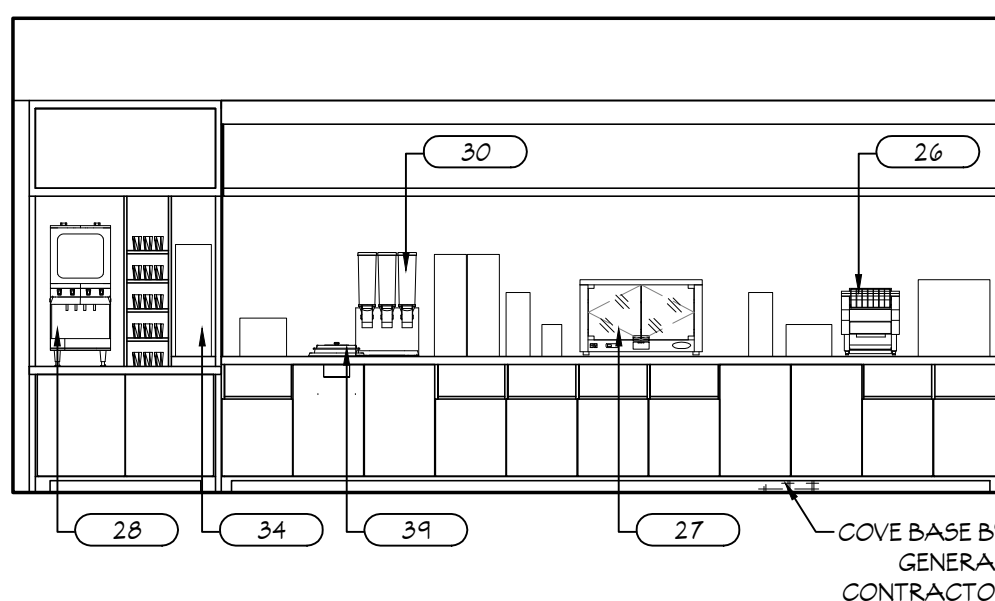


6 ELEVATION
SCALE: 1/4" = 1'-0"

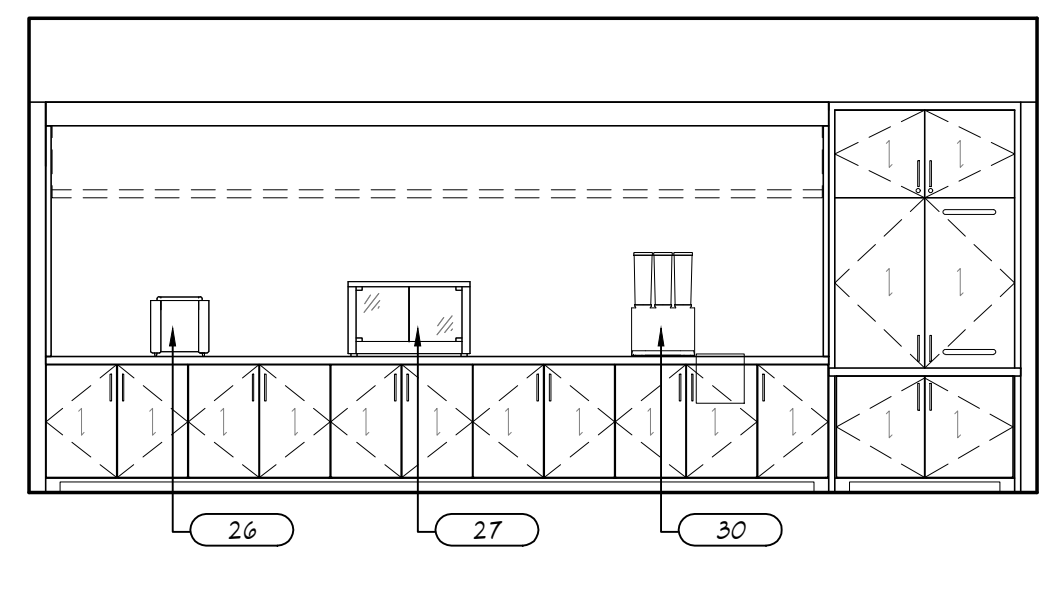

7 ELEVATION
SCALE: 1/4" = 1'-0"

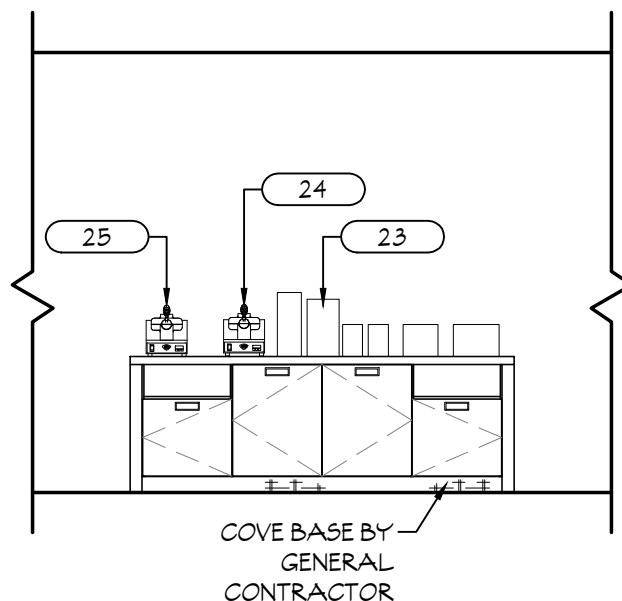

8 ELEVATION
SCALE: 1/4" = 1'-0"

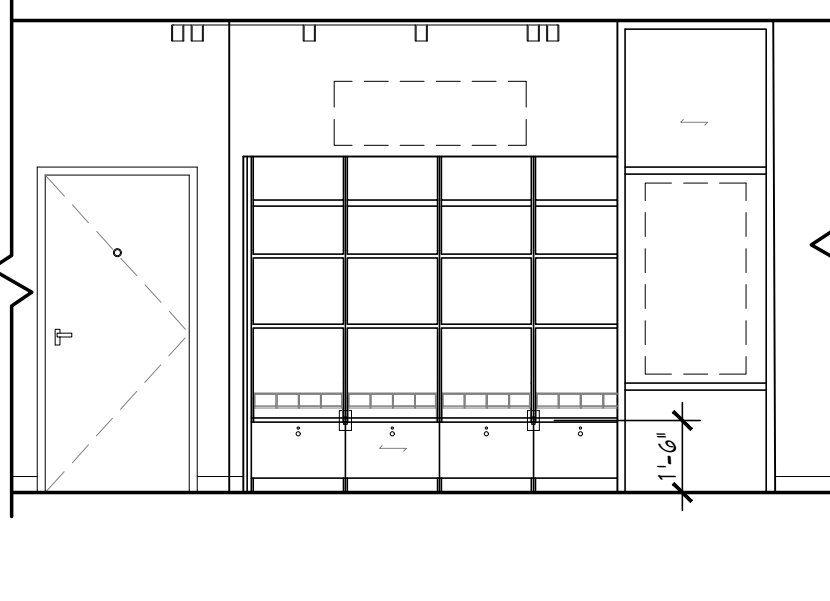

9 ELEVATION
SCALE: 1/4" = 1'-0"



10 ELEVATION
SCALE: 1/4" = 1'-0"

GENERAL NOTES

* Architects
* Plumbers
* Electricians
* Construction Mgmt.

MAUST ARCHITECTURAL SERVICES
DIVISION OF
L.E.M., INC.
112 NORTH MAIN STREET
GOSHEN, INDIANA 46526

HOME 2
SUITES BY HILTON

SHEET SIZE 24x36

FT. WAYNE, INDIANA

REVISIONS:

PRELIMINARY - NOT FOR CONSTRUCTION

DATE: 05/01/26

JOB NO.: MAS-26-105

NAME:

KITCHEN EQUIPMENT PLAN

SHEET:

K100