


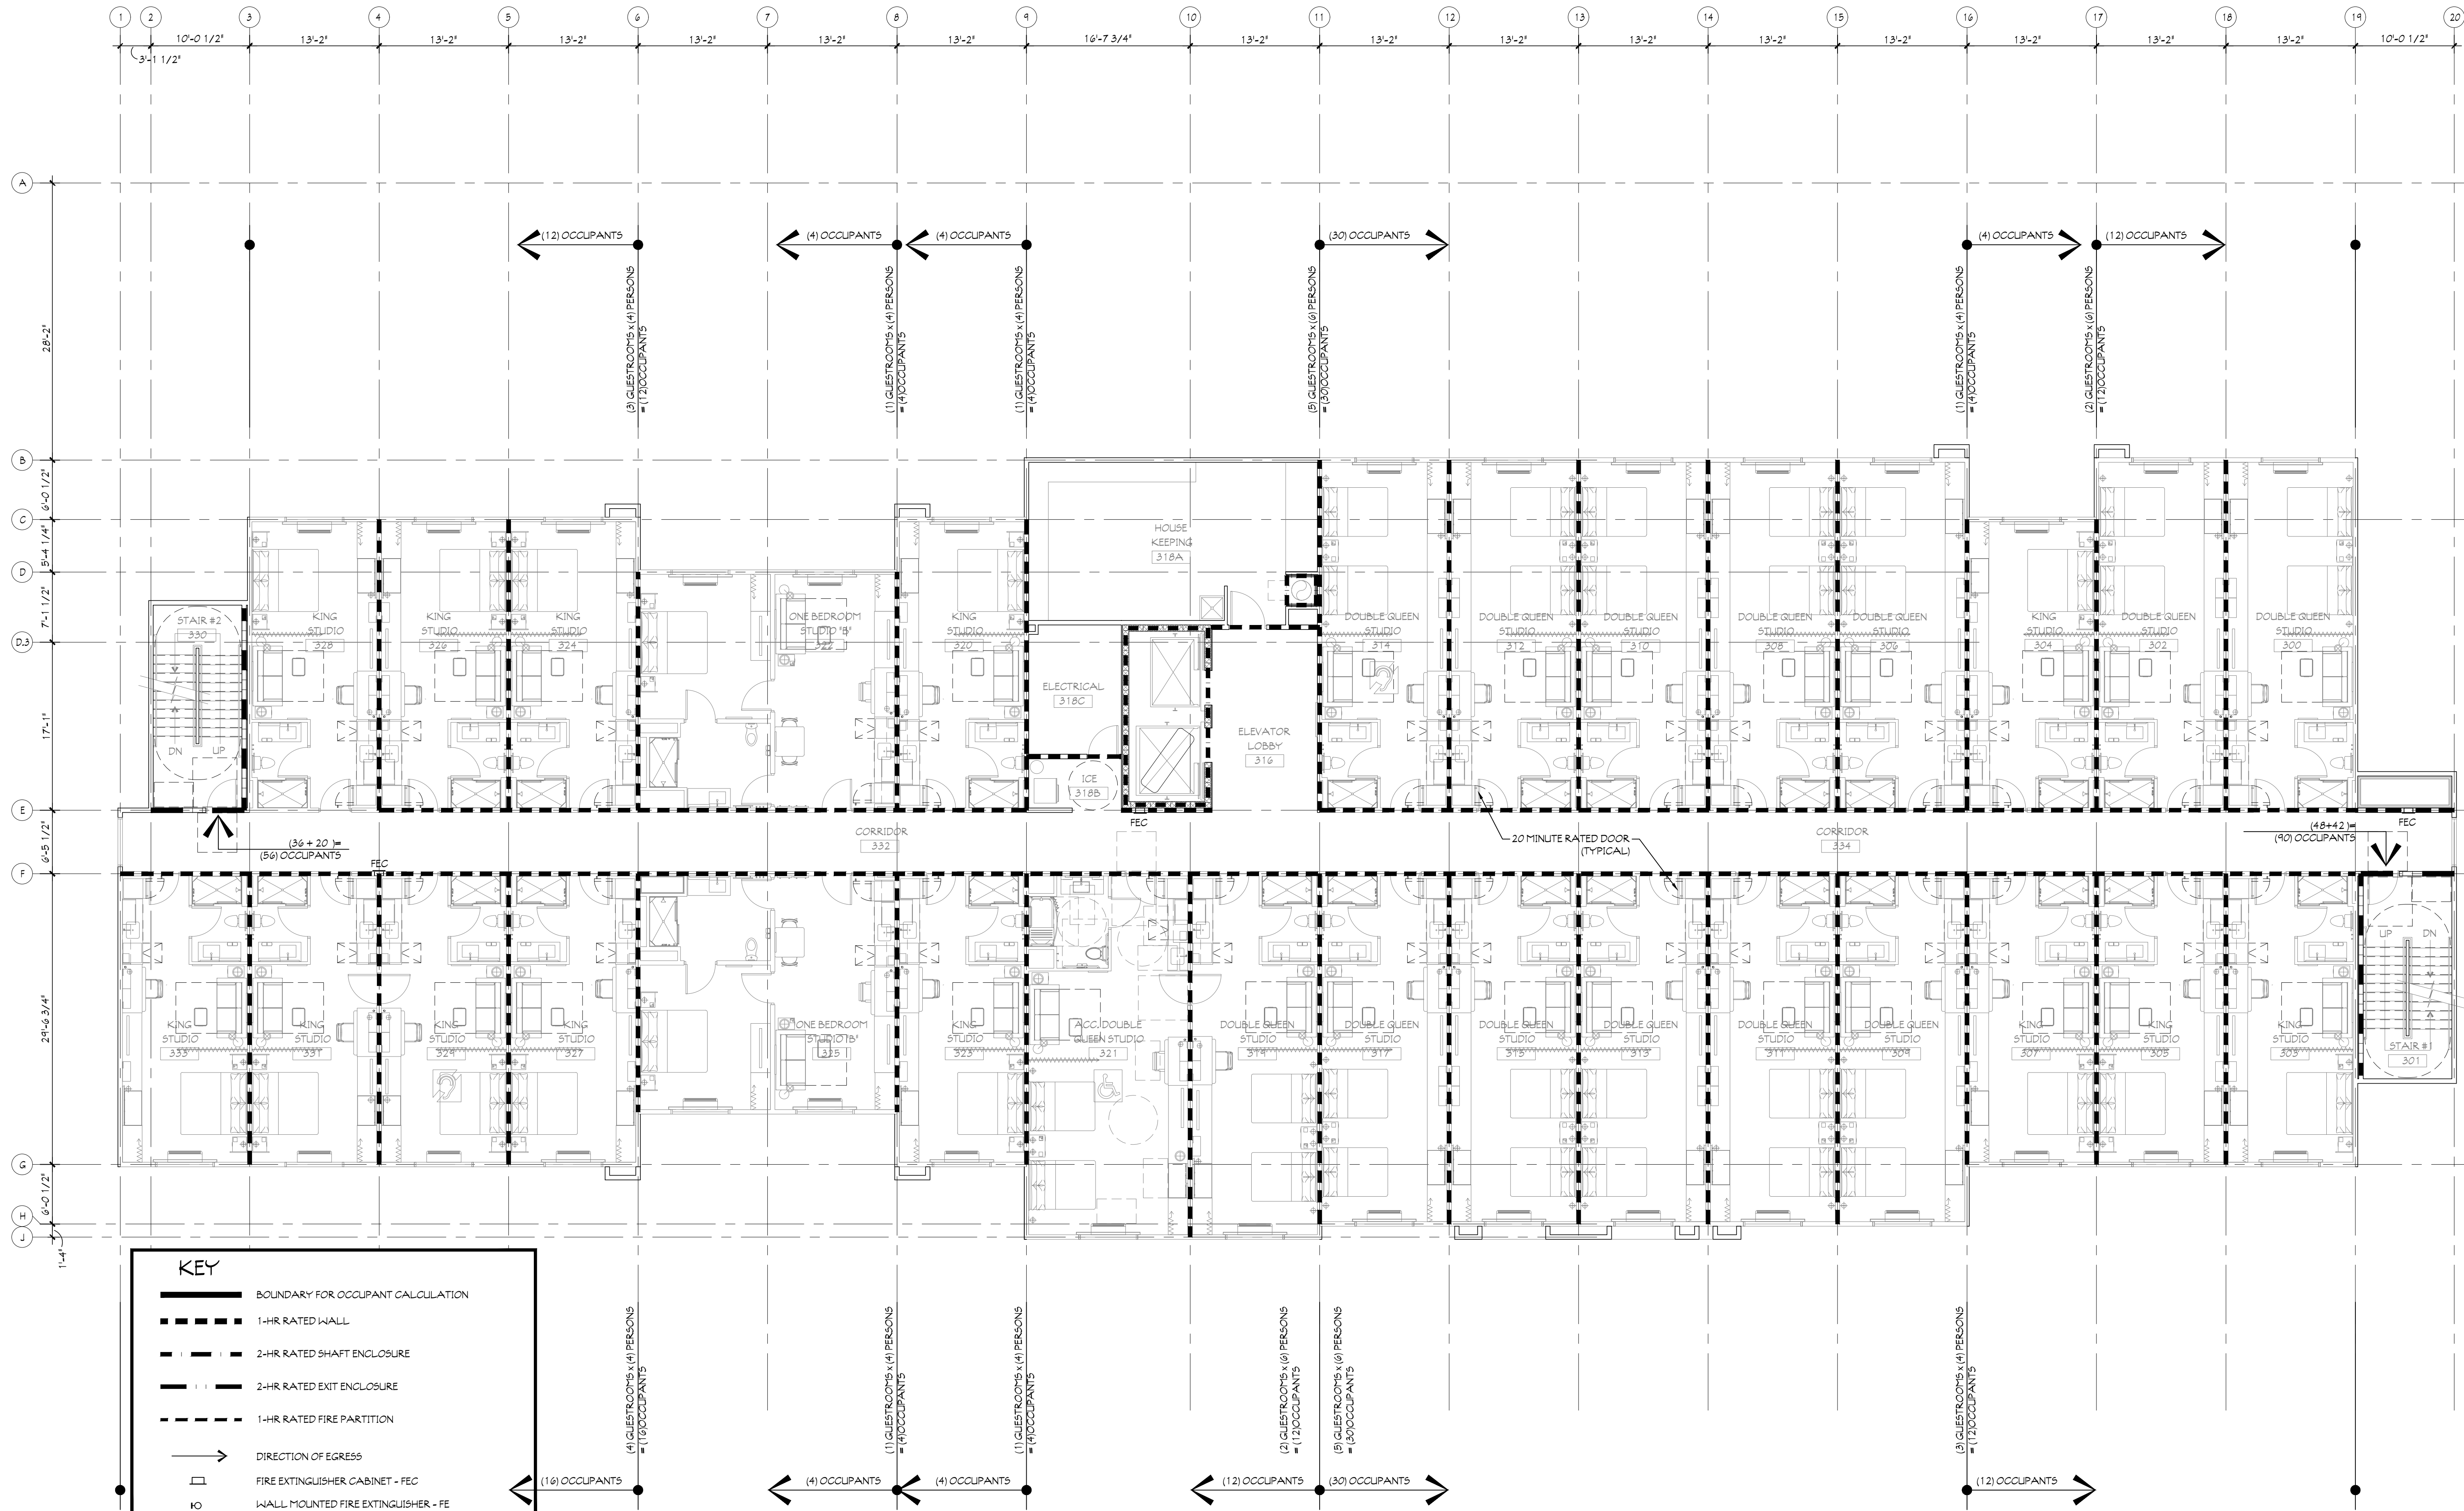

KEY

- BOUNDARY FOR OCCUPANT CALCULATION
- 1-HR RATED WALL
- 2-HR RATED SHAFT ENCLOSURE
- 2-HR RATED EXIT ENCLOSURE
- 1-HR RATED FIRE PARTITION
- DIRECTION OF EGRESS
- FIRE EXTINGUISHER CABINET - FEC
- WALL MOUNTED FIRE EXTINGUISHER - FE

GENERAL NOTES:

- FLOOR / CEILING ASSEMBLY IS 1-HR RATED
- OCCUPANT LOAD IN GUESTROOMS IS ASSUMED TO BE (2) GUESTS PER ROOM - (4) OR (6) GUESTS PER ROOM SUITE
- SEE THE DOOR SCHEDULE FOR RATINGS OF INDIVIDUAL DOORS.
- INSTALL AREA OF RESCUE ASSISTANCE SYSTEM - THE SYSTEM SHALL BE PROVIDED WITH BOTH VISIBLE AND AUDIBLE SIGNALS BETWEEN EACH AREA OF RESCUE ASSISTANCE AND PRIMARY ENTRY/CHECK-IN ENTRANCE

1 THIRD FLOOR LIFE SAFETY PLAN
SCALE: 1/8" = 1'-0"

GENERAL NOTES

ALTHOUGH DRAWINGS ARE PREPARED TO SCALE, THE ACCURACY OF THE DRAWINGS CANNOT BE GUARANTEED. THE USER SHALL VERIFY ALL DIMENSIONS AND CONDITIONS PRIOR TO CONSTRUCTION. DIMENSIONS SHOULD BE DELETED FROM PRELIMINARY PLANS.

ALL DIMENSIONS FOR OPENING SIZES AND FINISHES SHALL BE THE RESPONSIBILITY OF THE GENERAL CONTRACTOR. THE ARCHITECT SHALL NOT BE RESPONSIBLE FOR ANY CONSTRUCTION DETAILS OR CONDITIONS NOT SHOWN OR BROUGHT TO THEIR ATTENTION PRIOR TO CONSTRUCTION.

Architects
* MAUST ARCHITECTURAL SERVICES, INC.
* 112 NORTH MAIN STREET
* GOSHEN, INDIANA 46526
* PHONE: (574) 537-4500
* FAX: (574) 537-0808

Plumbers
* Rule 5 and MS4 Filing

MAUST ARCHITECTURAL SERVICES, INC.
DIVISION OF
L.E.M., INC.
112 NORTH MAIN STREET
GOSHEN, INDIANA 46526

These drawings are the property of Maust Architectural Services, Inc. and may not be reprinted, copied, or used in any manner without written consent of Maust Architectural Services, Inc.

HOME 2
SUITES BY HILTON

SHEET SIZE 24x36

FT. WAYNE, INDIANA

REVISIONS:

PRELIMINARY - NOT FOR CONSTRUCTION

DATE: 05/01/26
JOB NO.: MAS-26-105
NAME: THIRD FLOOR LIFE SAFETY PLAN
SHEET: LS103