


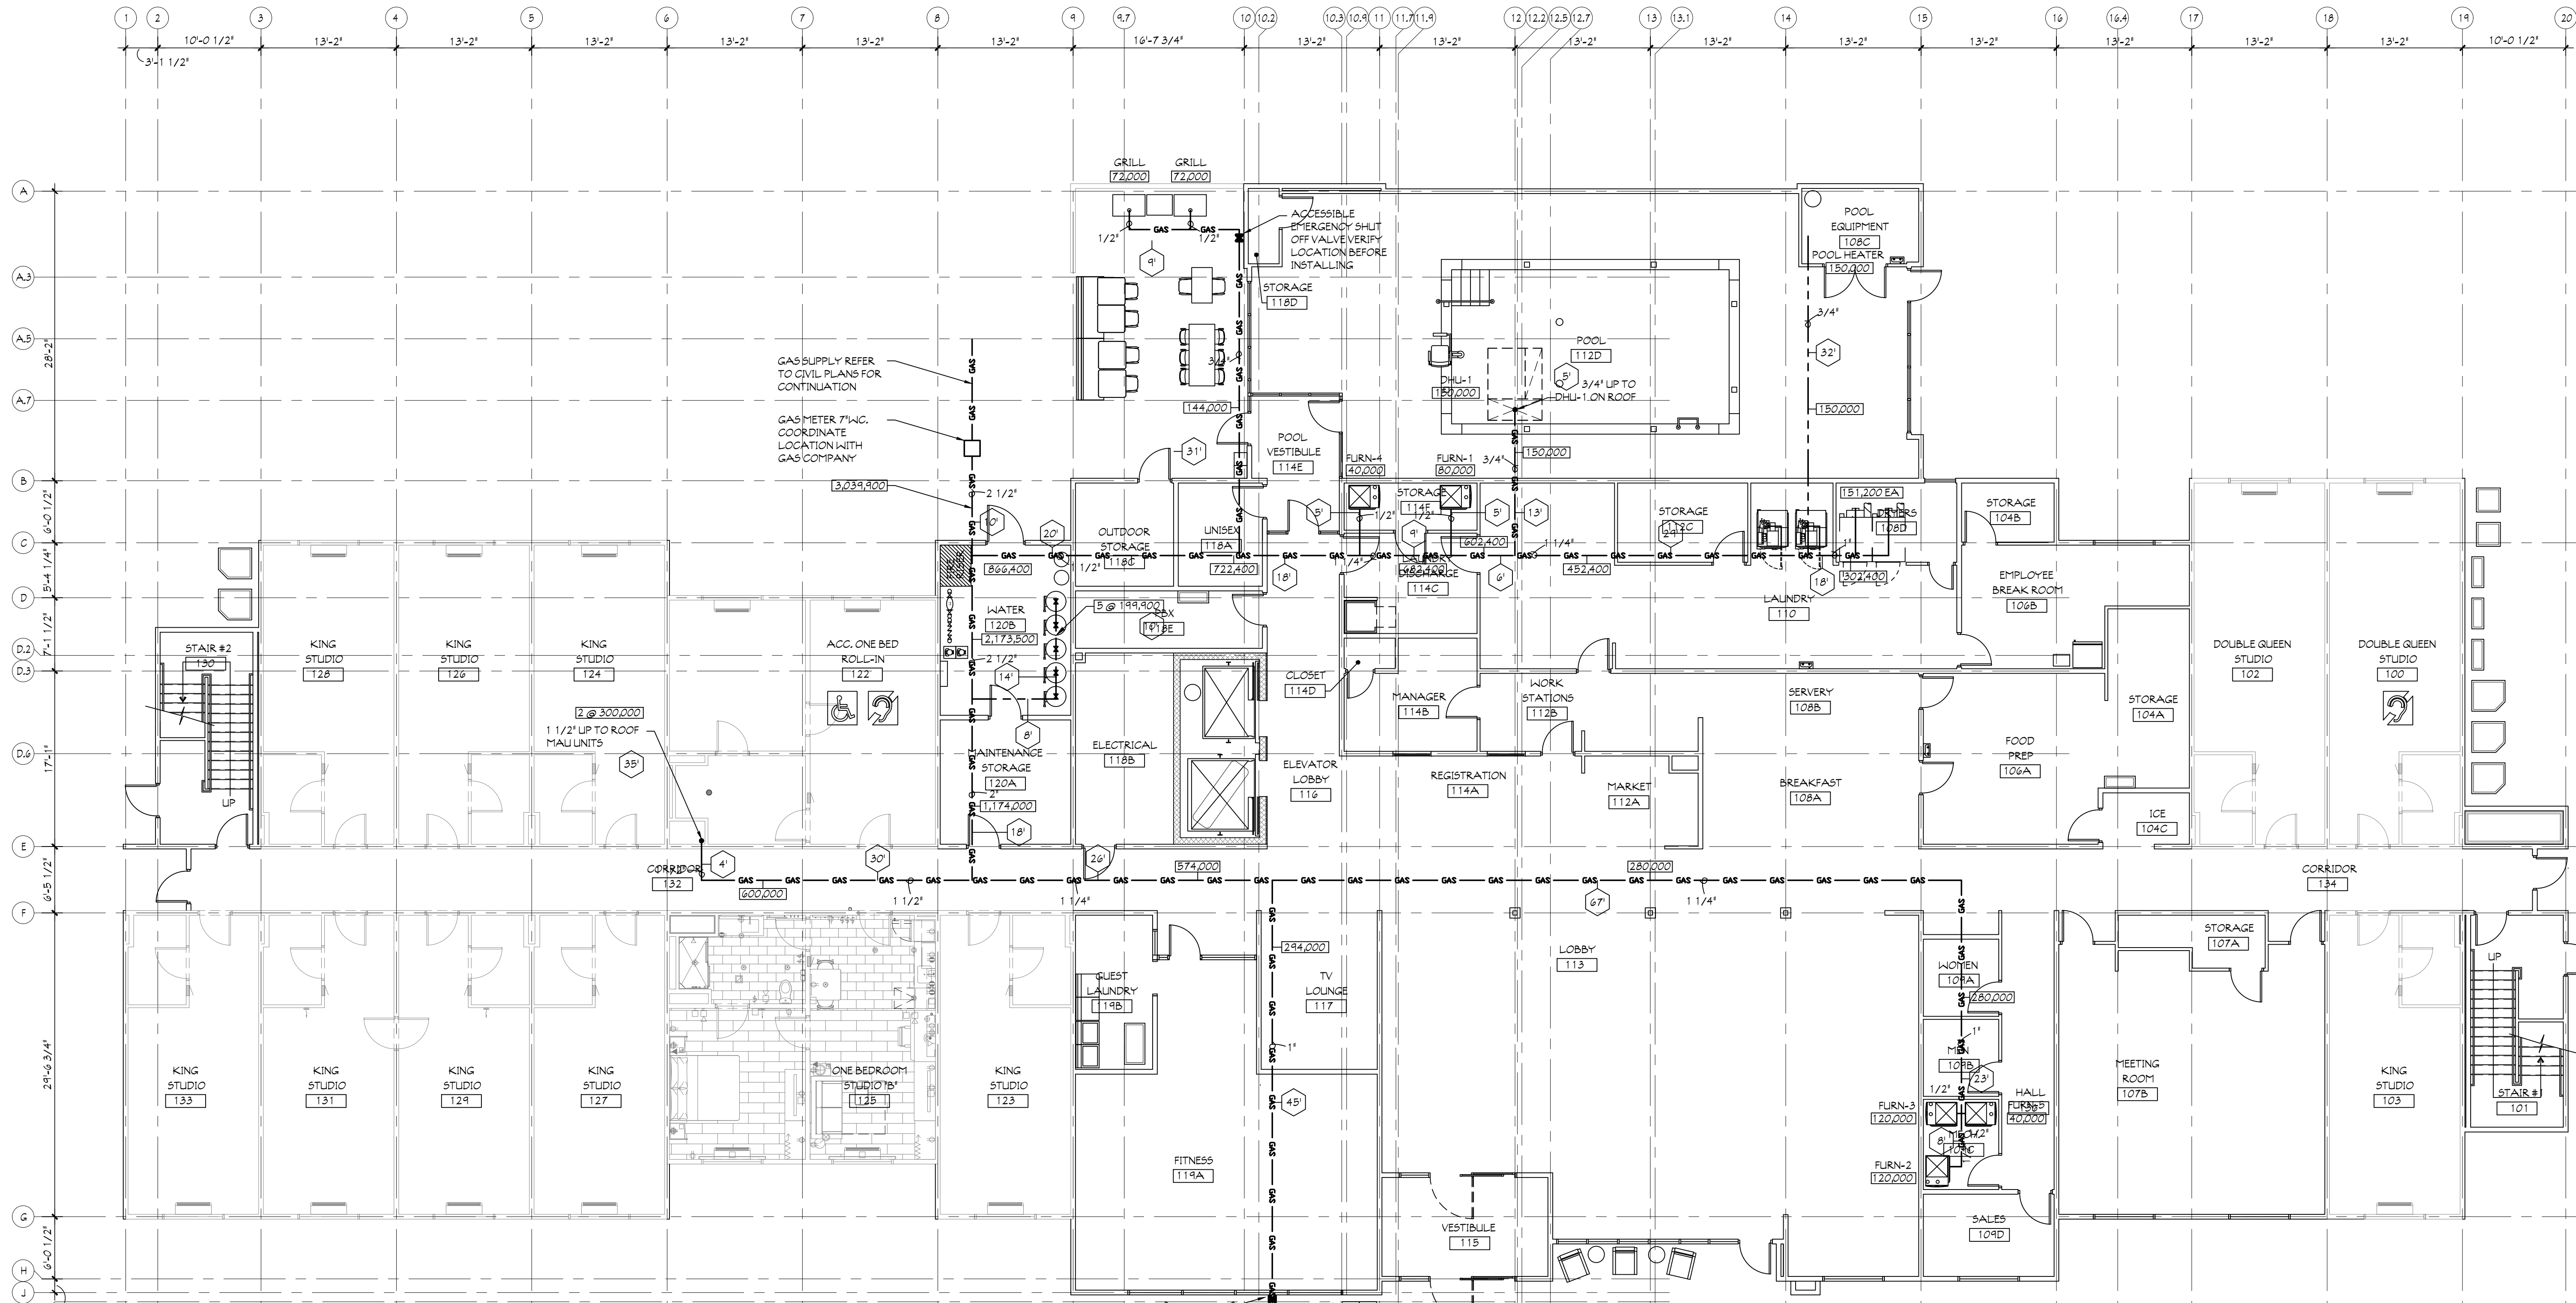


GAS LOAD SCHEDULE	
EQUIPMENT	BTUH
DHU-1	150,000
*POOL HEATER	150,000
DRYER	151,200
DRYER	151,200
WH	199,900
WH	199,900
WH	199,900
WH	199,900
WH	199,900
MAU#1	300,000
MAU#2	300,000
FURN#1	80,000
FURN#2	120,000
FURN#3	120,000
FURN#4	40,000
FURN#5	40,000
GRILL	72,000
GRILL	72,000
FIREPIT	147,000
FIREPIT	147,000
TOTAL USAGE	3,039,900

* VERIFY WITH POOL CONTRACTOR BEFORE INSTALLING GAS LINE

LEDGEND	
PIPE SIZE	1/2"
BTUH	120,000
PIPE DISTANCE	60"

1 FIRST FLOOR GAS PLAN
SCALE: 1/8" = 1'-0"

2 GAS LINE DROP TO EQUIPMENT DETAIL
SCALE: NOT TO SCALE

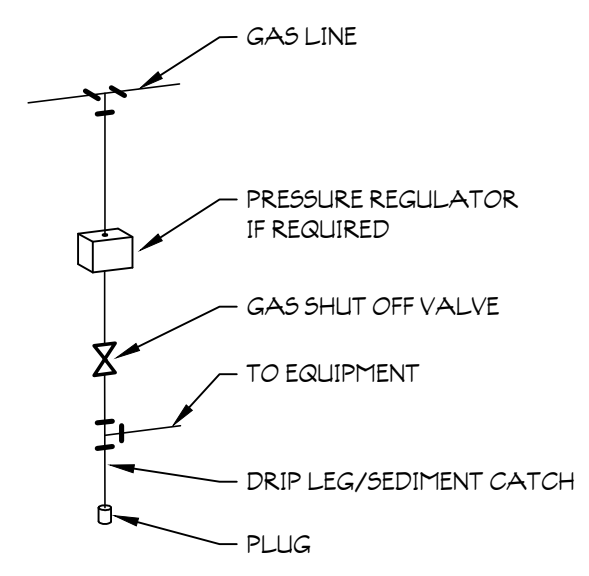

GENERAL NOTES

ALL DIMENSIONS UNLESS OTHERWISE NOTED ARE IN FEET AND INCHES. DIMENSIONS SHOULD BE DELETED FROM THE DRAWING IF NOT APPLICABLE.

ALL DIMENSIONS SHOULD BE VERIFIED BY THE GENERAL CONTRACTOR. THE ARCHITECT SHALL NOT BE RESPONSIBLE FOR ANY DISCREPANCIES OR OMISSIONS.

THESE DRAWINGS ARE THE PROPERTY OF MAUST ARCHITECTURAL SERVICES, INC. AND ARE NOT TO BE REPRODUCED, COPIED, OR TRANSMITTED IN ANY FORM OR BY ANY MEANS, ELECTRONIC OR MECHANICAL, WITHOUT THE WRITTEN PERMISSION OF MAUST ARCHITECTURAL SERVICES, INC.

Architects
MAUST ARCHITECTURAL SERVICES, INC.
DIVISION OF L.E.M., INC.
112 NORTH MAIN STREET
GOSHEN, INDIANA 46526
PHONE: (574) 537-8500
FAX: (574) 537-0808

REVISIONS:

DATE: 05/01/26
JOB NO.: MAS-26-105
NAME: FIRST FLOOR GAS PLAN
SHEET: M601

FT. WAYNE, INDIANA