




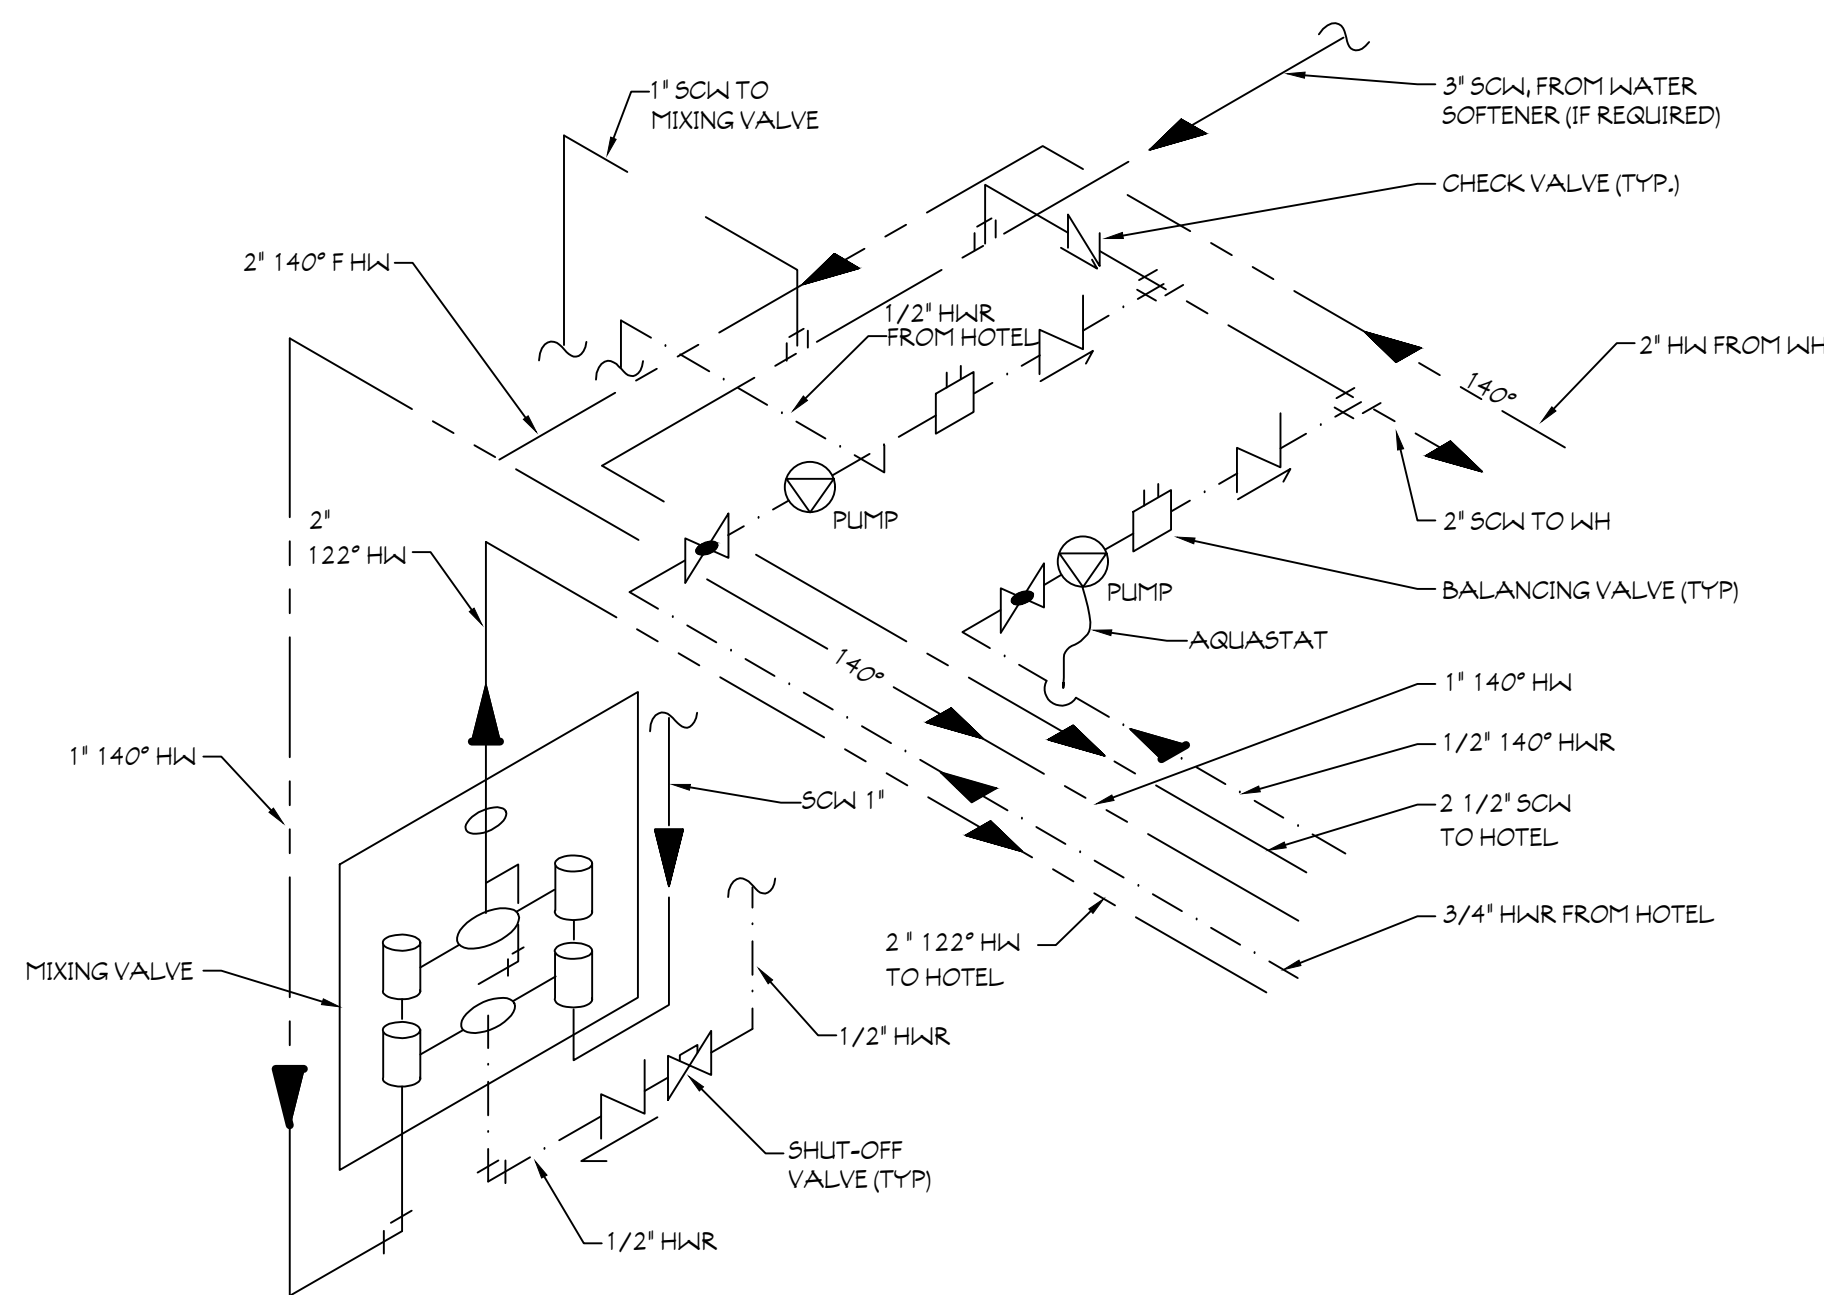


1 **TMV & HOT WATER RETURN DIAGRAM**
SCALE: NOT TO SCALE

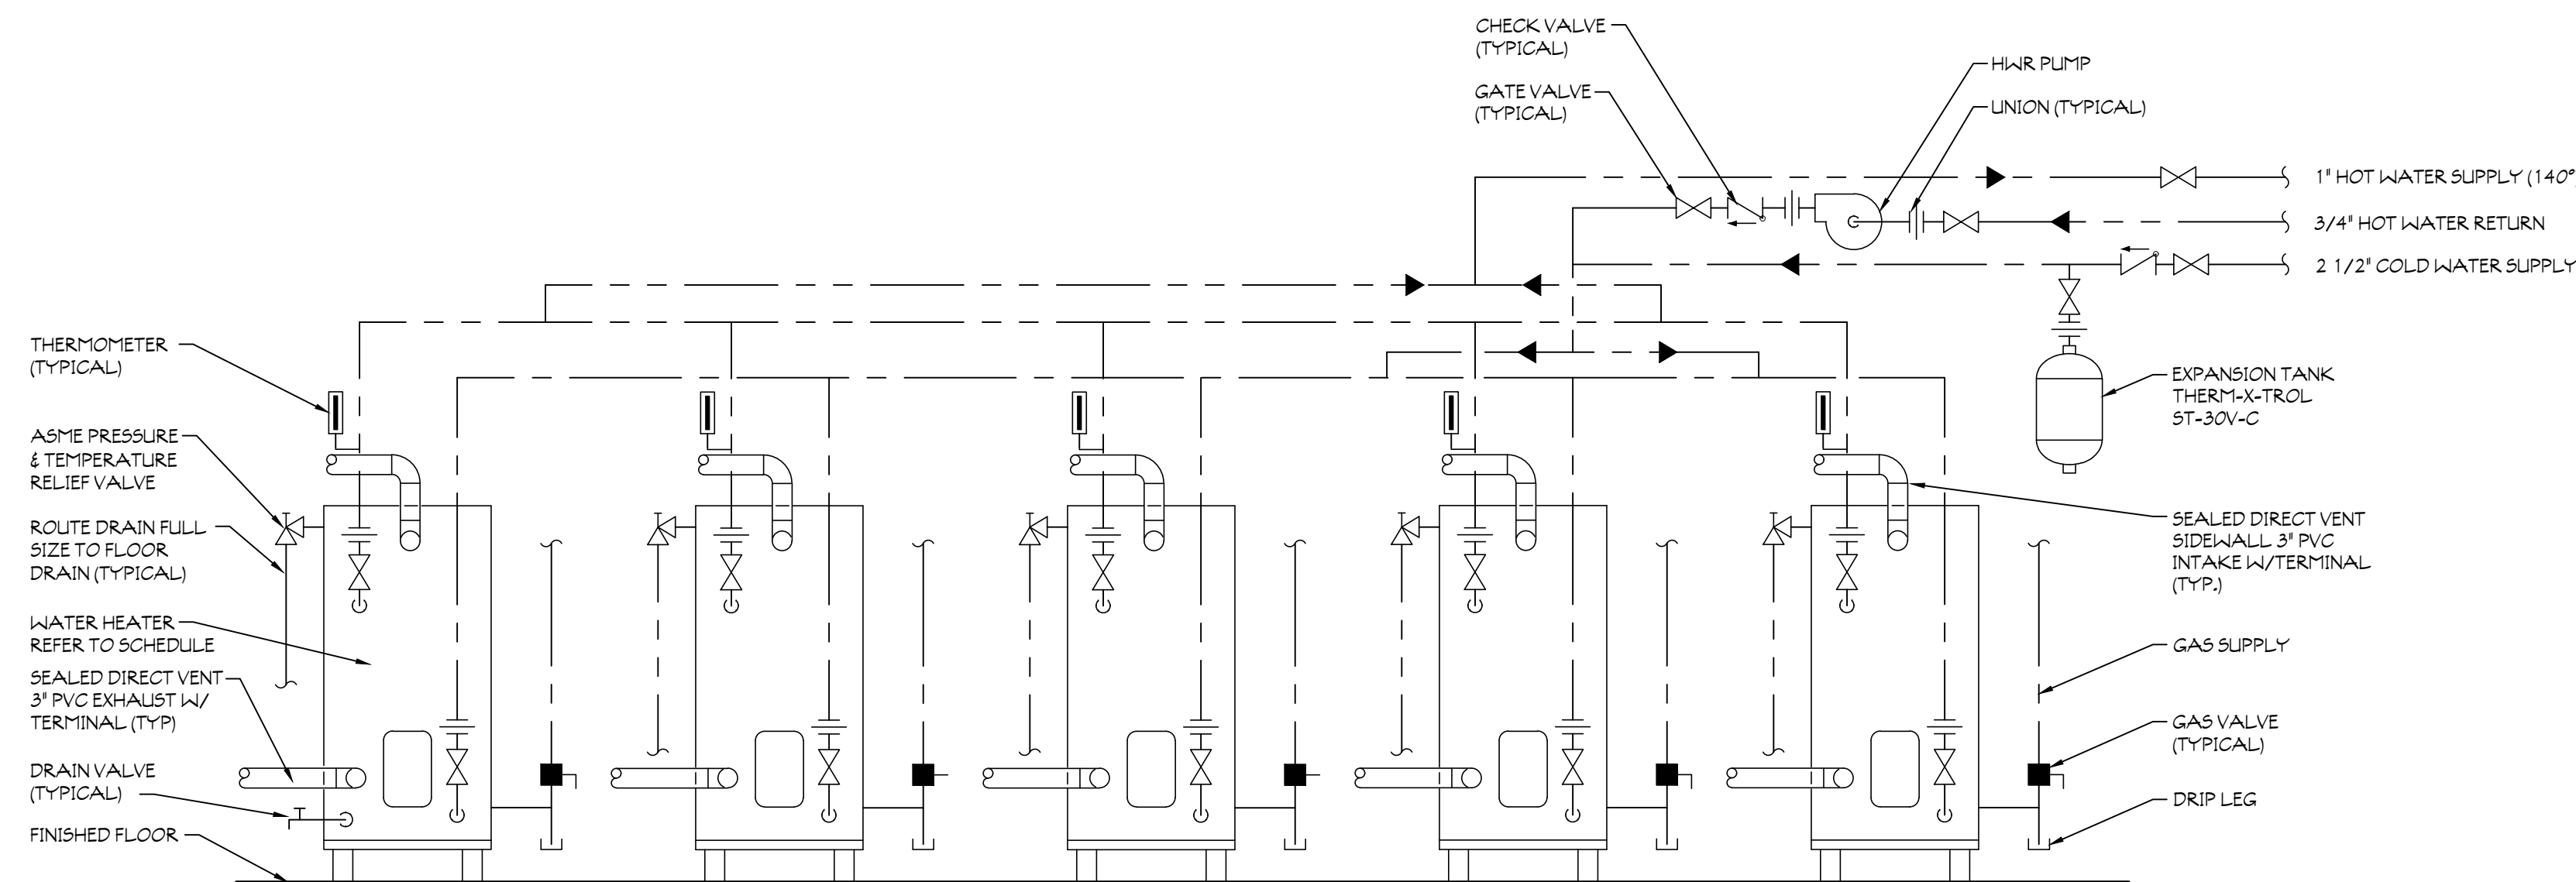


2 **WATER HEATER PIPING DETAIL**
SCALE: NOT TO SCALE

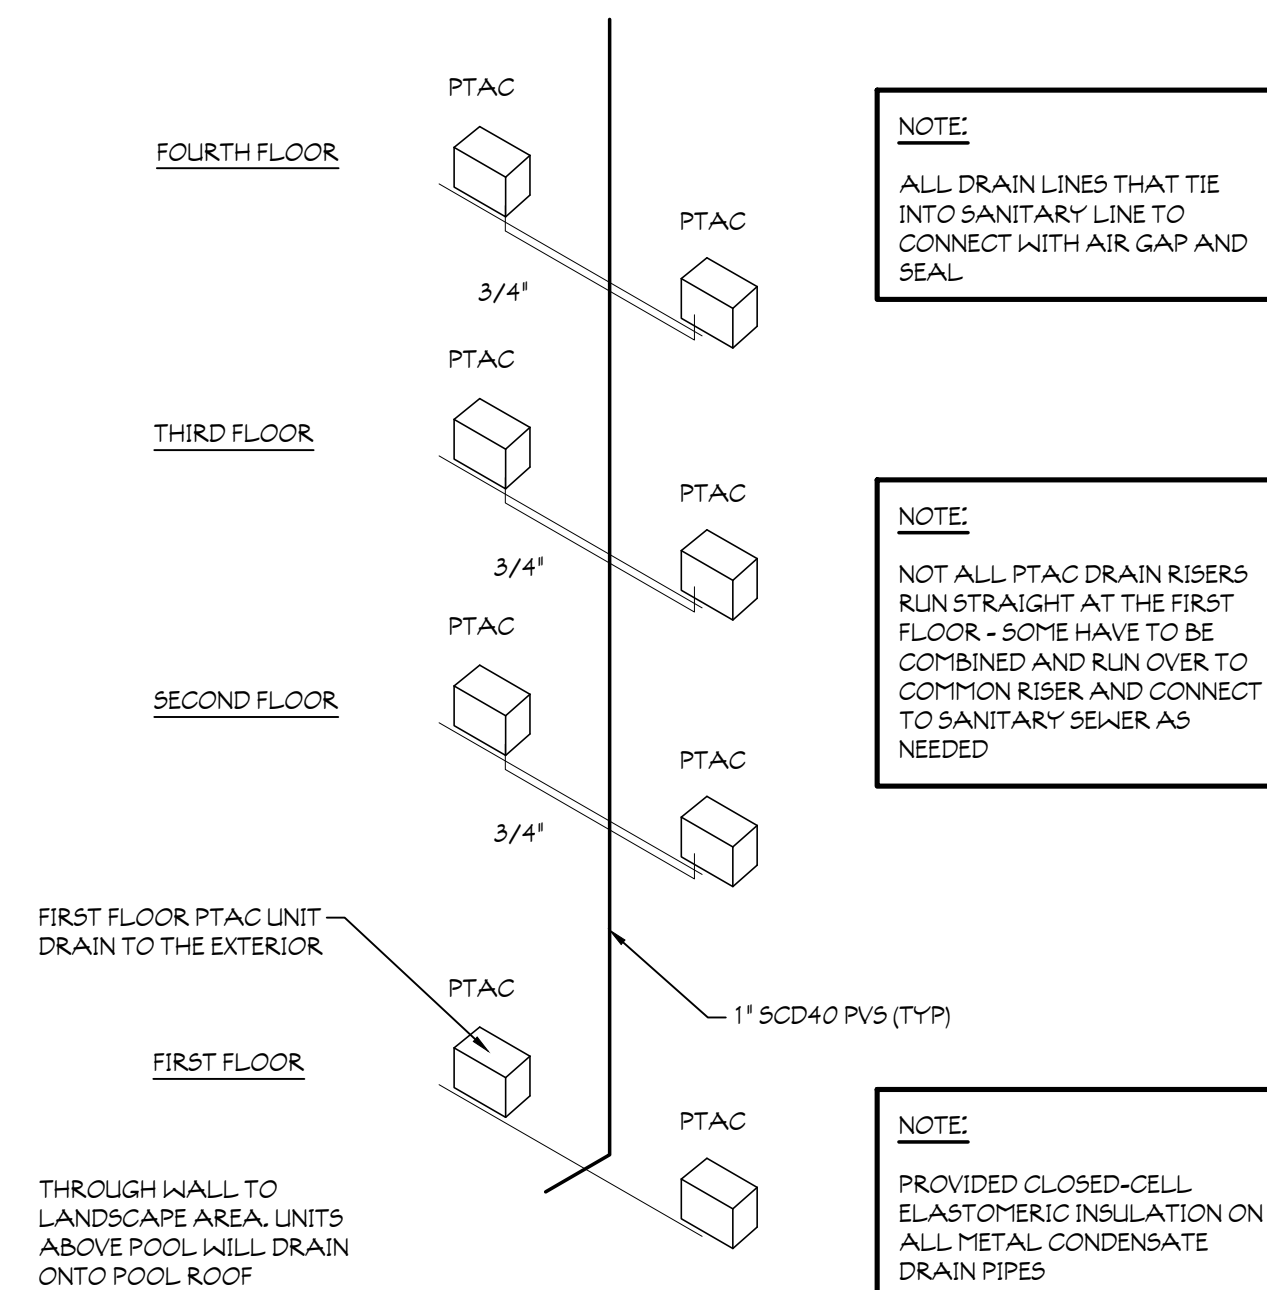


3 **CONDENSATE DRAIN**
SCALE: NOT TO SCALE

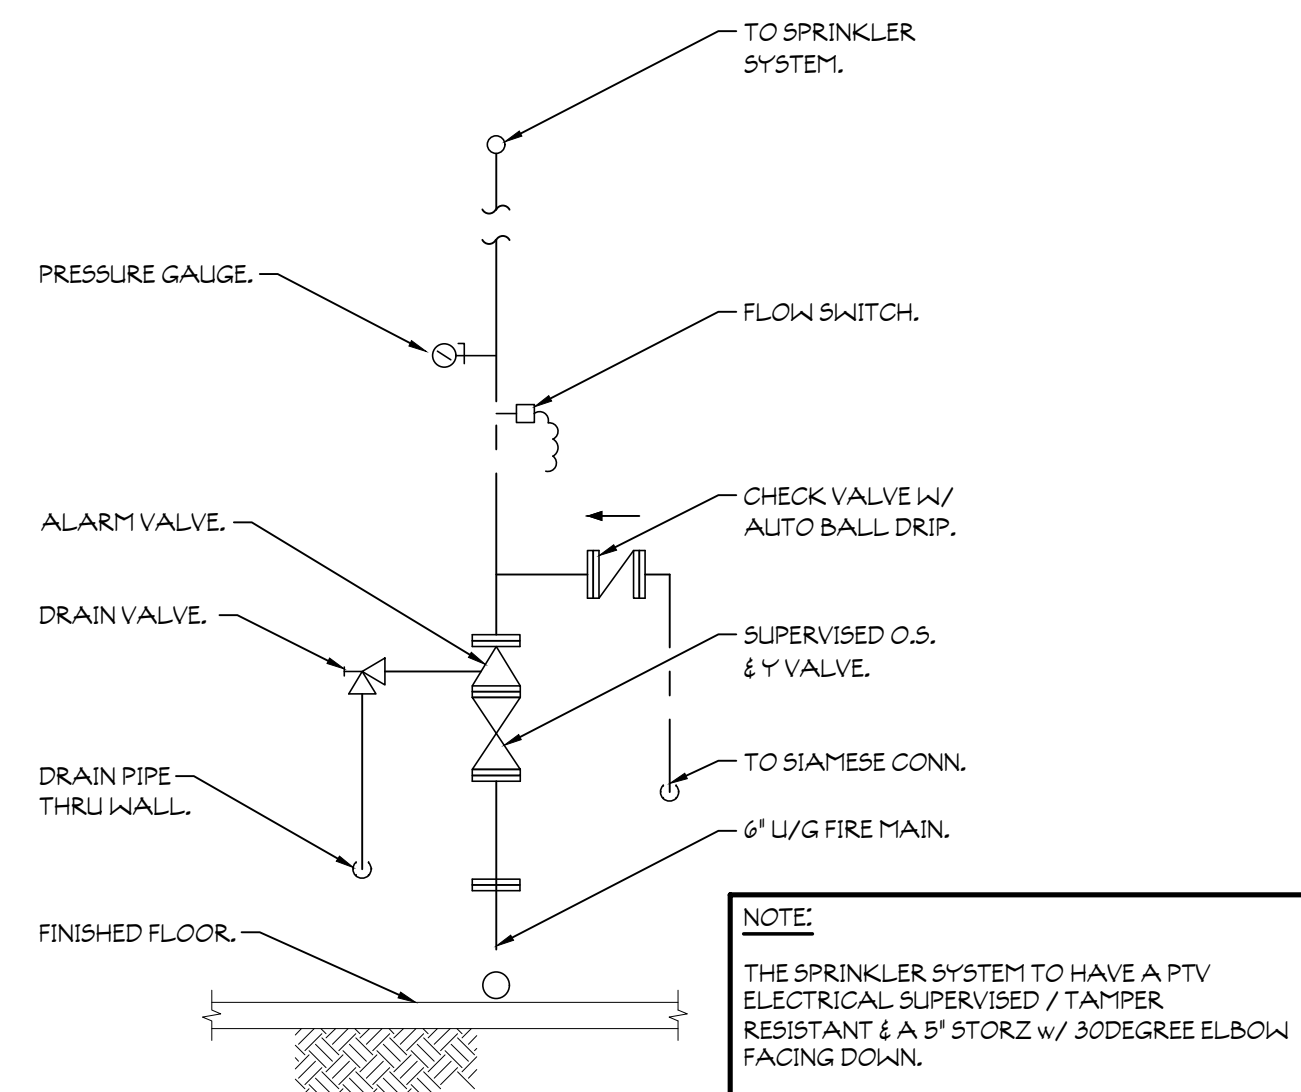


4 **TYPICAL WET PIPE SPRINKLER RISER**
SCALE: NOT TO SCALE

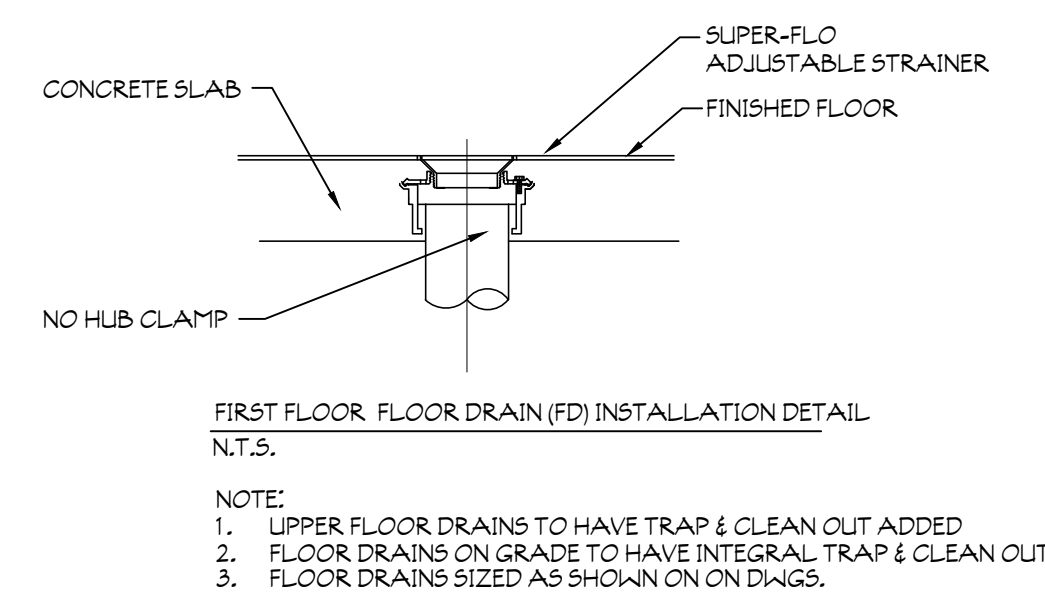


5 **FLOOR DRAIN DETAIL**
SCALE: NOT TO SCALE

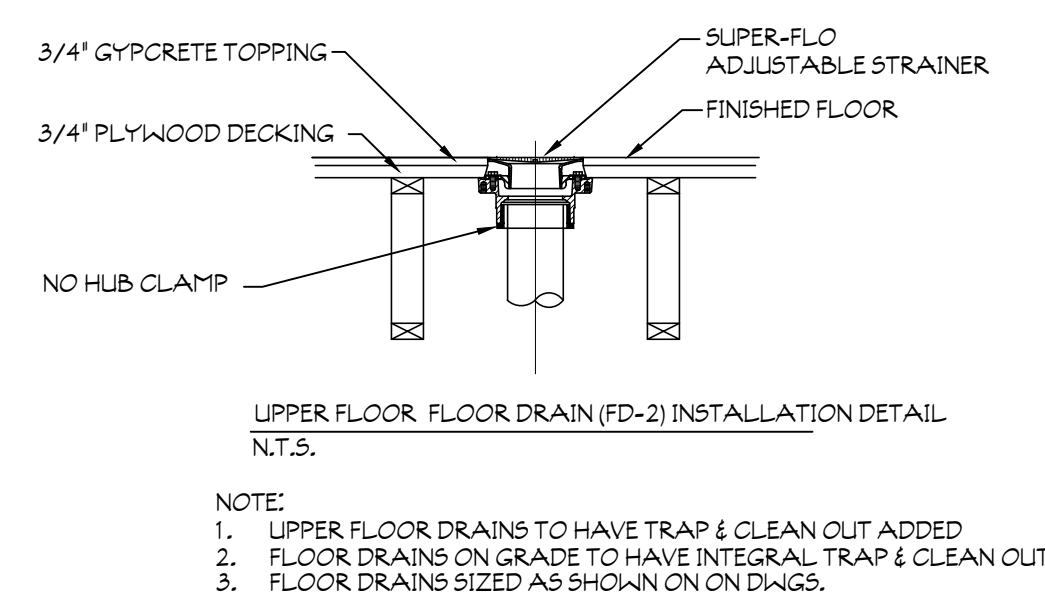

6 **FLOOR DRAIN DETAIL**
SCALE: NOT TO SCALE

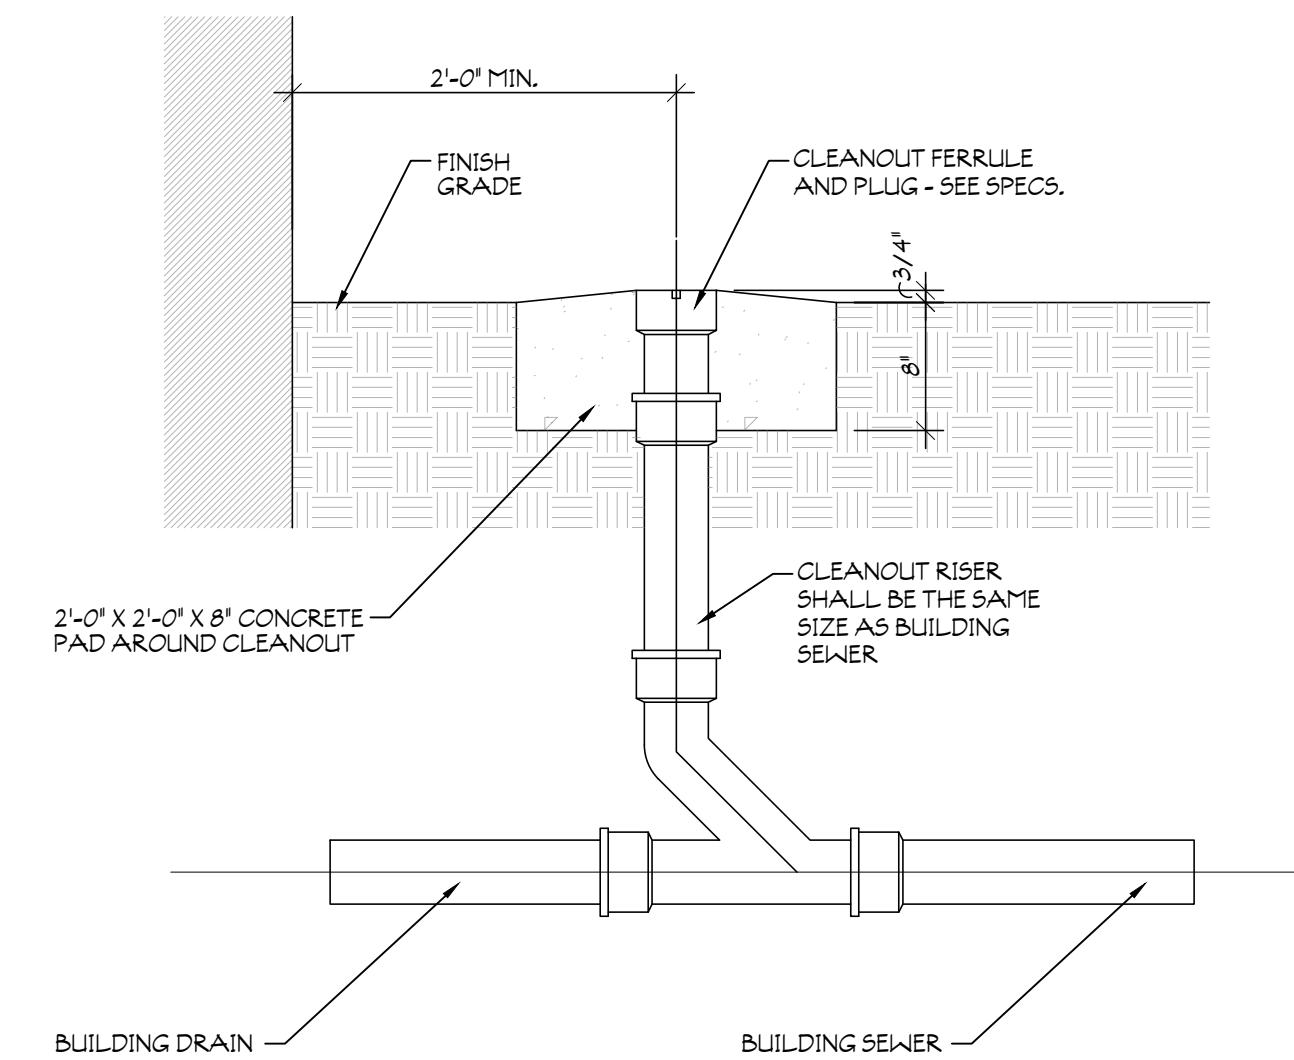


7 **TYPICAL EXTERIOR CLEANOUT**
SCALE: NOT TO SCALE

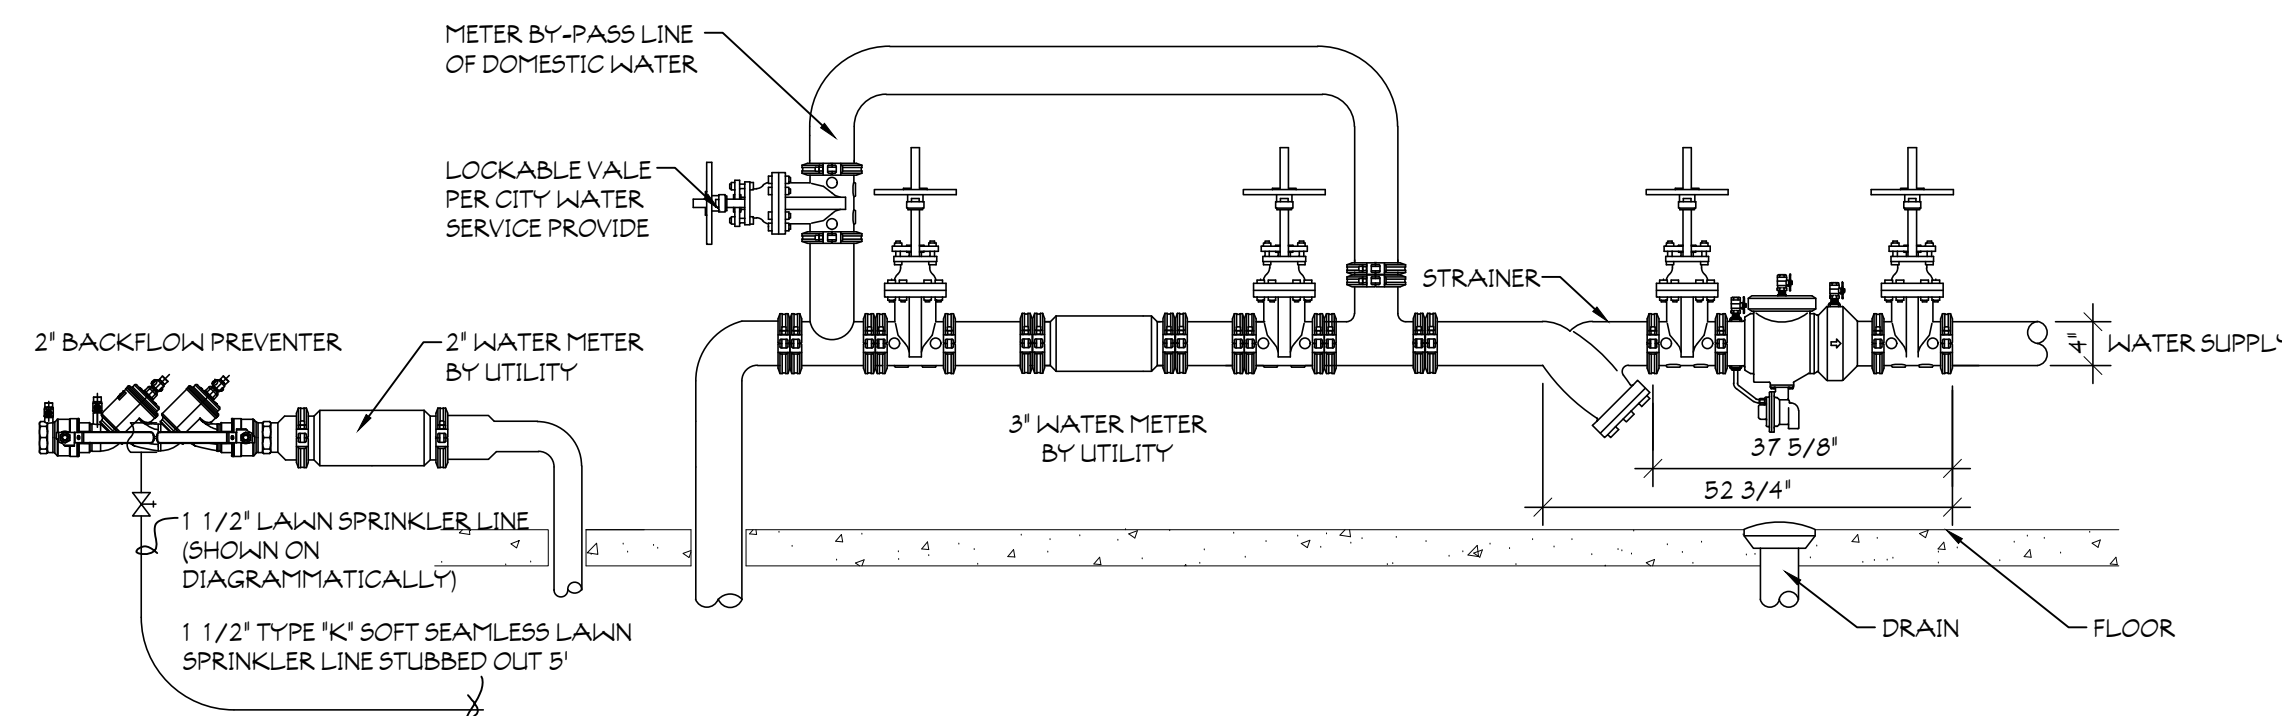

8 **TYPICAL 2" LAWN SPRINKLER RISER**
SCALE: NOT TO SCALE

9 **TYPICAL 4" BACKFLOW PREVENTER DTL.**
SCALE: NOT TO SCALE

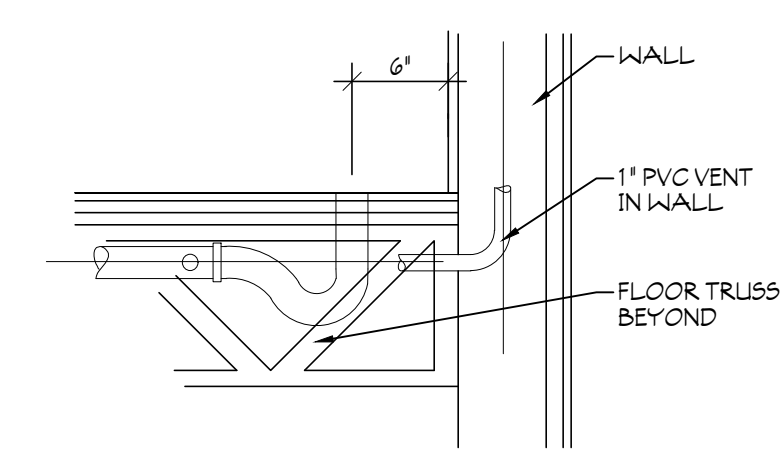

10 **2" OPEN SITE DRAIN AT ICE MACHINE**
SCALE: NOT TO SCALE

NOTE:
SANITARY & BUILDING DRAINS TO BE LOCATED AS REQUIRED BY STATE & LOCAL CODES

NOTE:
ALL BUILDING REQUIREMENTS TO FOLLOW SPECIFICATIONS PER HOTEL STANDARDS. CONTRACTOR MUST MAKE THEIR COMPANY FAMILIAR WITH THOSE STANDARDS SET FORTH BY THE HOTEL CHAIN. ALL DRAININGS SUBJECT TO CHANGE IF DRAININGS CONFLICT WITH HOTEL STANDARDS.

GENERAL NOTES

ALTHOUGH DRAININGS ARE DRAWN TO SCALE, THE ACCURACY OF THE DRAININGS CANNOT BE GUARANTEED. THE CONTRACTOR SHALL VERIFY THE DIMENSIONS OF THE DRAININGS PRIOR TO CONSTRUCTION. ALL DIMENSIONS ARE TO FACE UNLESS OTHERWISE NOTED. THE CONTRACTOR SHALL BE RESPONSIBLE FOR OBTAINING ALL NECESSARY PERMITS AND APPROVALS PRIOR TO CONSTRUCTION.

Architects
Plumbers
Mechanical Engineers
MAUIST ARCHITECTURAL SERVICES
DIVISION OF
L.E.M., INC.
112 NORTH MAIN STREET
GOSHEN, INDIANA 46526
PHONE (574) 537-8500
FAX (574) 537-0808

HOME 2
SUITES BY HILTON

SHEET SIZE 24x36

FT. WAYNE, INDIANA

REVISIONS:

PRELIMINARY - NOT FOR CONSTRUCTION

DATE: 05/01/26

JOB NO.: MAS-26-105

NAME:

PLUMBING DETAILS

SHEET:

P002