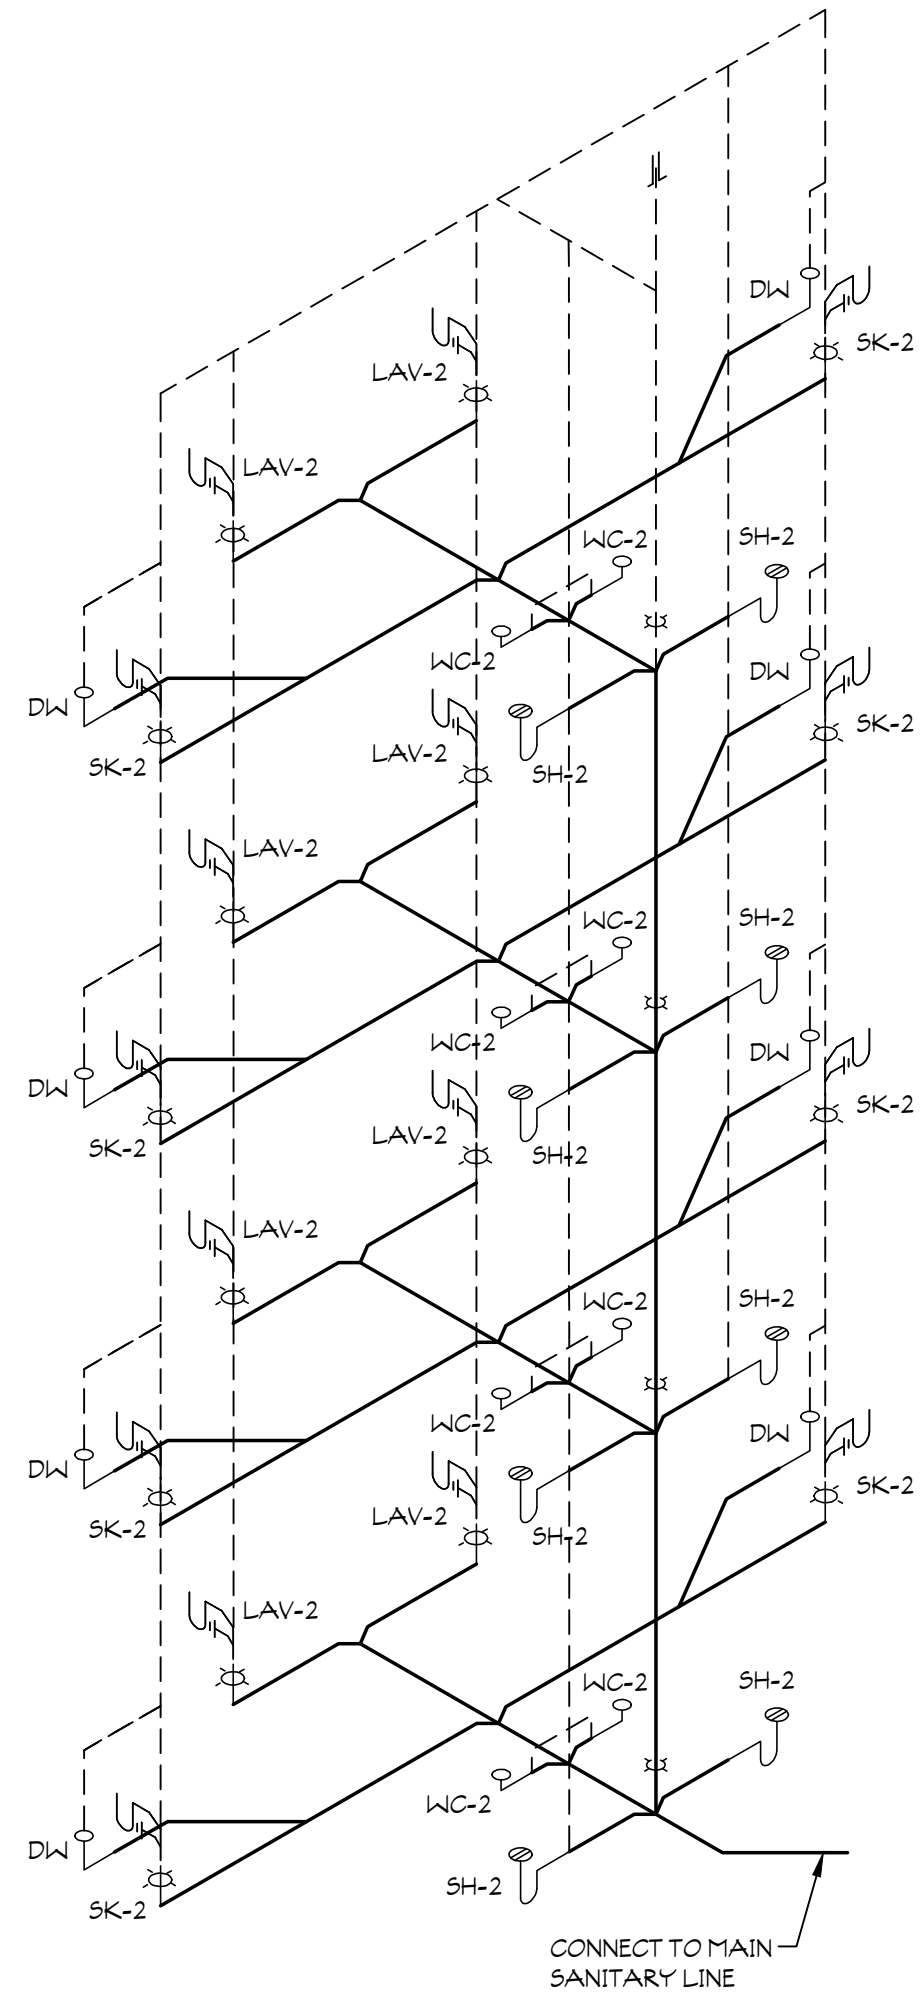
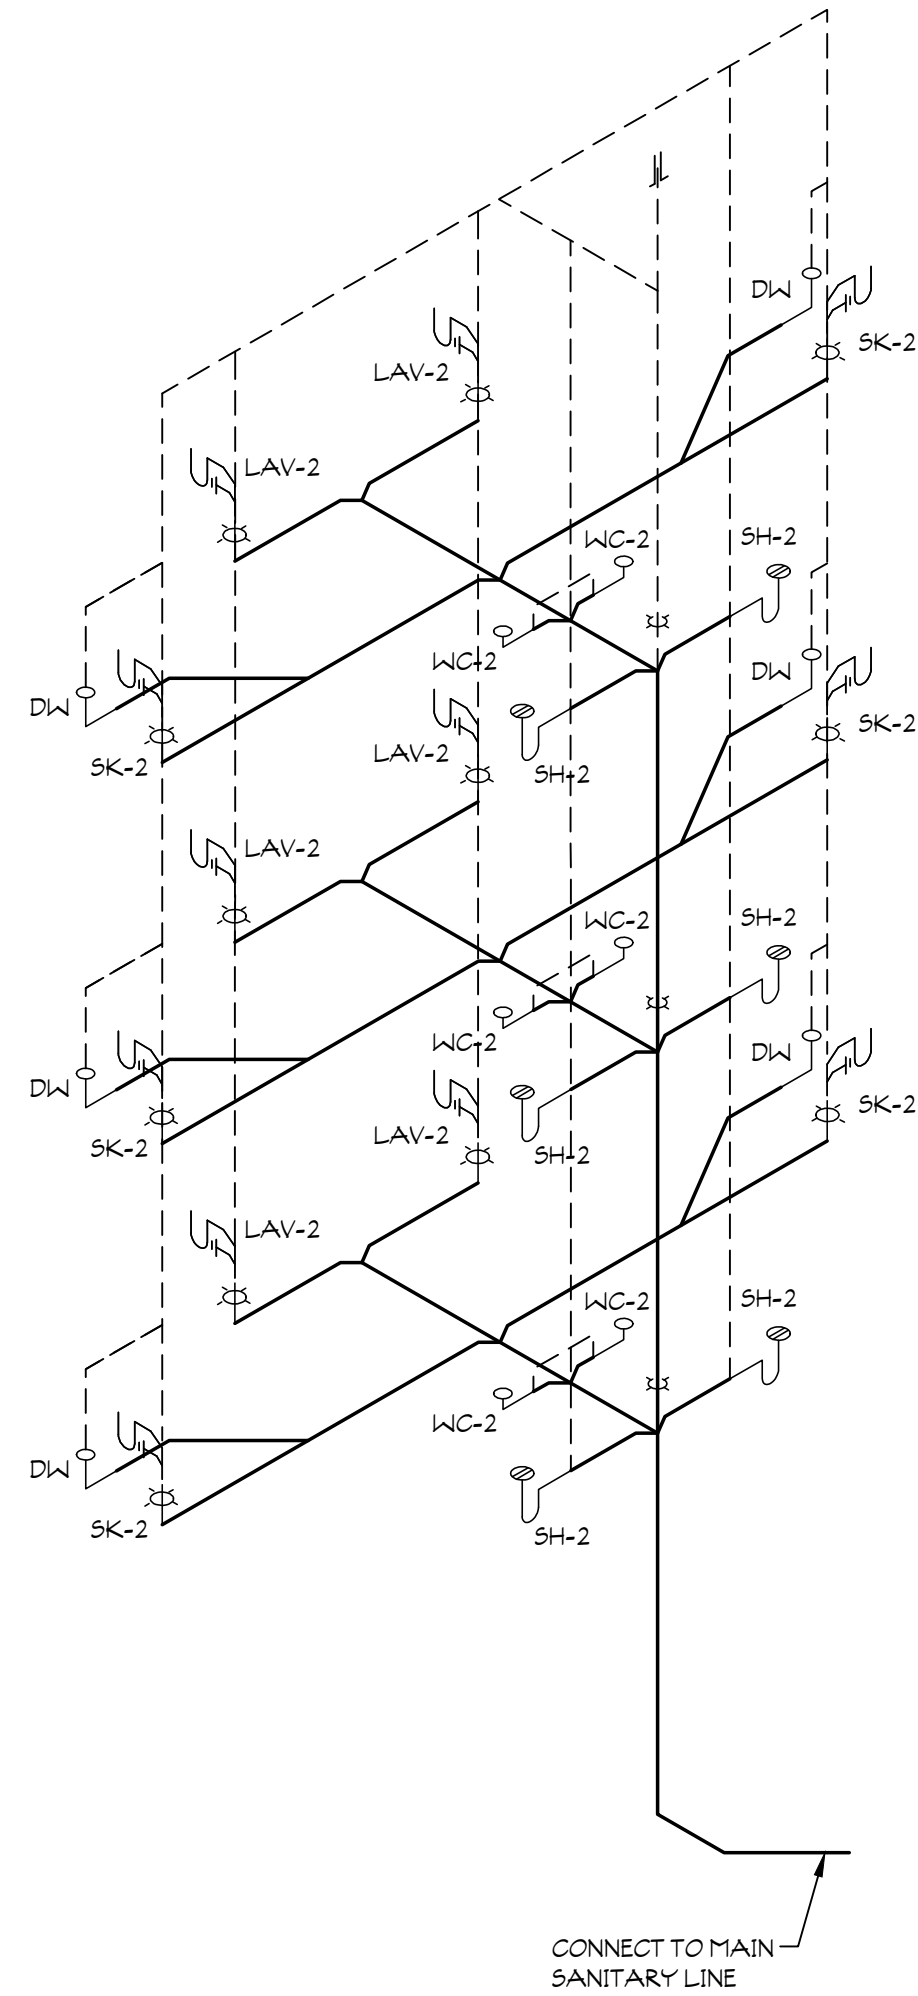
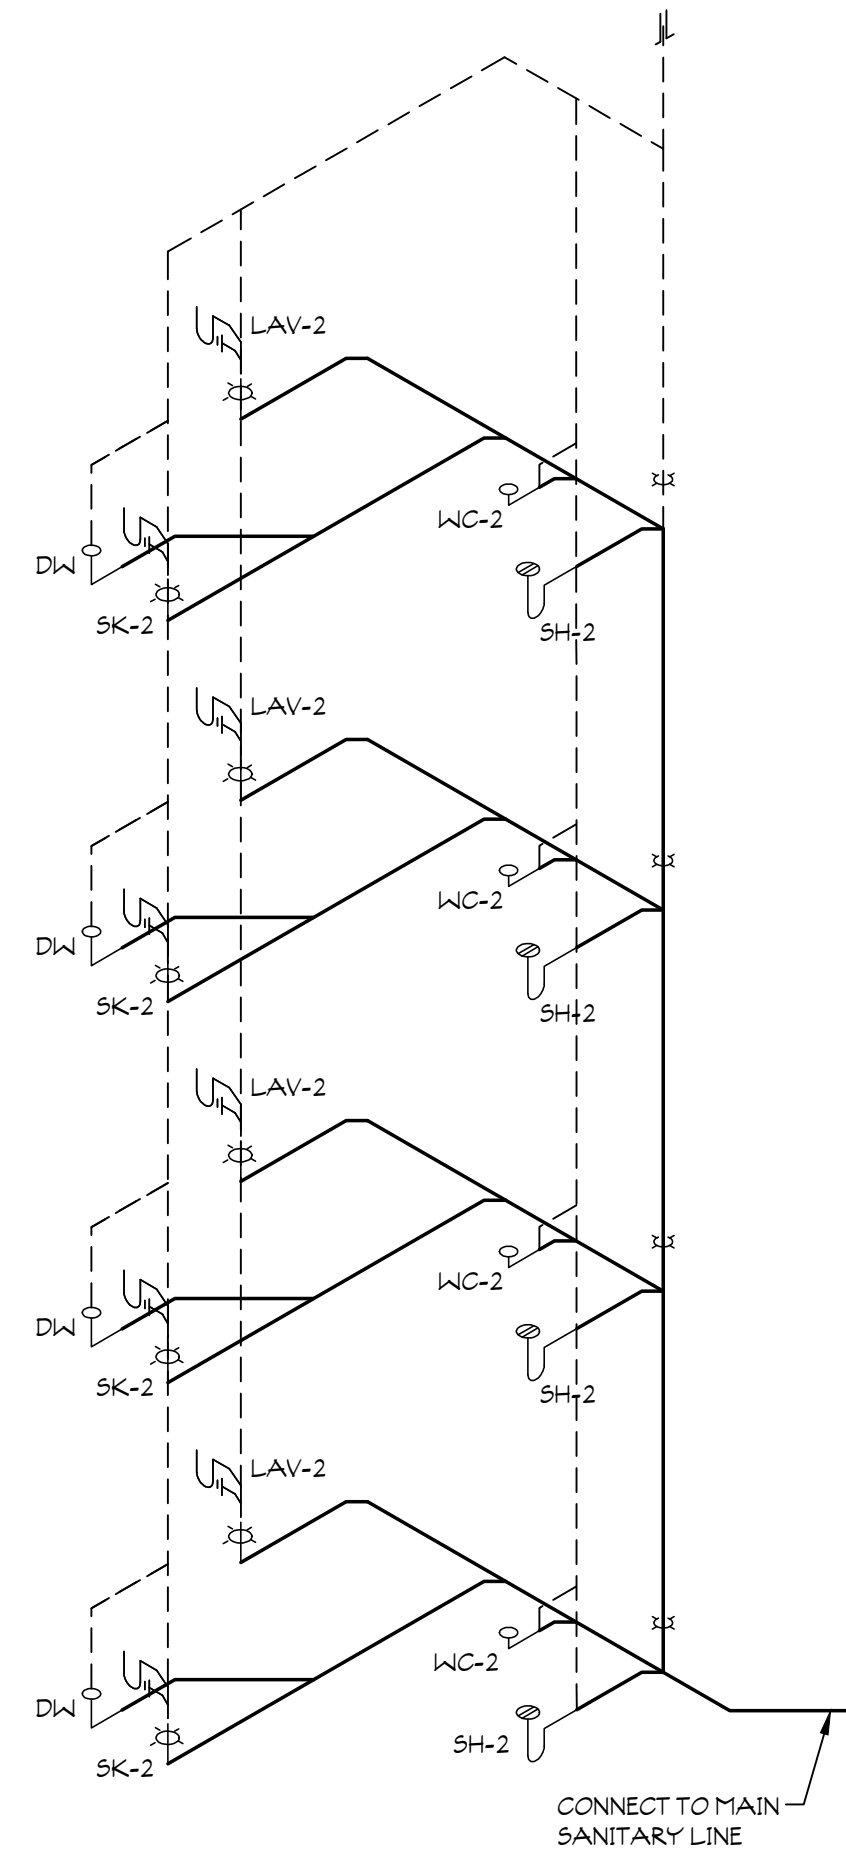
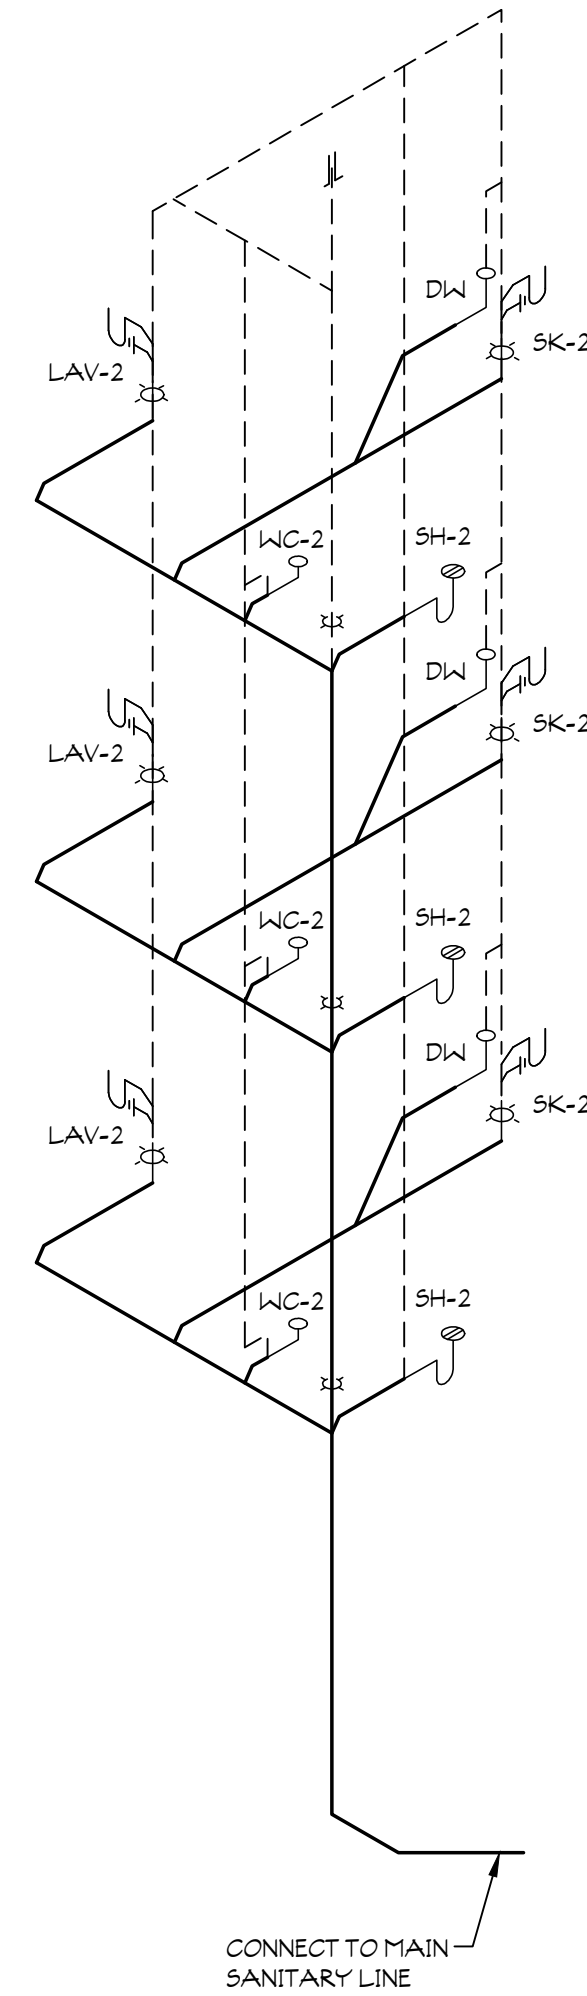
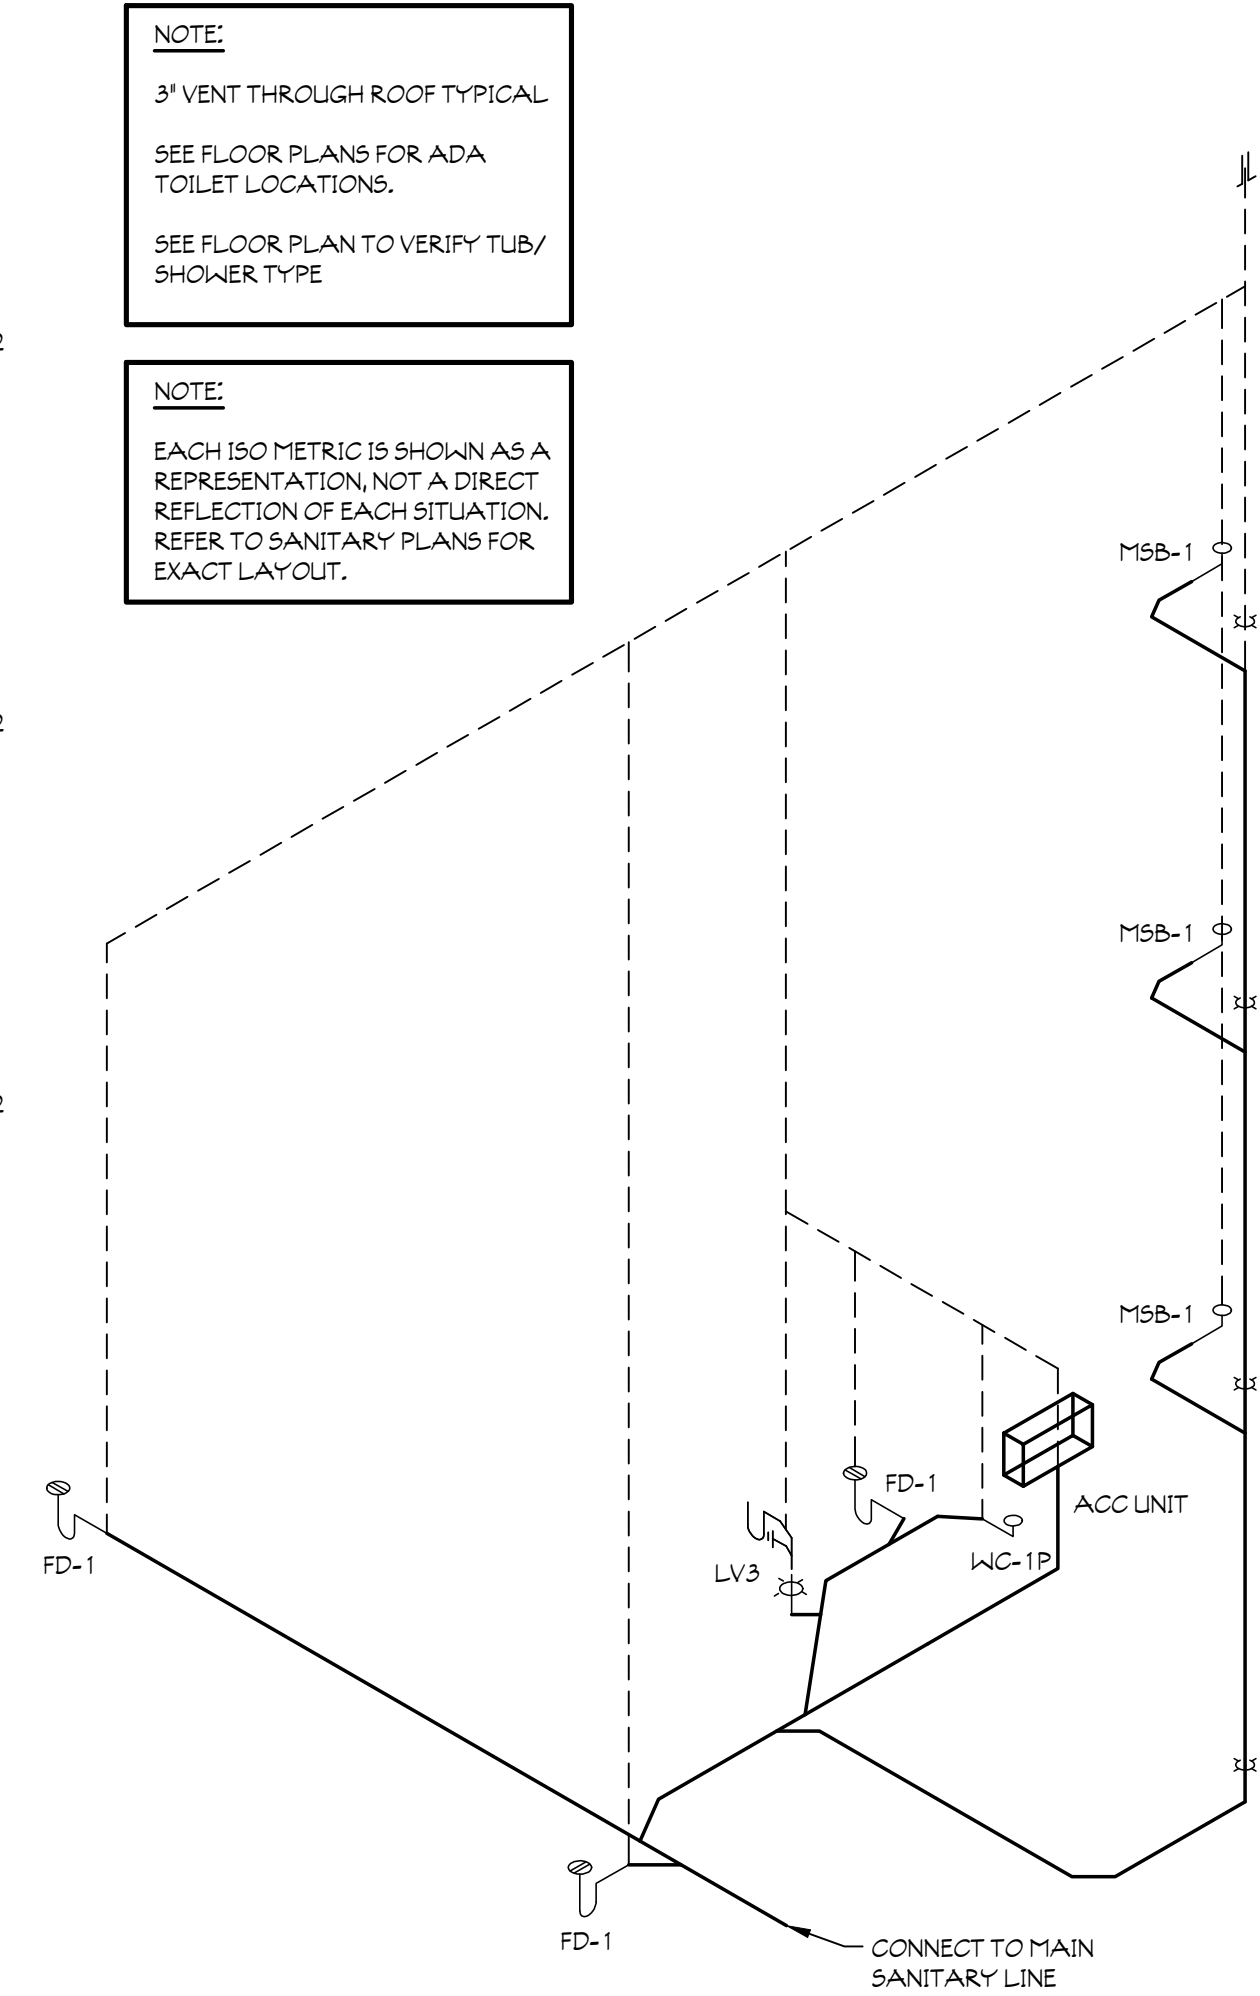


FOURTH FLOOR

THIRD FLOOR

SECOND FLOOR

FIRST FLOOR






**1 SANITARY RISER DIAGRAM**
SCALE: NOT TO SCALE**2 SANITARY RISER DIAGRAM**
SCALE: NOT TO SCALE**3 SANITARY RISER DIAGRAM**
SCALE: NOT TO SCALE**4 SANITARY RISER DIAGRAM**
SCALE: NOT TO SCALE**5 SANITARY RISER DIAGRAM**
SCALE: NOT TO SCALE

FOURTH FLOOR

THIRD FLOOR

SECOND FLOOR

FIRST FLOOR

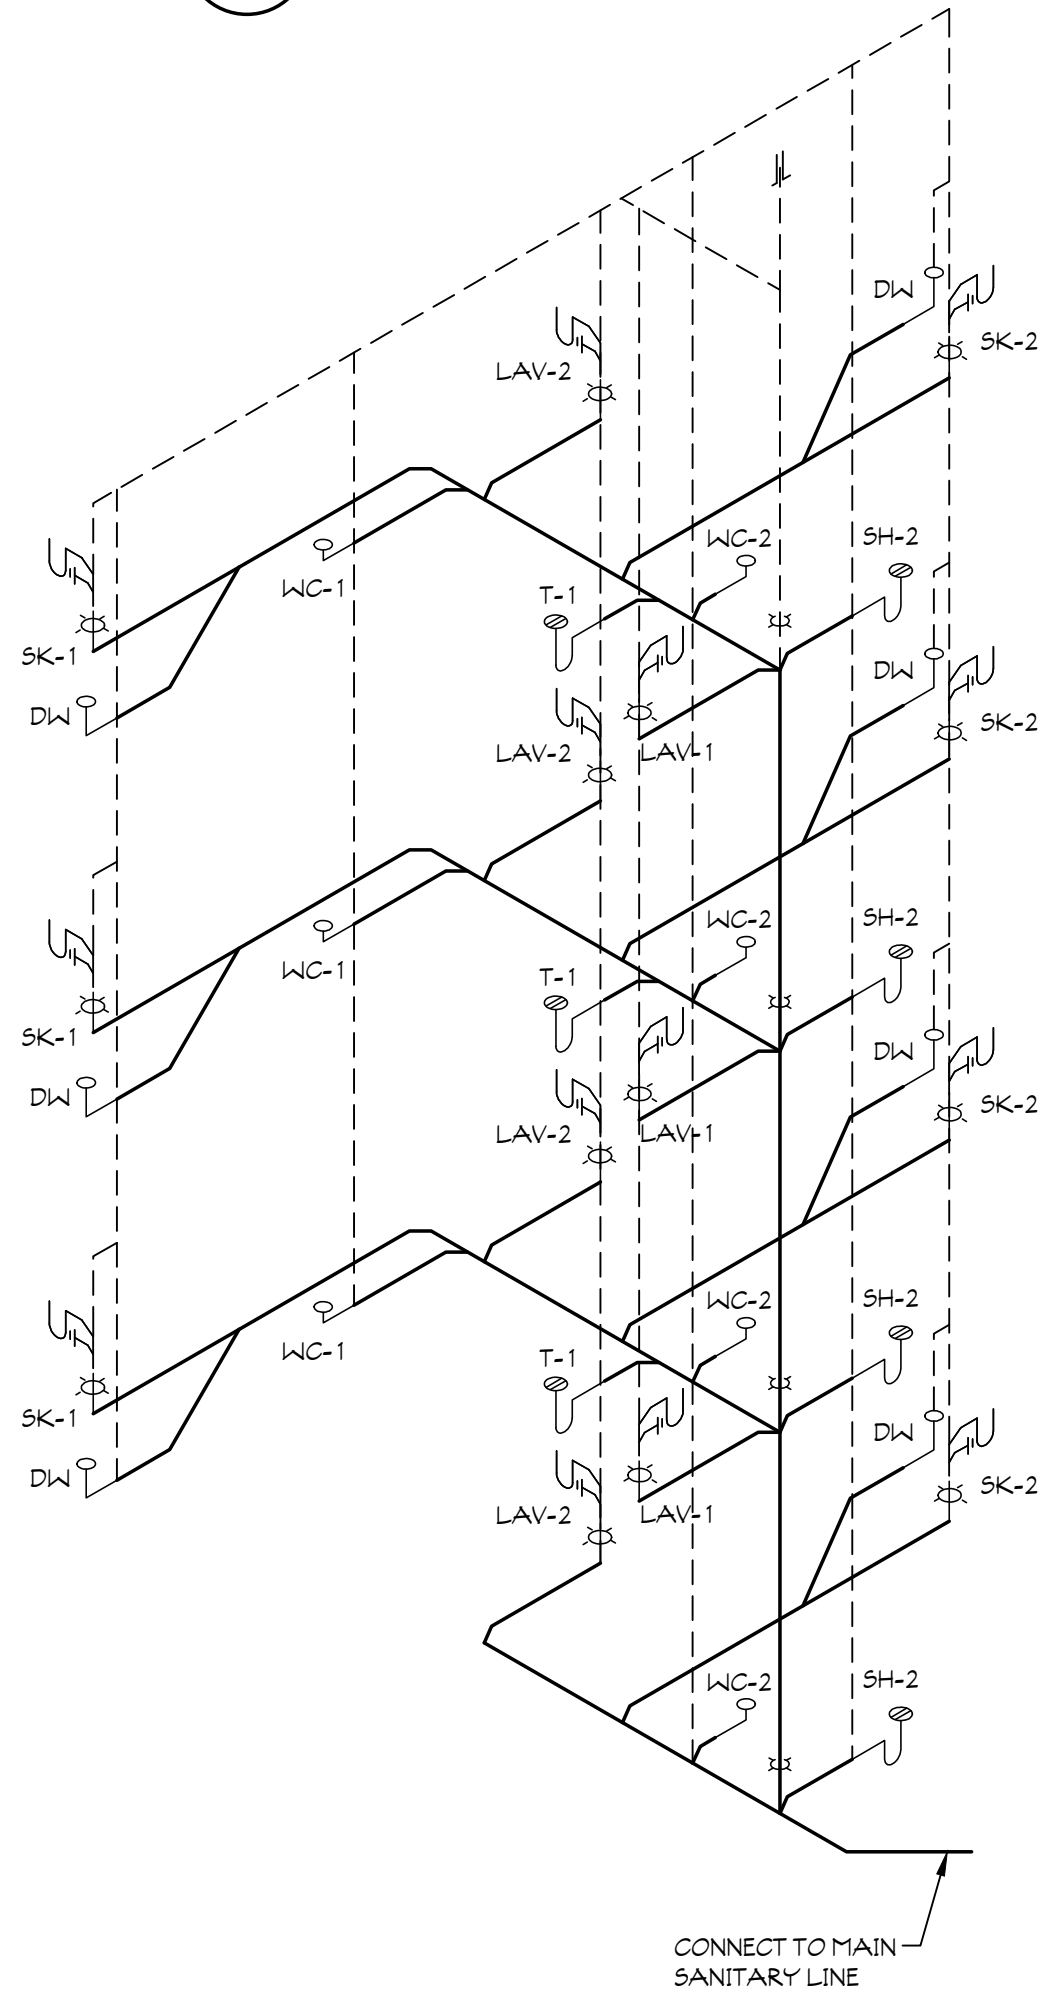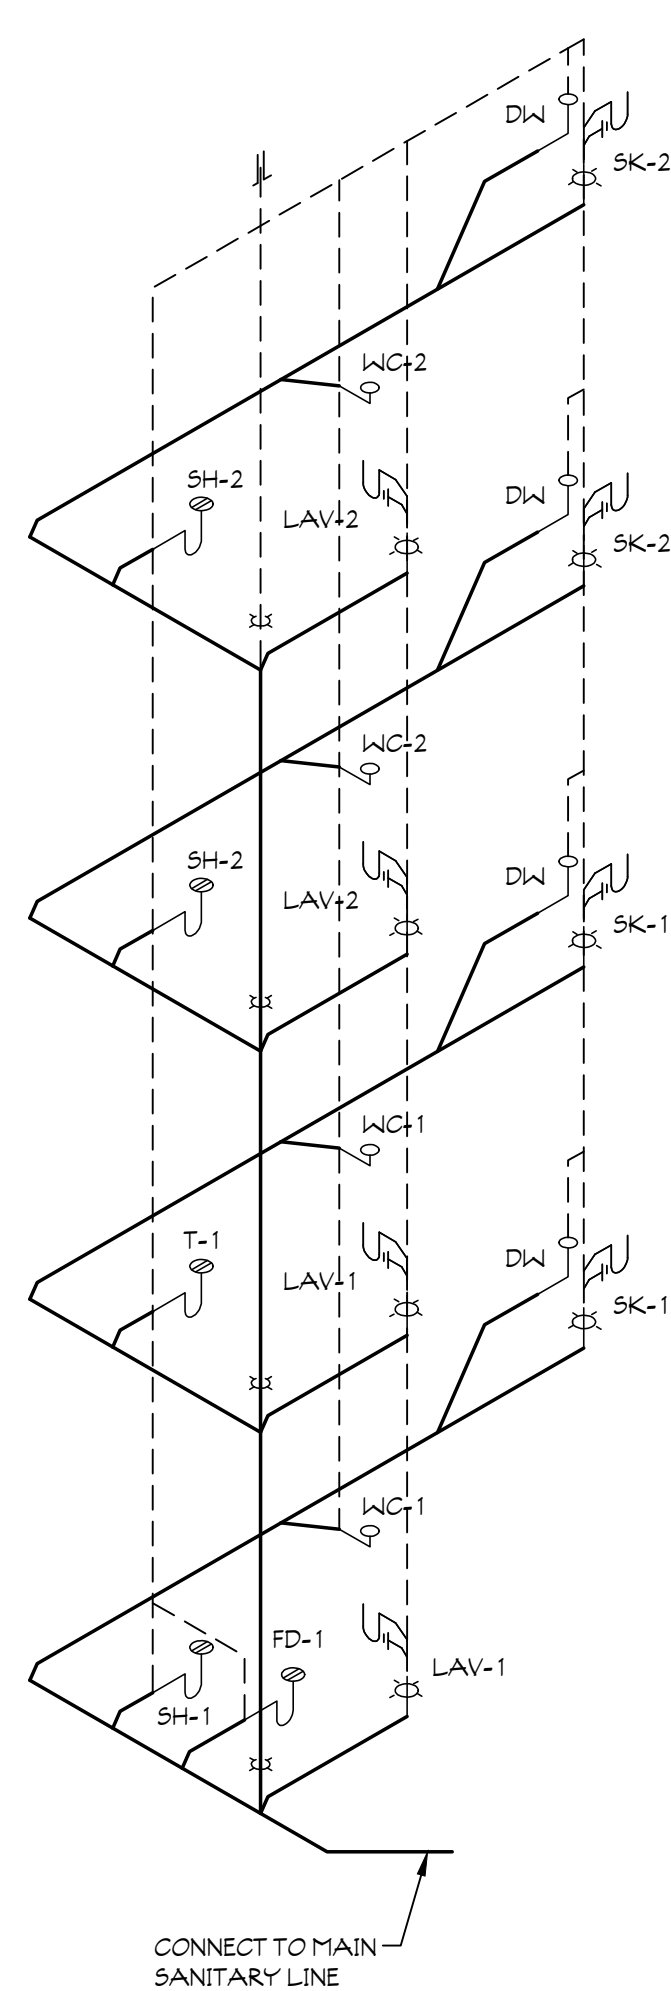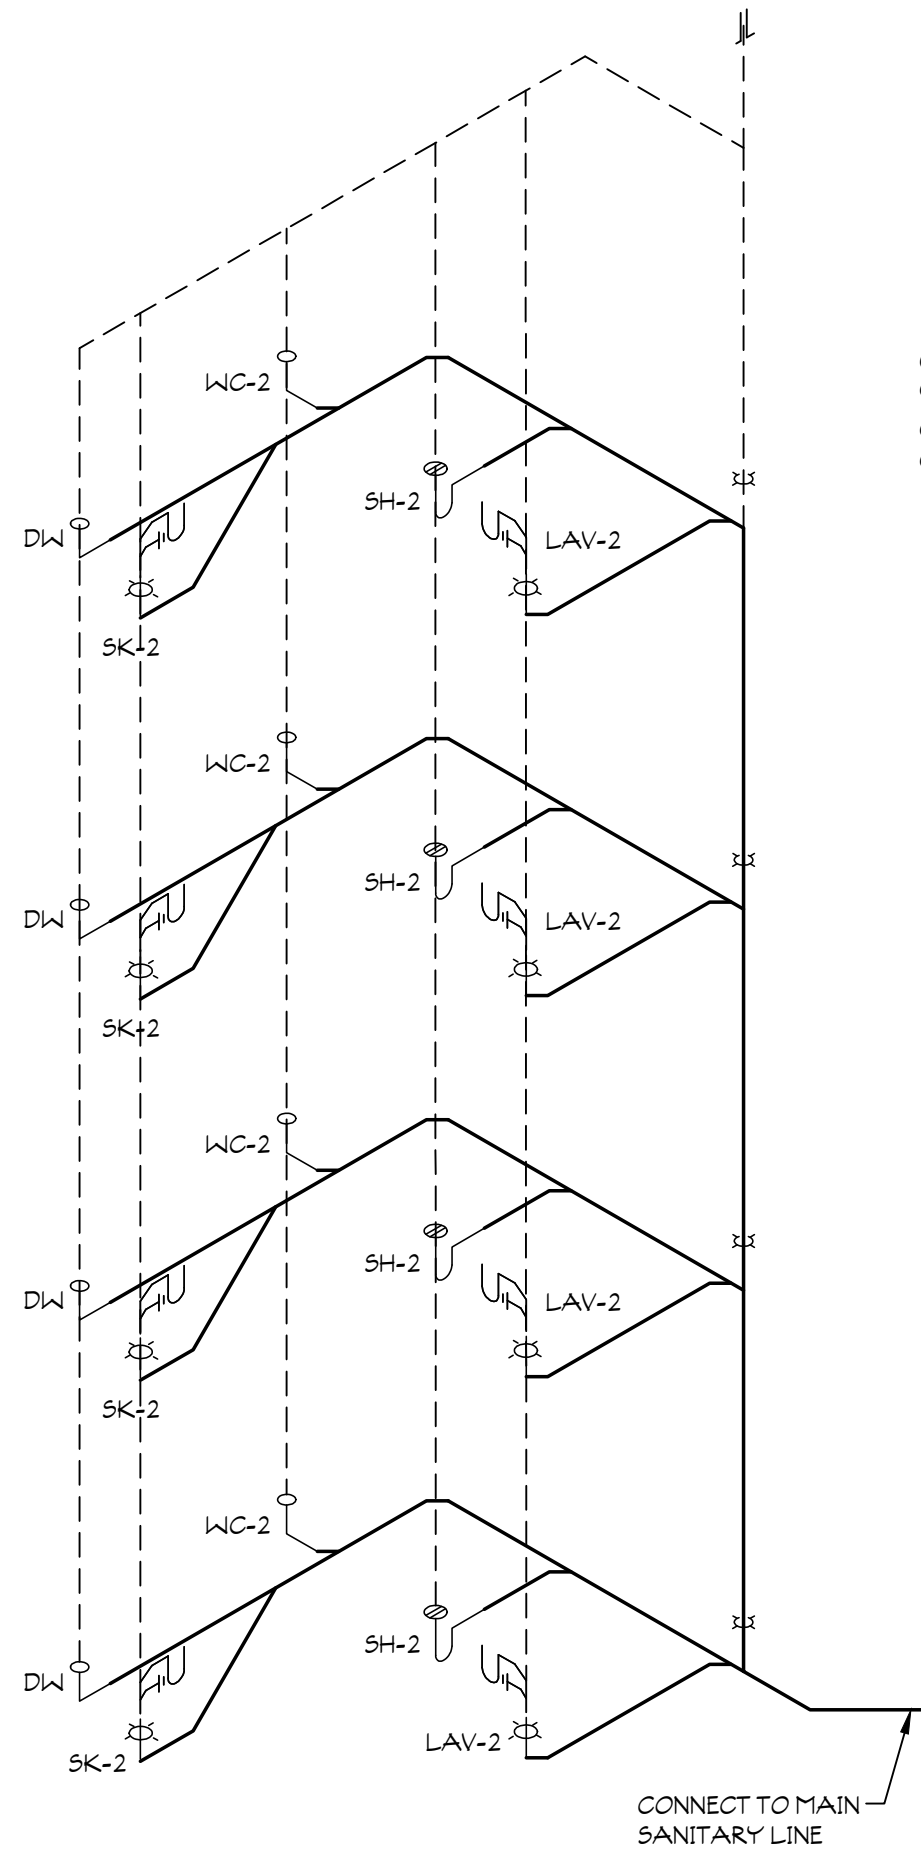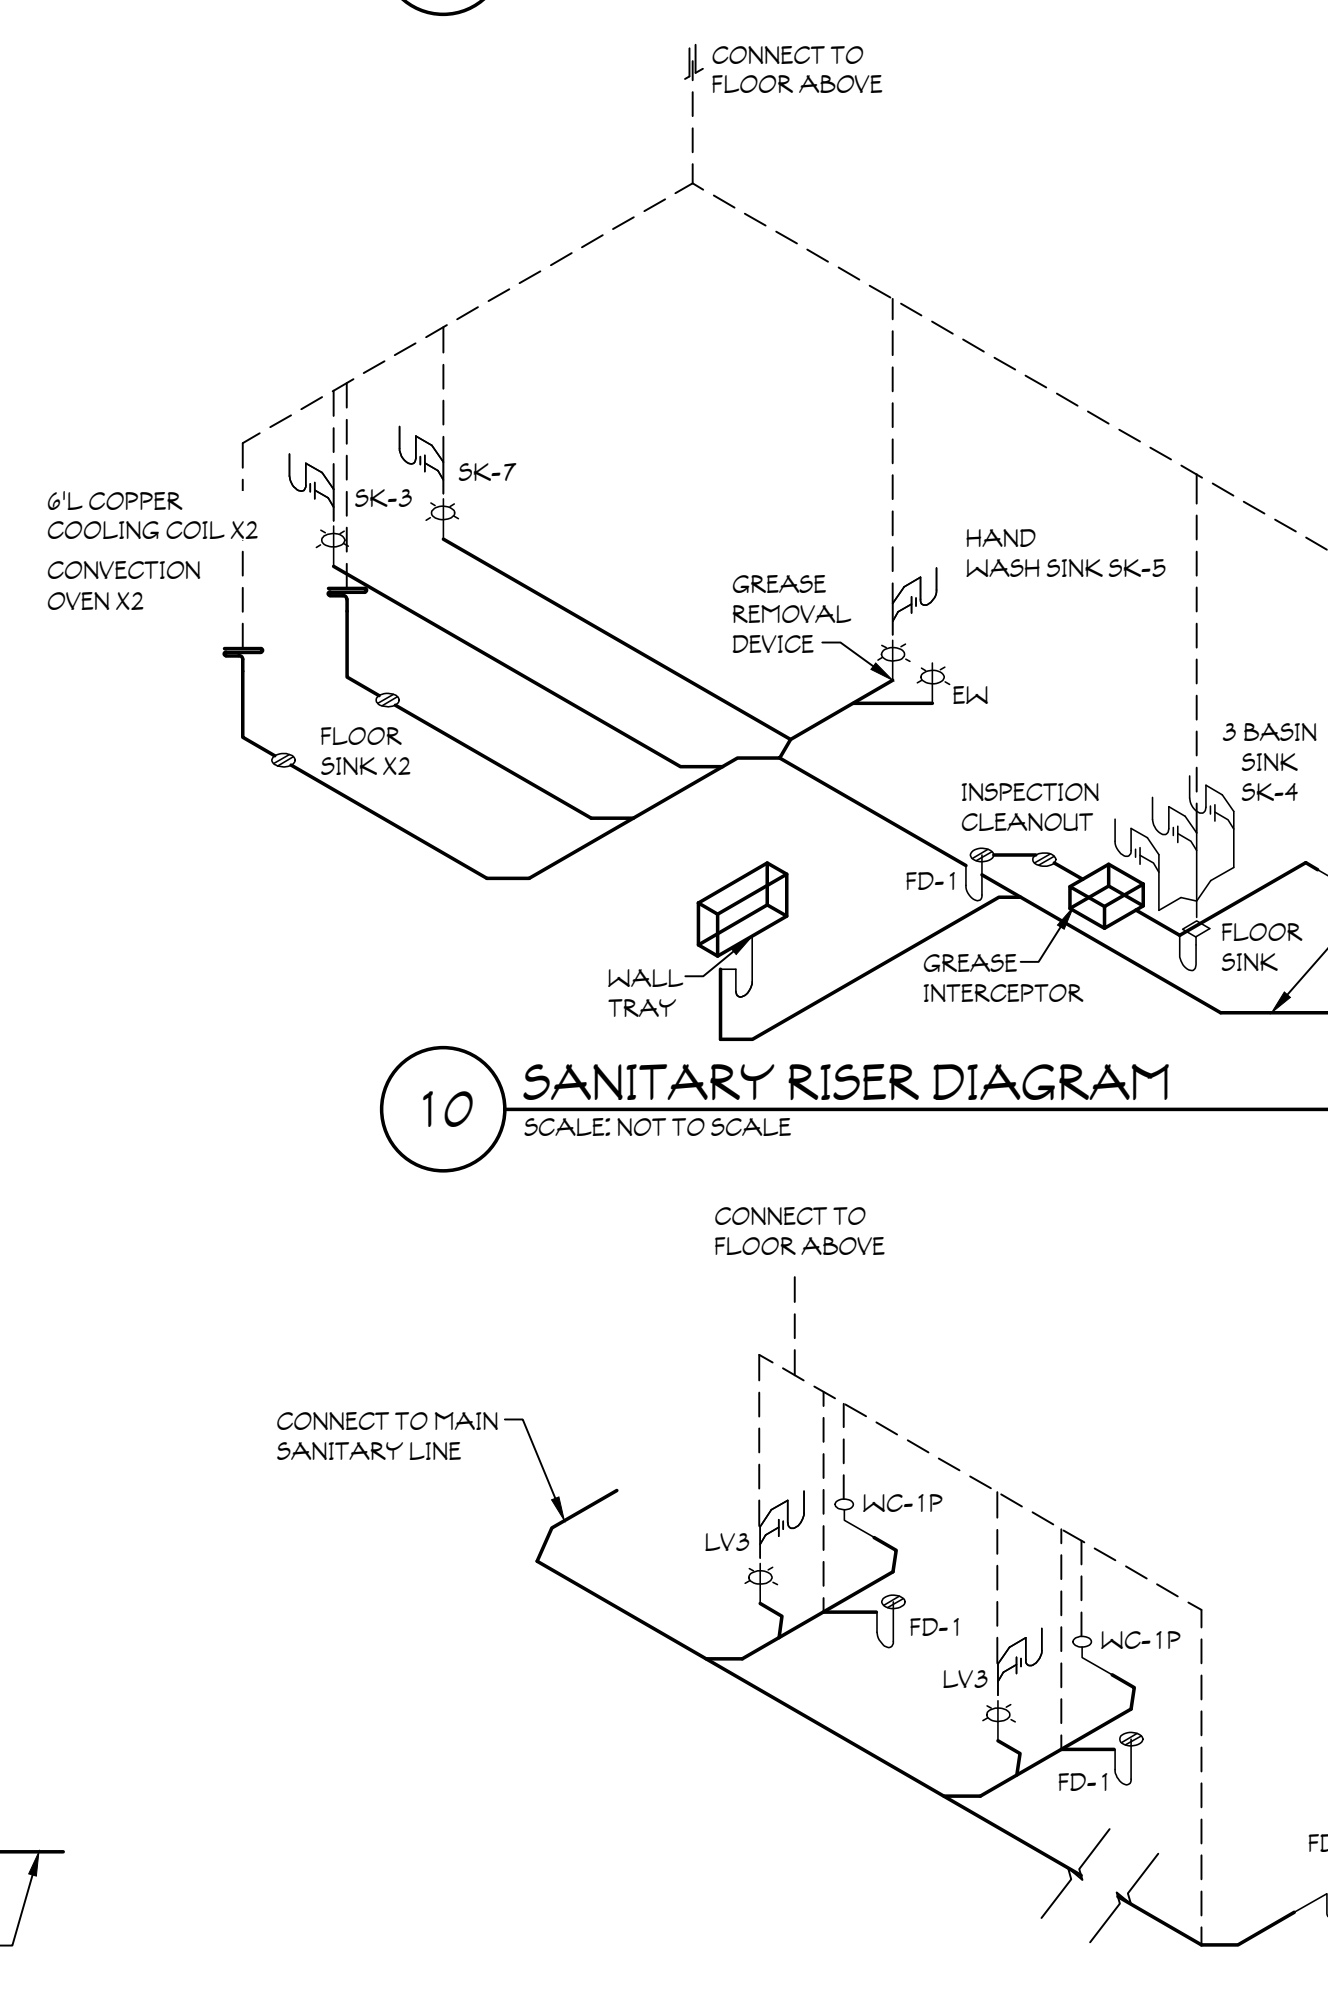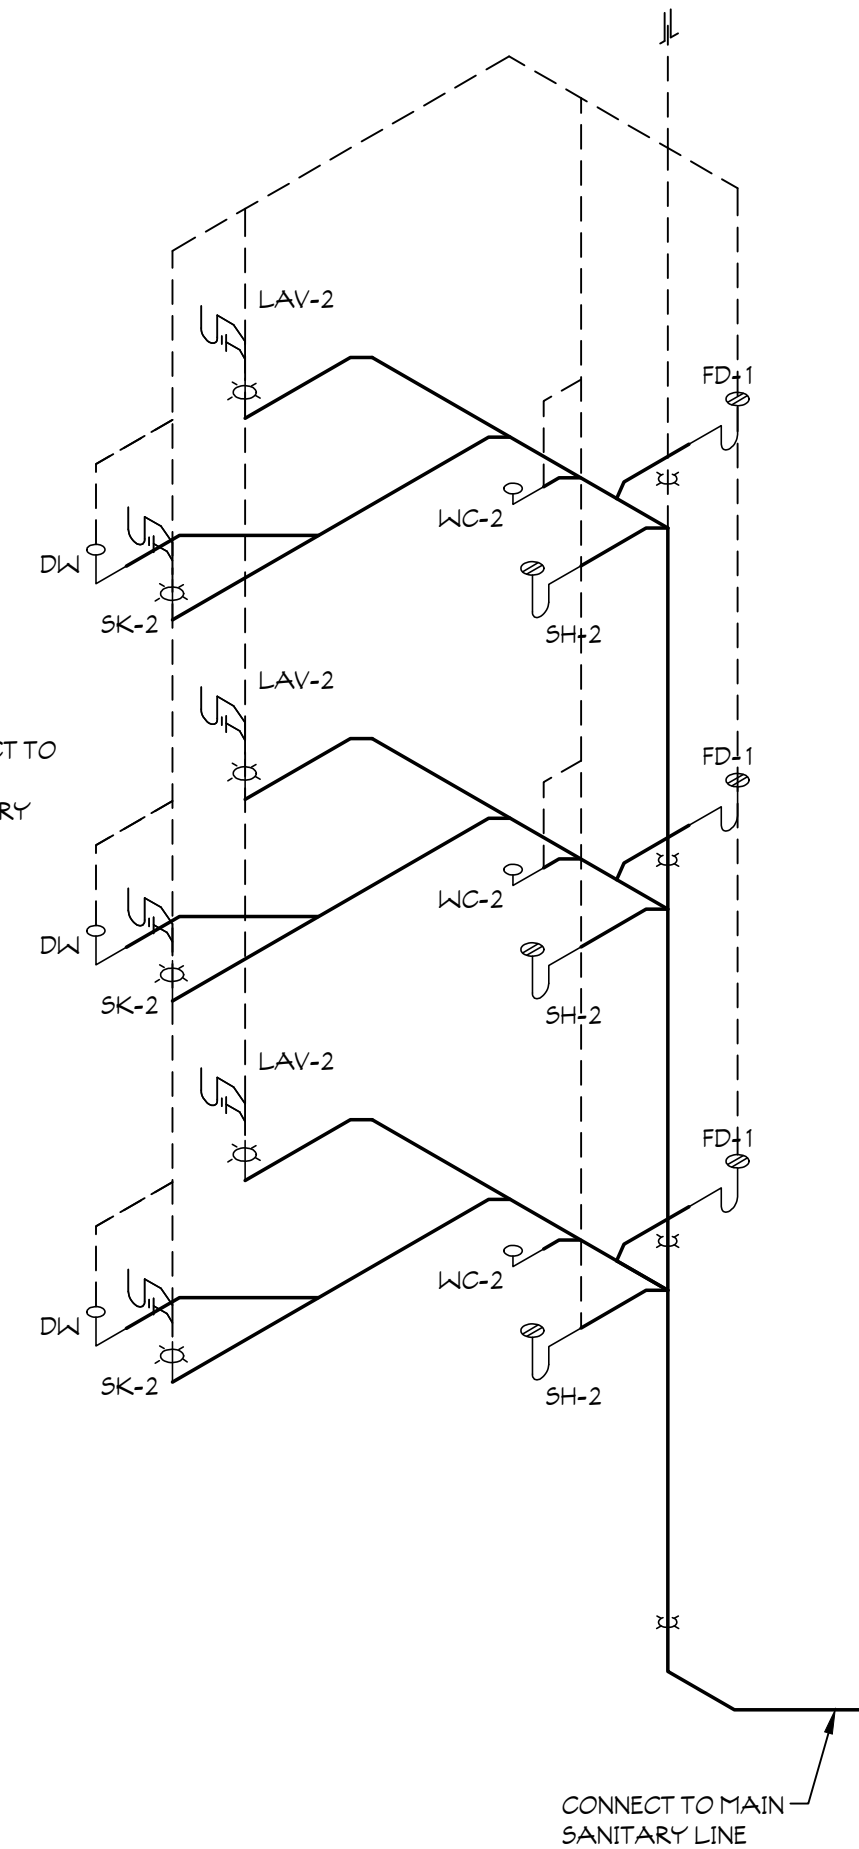**6 SANITARY RISER DIAGRAM**
SCALE: NOT TO SCALE**7 SANITARY RISER DIAGRAM**
SCALE: NOT TO SCALE**8 SANITARY RISER DIAGRAM**
SCALE: NOT TO SCALE**10 SANITARY RISER DIAGRAM**
SCALE: NOT TO SCALE**11 SANITARY RISER DIAGRAM**
SCALE: NOT TO SCALE

GENERAL NOTES

ALTHOUGH DRAWINGS ARE DRAWN TO SCALE, THE
AGENCY OF THE DRAWING CANNOT BE
RELIED UPON FOR EXACT DIMENSIONS.
OF REPRODUCTION, DIMENSIONS SHOULD BE DERIVED
FROM DIMENSIONED PLANS.

ALL DIMENSIONS IN THIS DRAWING ARE IN FEET AND INCHES.
DIMENSIONS SHALL NOT BE USED FOR ANY
GENERAL CONTRACTOR. THE ARCHITECT SHALL
BE RESPONSIBLE FOR THE ACCURACY OF THE
DIMENSIONS. THE ARCHITECT SHALL BE
BROUGHT TO THEIR ATTENTION PRIOR TO
CONSTRUCTION.

* Architects
* Plumbers
* Construction Mgmt.
* Rule 5 and MS4 Filing
* PHONE: (574) 537-8500
* FAX: (574) 537-0808
* 112 NORTH MAIN STREET
* GOSHEN, INDIANA 46526

MAUIST
ARCHITECTURAL
SERVICES
DIVISION OF
L.E.M., INC.

HOME
SUITES BY HILTON

SHEET SIZE 24x36

FT. WAYNE, INDIANA

REVISIONS:

PRELIMINARY - NOT
FOR CONSTRUCTION

DATE: 05/01/26

JOB NO.: MAS-26-105

NAME:

SANITARY RISER
DIAGRAMS

SHEET:

P004