


FOURTH FLOOR


THIRD FLOOR

SECOND FLOOR

FIRST FLOOR

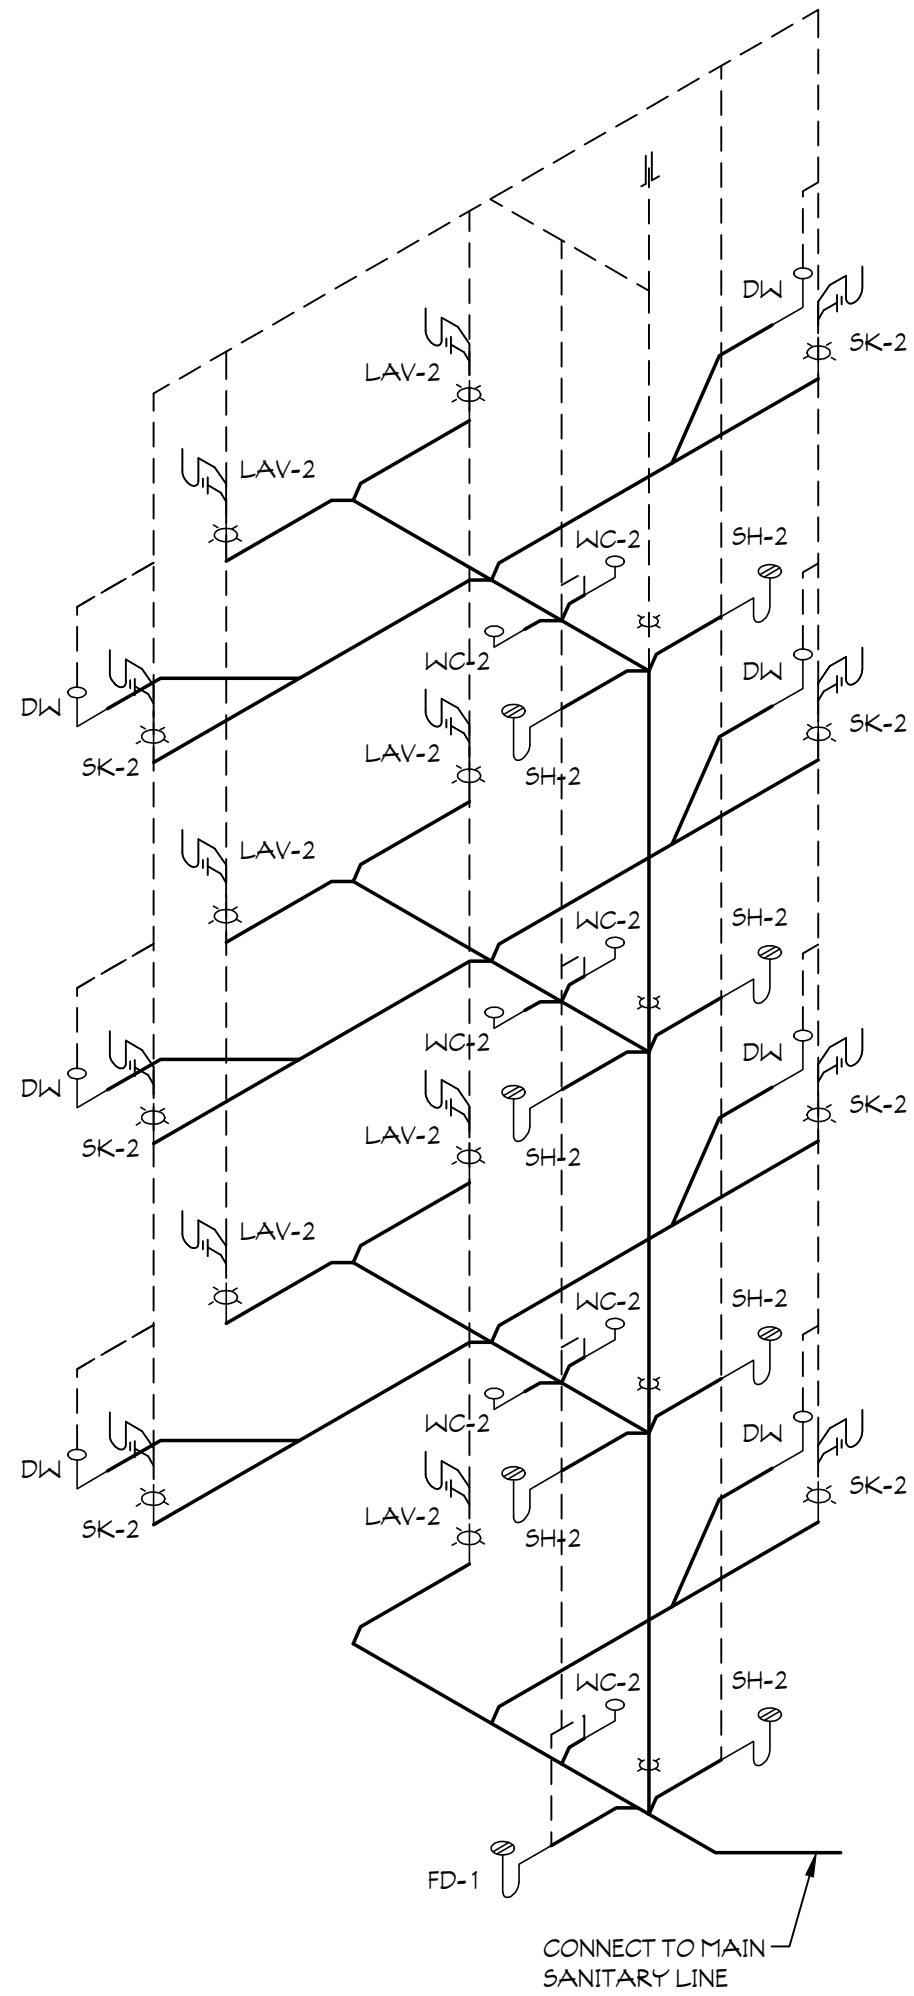

1 SANITARY RISER DIAGRAM
SCALE: NOT TO SCALE

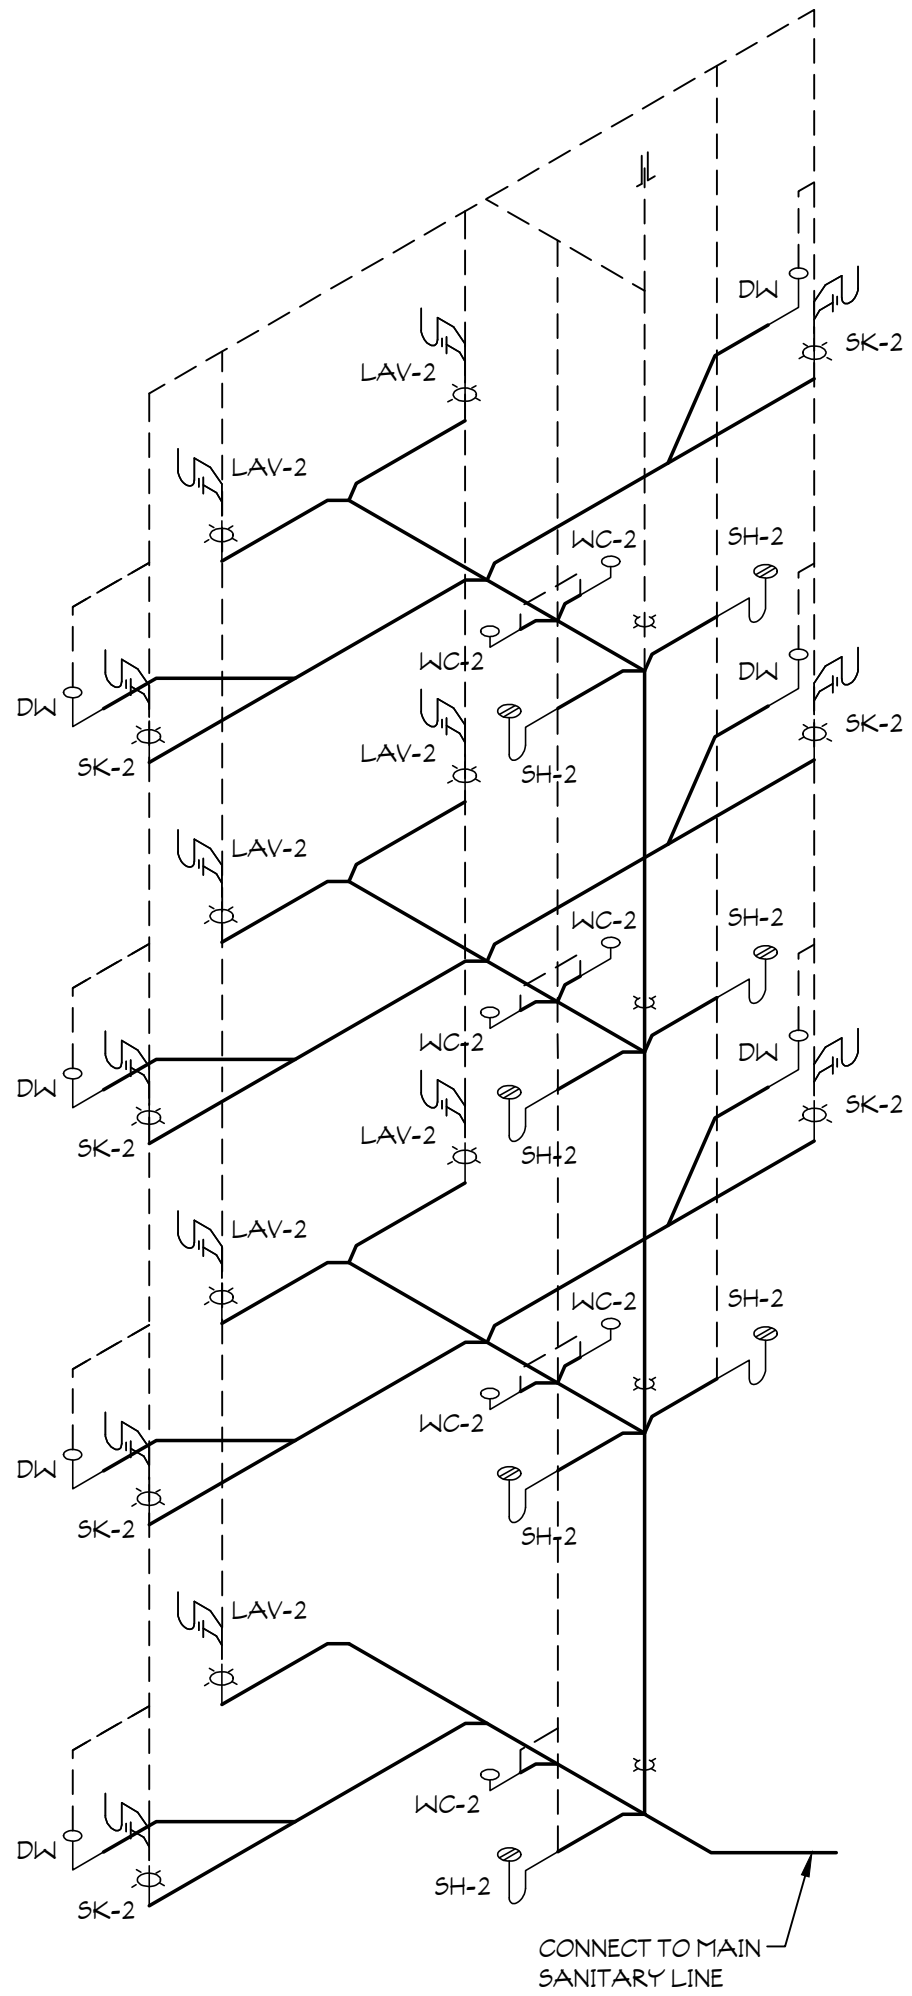

2 SANITARY RISER DIAGRAM
SCALE: NOT TO SCALE

NOTE:
3" VENT THROUGH ROOF TYPICAL
SEE FLOOR PLANS FOR ADA
TOILET LOCATIONS.
SEE FLOOR PLAN TO VERIFY TUB/
SHOWER TYPE

NOTE:
EACH ISO METRIC IS SHOWN AS A
REPRESENTATION, NOT A DIRECT
REFLECTION OF EACH SITUATION.
REFER TO SANITARY PLANS FOR
EXACT LAYOUT.

GENERAL NOTES

ALTHOUGH DRAWINGS ARE DRAWN TO SCALE, THE
ACCURACY OF THE DRAWINGS CANNOT BE
GUARANTEED. THE USER SHALL BE RESPONSIBLE
FOR VERIFICATION OF ALL DIMENSIONS AND
NOTATIONS. DIMENSIONS SHALL BE DERIVED
FROM DIMENSIONED PLANS.

ALL DIMENSIONS INCLUDE OPENING SIZES AND
FINISHES. THE USER SHALL BE RESPONSIBLE FOR ANY
GENERAL CONTRACTOR, PLUMBING CONTRACTOR, OR
OTHER PROFESSIONAL TO BE BROUGHT TO THEIR ATTENTION PRIOR TO
CONSTRUCTION.

Architects
Plumbers
Engineers
Construction Mgmt.
Rule 5 and MS4 Filing

MAUSET ARCHITECTURAL SERVICES
DIVISION OF
L.E.M., INC.
112 NORTH MAIN STREET
GOSHEN, INDIANA 46526
PHONE (574) 537-8500
FAX (574) 537-0808

These drawings are the property of Maset Architectural Services, Inc. and may not be reproduced, copied,
or used in any manner without the express written consent of Maset Architectural Services, Inc.

HOME 2
SUITES BY HILTON

SHEET SIZE 24x36

FT. WAYNE, INDIANA

REVISIONS:

PRELIMINARY - NOT FOR CONSTRUCTION

DATE: 05/01/26
JOB NO.: MAS-26-105
NAME: SANITARY RISER DIAGRAMS
SHEET: P005