


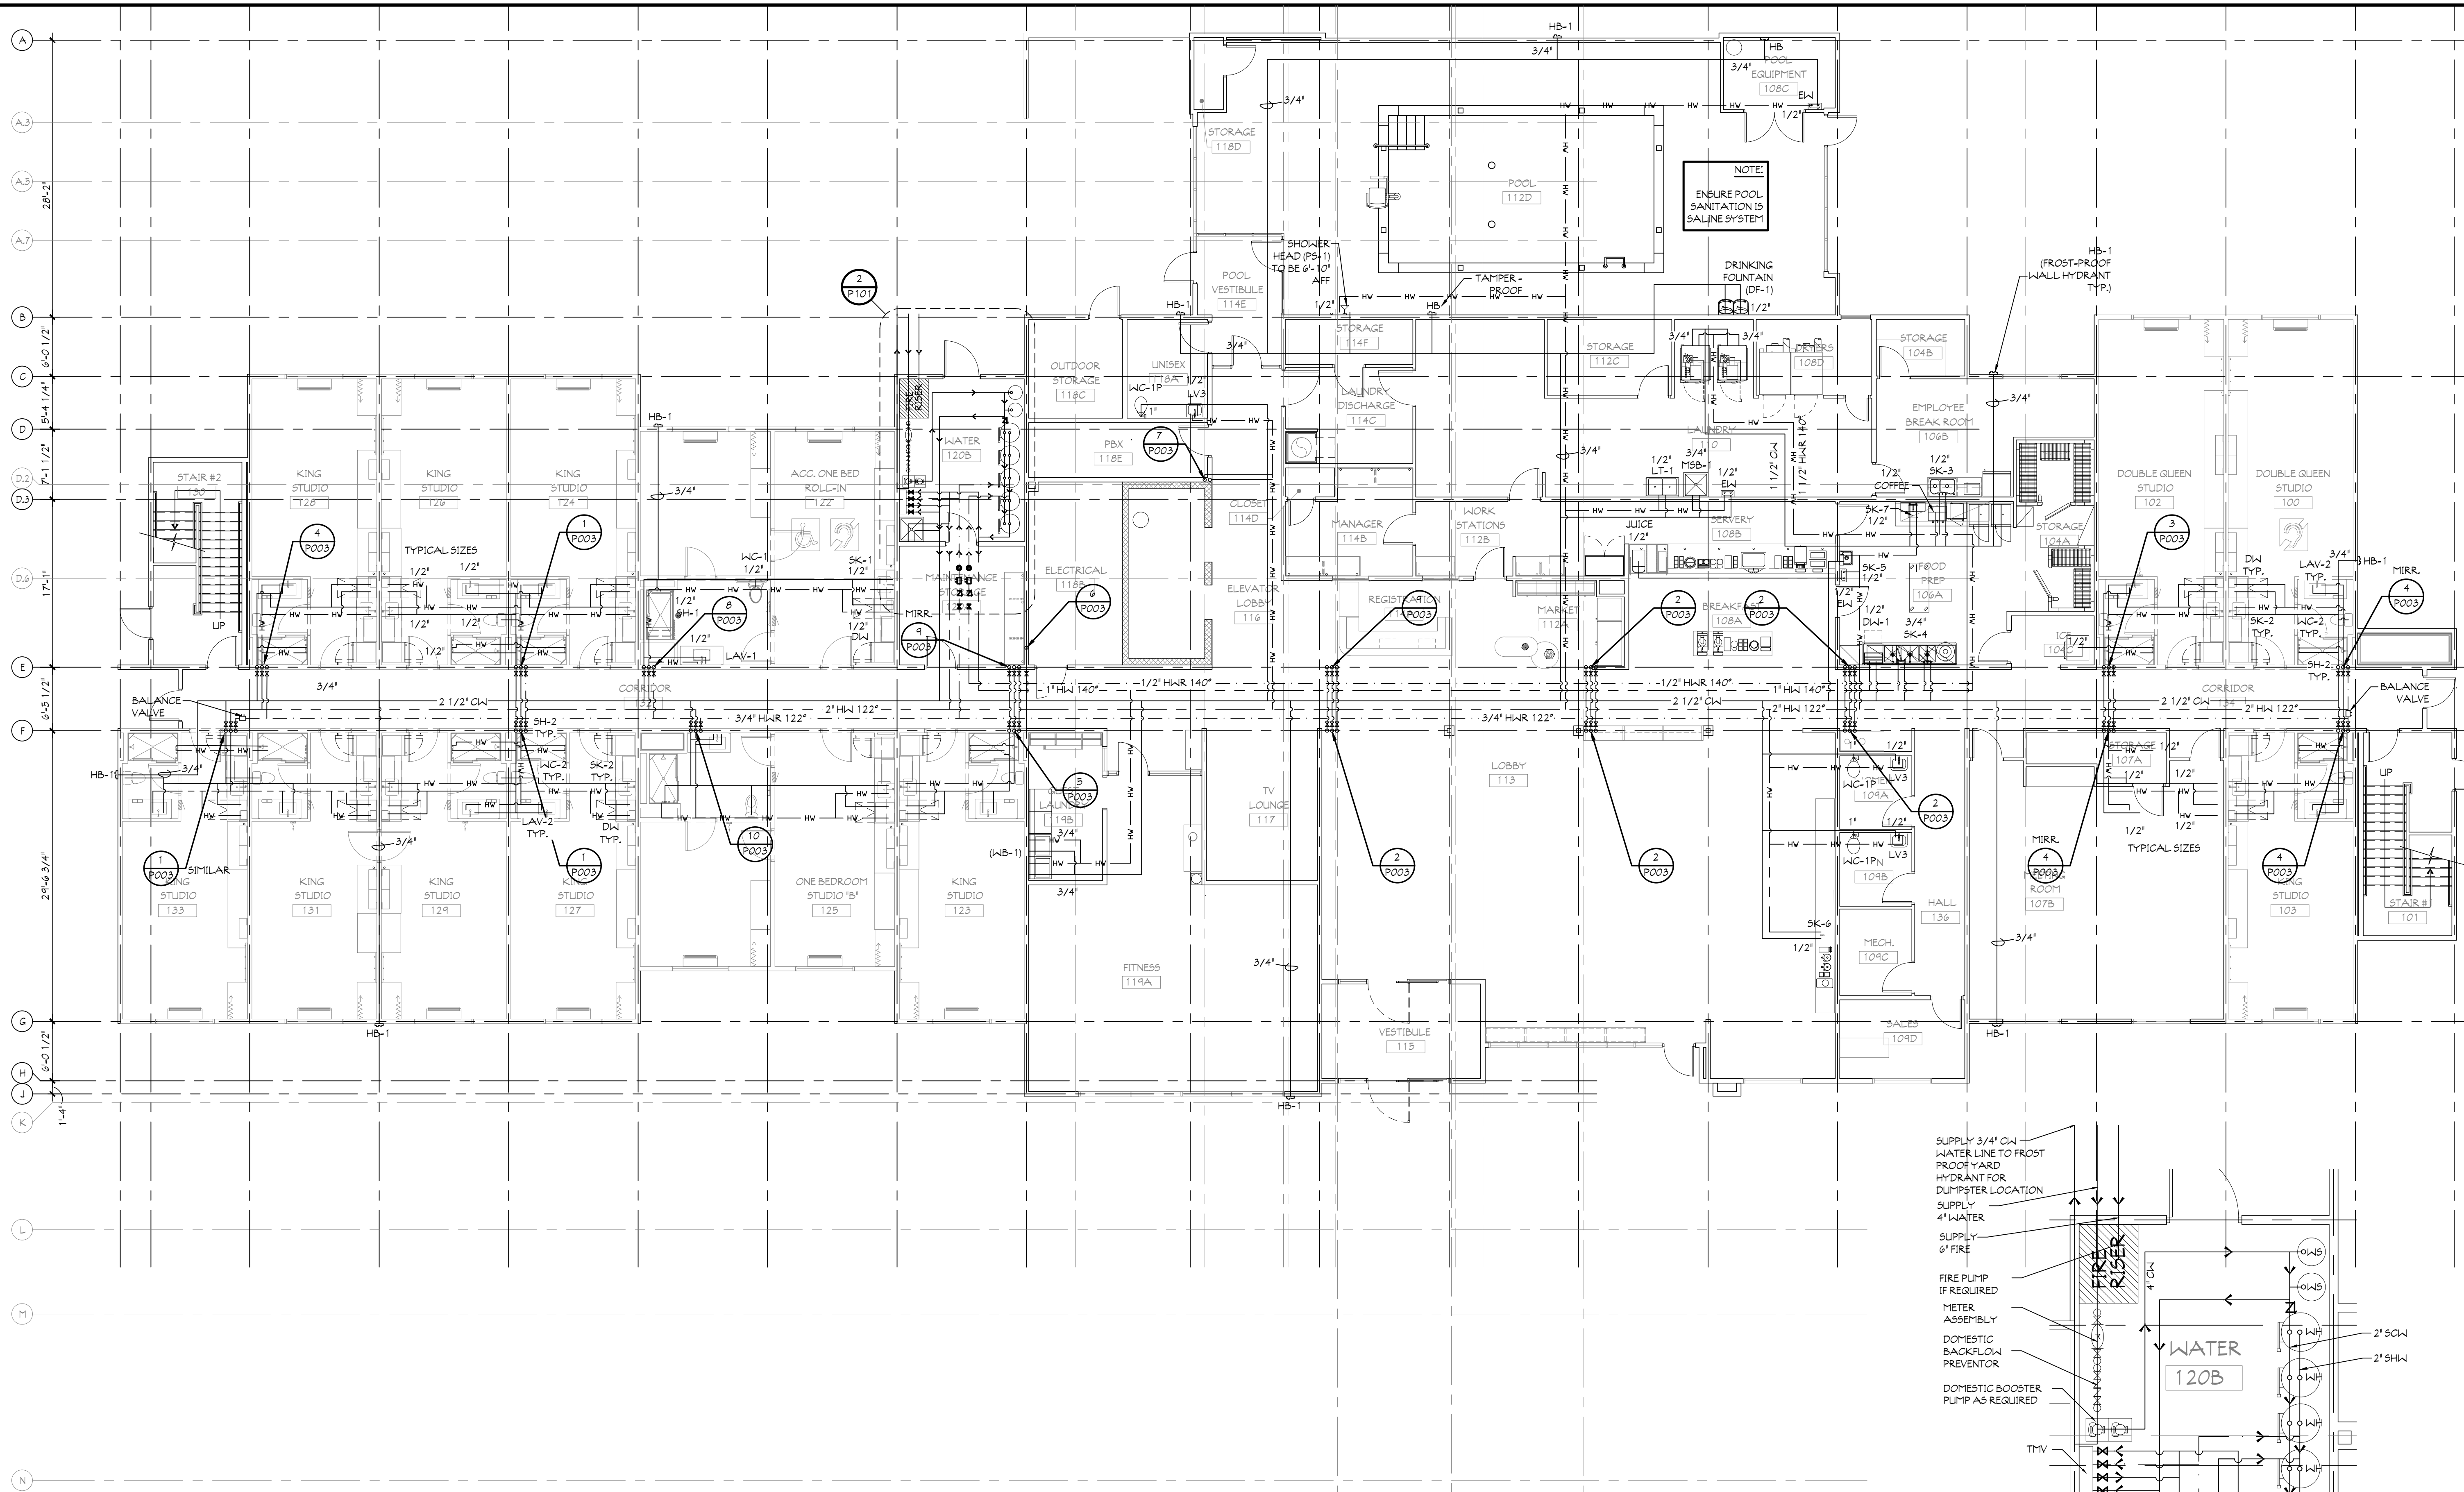

GENERAL NOTES:


ALL TRADES NEED TO FIRE CAULK THEIR OWN PENETRATIONS PER CODE.

ANY DAMAGE TO FINISHED DRYWALL OR FINISHED SURFACE WILL BE THE RESPONSIBILITY OF THE SUB CONTRACTOR

ALL SUBCONTRACTORS ARE RESPONSIBLE TO CLEAN UP ALL DEBRIS AND MATERIALS AT THE END OF EACH DAY

1 FIRST FLOOR PLUMBING PLAN
SCALE: 1/8" = 1'-0"

2 WATER ROOM
SCALE: 1/4" = 1'-0"

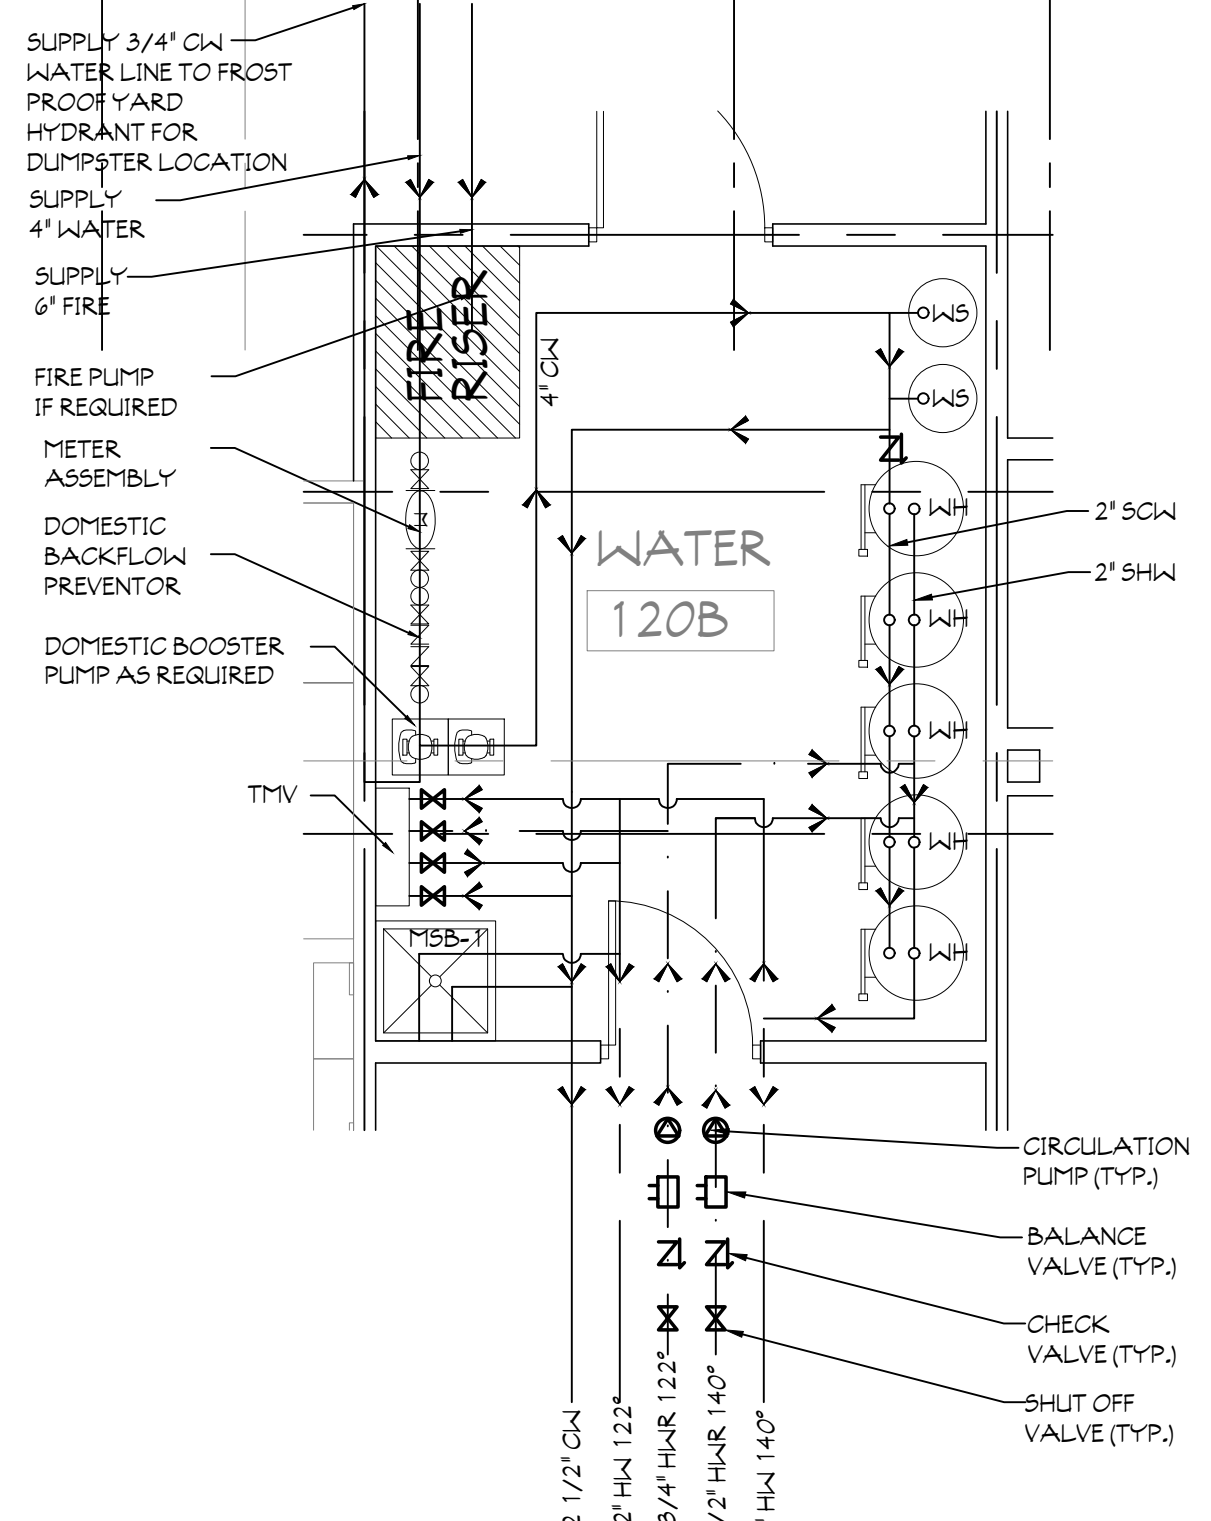

GENERAL NOTES

ALTHOUGH DRAWINGS ARE DRAWN TO SCALE, THE ACCURACY OF THE DRAWINGS CANNOT BE GUARANTEED. THE CONTRACTOR SHALL VERIFY ALL DIMENSIONS AND CONDITIONS PRIOR TO CONSTRUCTION. DIMENSIONS SHALL BE DELETED FROM DIMENSIONED PLANS.

ALL DIMENSIONS UNLESS OTHERWISE NOTED SHALL BE IN FEET AND INCHES. DIMENSIONS SHALL NOT BE HELD RESPONSIBLE FOR ANY CONSTRUCTION. THE CONTRACTOR SHALL BE RESPONSIBLE FOR OBTAINING ALL NECESSARY PERMITS AND APPROVALS PRIOR TO CONSTRUCTION.

Architects
Planners
* Rule 5 and MS4 Filing
* Construction Memo
* L.E.M., INC.
112 NORTH MAIN STREET
GOSHEN, INDIANA 46526
PHONE (574) 537-8500
FAX (574) 537-0808

MAUST ARCHITECTURAL SERVICES

HOME 2
SUITES BY HILTON

SHEET SIZE 24x36

FT. WAYNE, INDIANA

REVISIONS:

DATE: 05/01/26
JOB NO.: MAS-26-105
NAME: FIRST FLOOR PLUMBING PLAN
SHEET: P101