


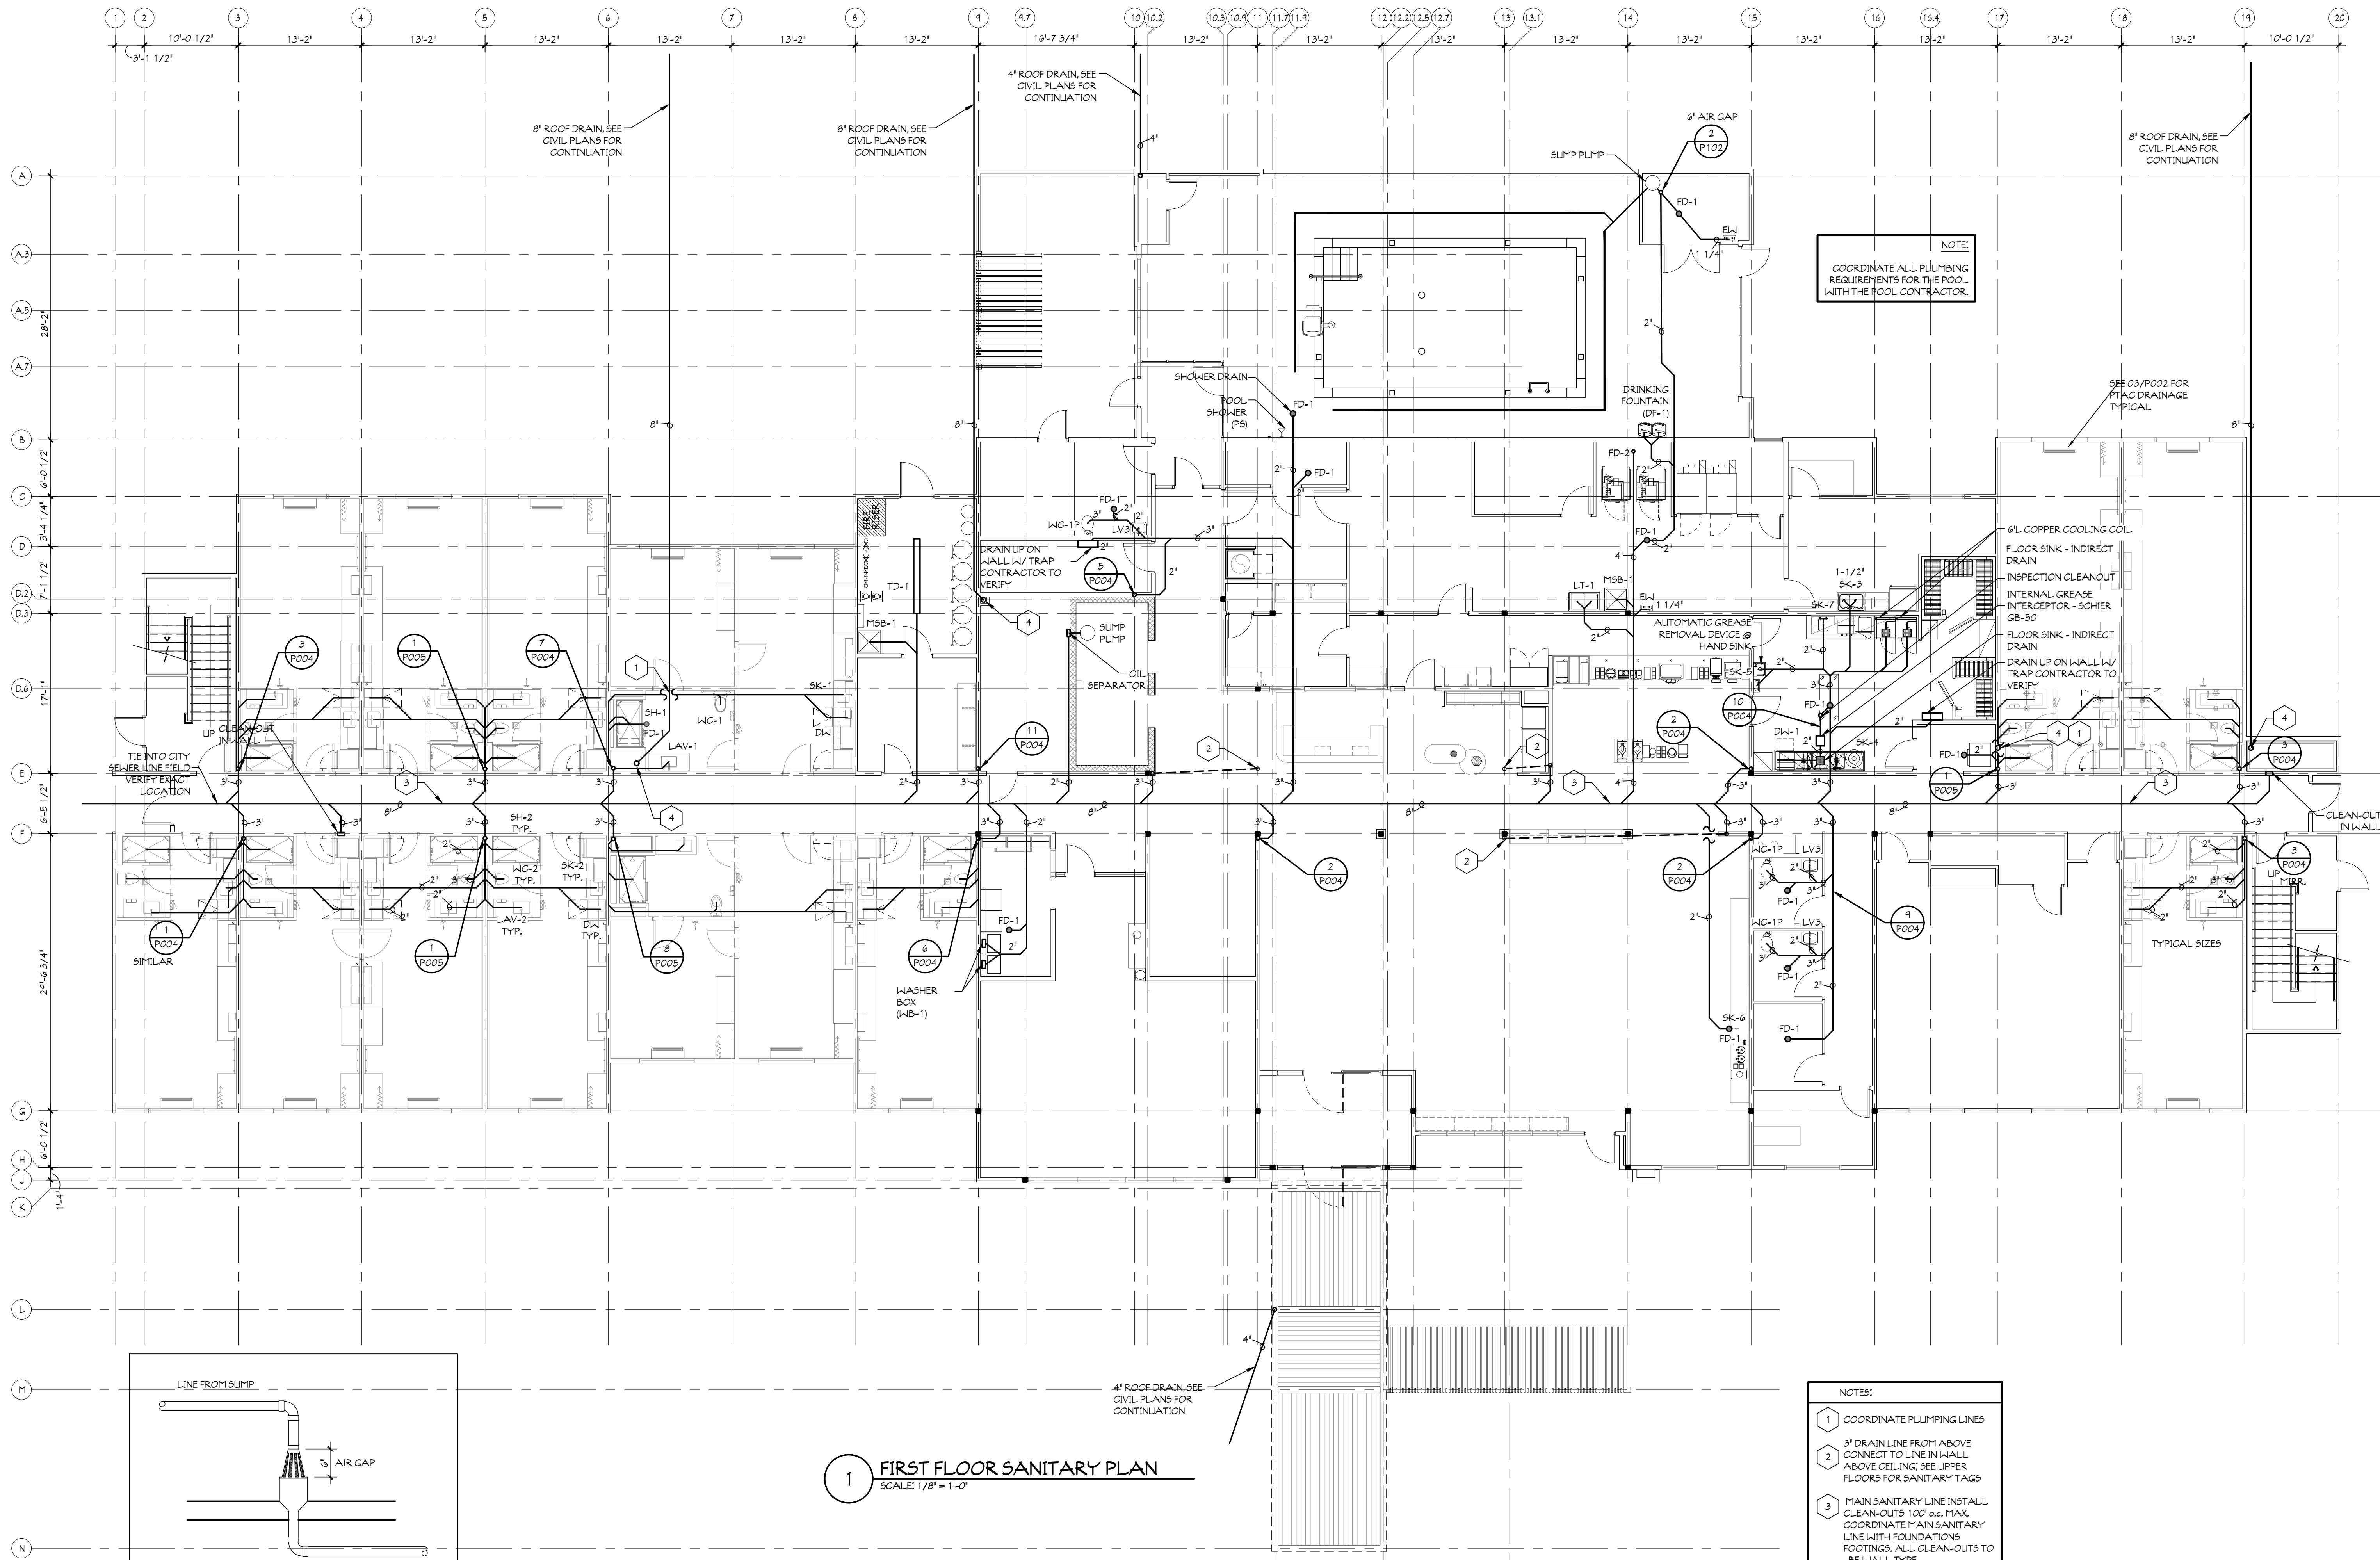

2 POOL SUMP AIR GAP DETAIL
SCALE: 3/4" = 1'-0"

1 FIRST FLOOR SANITARY PLAN
SCALE: 1/8" = 1'-0"

- NOTES:
- 1 COORDINATE PLUMBING LINES
 - 2 3" DRAIN LINE FROM ABOVE CONNECT TO LINE IN WALL ABOVE CEILING; SEE UPPER FLOORS FOR SANITARY TAGS
 - 3 MAIN SANITARY LINE INSTALL CLEAN-OUTS 100' o.c. MAX. COORDINATE MAIN SANITARY LINE WITH FOUNDATIONS FOOTINGS. ALL CLEAN-OUTS TO BE WALL TYPE
 - 4 6" ROOF DRAIN LINE UP TO ROOF
- PLUMBING CONTRACTOR TO VERIFY ALL PIPING AND EQUIPMENT

GENERAL NOTES

ALTHOUGH DRAWINGS ARE PREPARED TO SCALE, THE ACCURACY OF THE DRAWINGS CANNOT BE GUARANTEED. THE CONTRACTOR SHALL BE RESPONSIBLE FOR THE VERIFICATION OF ALL DIMENSIONS AND CONDITIONS PRIOR TO CONSTRUCTION. DIMENSIONS SHOWN ON THE DRAWINGS SHALL BE USED FOR CONSTRUCTION UNLESS OTHERWISE NOTED.

* Architects

MAUST ARCHITECTURAL SERVICES
DIVISION OF
L.E.M., INC.
112 NORTH MAIN STREET
GOSHEN, INDIANA 46526
PHONE: (574) 537-4500
FAX: (574) 537-0808

* Plumbers

* Construction Mgmt.
* Rule 5 and MS4 Filing

HOME 2
SUITES BY HILTON

SHEET SIZE 24x36

FT. WAYNE, INDIANA

REVISIONS:

PRELIMINARY - NOT FOR CONSTRUCTION

DATE: 05/01/26

JOB NO.: MAS-26-105

NAME:

FIRST FLOOR

SANITARY PLAN

SHEET:

P102