


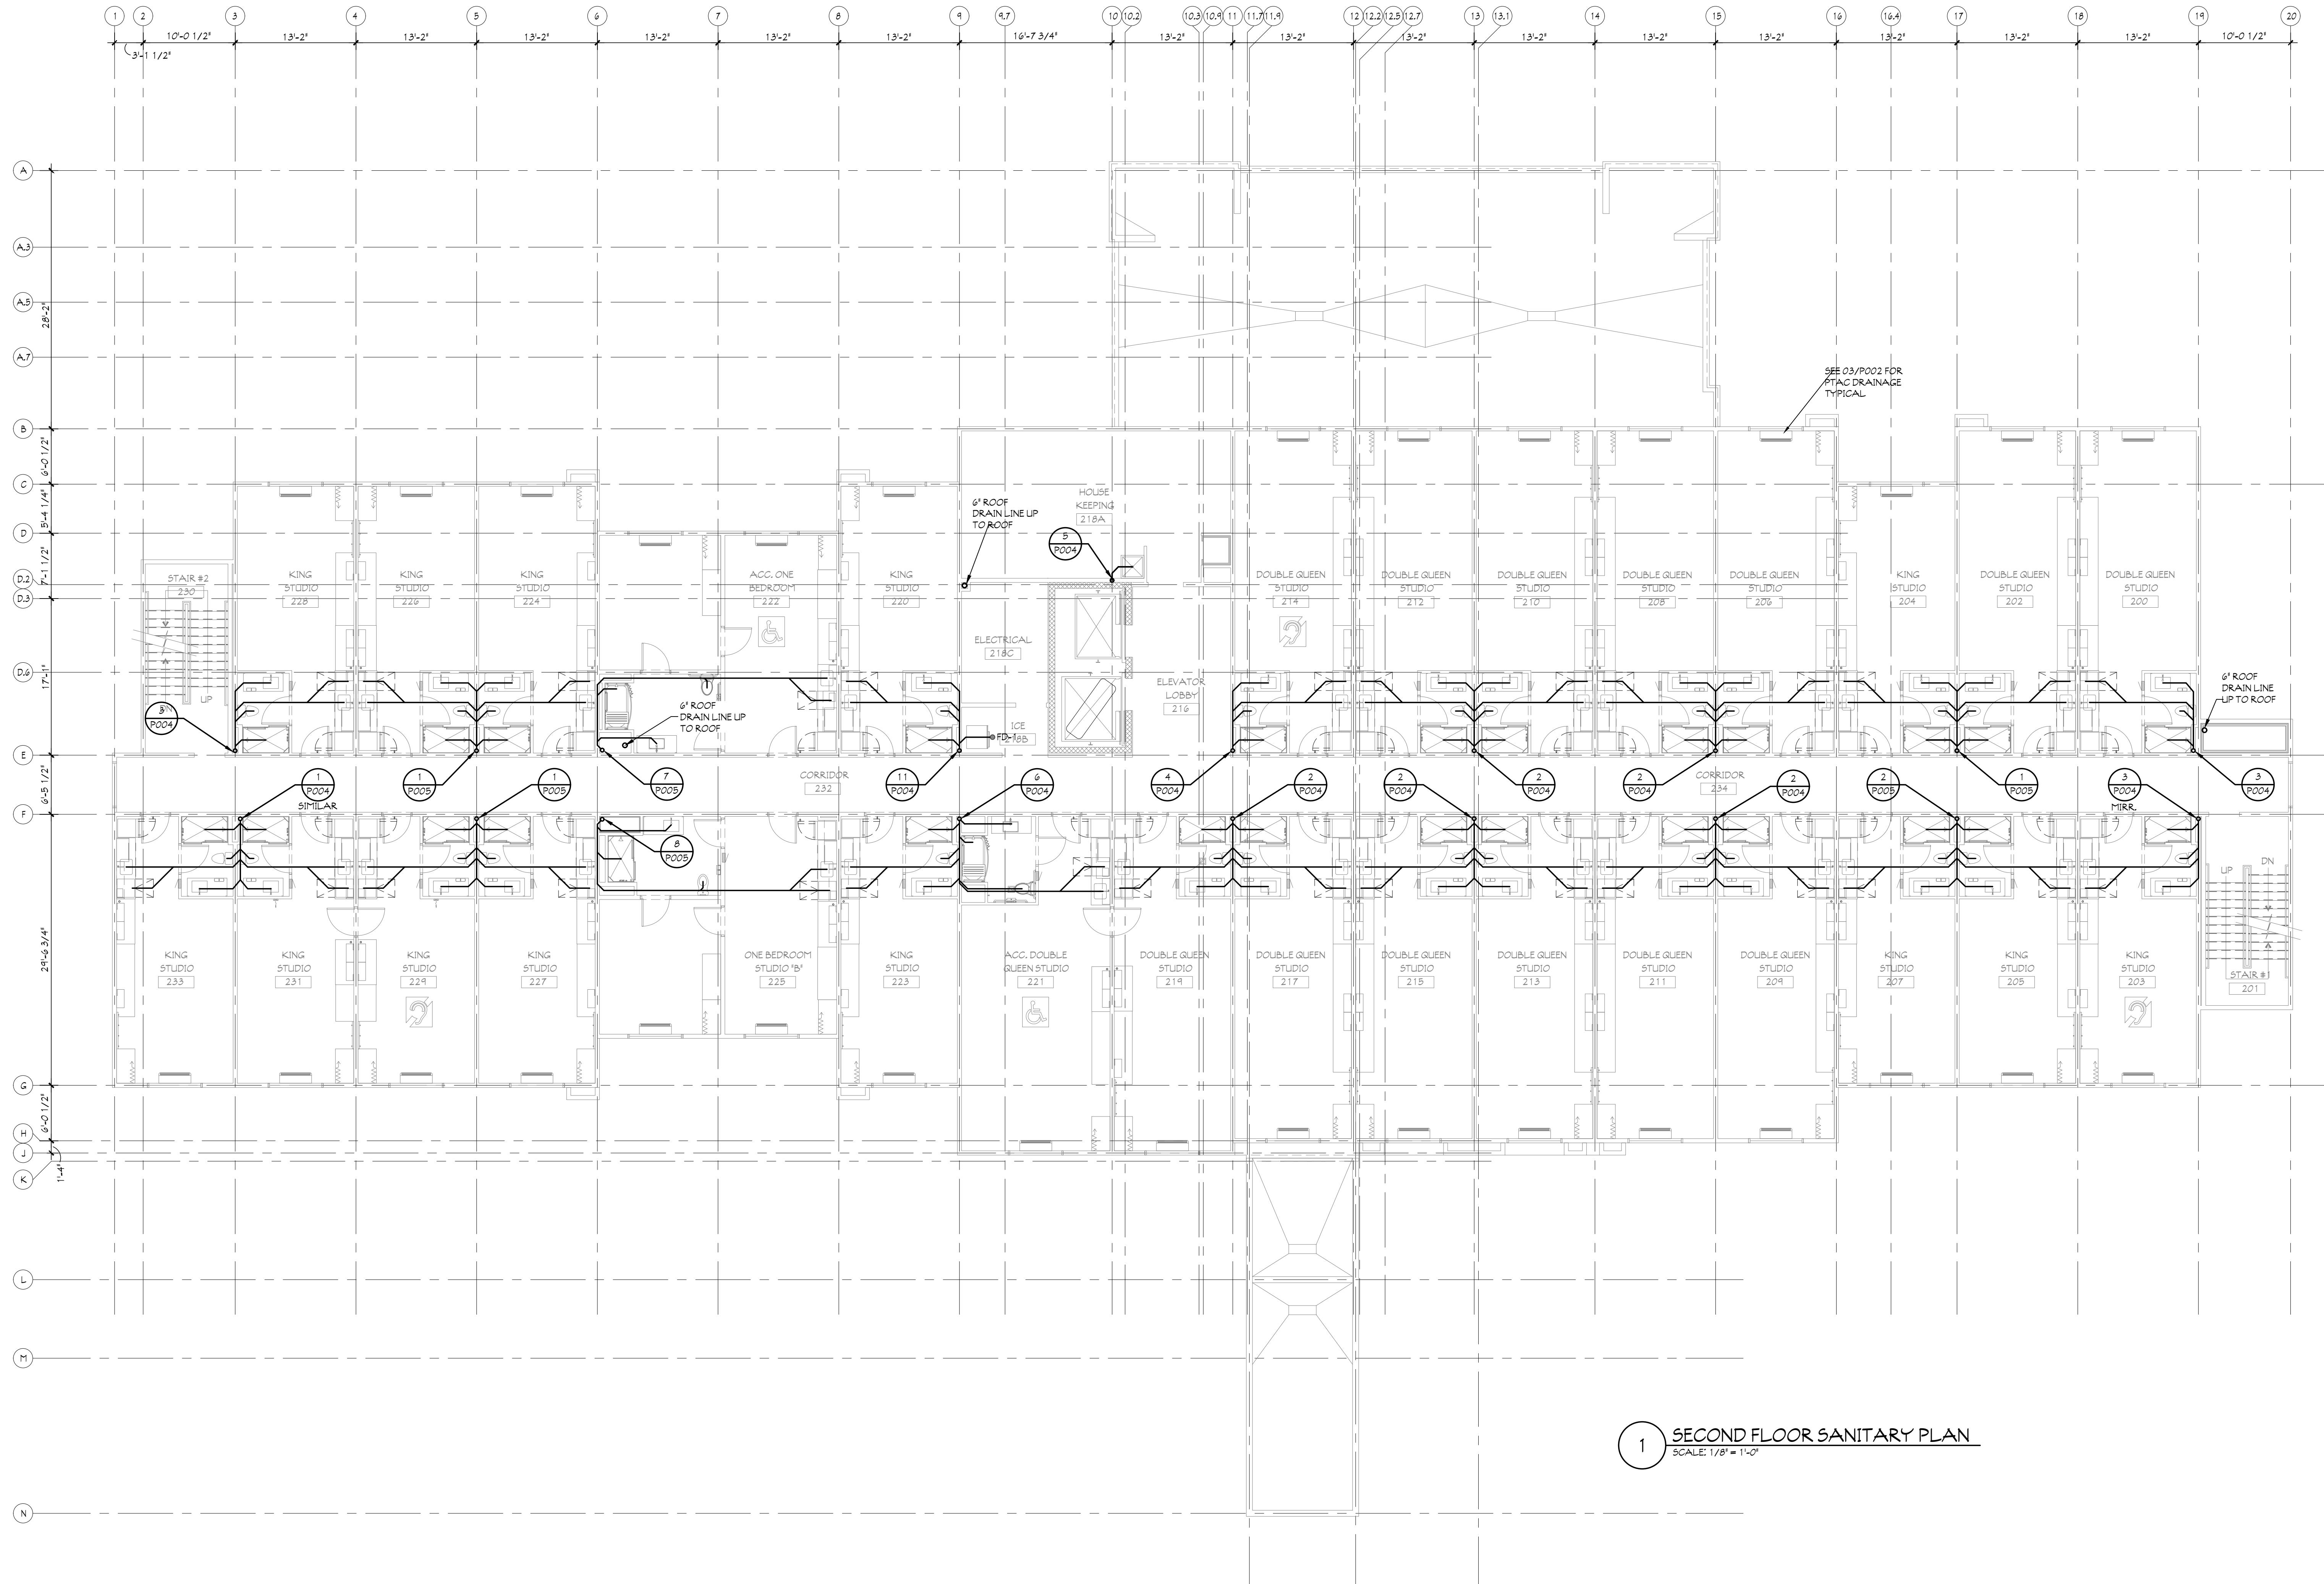

1 SECOND FLOOR SANITARY PLAN
SCALE: 1/8" = 1'-0"


GENERAL NOTES

ALTHOUGH DRAWINGS ARE PREPARED TO SCALE, THE
ACCURACY OF THE DRAWINGS CANNOT BE
GUARANTEED. THE USER SHALL BE RESPONSIBLE FOR
OBTAINING ALL NECESSARY PERMITS AND
OBTAINING ALL NECESSARY INFORMATION FROM
THE FIELD PRIOR TO CONSTRUCTION.
ALL DIMENSIONS UNLESS OTHERWISE NOTED
SHALL BE IN FEET AND INCHES. DIMENSIONS
SHALL BE GIVEN TO THE CENTERLINE UNLESS
OTHERWISE NOTED. THE USER SHALL BE
RESPONSIBLE FOR OBTAINING ALL NECESSARY
INFORMATION FROM THE FIELD PRIOR TO
CONSTRUCTION.

* Architects
* Plumbers
* Electricians
* Construction Mgmt.
* Rule 5 and M54 Filing
* L.E.M., INC.
PHONE: (574) 537-4500
FAX: (574) 537-0808
112 NORTH MAIN STREET
GOSHEN, INDIANA 46526

MAUST ARCHITECTURAL SERVICES
DIVISION OF
L.E.M., INC.

These drawings are the property of Maust Architectural Services and may not be copied, reproduced, or used in any manner without the written consent of Maust Architectural Services.

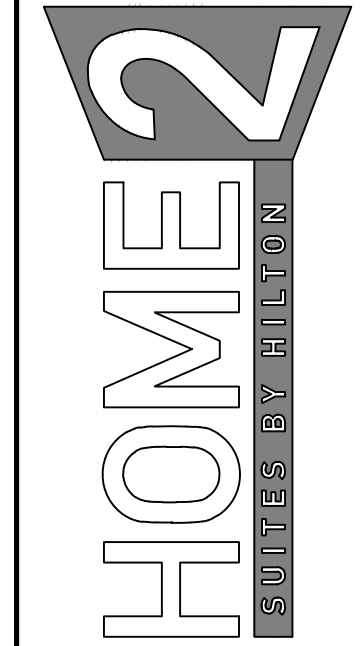

SHEET SIZE 24x36

FT. WAYNE, INDIANA

REVISIONS:	

DATE: 05/01/26
JOB NO.: MAS-26-105
NAME:
SECOND FLOOR
SANITARY PLAN
SHEET:
P202