



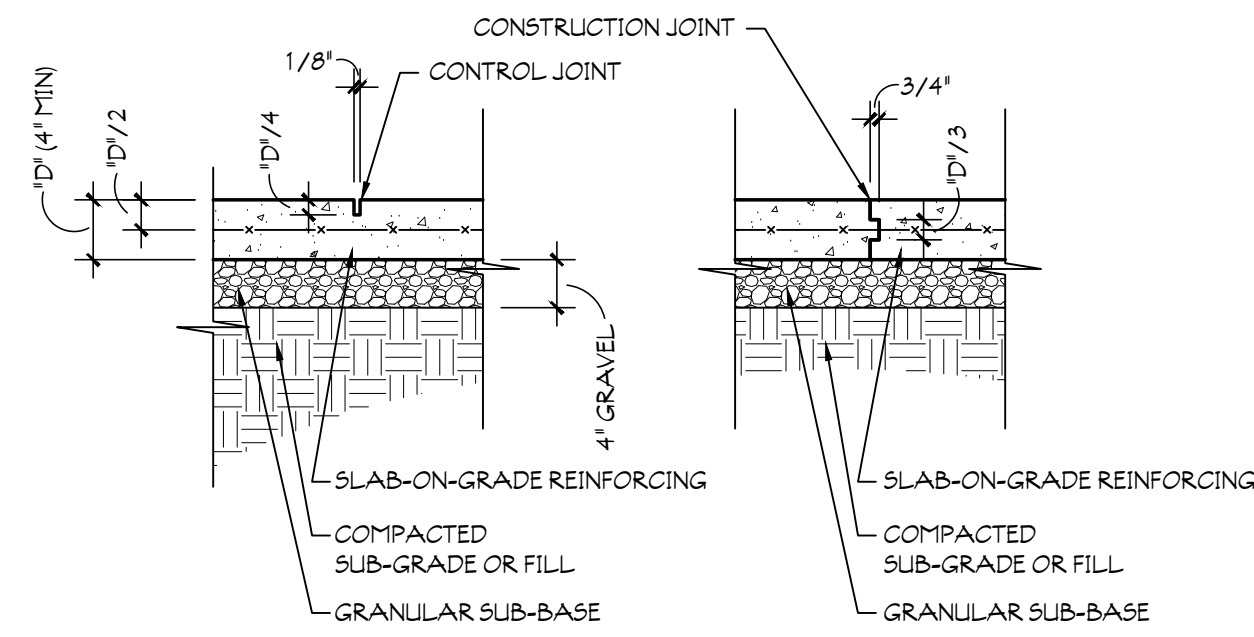


- NOTE:
1. SAW-CUT CONTROL JOINTS WITHIN 12 HOURS OF SLAB PLACEMENT. PROVIDE JOINT SEALANT.
 2. CLEAN ALL SURFACES IN FUTURE CONTACT WITH CONCRETE AT CONSTRUCTION JOINTS PRIOR TO PLACING NEW CONCRETE.


1 CONC. SLAB SECTION
SCALE: 3/4" = 1'-0"

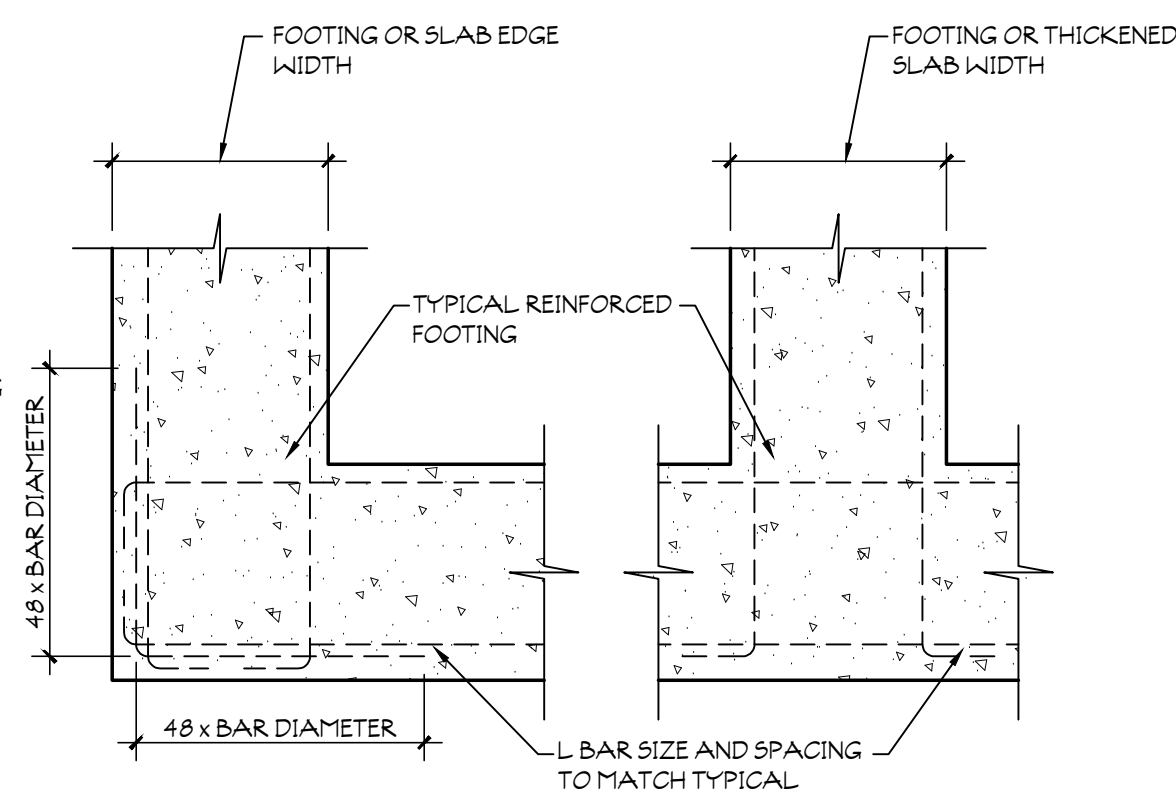


2 FOOTING DETAIL
SCALE: 3/4" = 1'-0"

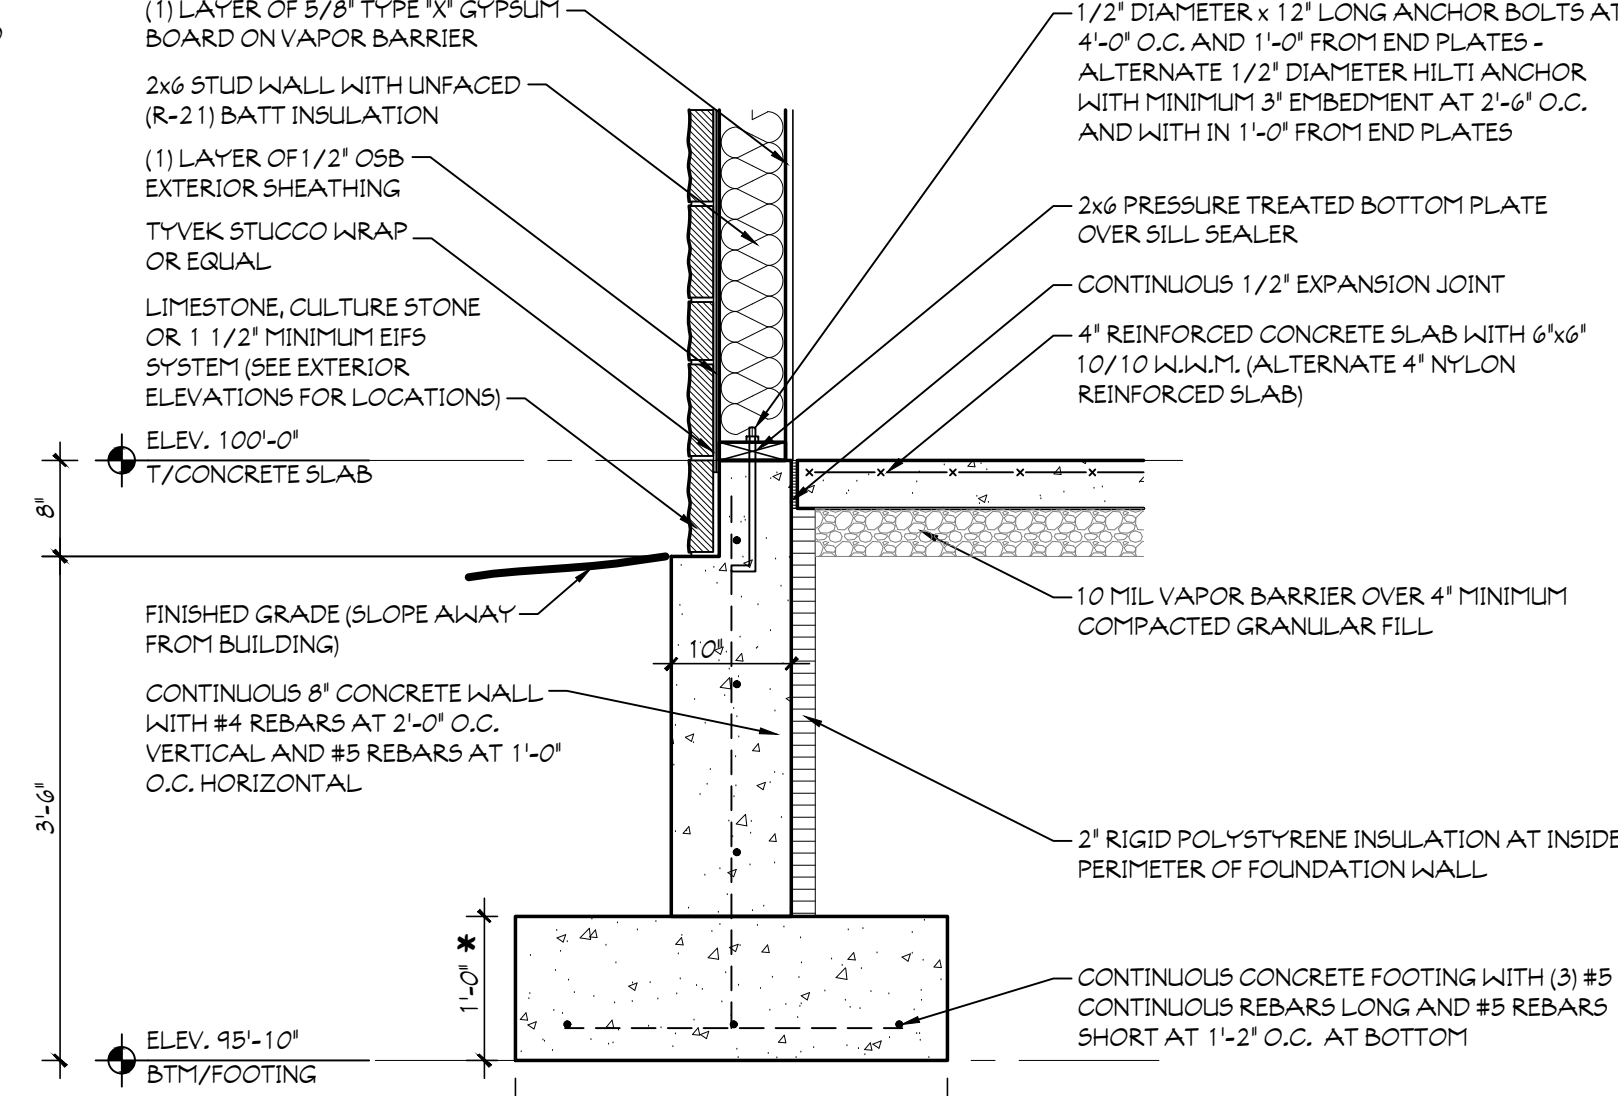


3 FOUNDATION SECTION
SCALE: 3/4" = 1'-0"

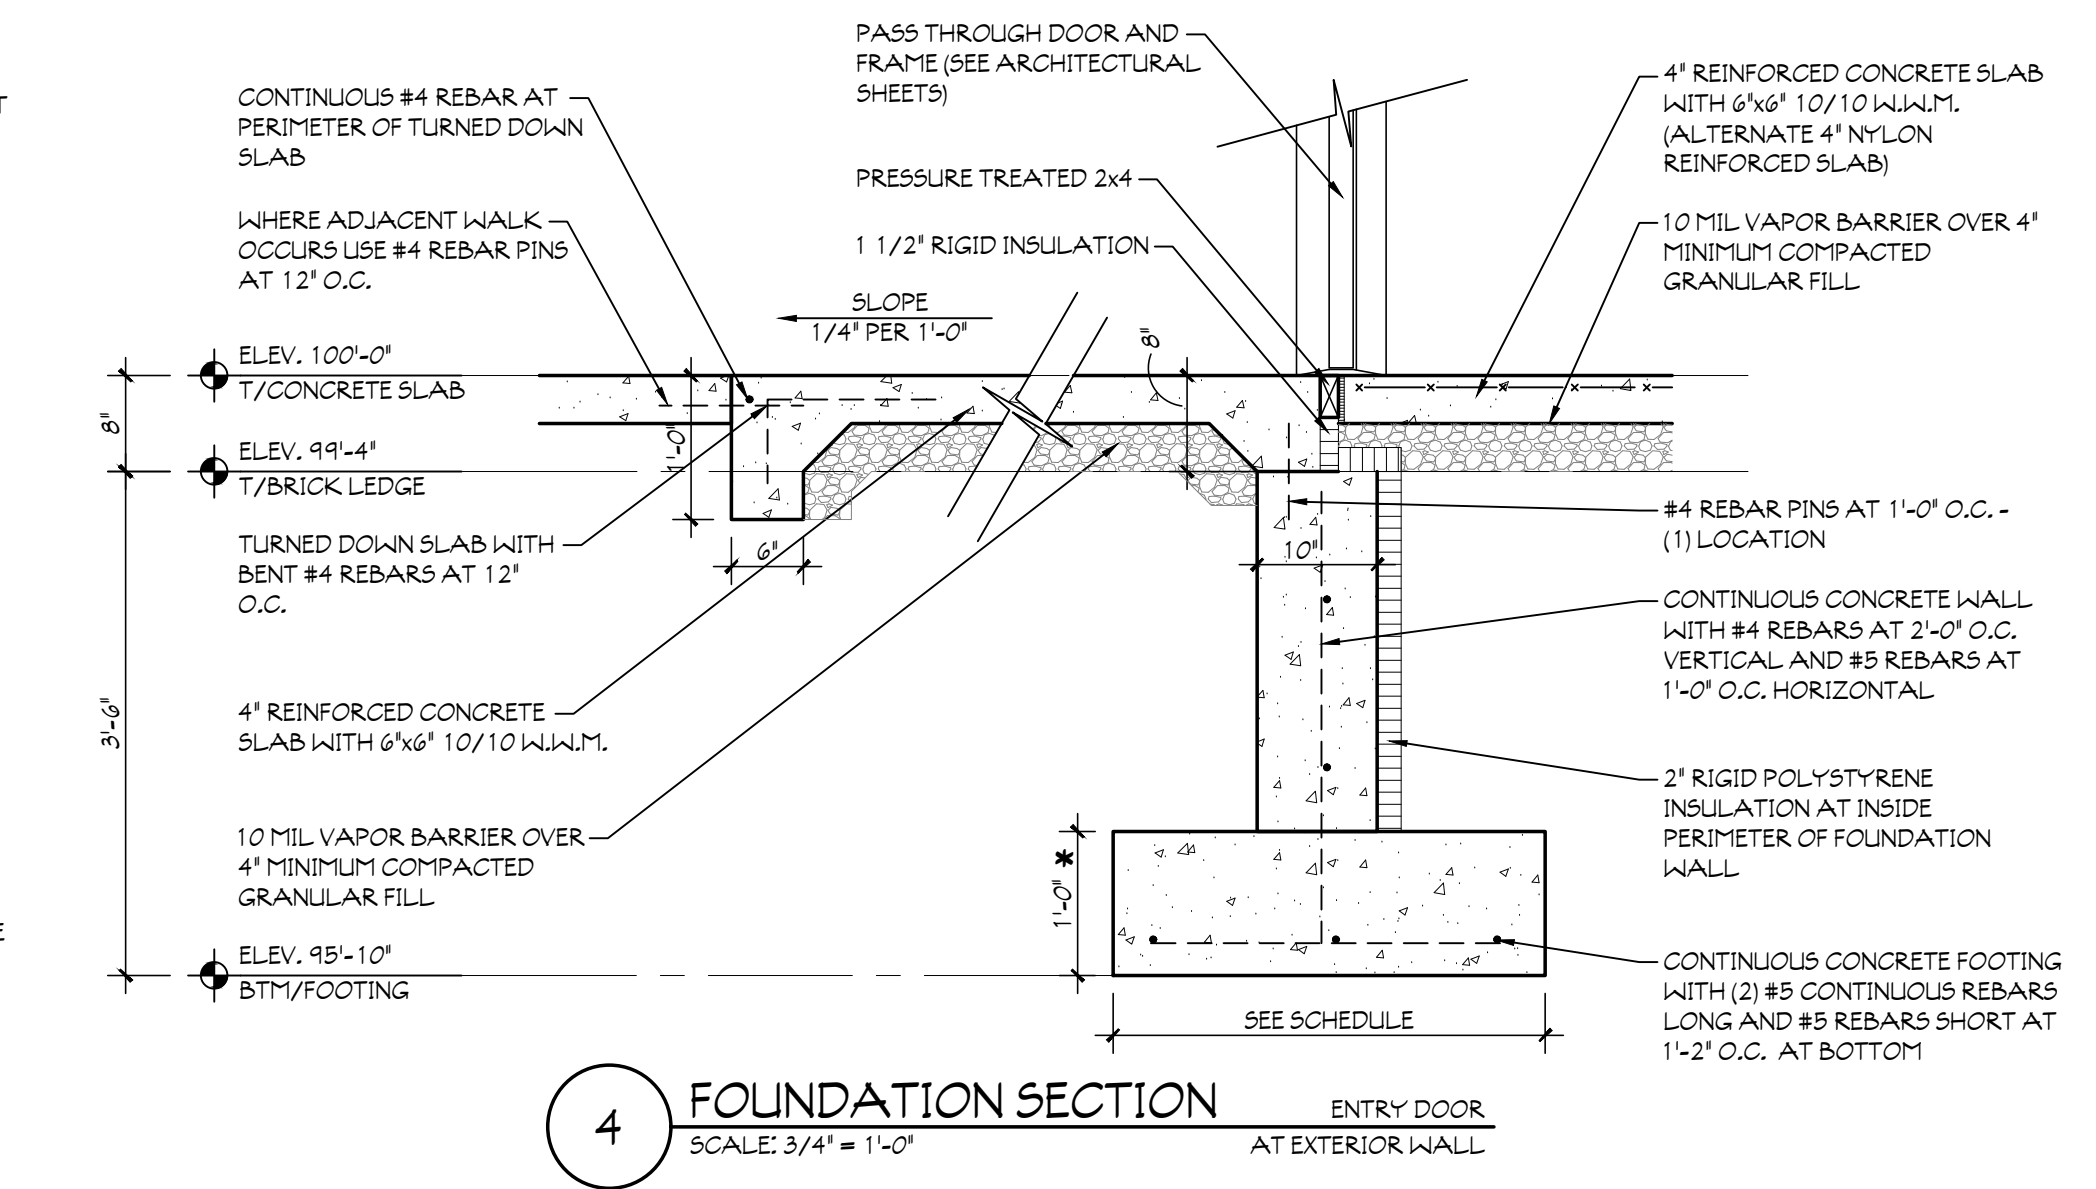


4 FOUNDATION SECTION
SCALE: 3/4" = 1'-0"

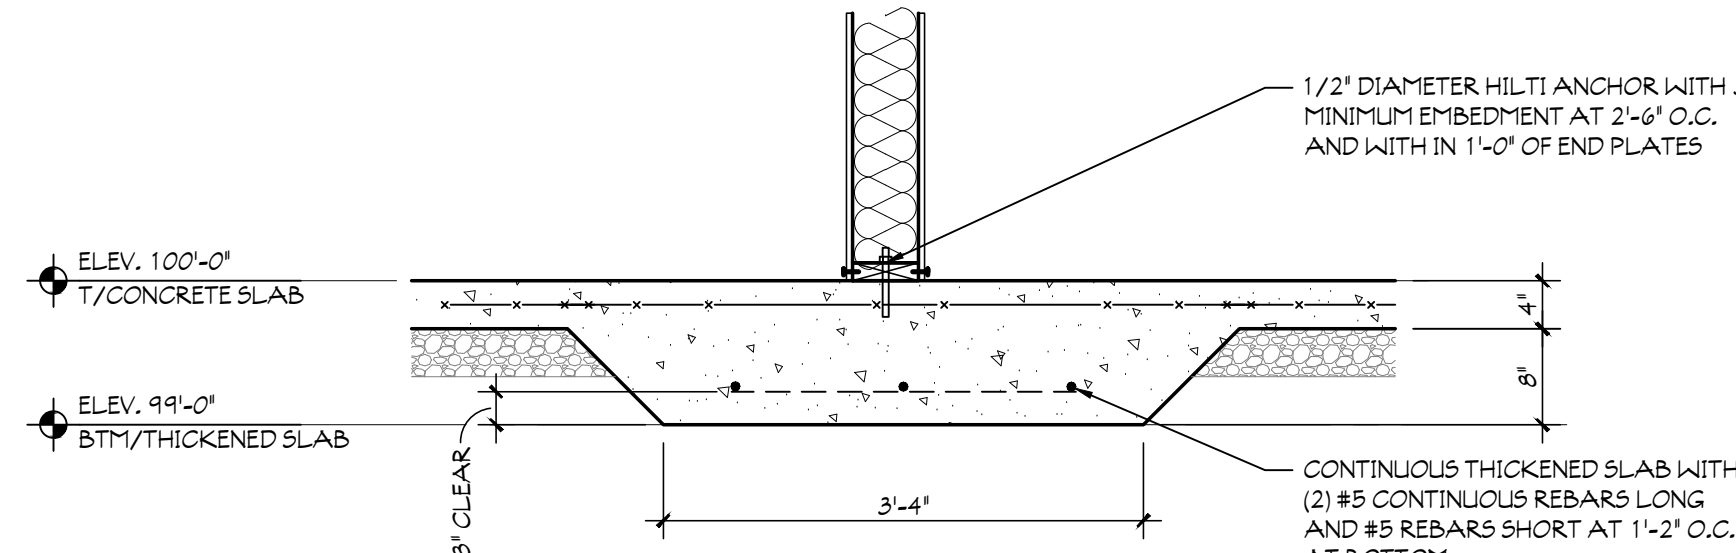


5a THICKENED SLAB
SCALE: 3/4" = 1'-0"

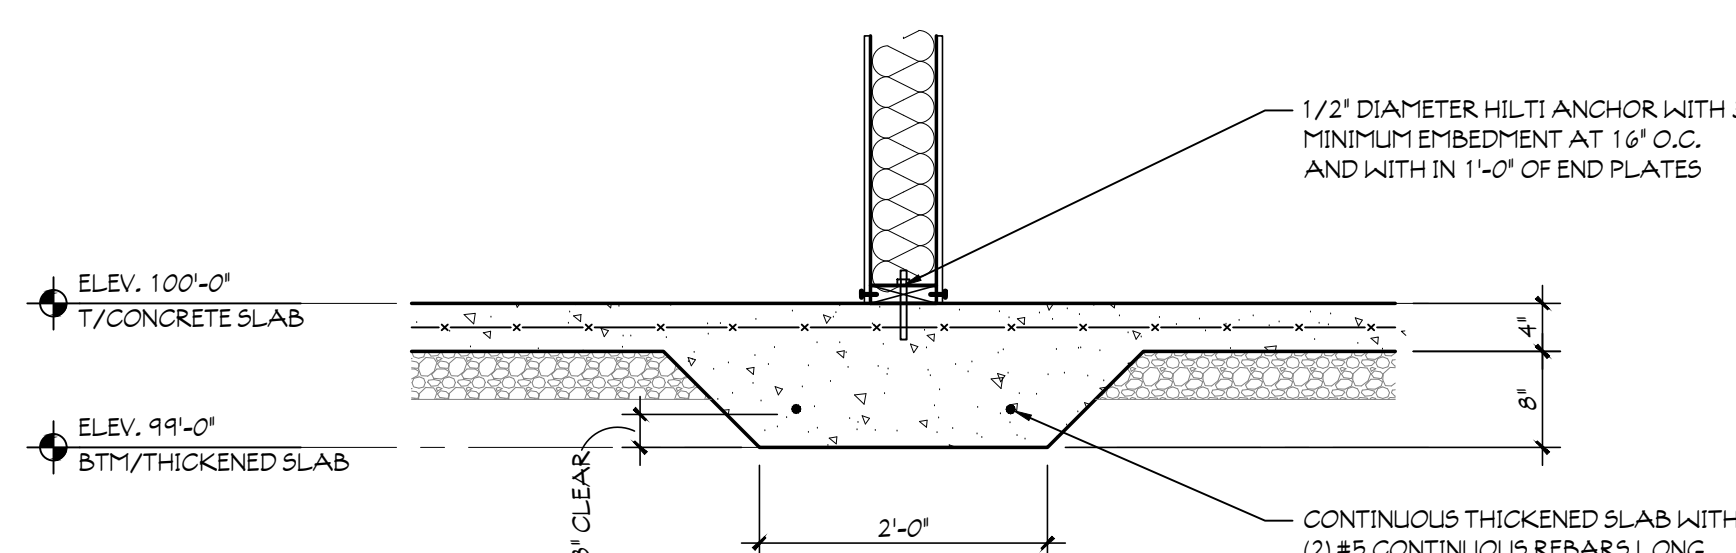

5b THICKENED SLAB
SCALE: 3/4" = 1'-0"

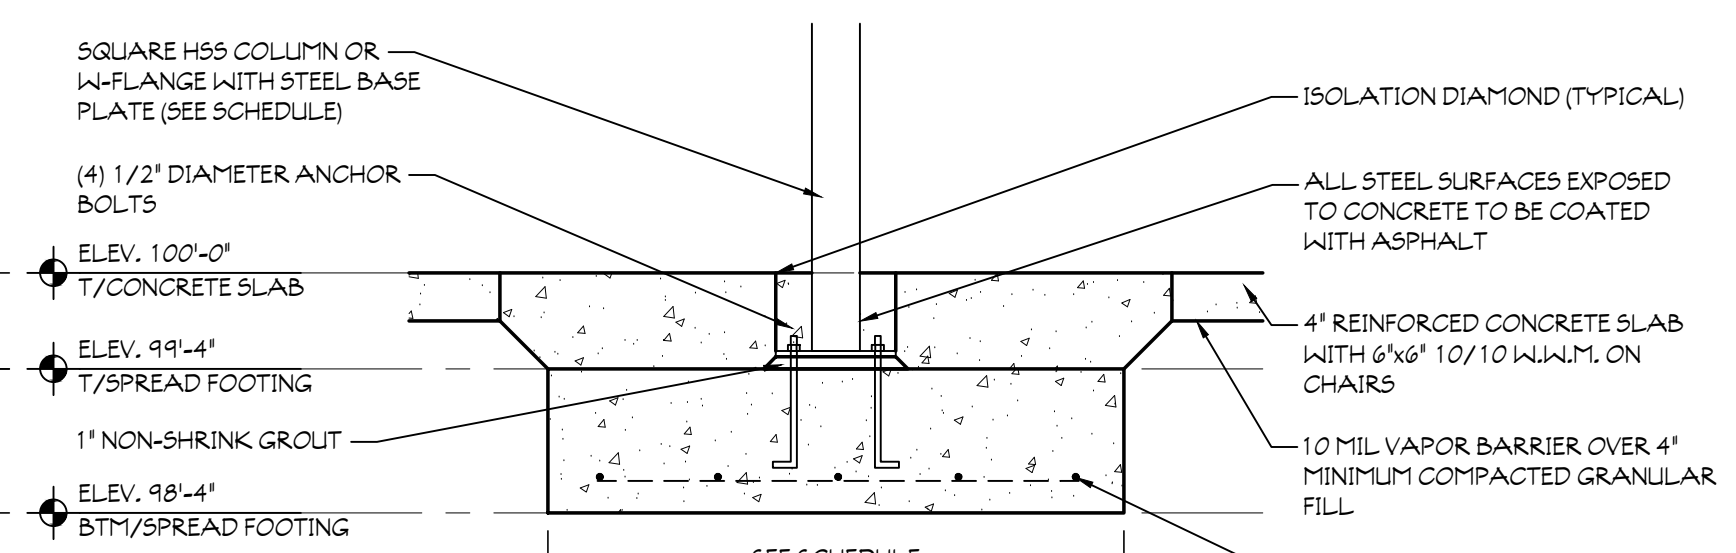

6 SPREAD FOOTING
SCALE: 3/4" = 1'-0"

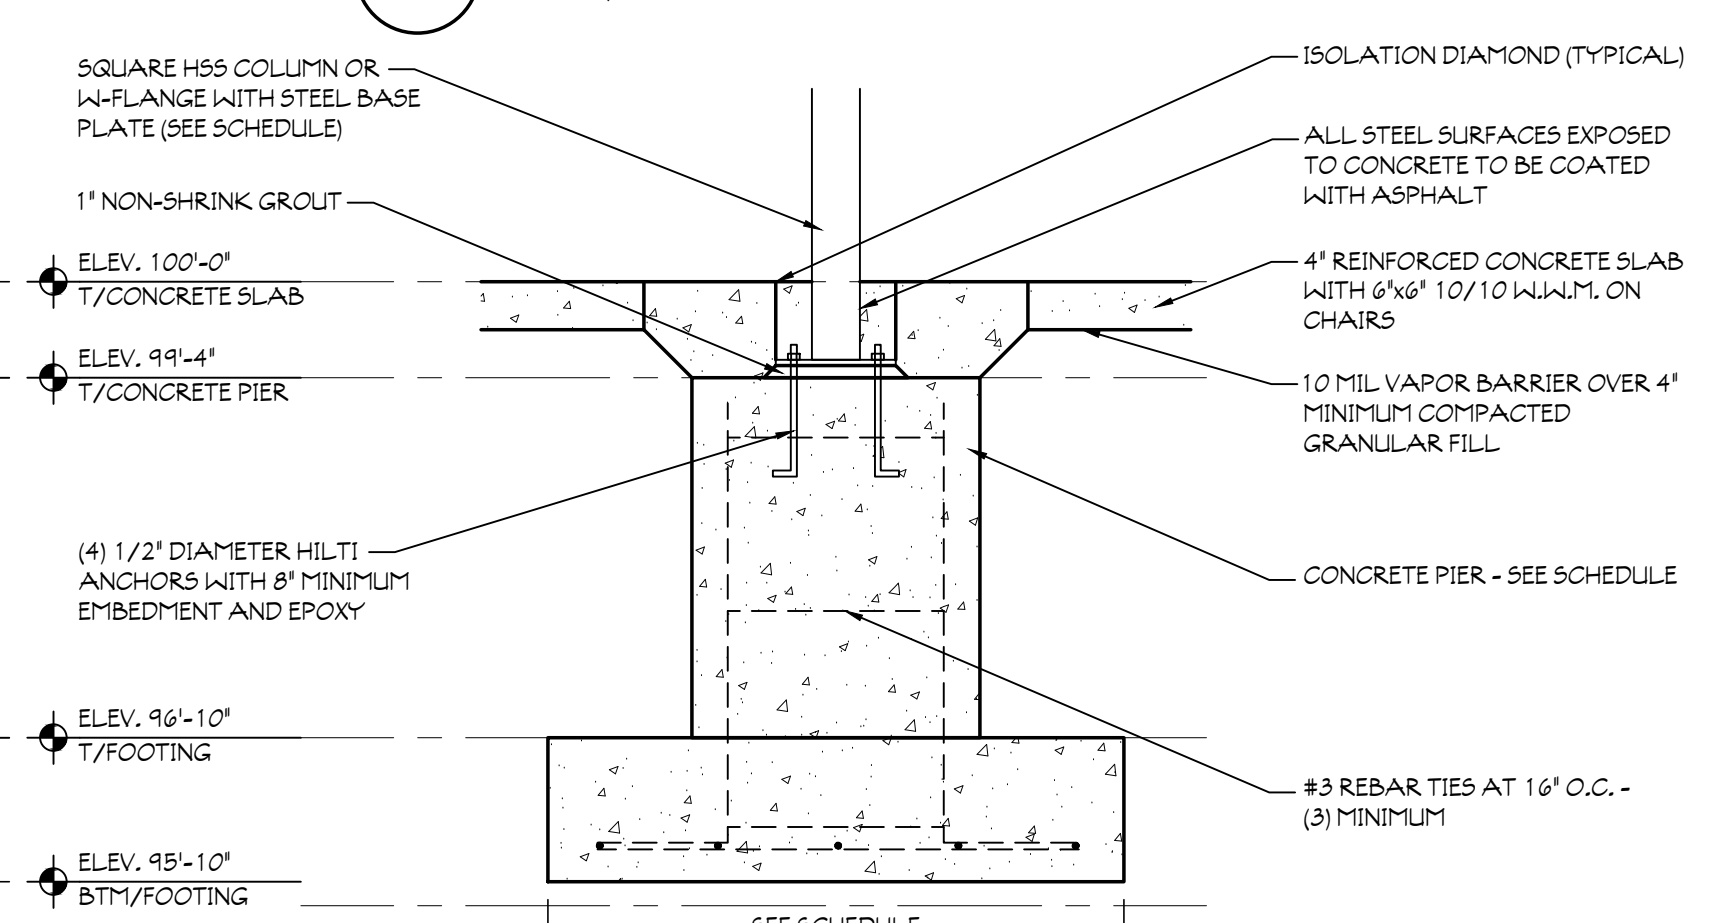

7 PIER/FOOTING SECTION
SCALE: 3/4" = 1'-0"

NOTE:
VERIFY WITH SOIL ENGINEER AND REPORT FOR EXISTING SOILS AND FOOTING DEPTHS


NOTE:
VERIFY WITH SOIL ENGINEER AND REPORT FOR EXISTING SOILS AND FOOTING DEPTHS

NOTE:
ELEVATOR INSTALLATION AND SPECIFICATION TO BE VERIFIED PER MANUFACTURER


NOTE:
VERIFY WITH SOIL ENGINEER AND REPORT FOR EXISTING SOILS AND FOOTING DEPTHS

NOTE:
SEE FOUNDATION PLAN SCHEDULE FOR VERIFICATION


8 ELEVATOR PIT DETAIL
SCALE: 3/4" = 1'-0"

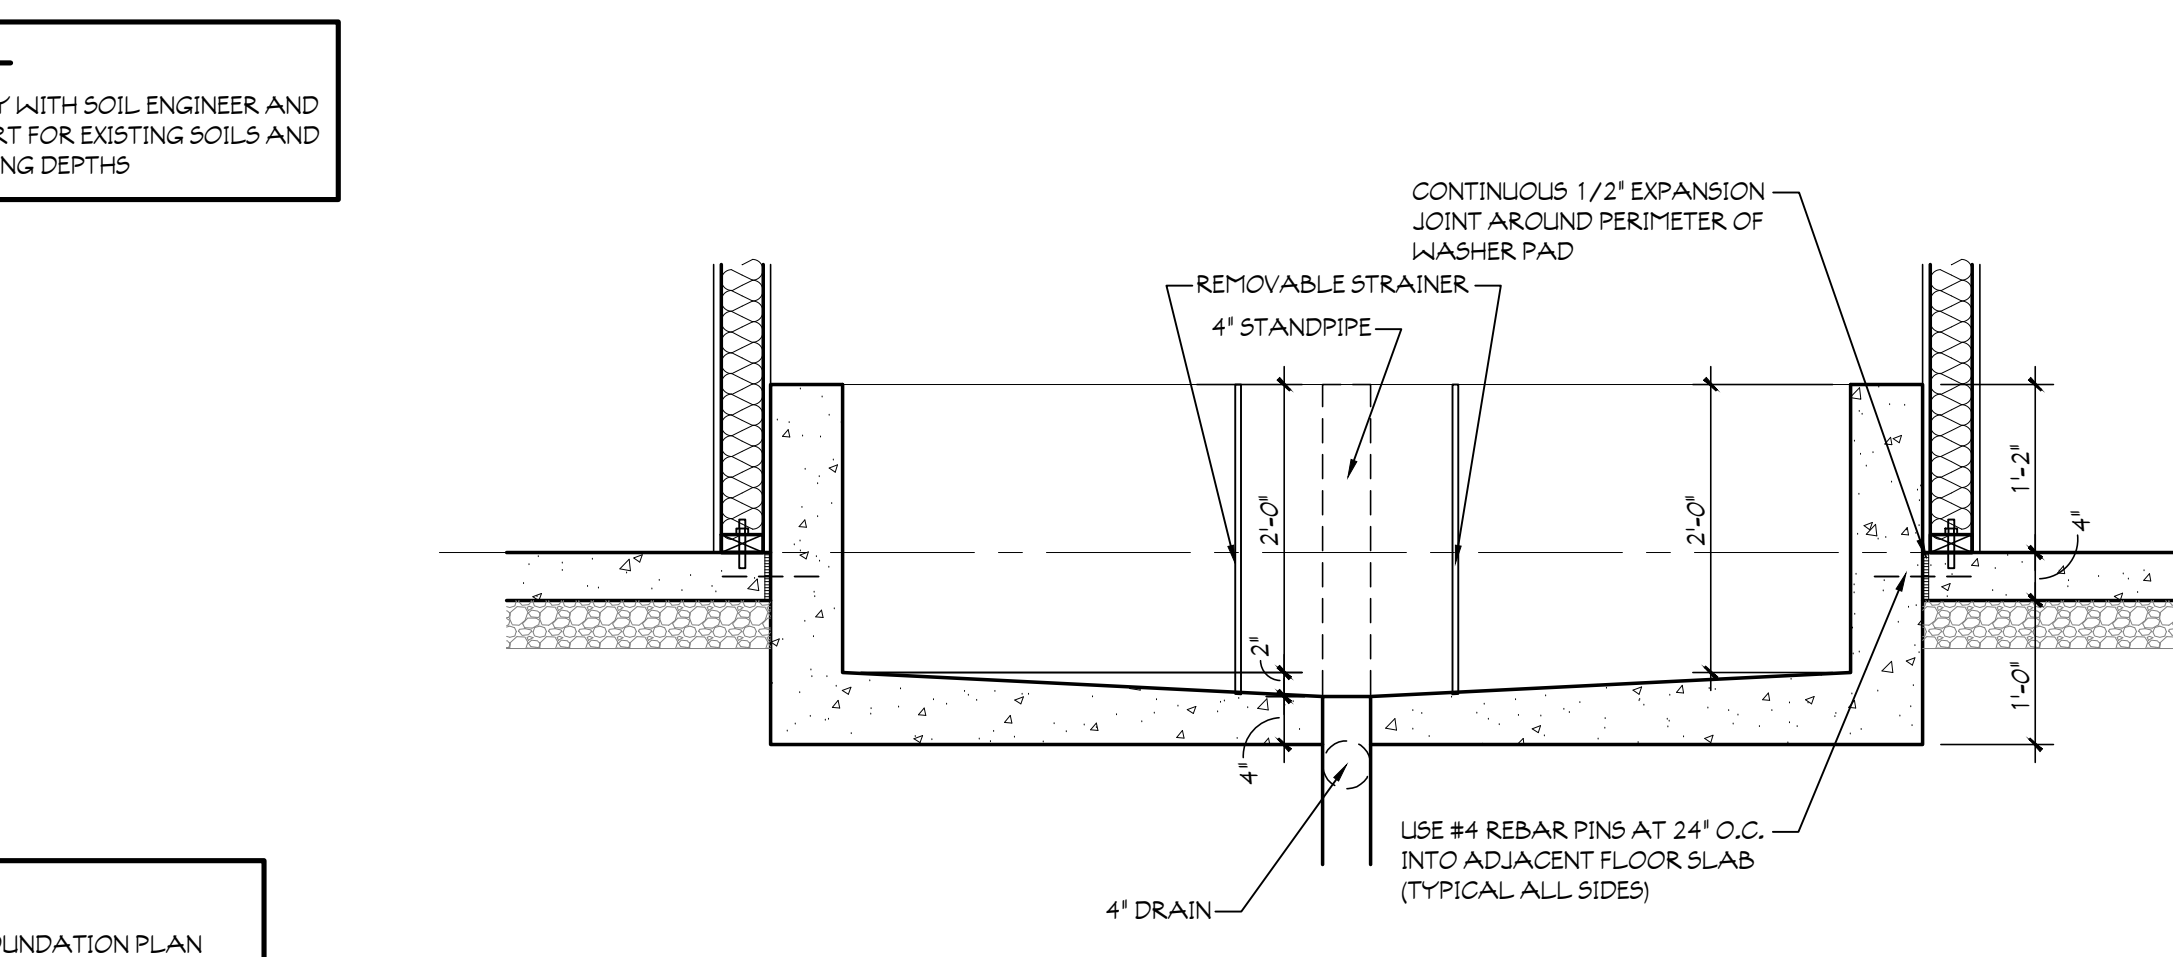


10 WASHER SECTION
SCALE: 3/4" = 1'-0"

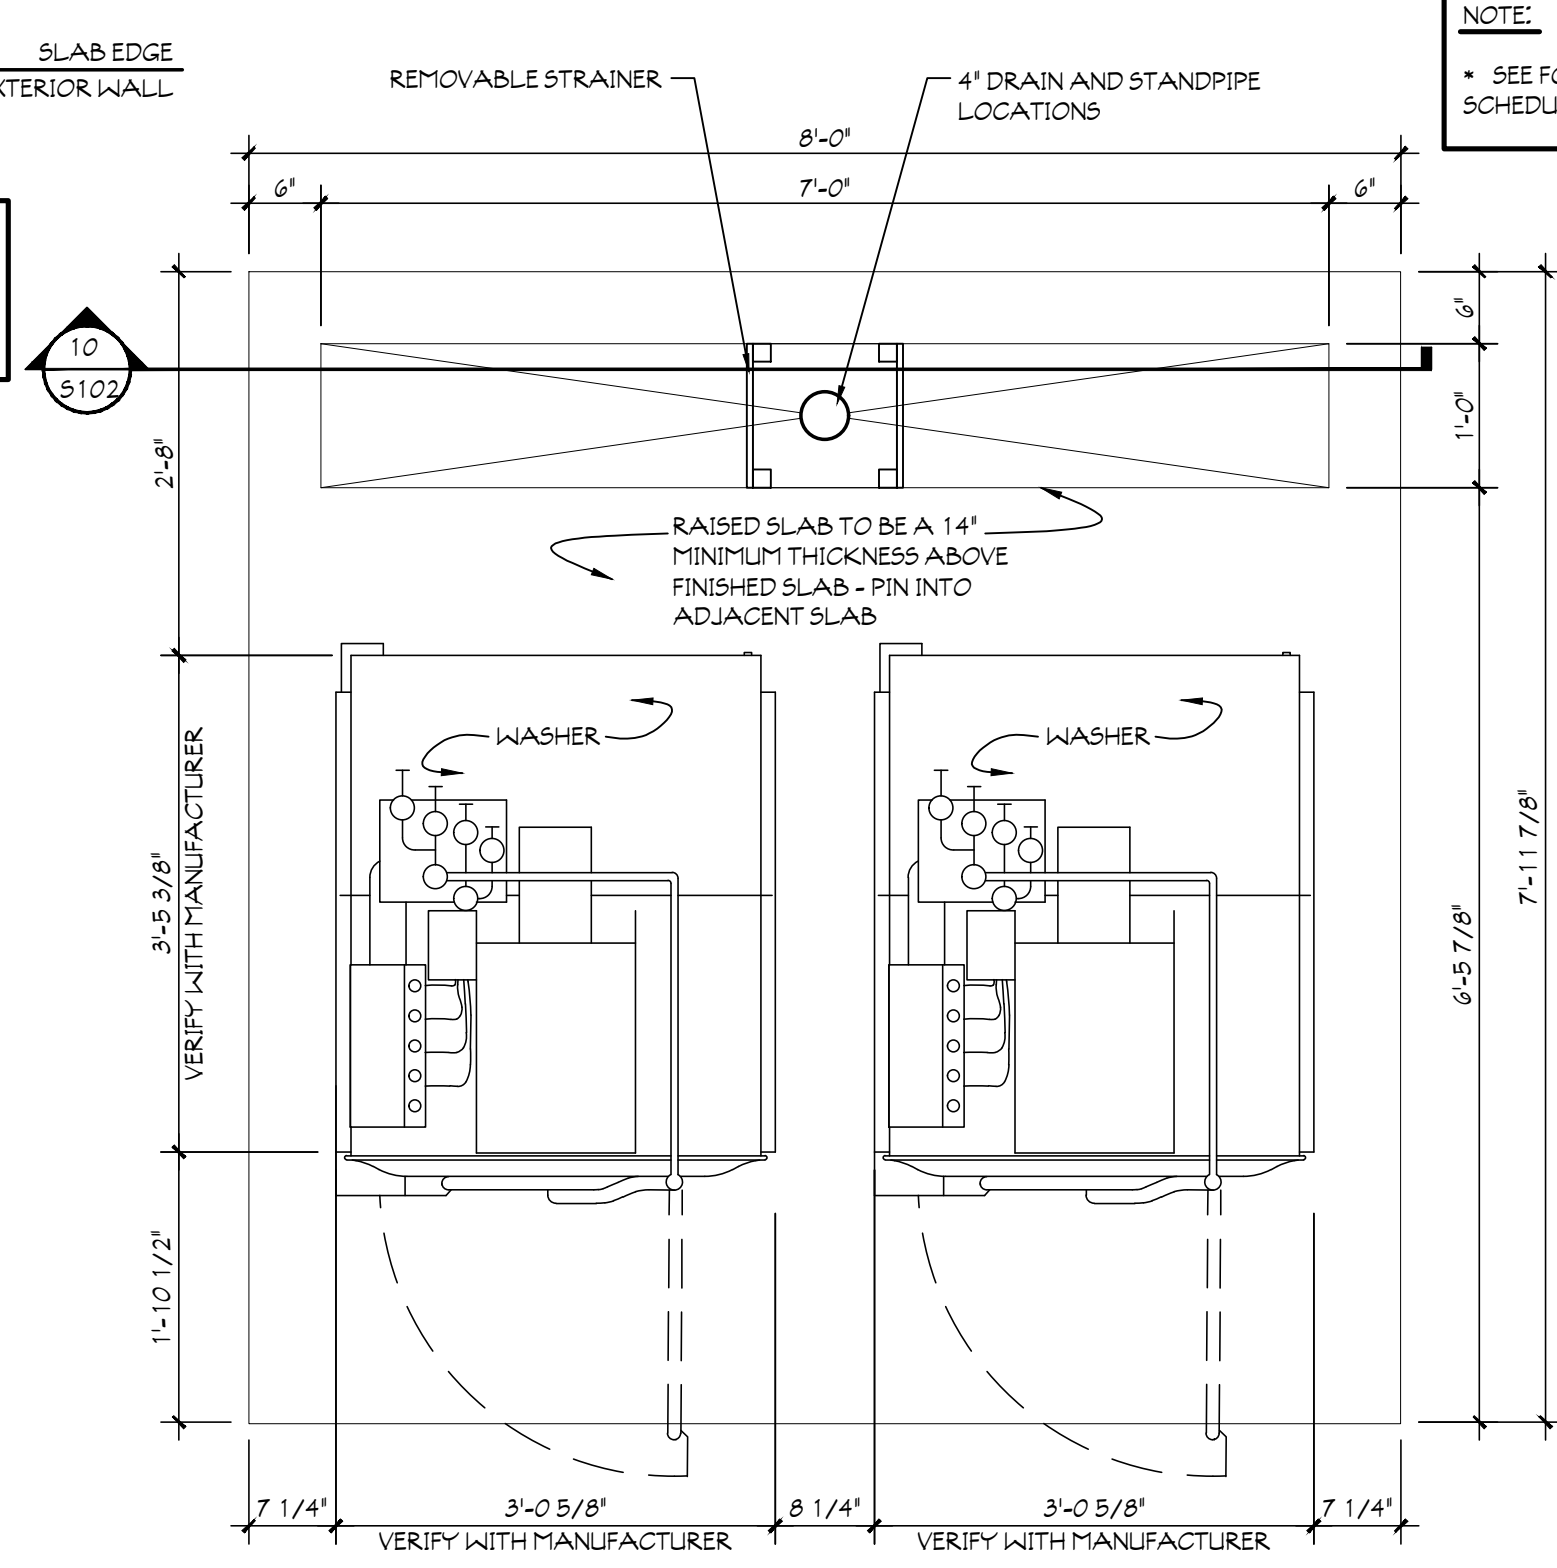


9 WASHER PAD PLAN
SCALE: 3/4" = 1'-0"

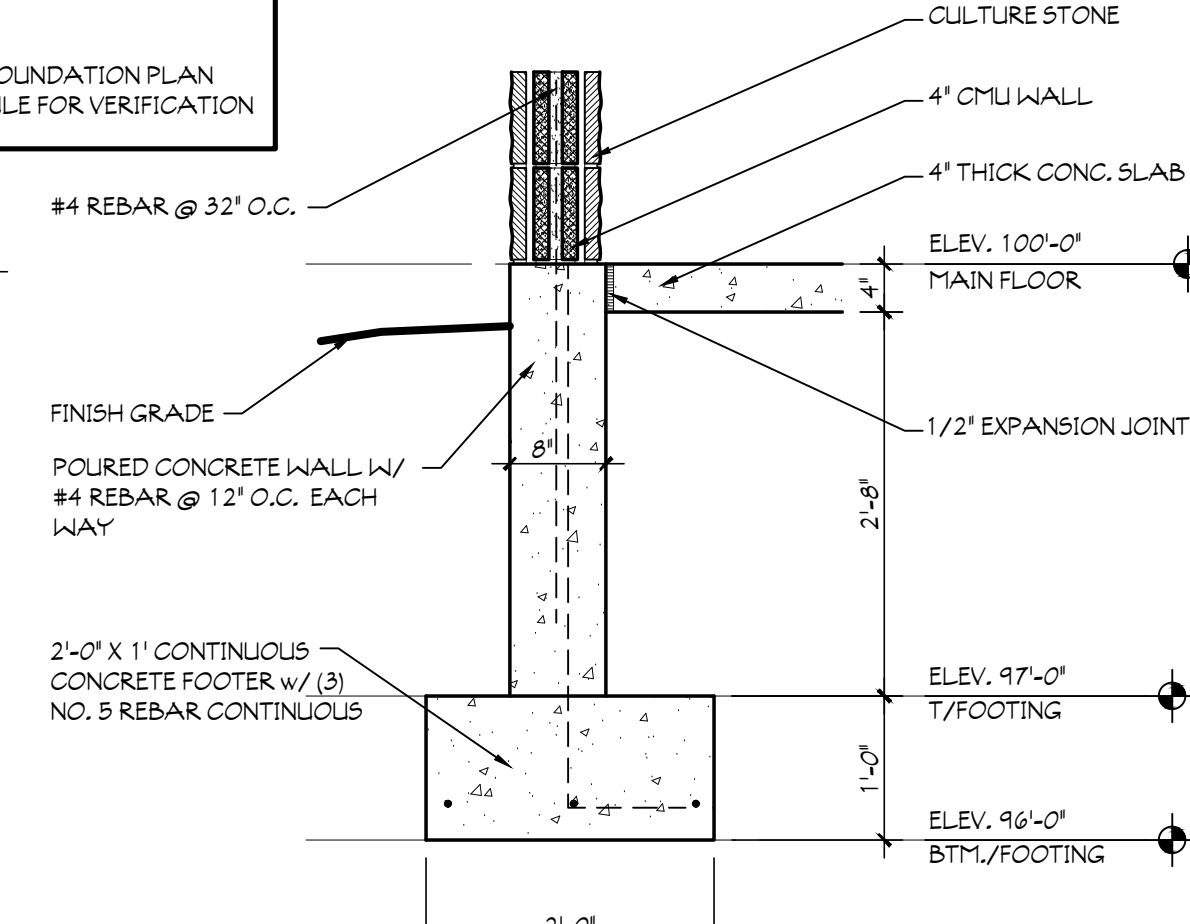

13 PATIO WALL FOOTING
SCALE: 3/4" = 1'-0"

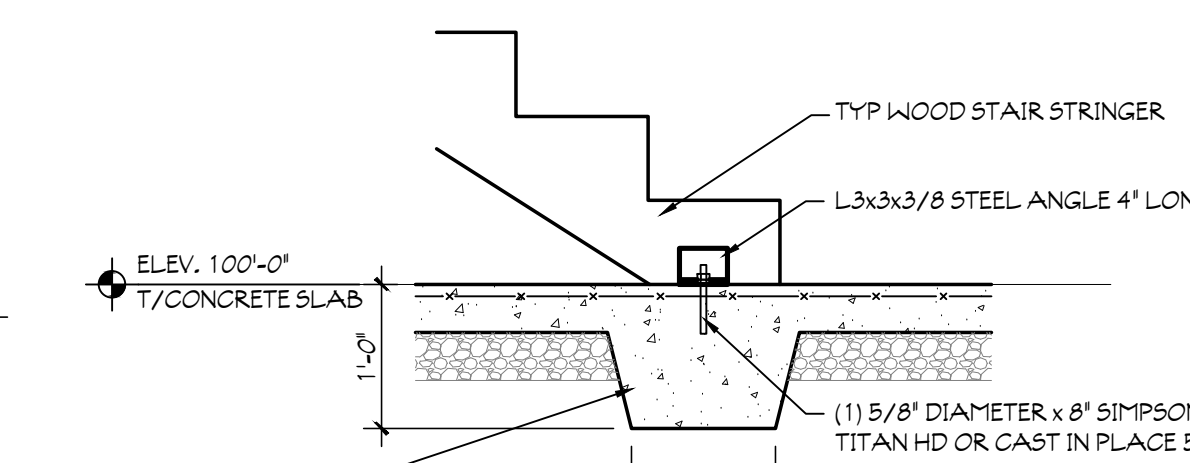

11 STAIR STRINGER
SCALE: 3/4" = 1'-0"

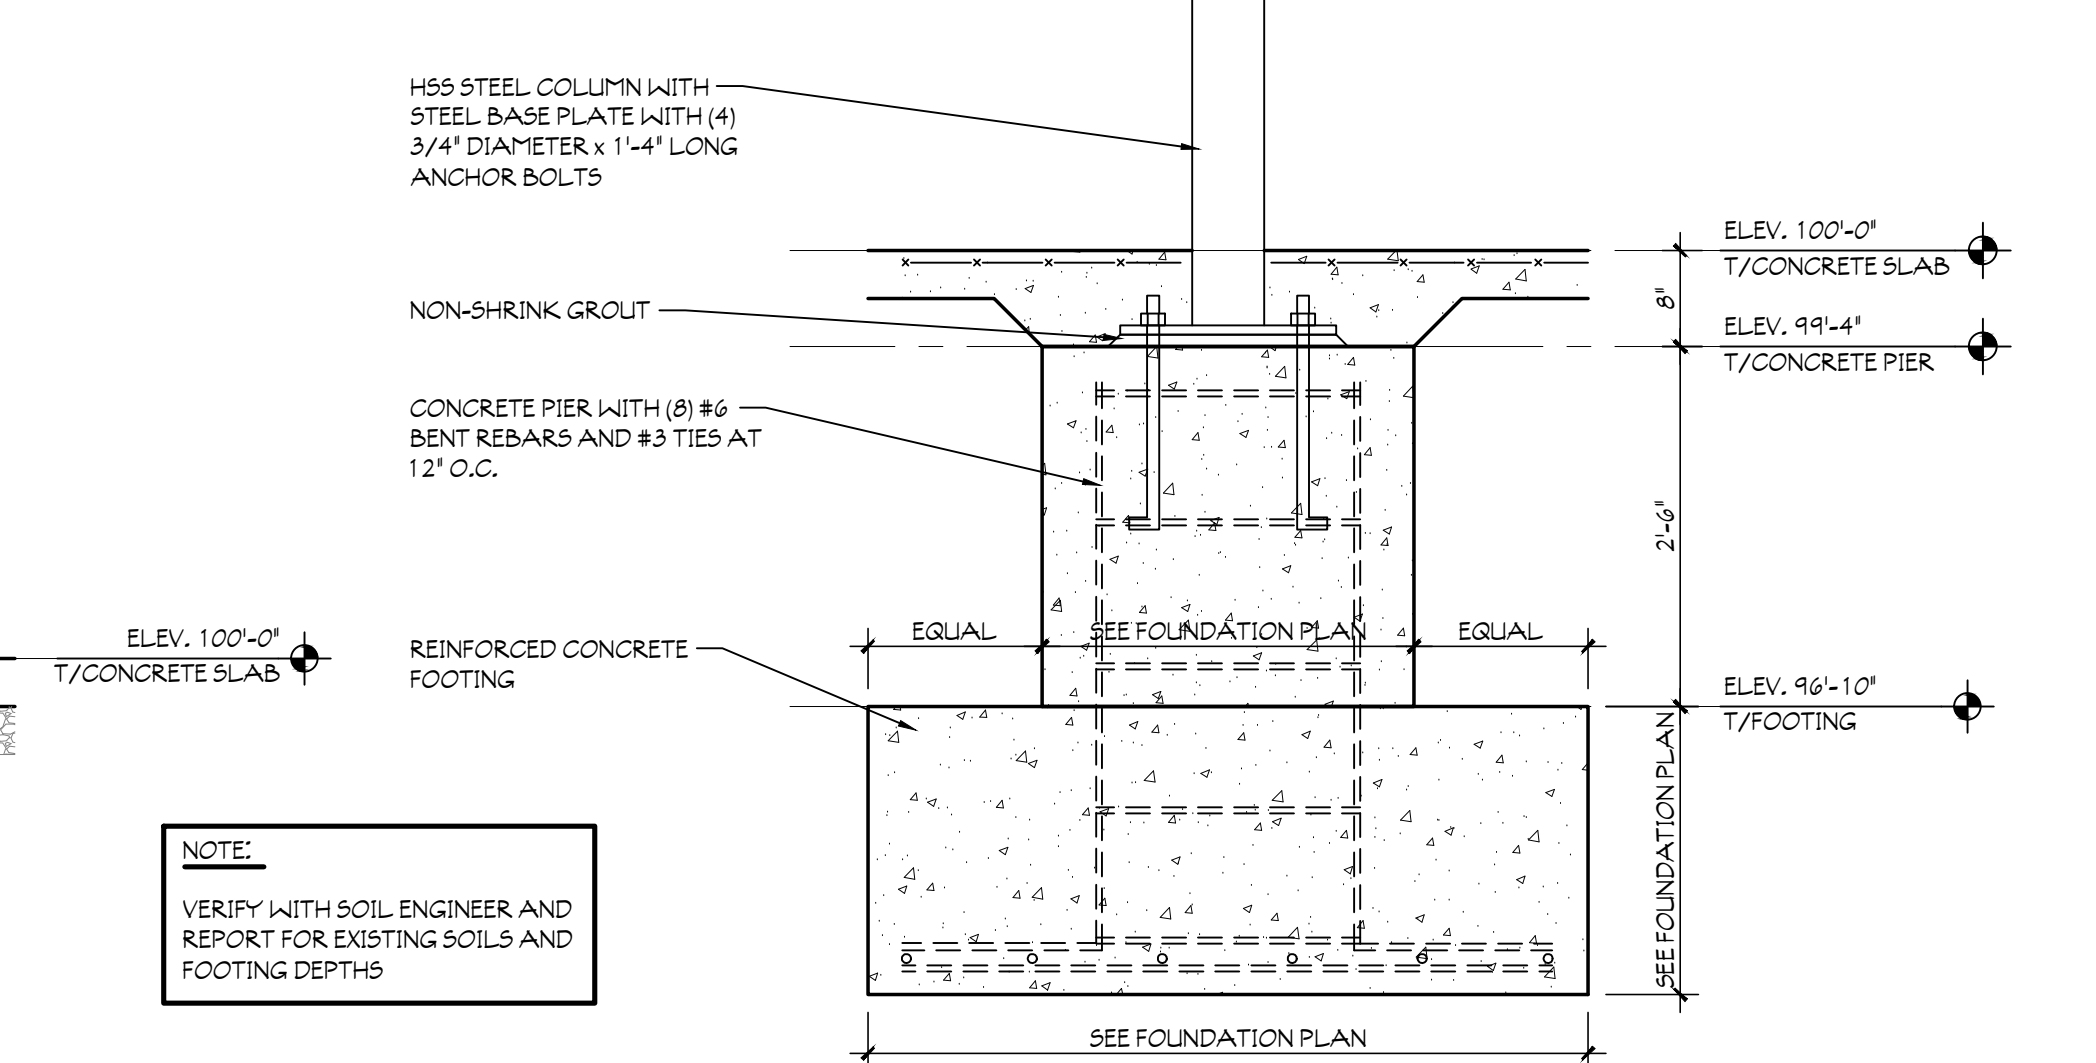

12 CANOPY COLUMN
SCALE: 3/4" = 1'-0"

NOTE:
VERIFY WITH SOIL ENGINEER AND REPORT FOR EXISTING SOILS AND FOOTING DEPTHS

GENERAL NOTES

ALTHOUGH DRAWINGS ARE PREPARED TO SCALE, THE ACCURACY OF THE DRAWINGS CANNOT BE GUARANTEED. DIMENSIONS SHOWN ON THE DRAWINGS SHALL BE USED FOR CONSTRUCTION. DIMENSIONS SHOWN ON THE DRAWINGS SHALL BE USED FOR CONSTRUCTION.

Architects
Planners
Engineers
Construction Mgmt.
MAUST ARCHITECTURAL SERVICES
DIVISION OF
L.E.M., INC.
112 NORTH MAIN STREET
GOSHEN, INDIANA 46526
PHONE: (574) 537-8500
FAX: (574) 537-0808

HOME 2
SUITES BY HILTON

SHEET SIZE 24x36

FT. WAYNE, INDIANA

REVISIONS:

DATE: 05/01/26
JOB NO.: MAS-26-105
NAME:
FOUNDATION DETAILS
SHEET:

PRELIMINARY - NOT FOR CONSTRUCTION

5102