


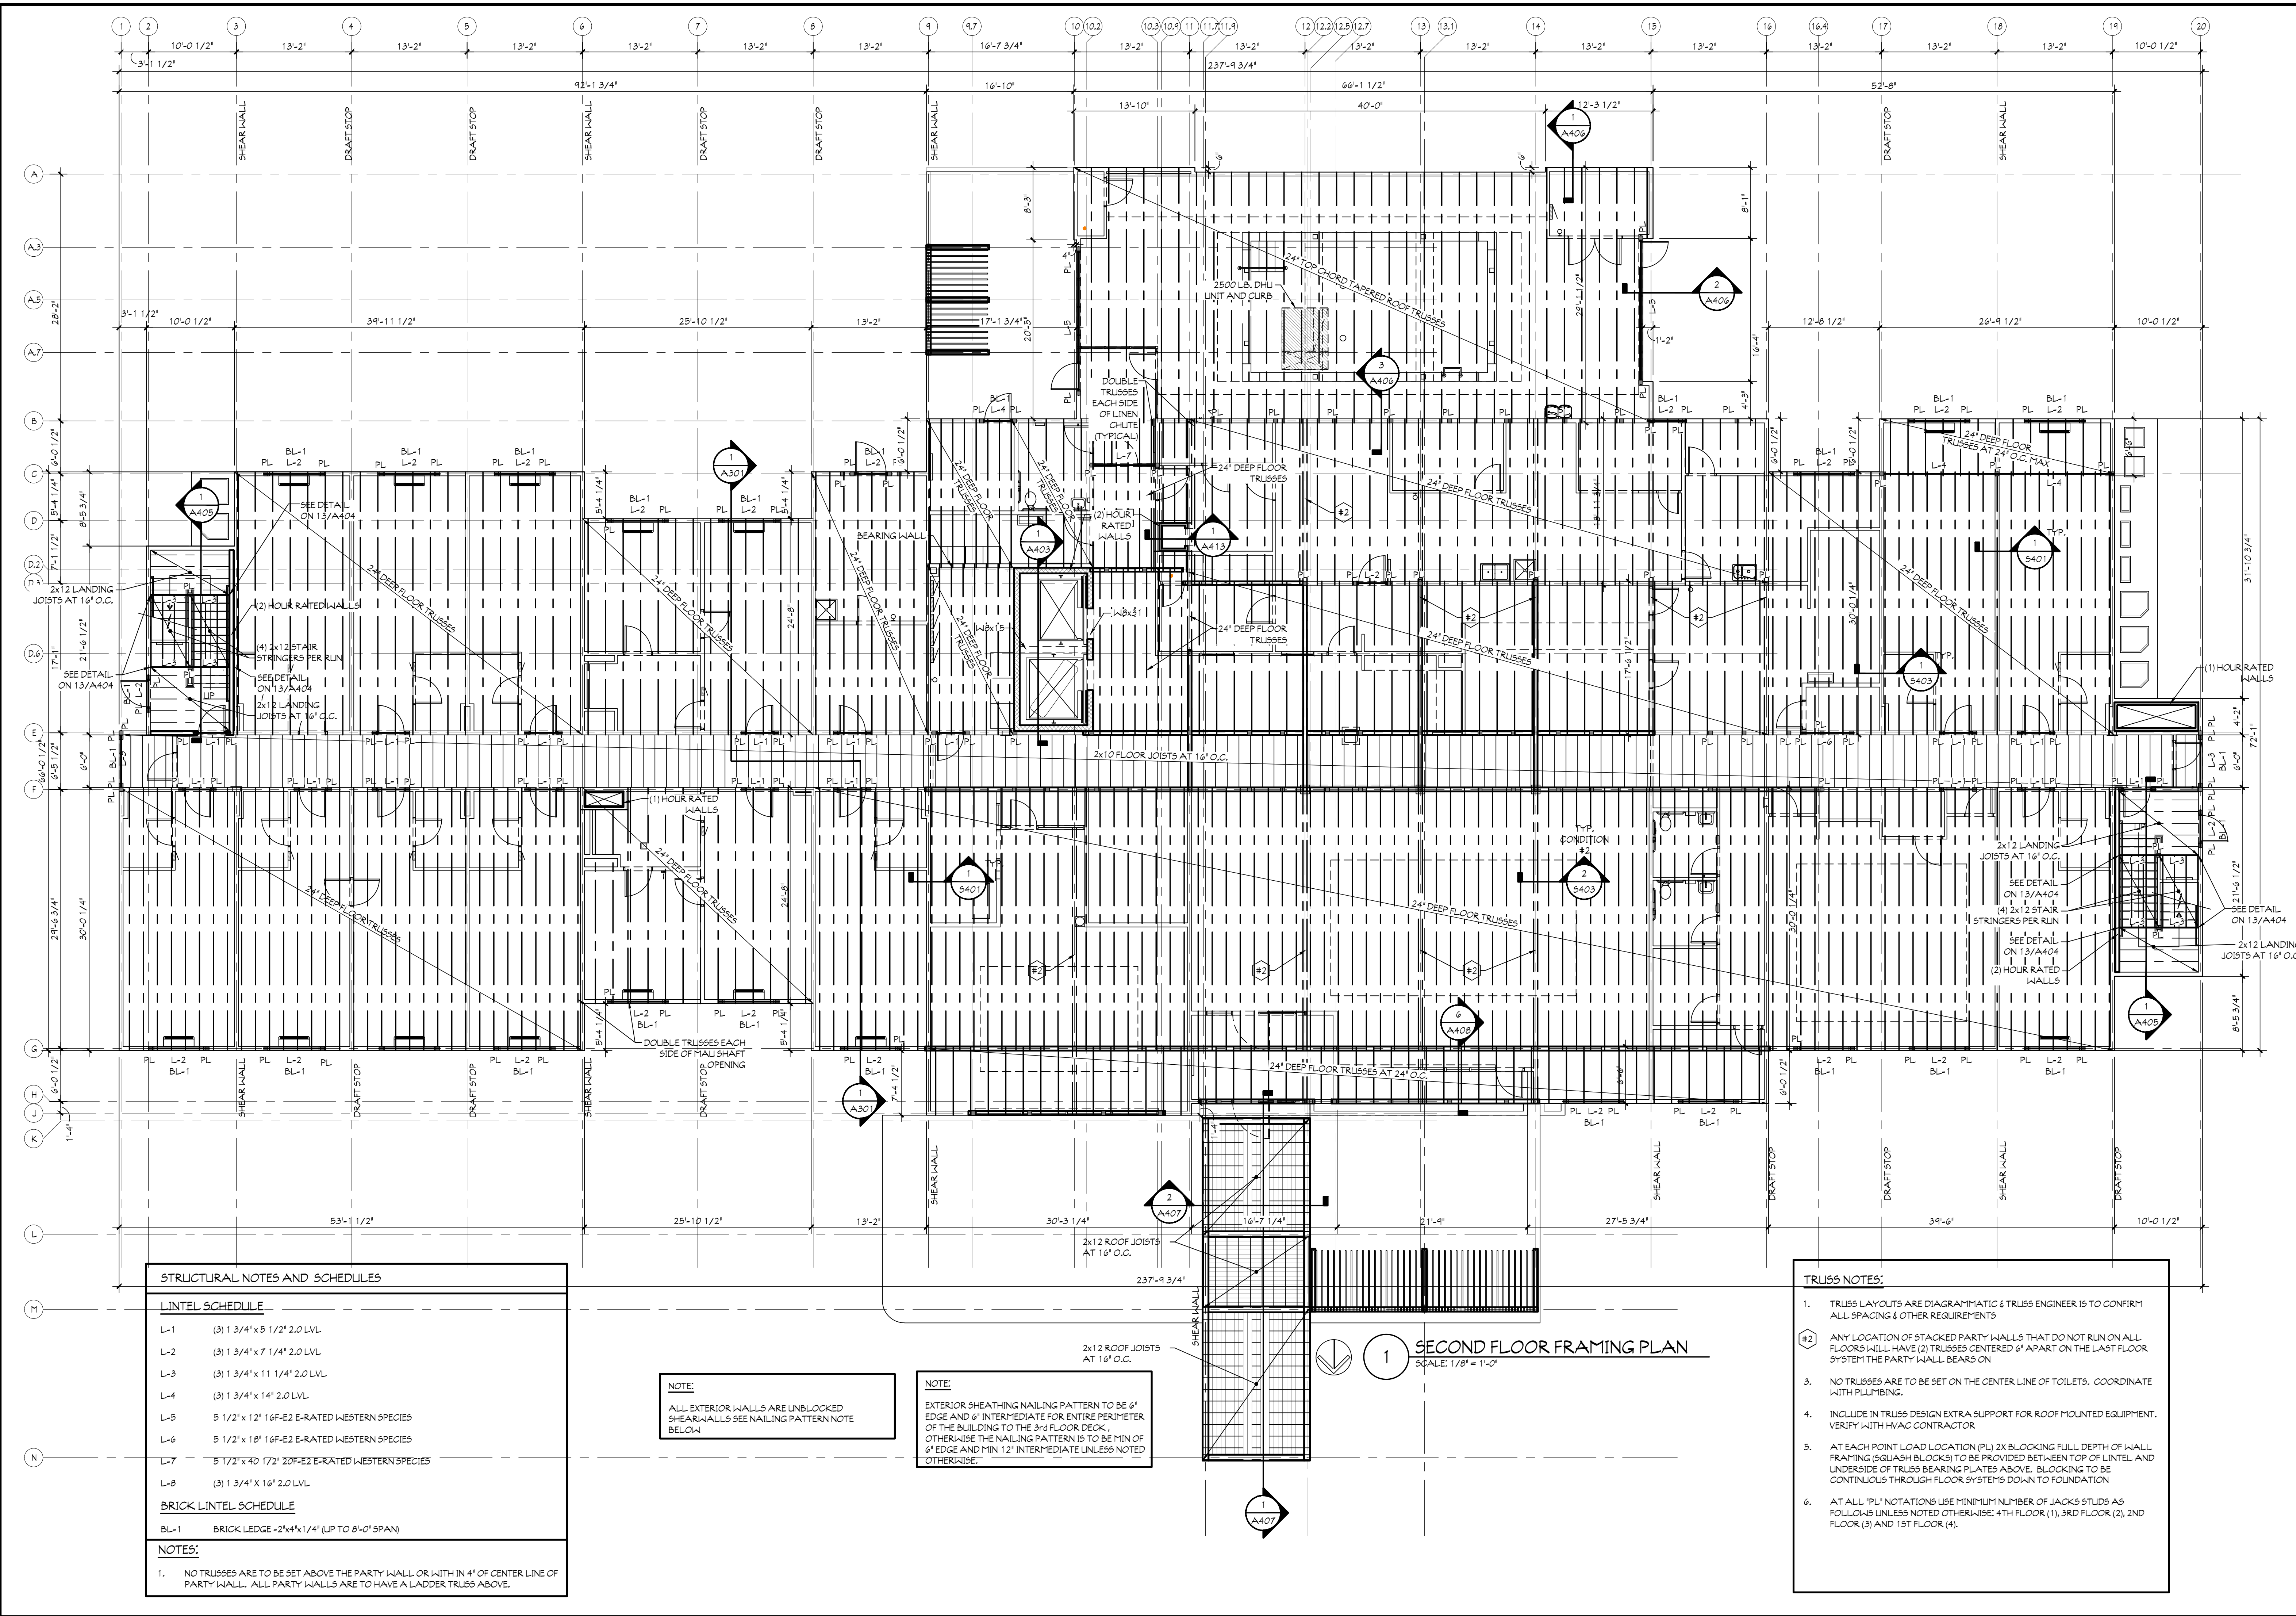


GENERAL NOTES

ALL DIMENSIONS UNLESS OTHERWISE NOTED ARE IN FEET AND INCHES. DIMENSIONS SHOULD BE ROUNDED UP TO THE NEXT WHOLE INCH.

ALL DIMENSIONS UNLESS OTHERWISE NOTED ARE IN FEET AND INCHES. DIMENSIONS SHOULD BE ROUNDED UP TO THE NEXT WHOLE INCH.

MAUIST ARCHITECTURAL SERVICES
DIVISION OF L.E.M., INC.
112 NORTH MAIN STREET
GOSHEN, INDIANA 46526
PHONE: (574) 537-8500
FAX: (574) 537-0808

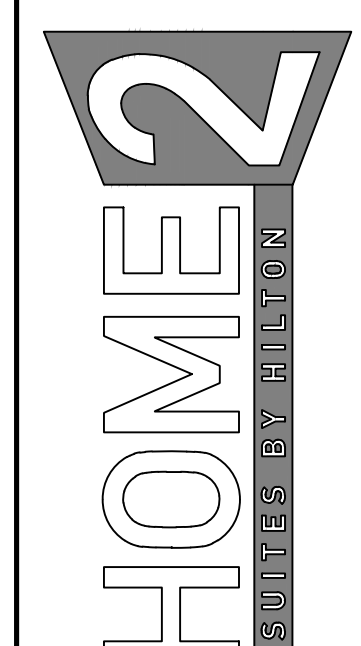

SHEET SIZE 24x36

FT. WAYNE, INDIANA

REVISIONS:

DATE: 05/01/26
JOB NO.: MAS-26-105
NAME: SECOND FLOOR FRAMING PLAN
SHEET:

5202