


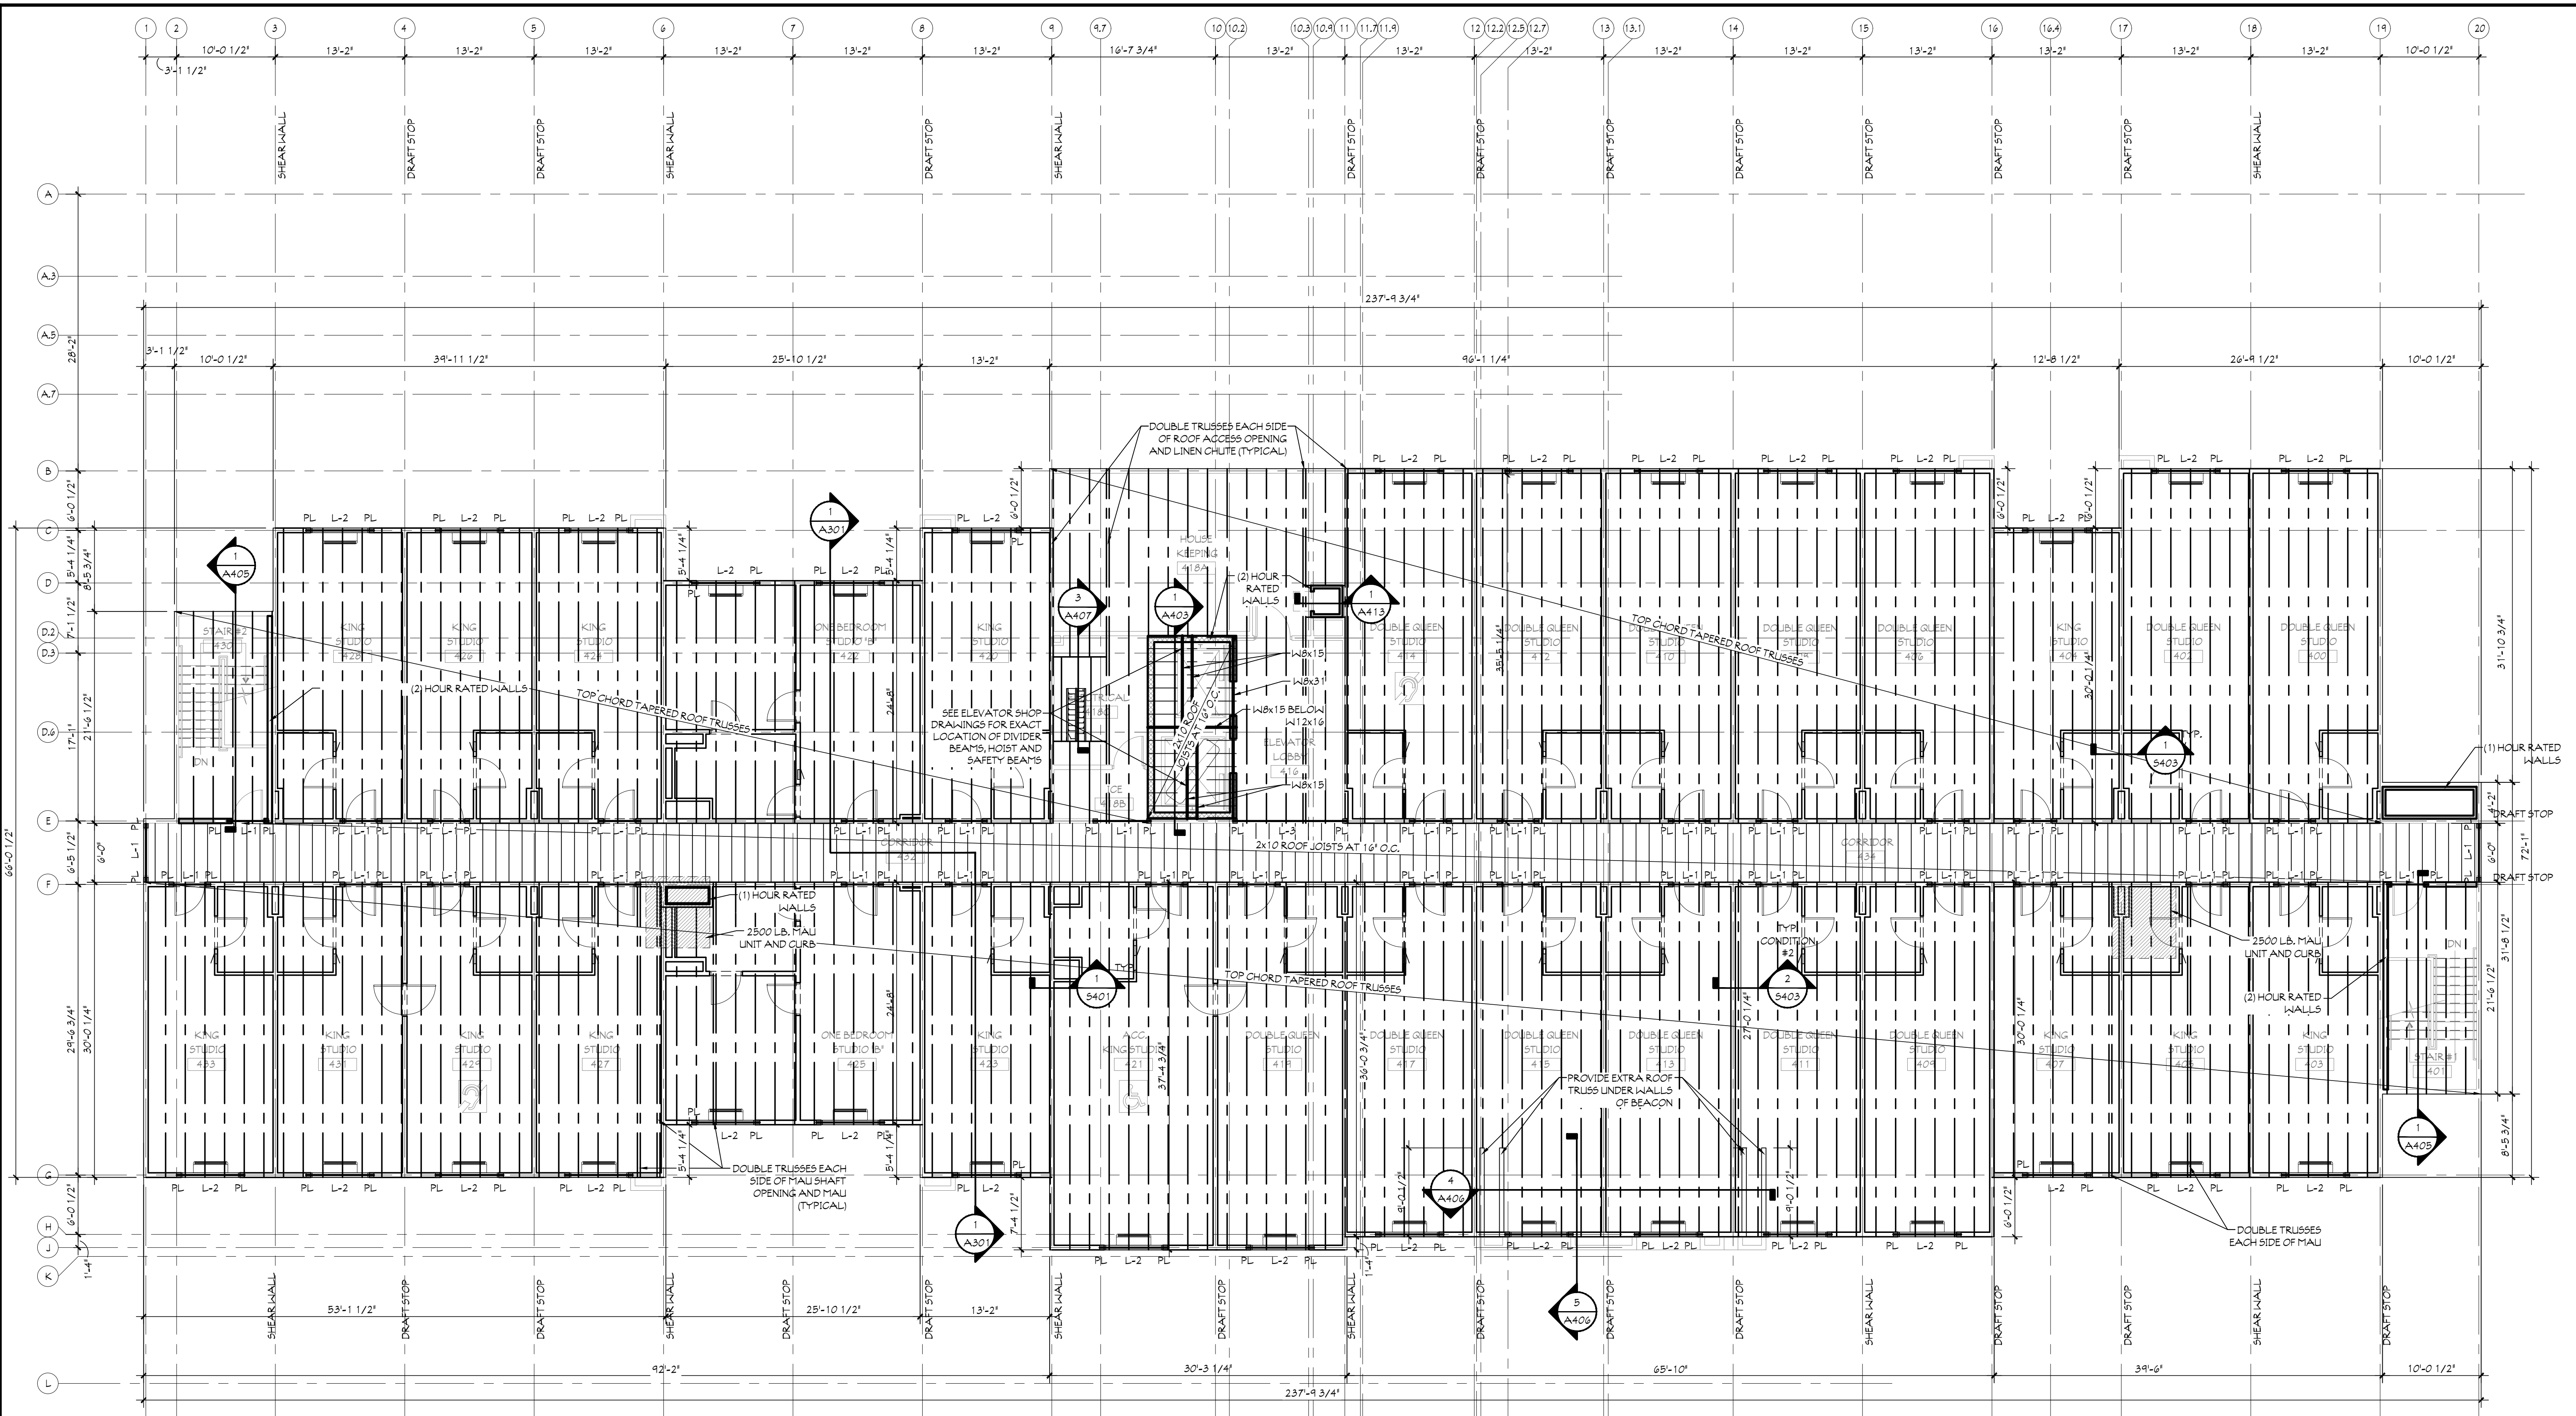

STRUCTURAL NOTES AND SCHEDULES	
LINTEL SCHEDULE	
L-1	(3) 1 3/4" x 5 1/2' 2.0 LVL
L-2	(3) 1 3/4" x 7 1/4' 2.0 LVL
L-3	(3) 1 3/4" x 11 1/4' 2.0 LVL
L-4	(3) 1 3/4" x 14' 2.0 LVL
L-5	5 1/2" x 12' 16F-E2 E-RATED WESTERN SPECIES
L-6	5 1/2" x 18' 16F-E2 E-RATED WESTERN SPECIES
L-7	5 1/2" x 40 1/2' 20F-E2 E-RATED WESTERN SPECIES
L-8	(3) 1 3/4" x 16' 2.0 LVL
BRICK LINTEL SCHEDULE	
BL-1	BRICK LEDGE - 2"x4"x1/4" (UP TO 8'-0" SPAN)
NOTES:	
1. NO TRUSSES ARE TO BE SET ABOVE THE PARTY WALL OR WITH IN 4' OF CENTER LINE OF PARTY WALL. ALL PARTY WALLS ARE TO HAVE A LADDER TRUSS ABOVE.	

- TRUSS NOTES:**
- TRUSS LAYOUTS ARE DIAGRAMMATIC & TRUSS ENGINEER IS TO CONFIRM ALL SPACING & OTHER REQUIREMENTS
 - ANY LOCATION OF STACKED PARTY WALLS THAT DO NOT RUN ON ALL FLOORS WILL HAVE (2) TRUSSES CENTERED 6' APART ON THE LAST FLOOR SYSTEM THE PARTY WALL BEARS ON
 - NO TRUSSES ARE TO BE SET ON THE CENTER LINE OF TOILETS. COORDINATE WITH PLUMBING.
 - INCLUDE IN TRUSS DESIGN EXTRA SUPPORT FOR ROOF MOUNTED EQUIPMENT. VERIFY WITH HVAC CONTRACTOR.
 - AT EACH POINT LOAD LOCATION (PL) 2X BLOCKING FULL DEPTH OF WALL FRAMING (SQUASH BLOCKS) TO BE PROVIDED BETWEEN TOP OF LINTEL AND UNDERSIDE OF TRUSS BEARING PLATES ABOVE. BLOCKING TO BE CONTINUOUS THROUGH FLOOR SYSTEMS DOWN TO FOUNDATION
 - AT ALL "PL" NOTATIONS USE MINIMUM NUMBER OF JACKS STUDS AS FOLLOWS UNLESS NOTED OTHERWISE: 4TH FLOOR (1), 3RD FLOOR (2), 2ND FLOOR (3) AND 1ST FLOOR (4).

1 ROOF FRAMING PLAN
SCALE: 1/8" = 1'-0"

NOTE:
ALL EXTERIOR WALLS ARE UNBLOCKED SHEAR WALLS
SEE NAILING PATTERN NOTE BELOW

NOTE:
EXTERIOR SHEATHING NAILING PATTERN TO BE 6" EDGE AND 6" INTERMEDIATE FOR ENTIRE PERIMETER OF THE BUILDING TO THE 3RD FLOOR DECK, OTHERWISE THE NAILING PATTERN IS TO BE MIN OF 6" EDGE AND MIN 12" INTERMEDIATE UNLESS NOTED OTHERWISE.

GENERAL NOTES

ALTHOUGH DRAWINGS ARE PREPARED TO SCALE, THE ACCURACY OF THE DRAWINGS CANNOT BE GUARANTEED. THE USER SHALL BE RESPONSIBLE FOR VERIFYING ALL DIMENSIONS AND CONDITIONS PRIOR TO CONSTRUCTION. DIMENSIONS SHOWN ON THE DRAWINGS SHALL BE USED FOR CONSTRUCTION.

ALL DIMENSIONS UNLESS OTHERWISE NOTED SHALL BE IN FEET AND INCHES. DIMENSIONS SHALL BE ROUNDED UP TO THE NEXT WHOLE INCH. DIMENSIONS SHALL BE ROUNDED DOWN TO THE NEXT WHOLE INCH. DIMENSIONS SHALL BE ROUNDED TO THE NEAREST 1/8".

ALL DIMENSIONS UNLESS OTHERWISE NOTED SHALL BE IN FEET AND INCHES. DIMENSIONS SHALL BE ROUNDED UP TO THE NEXT WHOLE INCH. DIMENSIONS SHALL BE ROUNDED DOWN TO THE NEXT WHOLE INCH. DIMENSIONS SHALL BE ROUNDED TO THE NEAREST 1/8".

* Architects
Planners
Engineers
Construction Mgmt.
* Rule 5 and MS4 Filing
L.E.M., INC.
PHONE: (574) 537-8500
FAX: (574) 537-0808
112 NORTH MAIN STREET
GOSHEN, INDIANA 46526

MAUIST ARCHITECTURAL SERVICES
DIVISION OF L.E.M., INC.

HOME 2
SUITES BY HILTON

SHEET SIZE 24x36

FT. WAYNE, INDIANA

REVISIONS:

DATE: 05/01/26
JOB NO.: MAS-26-105
NAME: ROOF FRAMING PLAN
SHEET: 5301