



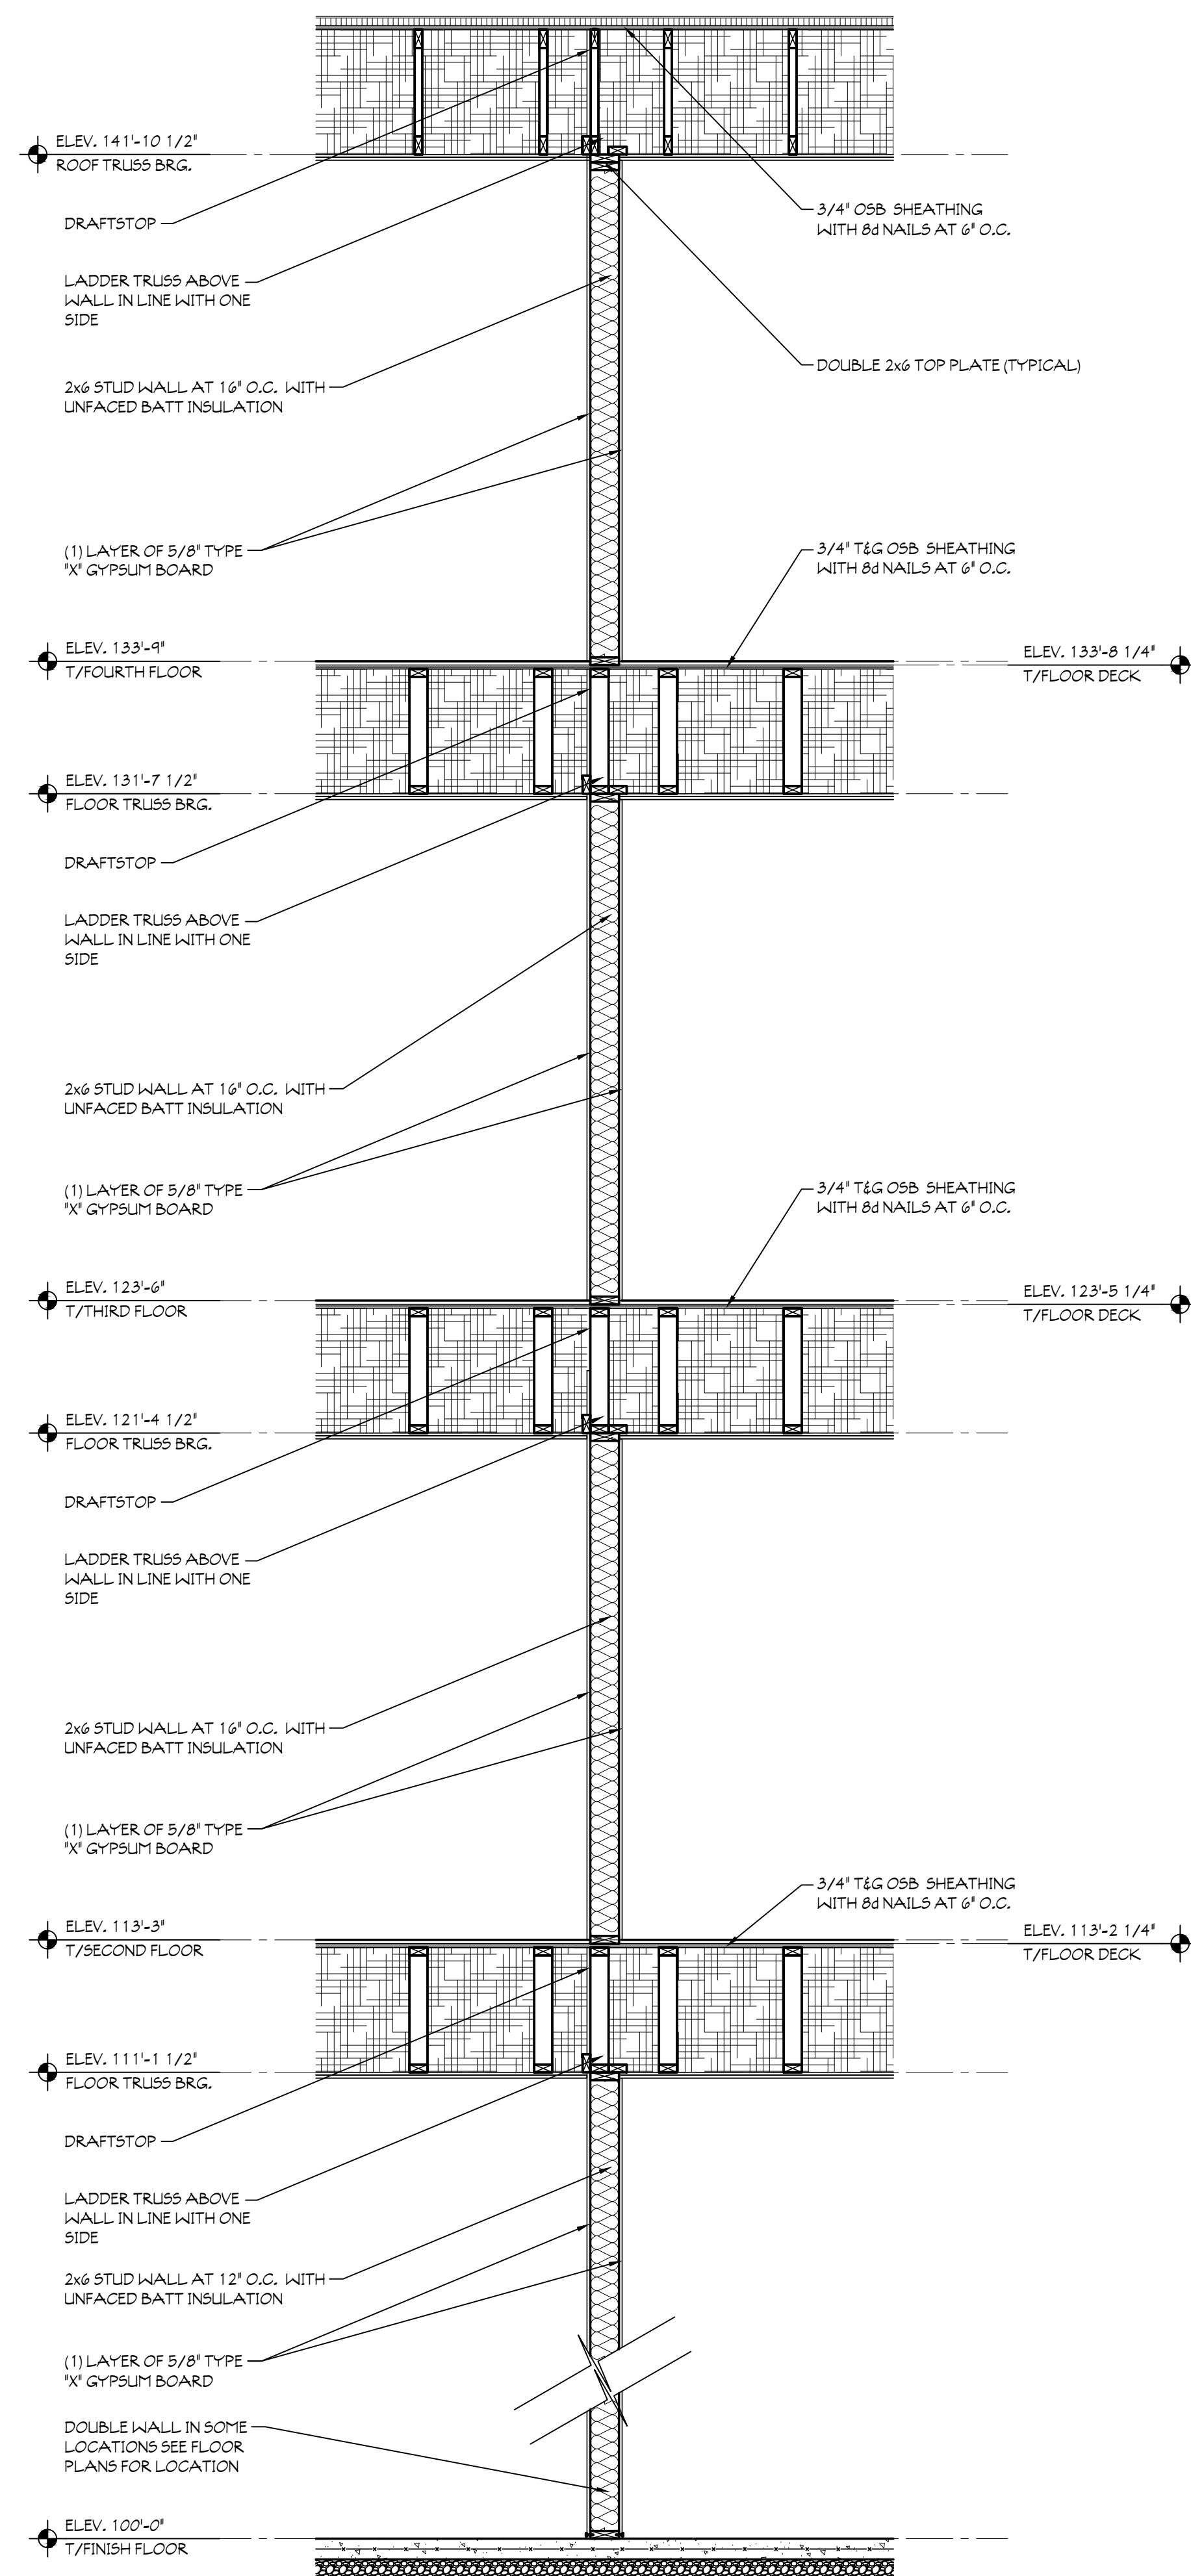

1 PARTY WALL DETAIL #1
SCALE: 1/2" = 1'-0" WALL ALL FLOORS

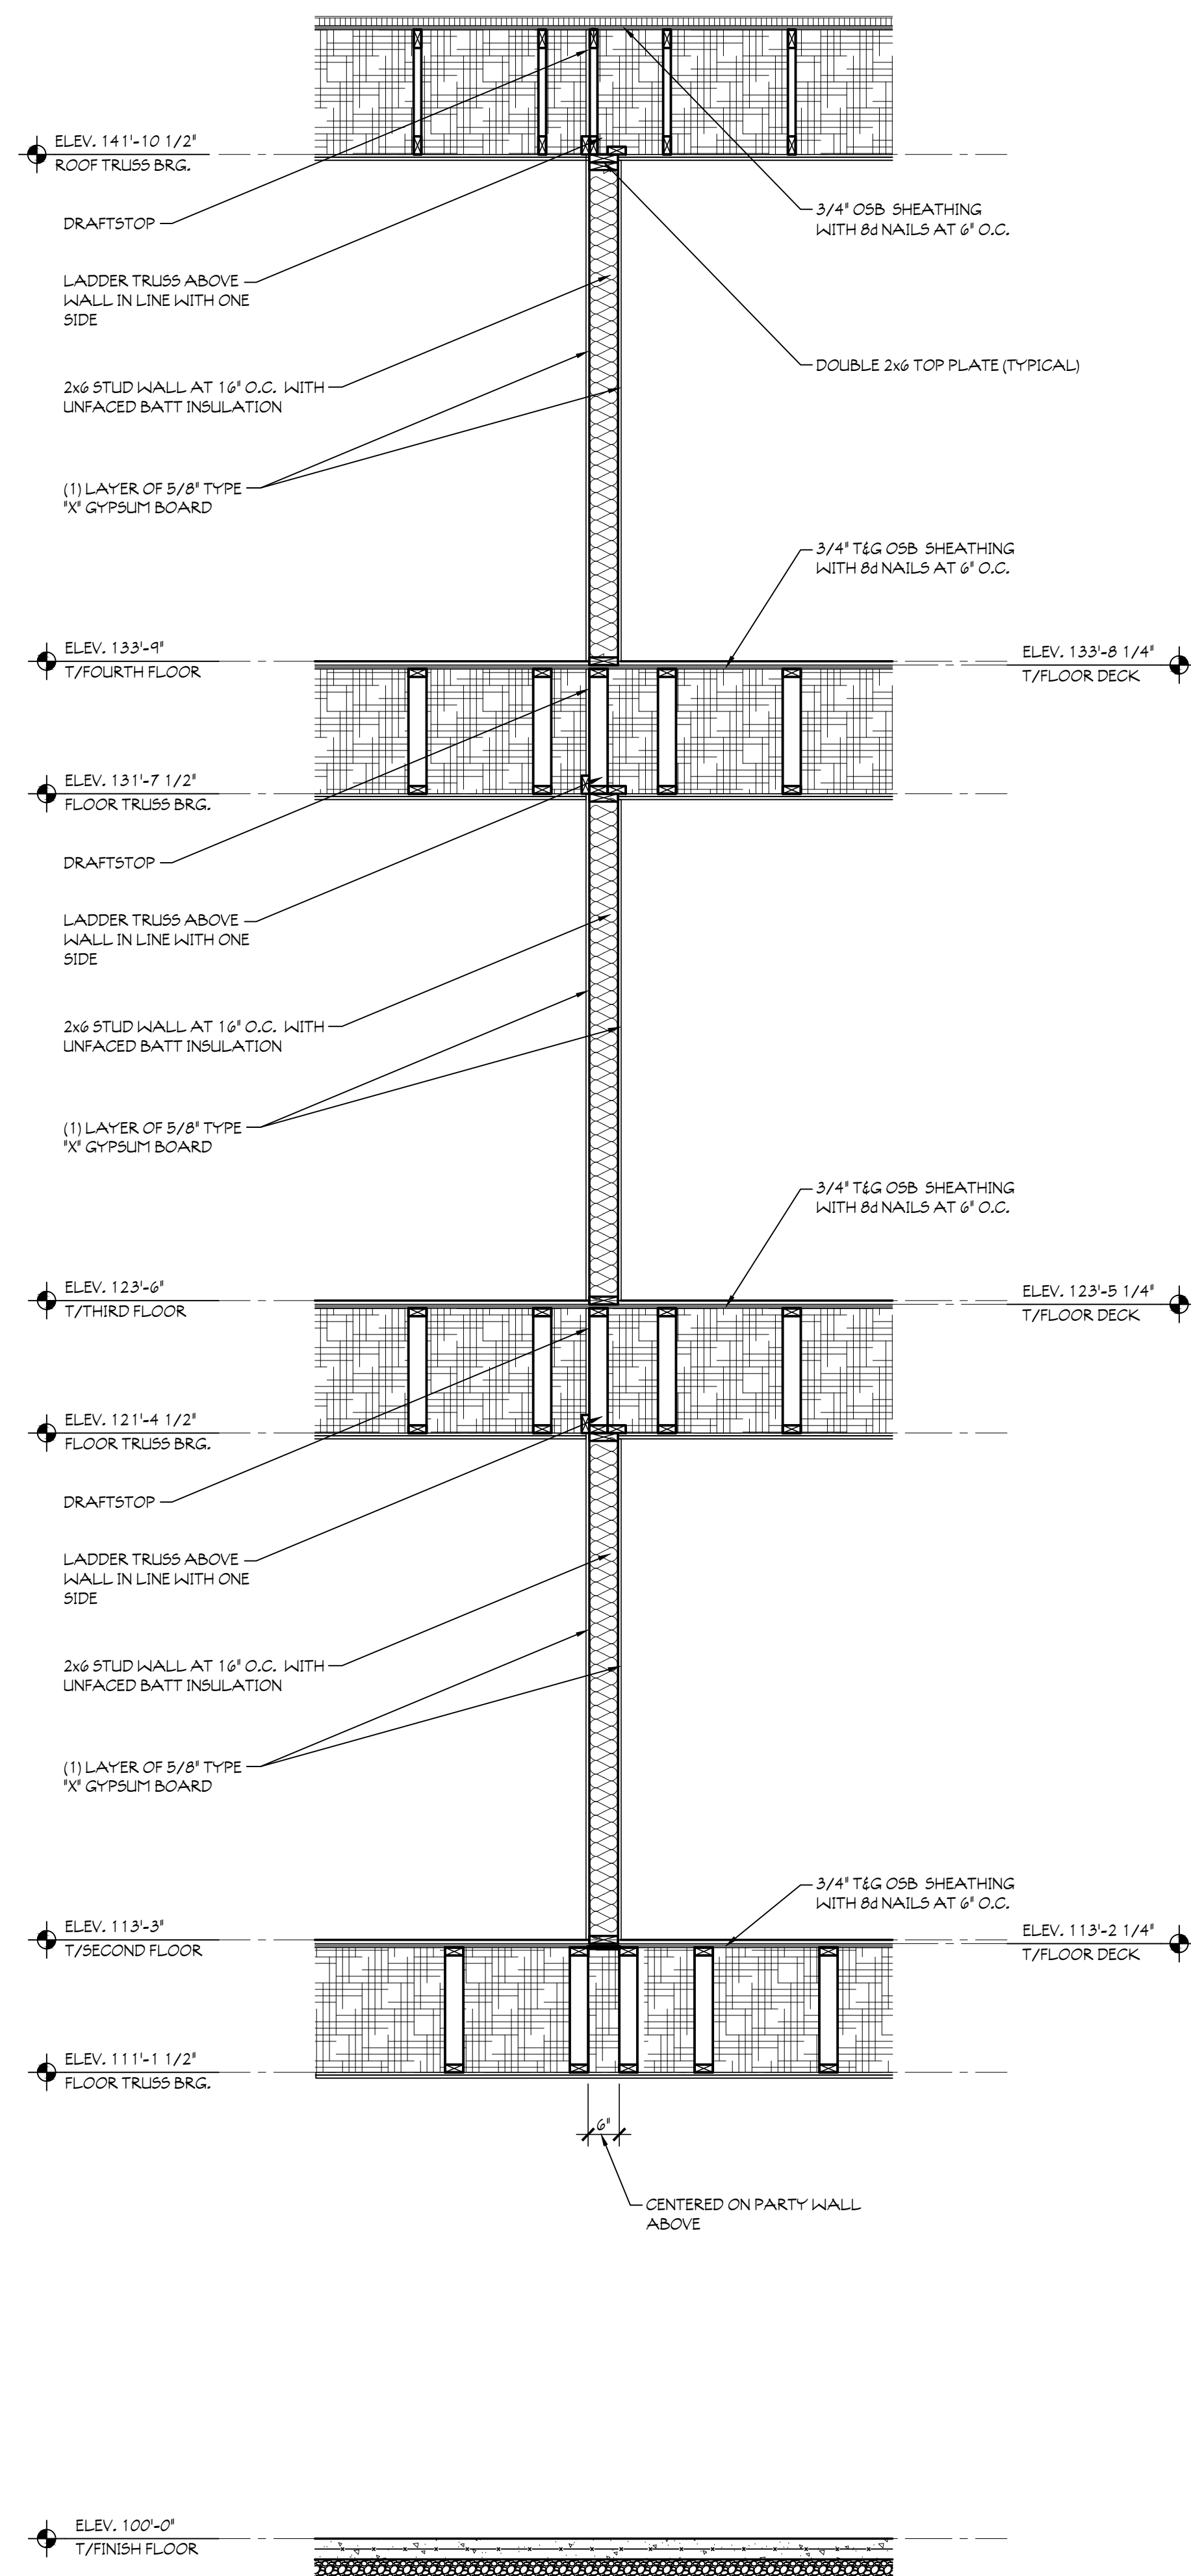

2 PARTY WALL DETAIL #2
SCALE: 1/2" = 1'-0" NO WALL 1ST FLOOR

GENERAL NOTES


- ALTHOUGH DRAWINGS ARE DRAWN TO SCALE, THE ACCURACY OF THE DRAWING CANNOT BE GUARANTEED DUE TO DISCREPANCIES IN THE METHODS OF REPRODUCTION. DIMENSIONS SHOULD BE DERIVED FROM DIMENSIONED PLANS.
- ALL DIMENSIONS, ROUGH OPENING SIZES, AND ELEVATION MARKERS MUST BE FIELD VERIFIED BY THE GENERAL CONTRACTOR. MAIST ARCHITECTURAL SERVICES SHALL NOT BE HELD RESPONSIBLE FOR ANY DIMENSIONAL DISCREPANCIES WHICH HAVE NOT BEEN BROUGHT TO THEIR ATTENTION PRIOR TO

M

MAUST
ARCHITECTURAL
SERVICES
DIVISION OF
L.E.M., INC.
112 NORTH MAIN STREET
GOSHEN, INDIANA 46526

* Architects
* Planners
* Consultants
* Construction Mgmt.
* Rule 5 and MS4 Filing

PHONE (574) 537-8500
FAX (574) 537-0808

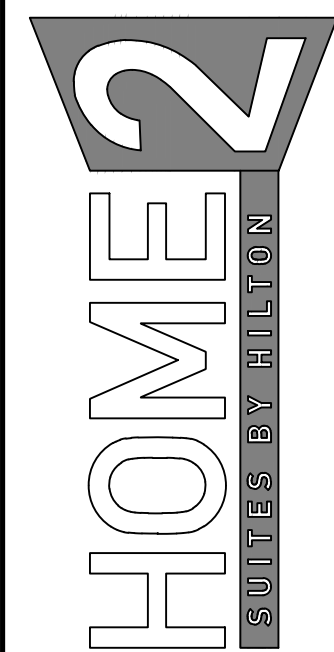

SHEET SIZE 24x36

FT. WAYNE, INDIANA

REVISIONS:

PRELIMINARY - NOT
FOR CONSTRUCTION

DATE: 05/01/26

JOB NO.: MAS-26-105

NAME _____

PARTY WALL DETAILS

SHEET

S403